

DÄR INGET ANNA T ANGES GÄLLER:
INFÄLLT MONTAGE PRIORITERAS DÄR BYGGNADS
KONSTRUKTIONEN TILLÅTTER VID UPL. MONTAGE FÖRLÄGG
KABLAG E I EL-LIST
BRANDTÄTNING I SAMMA KLASS SOM VÄGGENS
BRANDKLASS.
HÖJD ANGES METER ÖFG.
STRÖMBRYTARE +1.0, UTTAG +0.3
HALOGENFRITT MATERIAL
KABEL 3G1,5
STRECKAK AVSER BEFINTLIGT
FYLLD SYMBOL = INFÄLLD, EJ FYLLD = UTANPÅLIGGANDE.

2VÄGS UTTAG
1VÄGS UTTAG
STÄDUTTAG 1VÄGSUTTAG +0,9.
2VÄGS UTTAG PLACERAS OVAN UNDERTAK
CEE 3FAS 16A UTTAG +1,8

3VÄGS UTTAG I FÖNSTERBÄNKSCHANAL
2POLIG SÄKERHETSBRYTARE

A  3POLIG SÄKERHETSBRYTAR MED MÄRKSTRÖM

A 2POLIG SÄKERHETSBRYTARE FÖR DÖRAUTOMATIK
MONTERAS I ANSLUTNING TILL AUTOMATIKEN.

GVF 1-VÄGS UTTAG PLACERAS I SKÅP FÖR
GOLVVÄRMEFÖRDELARE



DA DÖRRAUTOMATIK

AK ARMBÅGSKONTAKT, HÖJD CC +0.8

CENTRAI

— KABEL
— — BEFINTLIG KABEL

- 1 KABLÄR FÖRLÄGGAS I KANALISATION I MARK/PLATTA
- 2 SPIRALKABEL MED UTTAG FÖR MATNING TILL
- 3 LADDVÄRMS DOSA OVAN UNDER TAK
- 4 VÄGUTTAG TILL PÅ DOSLÅT PÅ KABELSTEGE FÖR
- 5 ANSLUTNING AV AKTIV SKYLT FÖR HÖRSLINGA.
- 6 ANSLUTNING FLÄKTLUFTVÄRME
- 7 MATNING TABLÅ FETTAVSKILJARE
- 8 MATNING SCHUNT
- 9 FRÄNLUFTSFLÄKT
- 10 MATNING KYLURUM +1,7
- 11 INKOPPLING TRAFÖ FÖR BLÄNDARE. OVAN UNDER TAK
- 12 MATNING VÄRMEKABEL, PLACERING SAMORDNAS
- 13 MATNING AVFROSTNING -1,7
- 14 MONTERAS PÅ DOSLÅT PÅ KABELSTEGE.
- 15 TRÖMFGÖRSÖRNING MANOVERPANEL LJUD.
- 16 ANSLUTS TILL MP ENLIGT E646D-1-512
- 17 TRÖMFGÖRSÖRNING TILL INBROTTSALARM-CENTRAL

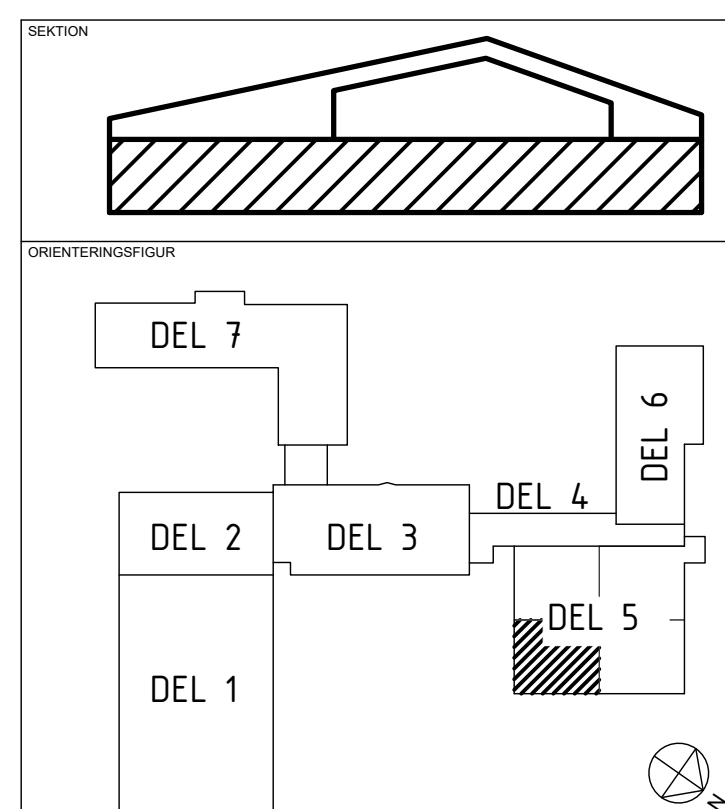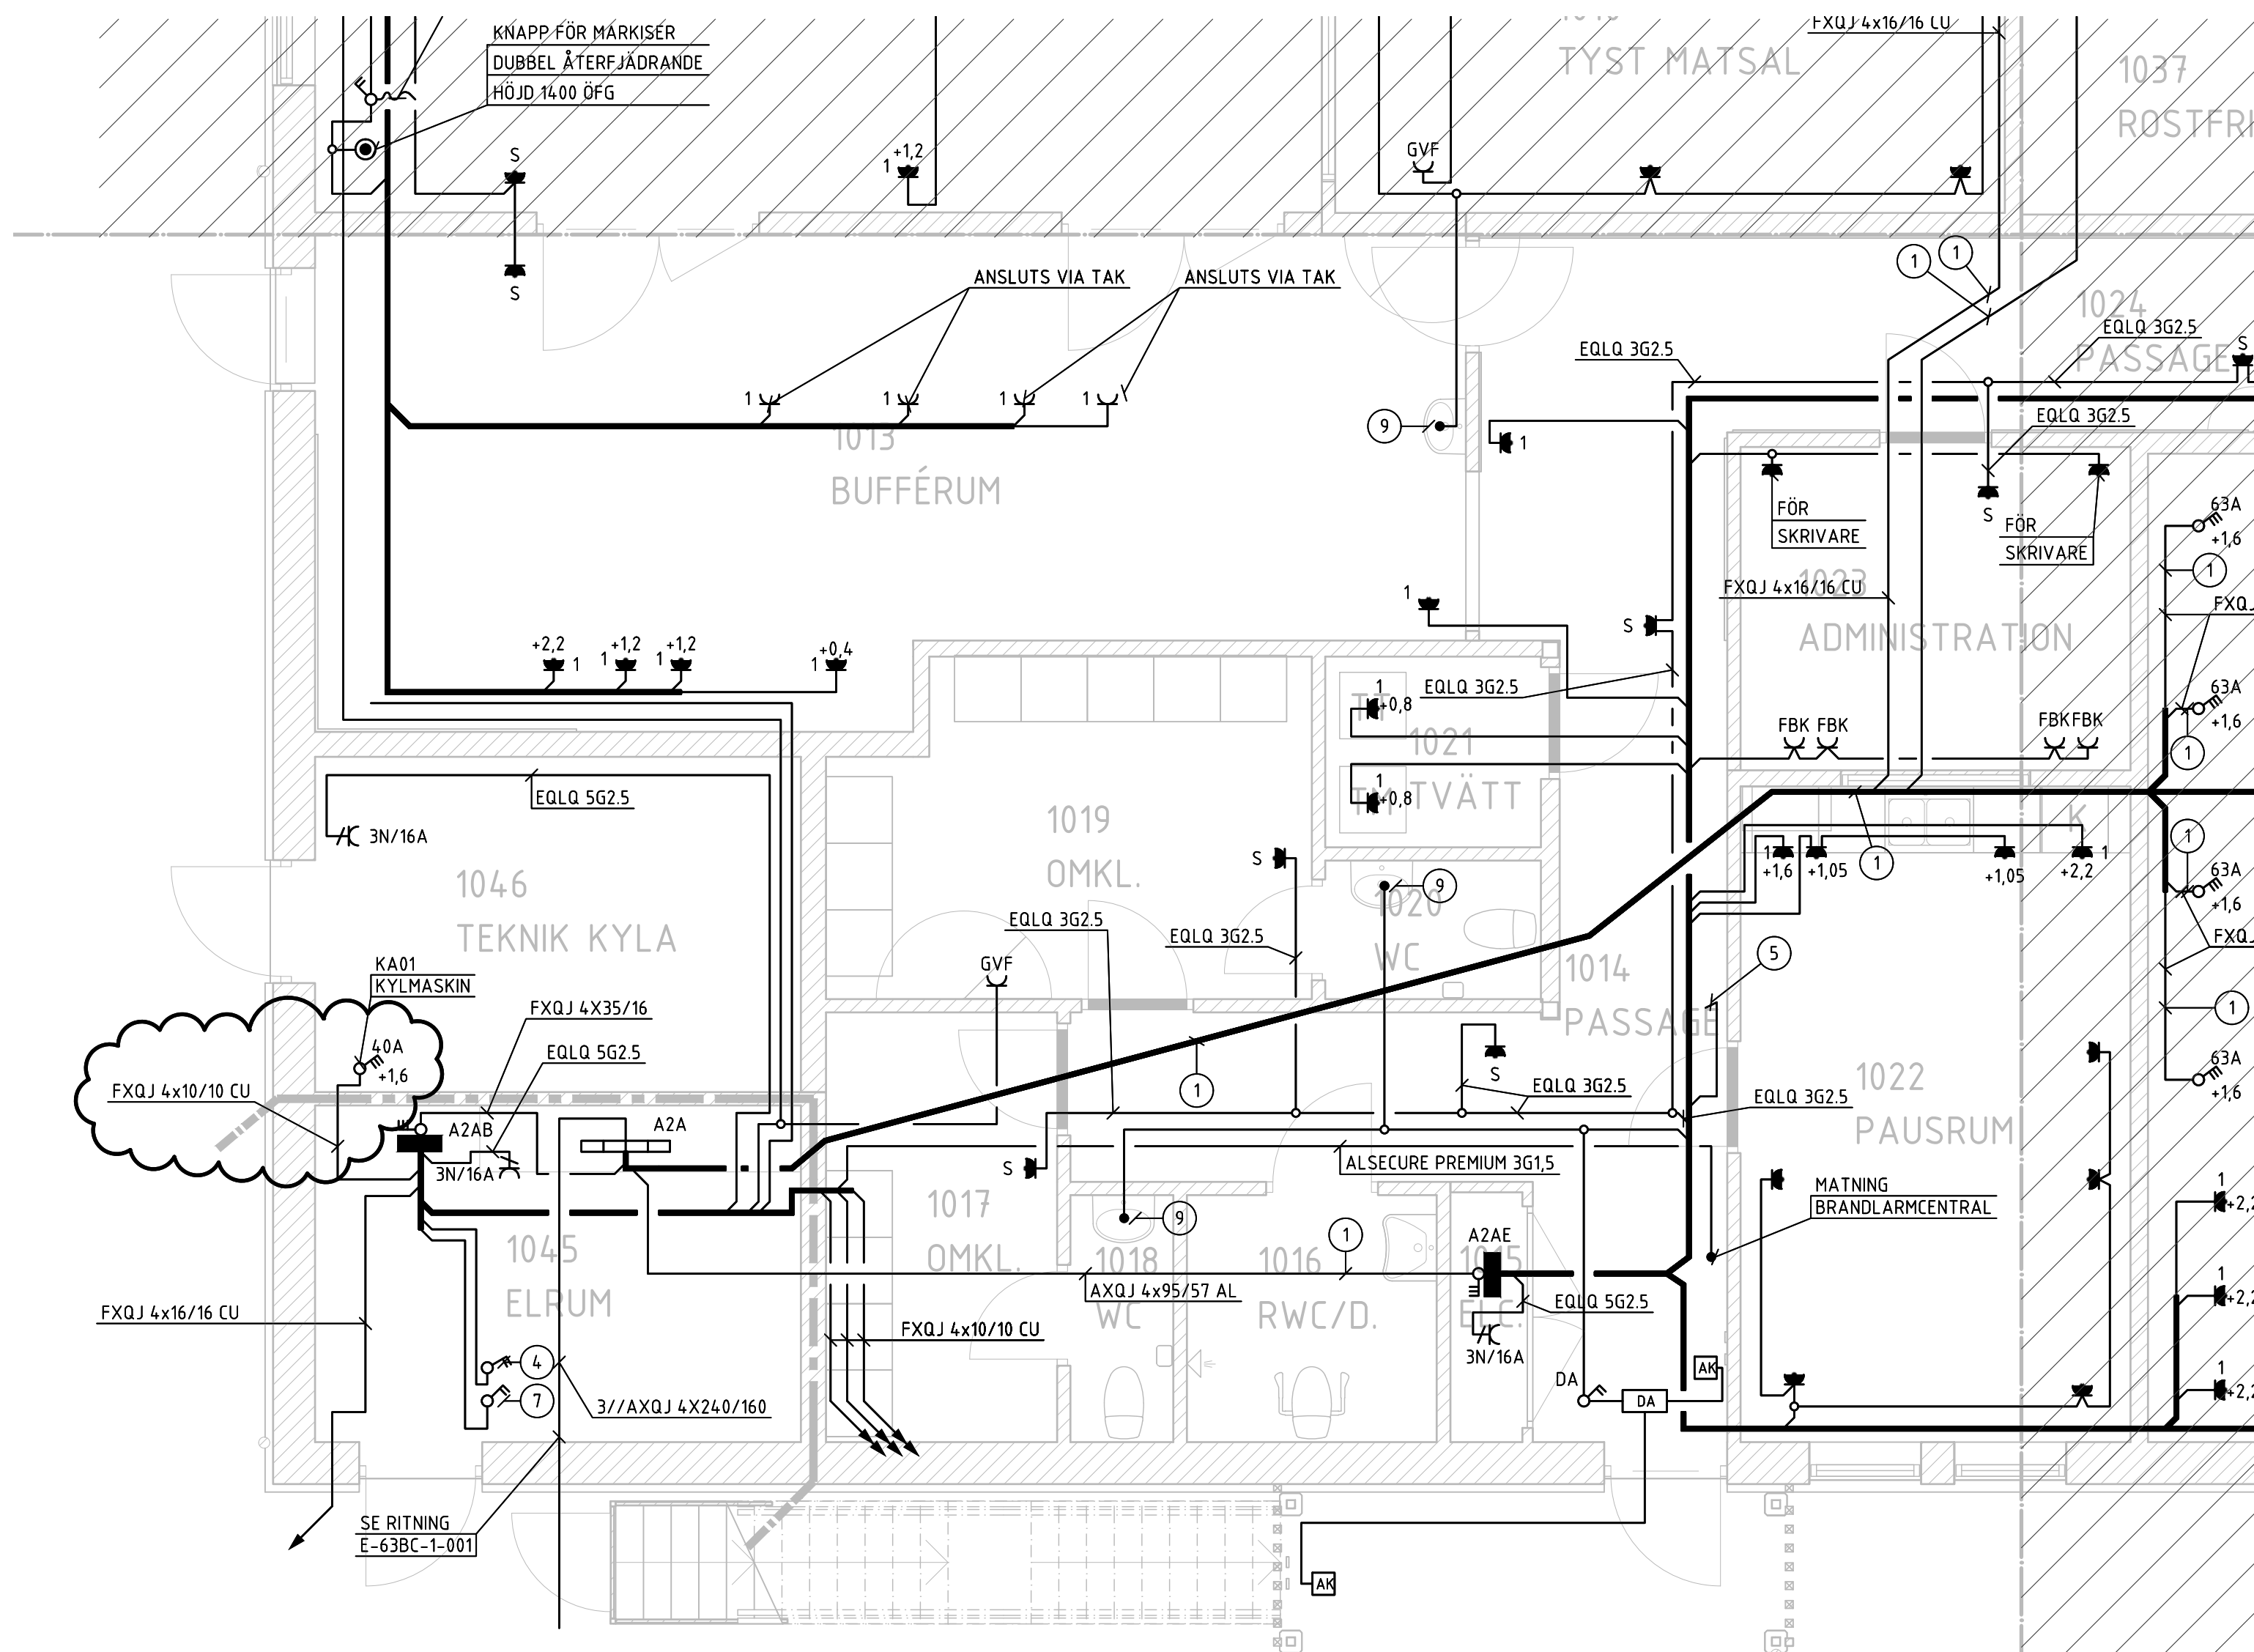

STATUS

FÖRFRÅGNINGSUNDERLAG

BYGGHANDLING

DATUM	GÖDKÄND AV	ÄNDRINGS PM
2025-01-31	GIN	KFU01
BESTÄLLARE		



PROJEKTNAMN

CENTRAALKÖK

OMRADE
ROBERTSFORS KOMMUN

PROJEKTNUMMER	ADRESS
	YTTRE RINGVÄGEN 4
DIARIENUMMER	FÄRTIDNET

DISCIPLIN	FÖRETAG
F	FORDONET 1
	NORDCONSULT OVERSICHT AF

E	NORCONSULT SVERIGE AB
UPPDRAGSNUMMER	SKAPAD AV
1088371	GIN

TELEFON	KONTAKTPERSON
010 141 80 00	TOMAS BERGSTRÖM
RYGGNÄDSVERK	BLIUSHÖJD (BH 2000)

+45,54 (FG)

VÄNINGSPLAN 1	VÄNINGSDEL	DELOMRÅDE DEL 5.3
SYSTEM		

KRAFT
SPECIFICATION
PLAN 1

PLAN 1		
RITNINGSKATEGORI	SKALA	FORMAT
PLANER	1:50	A1

DOKUMENTNUMMER	ANDRING
E-63BC-1-513	A

2018-12-24 15:00:00

FILNAMN: File Path