


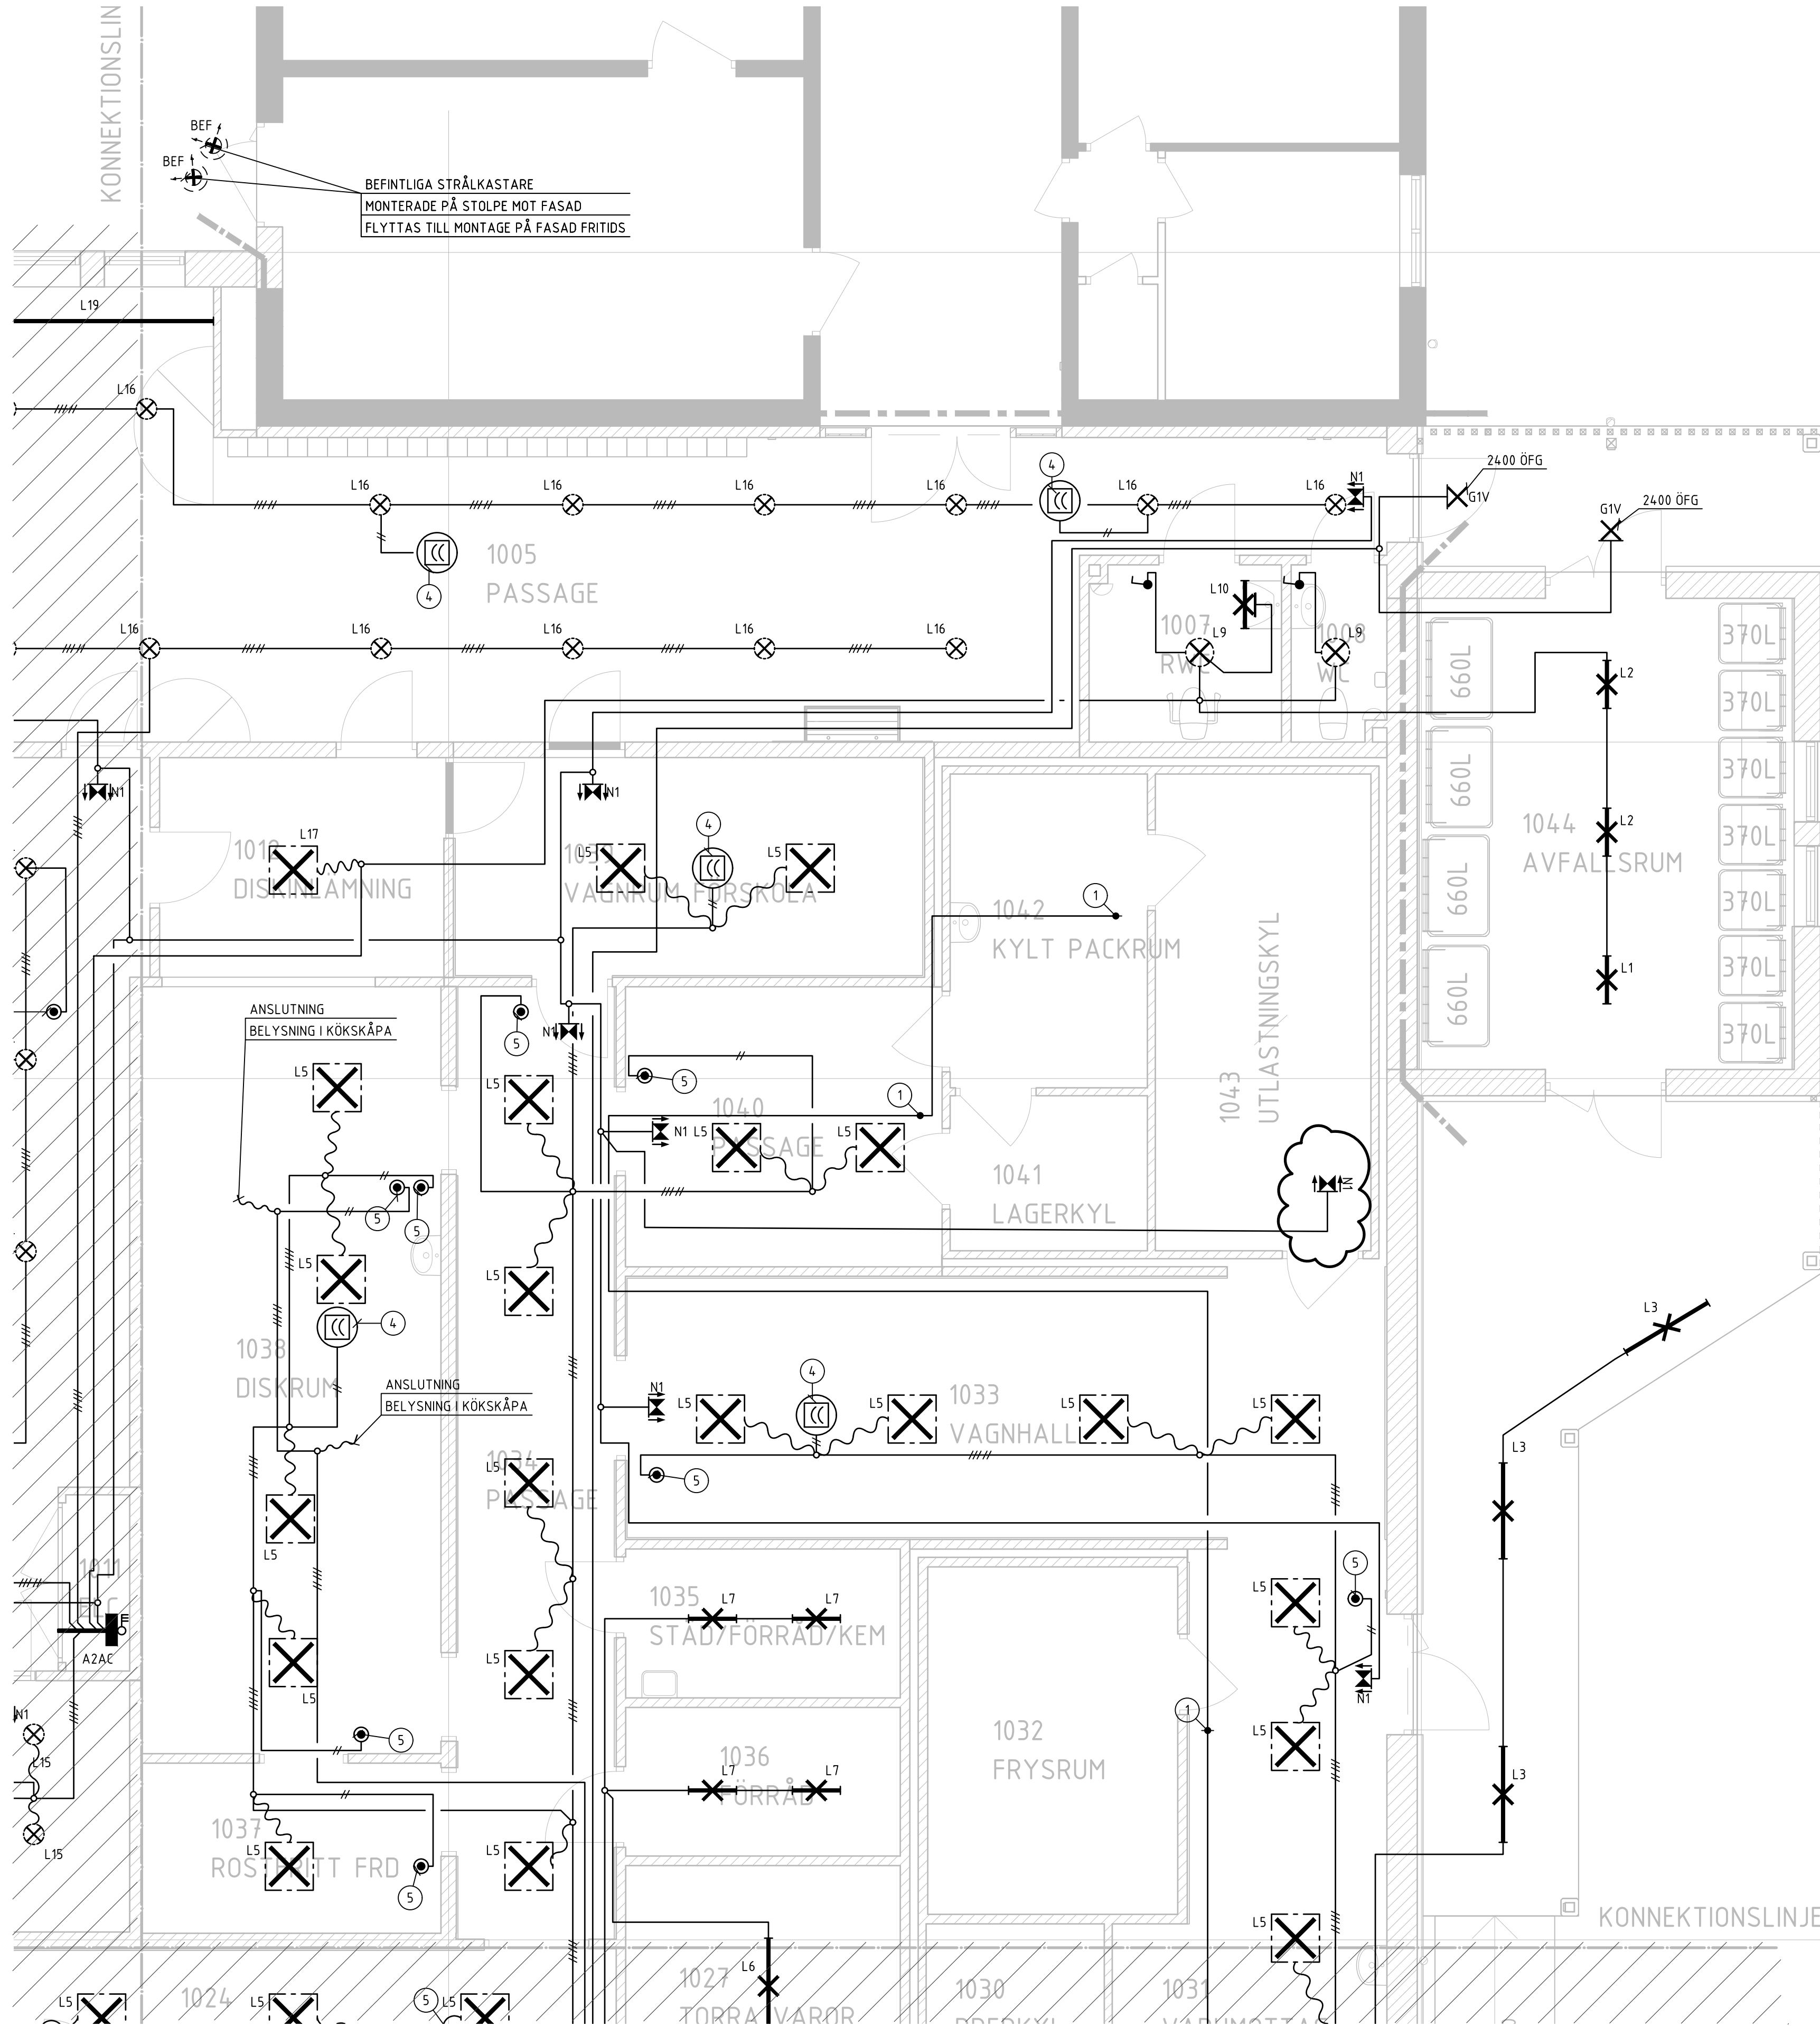

ANVISNINGAR
DÄR INGET ANNAT ANGES GÄLLER:
HALOGENFRITT MATERIAL
KABEL 3G15
HÖJD ANGES I METER.

SYMBOLFÖRKLARINGAR

- STRÖMSTÄLLARE IPOLIG
- STRÖMSTÄLLARE KRON
- STRÖMSTÄLLARE TRAPPKOPPLING
- STRÖMSTÄLLARE DIMMER
- TRYCKKNAPP

- 1 ANSLUTNING AV BELYSNING I KYL-/FRYSRUM
- 2 UTTAG FÖR LADDNING AV HANDLAMPA 0,5 M.Ö.G.
- 3 ANSLUTNING AV BEFINTLIG LEDNING TILL STOLPBELYSNING.
- 4 PIR-SENSOR TYP HELVAR 320 E17 046 29
- 5 ÅTERFJÄDRANDE TRYCKKNAPP MED INGÅNGSENHET HELVAR MINI 444 E17 045 88
- 6 SCENMODUL HELVAR 136W + RAM 2305

HÄNVISNINGAR
SE ÄVEN:
- ARMATURFÖRTECKNING

SEKTION

ORIENTERINGSFIGUR

STATUS
FÖRFRÅGNINGSUNDERLAG

HANDLING
BYGGHANDLING

DATUM
2025-01-31

LOKALISERING
GIN

ÄNDRINGAR PÅ
KFU01

BESTÄLLARE

ROBERTSFORS
KOMMUN

PROJEKTNAMN
CENTRALEKÖK

OMRÅDE
ROBERTSFORS KOMMUN

PROJEKTNUMMER
YTTRE RINGVÄGEN 4

DÄRNUMMER
FASTIGHET
FORDONET 1

DISCIPLIN
E

FÖRETAG
NORCONSULT SVERIGE AB

UPPDRAGSNUMMER
1088371

SKAPAD AV
GIN

TELEFON
010 141 80 00

KONTAKTPERSON
TOMAS BERGSTRÖM

BYGGNADSVÄRK
PÅLÖSHET (VATN) 2020
+45,54 (FG)

VÄNINGSPLAN
1

VÄNINGSDEL
1

DELOMRÅDE
DEL 4.2, 5.2

SYSTEM
BELYSNING

SPECIFIKATION
PLAN 1

TYTTNINGSGRÄNSVÄR
PLANER

SKALA
1:50

FORMAT
A1

ÄNDRING
A

DOCUMENTNUMMER
E-63F-1-512