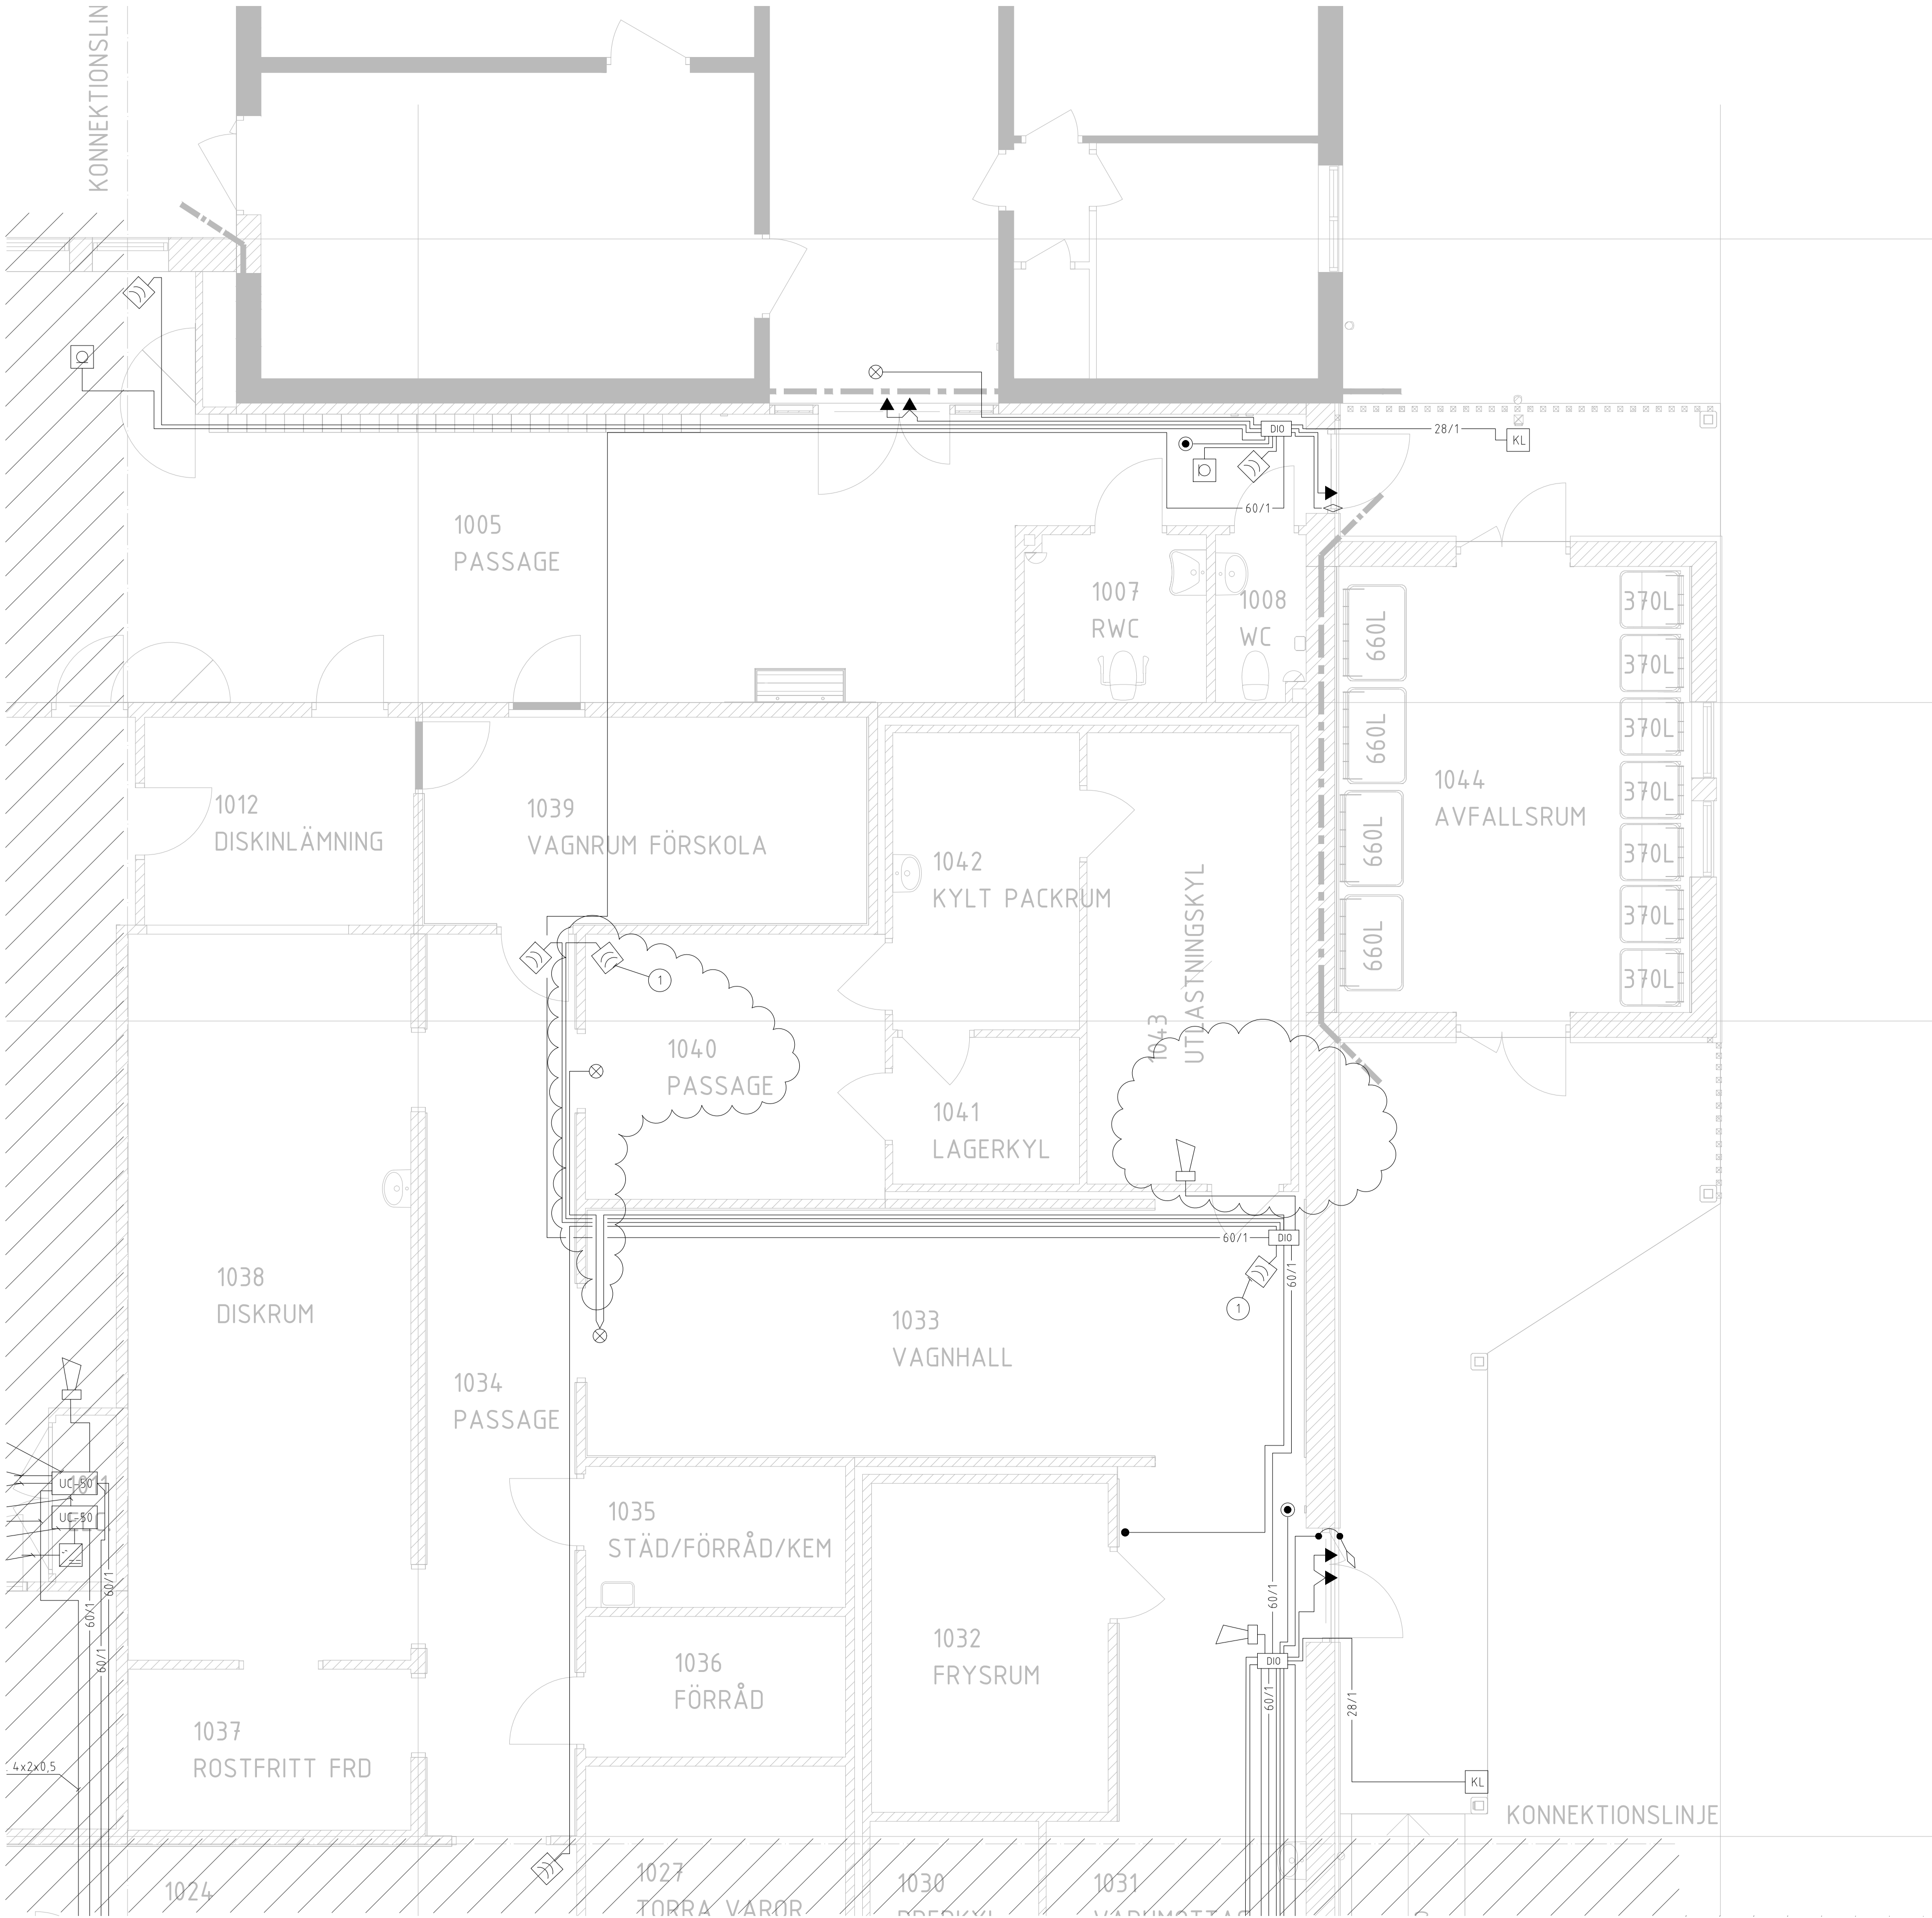


- ANVISNINGAR**
- DOSOR OCH UTTAG SOM PLACERAS PÅ LEDNINGSSTEGE MONTERAS PÅ STEGPLÅT.
RÖRESEDETEKTORER OCH LARMÖN MONTERAS 50mm NEDAN TAKVINKEL DÄR EJ ANNAT ANGES.
GLASKROSSDETEKTOR MONTERAS DIKT UNDER TAK RIKTADE MOT FÖNSTERPARTI.
- KABEL, DÄR EJ ANNAT ANGES: ELQXB 2X2X0,5
- SYMBOLFÖRKLARINGAR**
- UC-50 CENTRALAPPARAT INTEGRERAT LARM-/PASSERSYSTEM
 - NÄTDEL INKL. BATTERIBACKUP
 - M HÄNÖVERPANEL INTEGRERAT SYSTEM, MONTERAS +1600mm ÖG
 - MAGNETKONTAKT
 - IR DETEKTOR
 - IR DETEKTOR 360°
 - AKUSTISK GLASKROSSDETEKTOR
 - INDIKERINGSLAMP, MONTERAS OVAN DÖRRKARM
 - DÖRR-/LARMÖN, MONTERAS OVAN UNDER TAK
 - KL KORTLÄSARE, MONTERAS +1200mm ÖM
 - ÖPPNAKNAPP, MONTERAS +1200mm ÖG
 - KÄRMÖVERFÖRING
 - ELSLUTBLECK
- 60/1- FLOÖBR 1X2 + 2X2X0,22
-28/1- PTS-HF 2X2X0,6
- DETEKTOR FÖRBJÖDPLAS VIA KORTLÄSARE "LASTBRYGGA" TILLS TILKÖPLING SKER ELLER EFTER MAX 30 MIN.
ENHET TERMINERAS. SE INSTALLATIONS MANUAL AKTUELL ENHET.

SEKTION

ORIENTERINGSFIGUR

DEL 7
DEL 2
DEL 3
DEL 4
DEL 5
DEL 6
DEL 1

STATUS

FÖRFRÅGNINGSUNDERLAG

HANDLING

BYGGHANDLING

DATUM 2025-01-31
ANSÖKAN AV T. BERGSTRÖM
ÄNDRING NR KFU01

BESTÄLLARE

ROBERTSFORS KOMMUN

PROJEKTNAMN

CENTRALEKÖ

OMRÅDE

ROBERTSFORS KOMMUN

PROJEKTNUMMER

YTTRE RINGVÄGEN 4

DÄRNUMMER

FASTIGHET FORDONET 1

DISCIPLIN

E FÖRETAG NORCONSULT SVERIGE AB

UPPDRAGSNUMMER

1088371 ÖPN

TELEFON

010 141 80 00

KONTAKTPERSON

TOMAS BERGSTRÖM

BYGGNADSVÄRK

PLÅSHÖJD (MM) 1000

+45,54 (FG)

VÄNINGSPLAN

1

VÄNINGSDEL

DEL 4.2, 5.2

DELOMRÅDE

DEL 4.2, 5.2

SYSTEM

INBROTT & PASSAGE

SPECIFIKATION

PLAN 1

TITEL

PLANER

SKALA

1:50

FORMAT

A1

ÄNDRING

A

DOCUMENTNUMMER

E-64CCB-1-512