


FÖRKLARINGSTEXT
SE RITNING V-50-0-001

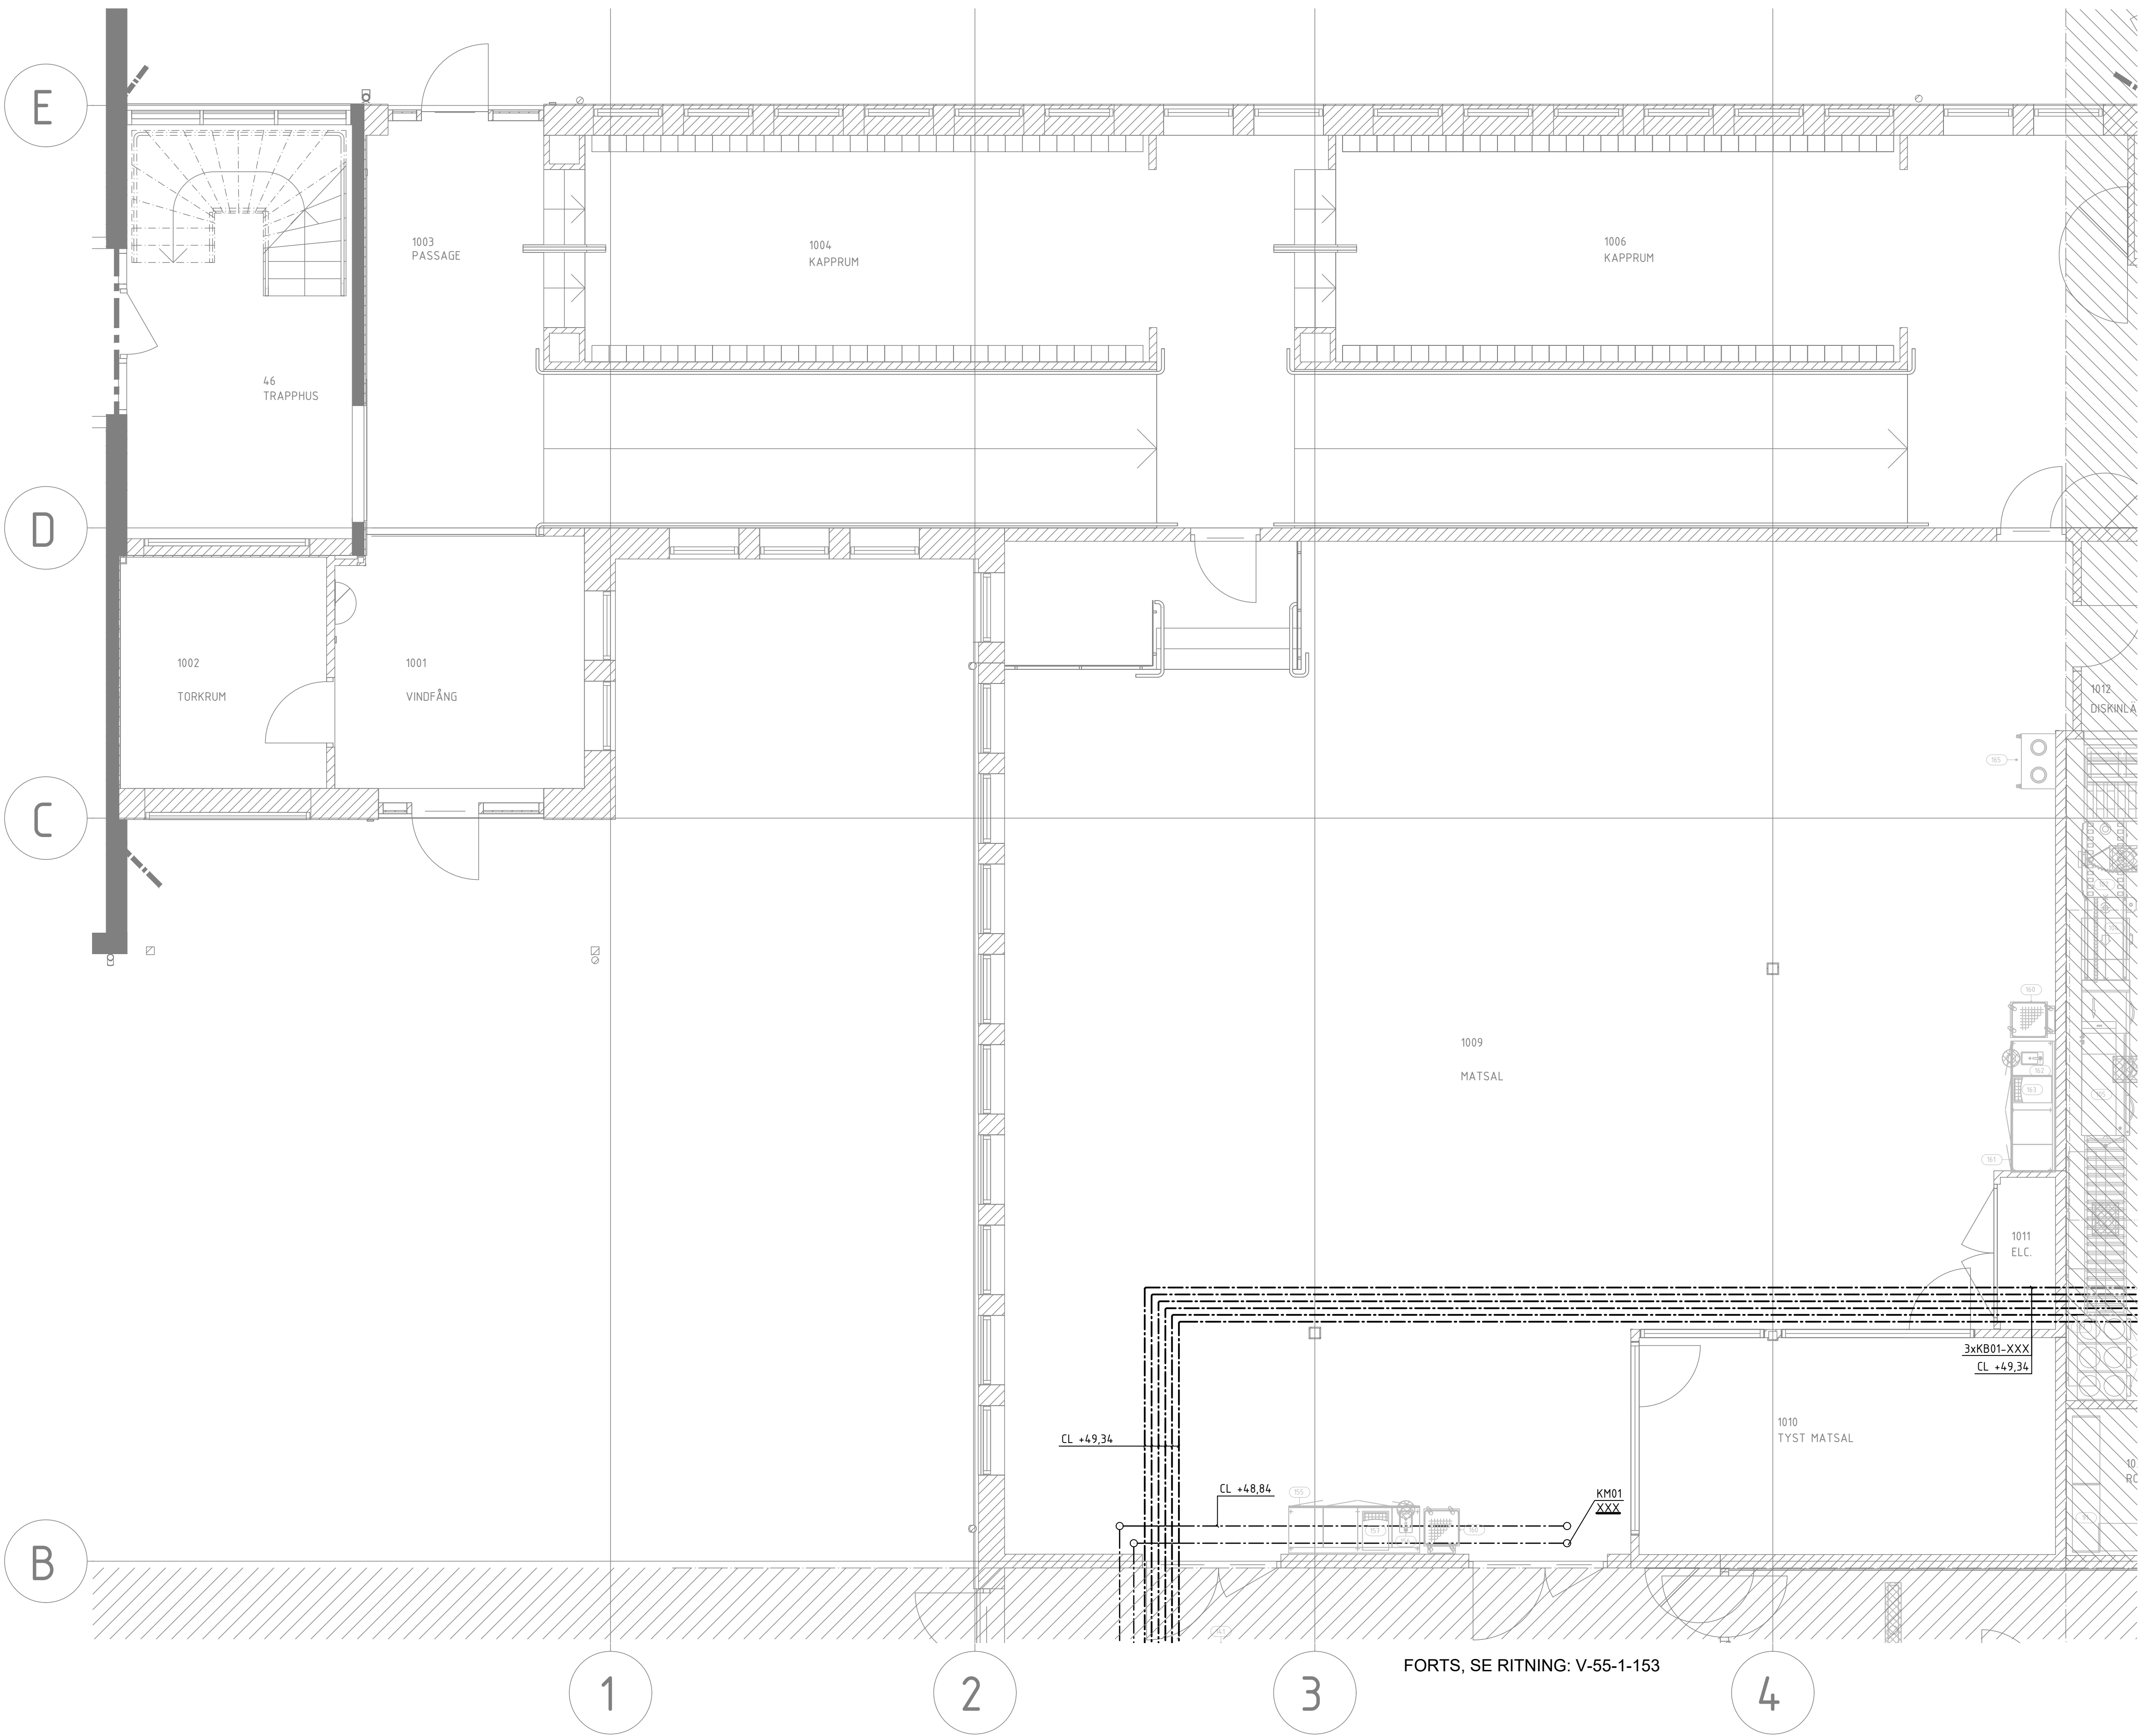

FORTS SE RITNING: V-55-1-152

SEKTION

ORIENTERINGSPOL

STATUS

FÖRFRÅGNINGSUNDERLAG

HANDLING

BYGGHANDLING

DATUM

2025-01-31

GODKÄND AV

T.BERGSTRÖM

ÄNDRINGS PM

KFU01

BESTÄLLARE

ROBERTSFORS
KOMMUN

PROJEKTNAMN

CENTRALKÖK

OMRADE

ROBERTSFORS KOMMUN

PROJEKTNUMMER

FÖRRETT

YTTRE RINGVÄGEN 4

DARIENUMMER

FASTIGHET

FÖR DONET 1

DISCIPLIN

FÖRETAG

NORCONSULT SVERIGE AB

OPPFÖRINGSNUMMER

SKAPAD AV

MAN

TELEFON

KONTAKTPERSON

010 141 80 00 JONAS JOHANSSON

BYGGNADSVÄRDE

(KLIMATKORRIGERT)

+45,54 (FG)

VÄNINGSPLAN

VÄNINGSDEL

DELOMRÅDE

1

DEL 4.1, 5.1

SYSTEM

55 KYLINSTALLATIONER

PROJEKTINFORMATION

PLAN 1 - DEL 4.1, 5.1

RITNINGSKATEGORI

PLAN

SKALA

1:50

FORMAT

A1

DOKUMENTNUMMER

V-55-1-151

ÄNDRING

A

FILNAMN: