
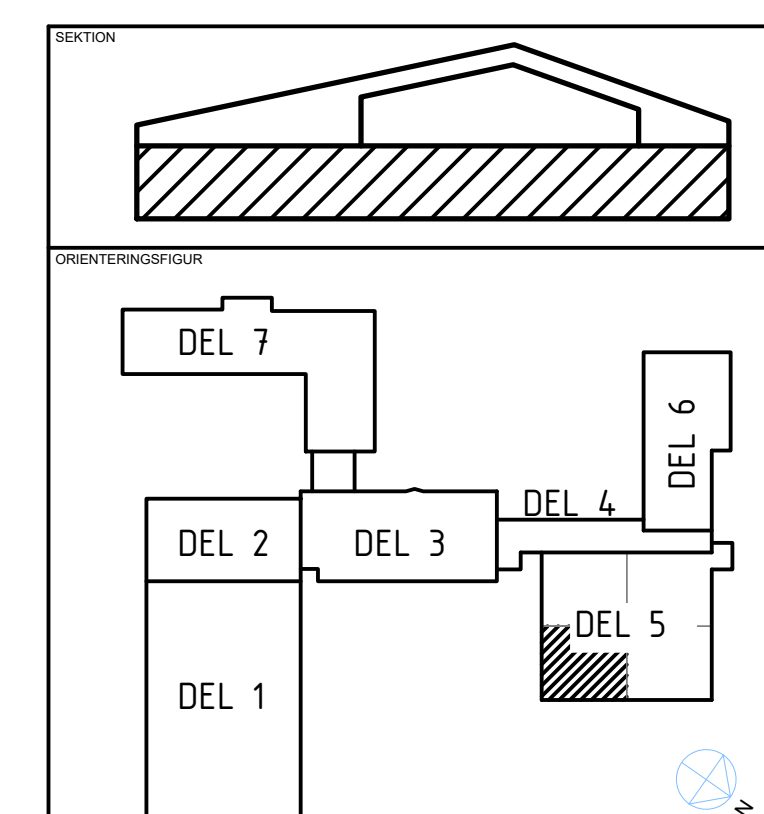


FÖRKLARINGSTEXT
SE RITNING V-50-0-001

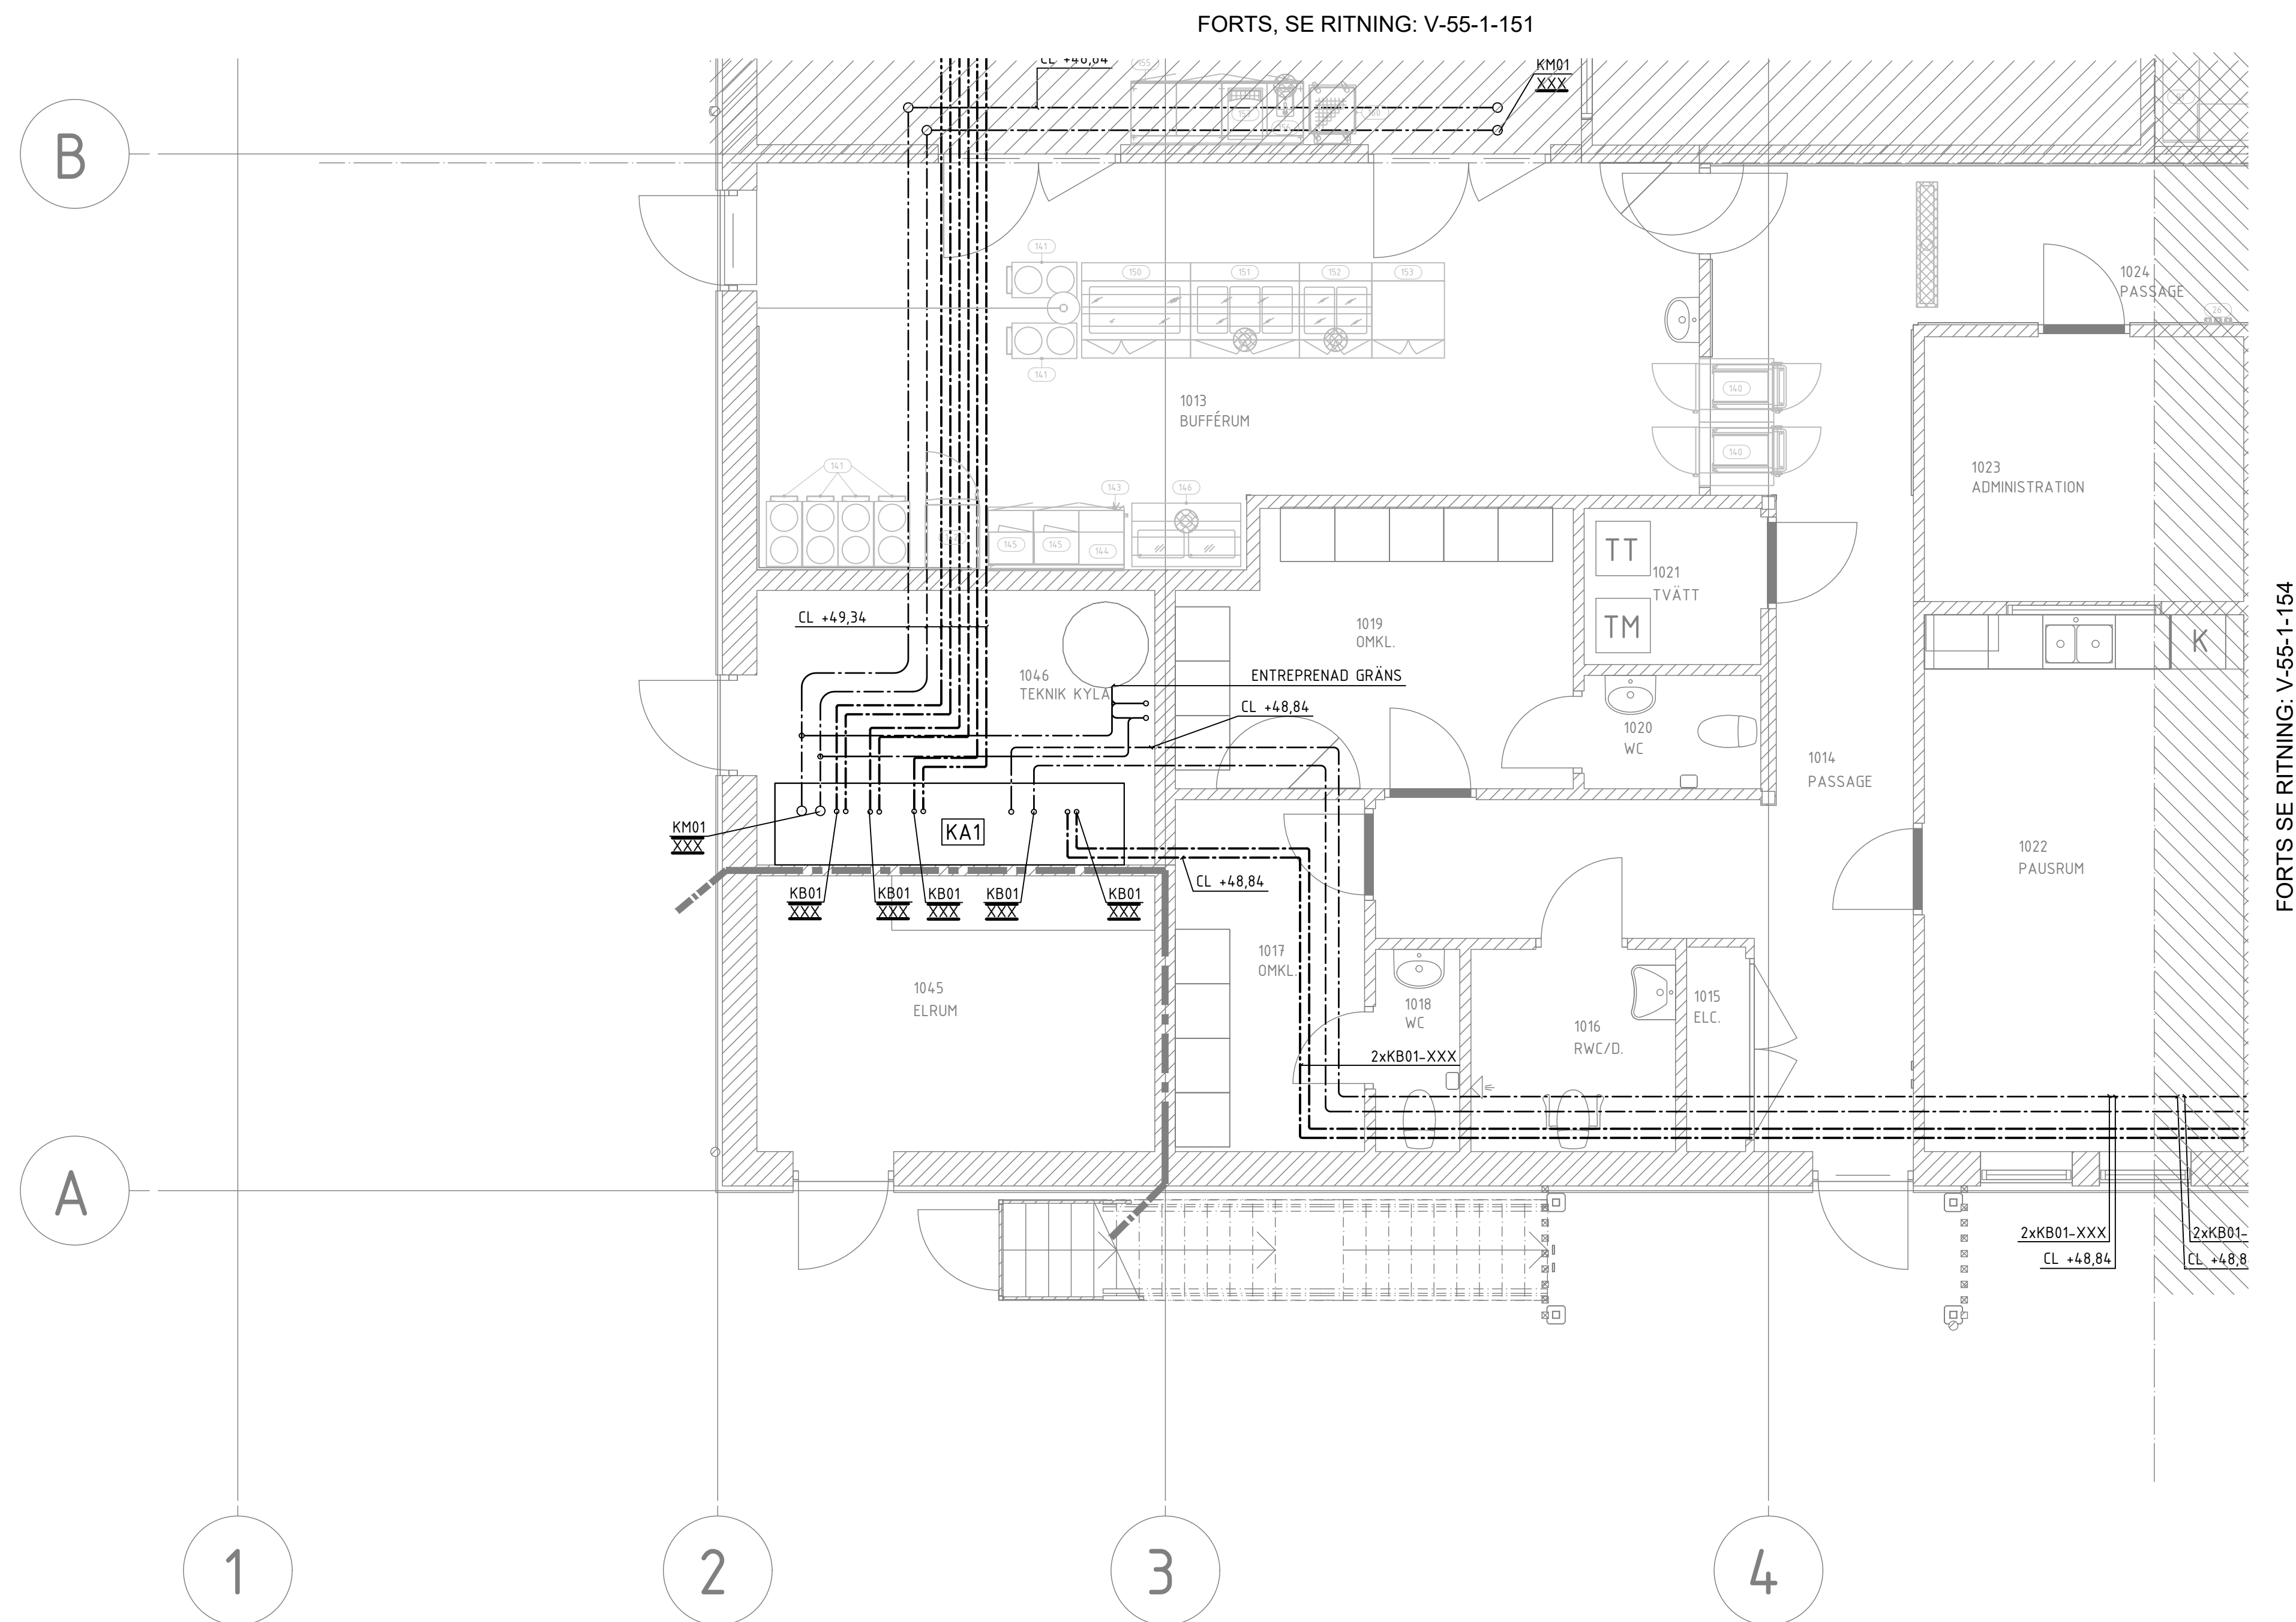

STATUS FÖRFRÅGNINGSUNDERLAG

HANDLING	BYGGHANDLING
----------	--------------

DATUM	GODKÄND AV	ÄNDRINGS
2025-01-31	T.BERGSTRÖM	KFU0

2025-01-31	BERGSTRÖM	RF 00
BESTÄLLARE		



PROJEKTNAMN

CENTRAALKÖK

OMRADE
ROBERTSFORS KOMMUN

PROJEKTNUMMER	ADRESS
	YTTRE RINGVÄGEN 4

DIARIENUMMER	FASTIGHET FORDONET 1
--------------	-------------------------

DISCIPLIN	FÖRETAG
VS	NORCONSULT SVERIGE AB

UPPDRAGSNUMMER 108 83 71	SKAPAD AV MAN
-----------------------------	------------------

TELEFON	KONTAKTPERSON
010 141 80 00	JONAS JOHANSSON

010 141 80 00	JONAS JONANSSON
BYGGNADSVÄRK	PLUSHÖJD (RH 2000) +45 54 (EG)

		445,54 (P)
VÄNINGSPLAN	VÄNINGSDEL	DELOMRÅDE
1		DEL 53

1	DEL 3.5
SYSTEM	
55 KYI INSTALLATIONER	

55 KYLINSTALLATIONER
SPECIFIKATION
PLAN 1 - DEL 53

RITNINGSKATEGORI	SKALA	FORMAT
PLAN	1:50	A1

PLAN	1:50	A1
DOKUMENTNUMMER		ÄNDERUNG
V. 55 1 153		A

V-55-1-153	A
------------	---

[illegible]