



FORTS, SE RITNING: V-55-1-152

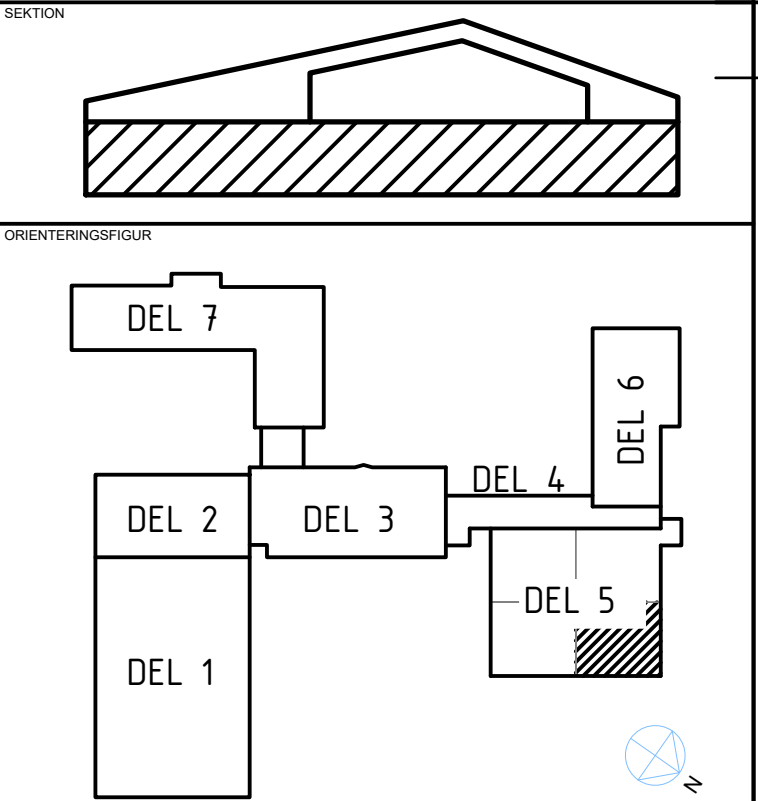

SEKTION		
ORIENTERINGSDIAGRAM		
STATUS		
FÖRFRÅGNINGSUNDERLAG		
HANDLING		
BYGGHANDLING		
DATUM	GODKÄND AV	ÄNDRINGS PM
2025-01-31	T.BERGSTRÖM	KFU01
BESTÄLLARE		
ROBERTSFORS KOMMUN		
PROJEKTNAMN		
CENTRALKÖK		
OMRADE		
ROBERTSFORS KOMMUN		
PROJEKTNUMMER	FÖRRETT	
	YTTRE RINGVÄGEN 4	
DIARIENUMMER	FÖRORDNET 1	
DISCIPLIN	FÖRETAG	
VS	NORCONSULT SVERIGE AB	
OPPFÖRINGSNUMMER	SKAPAD AV	
108 83 71	MAN	
TELEFON	KONTAKTPERSON	
010 141 80 00	JONAS JOHANSSON	
BYGGNADSVÄRDE	(KLIMATKORRIGERT 2000)	
	+45,54 (FG)	
VÄNINGSPLAN	VÄNINGSDEL	DELOMRÅDE
1		DEL 5.4
SYSTEM		
55 KYLINSTALLATIONER		
BESKRIVNING		
PLAN 1 - DEL 5.4		
RITNINGSKATEGORI	SKALA	FORMAT
PLAN	1:50	A1
DOKUMENTNUMMER	ÄNDRING	
V-55-1-154	A	

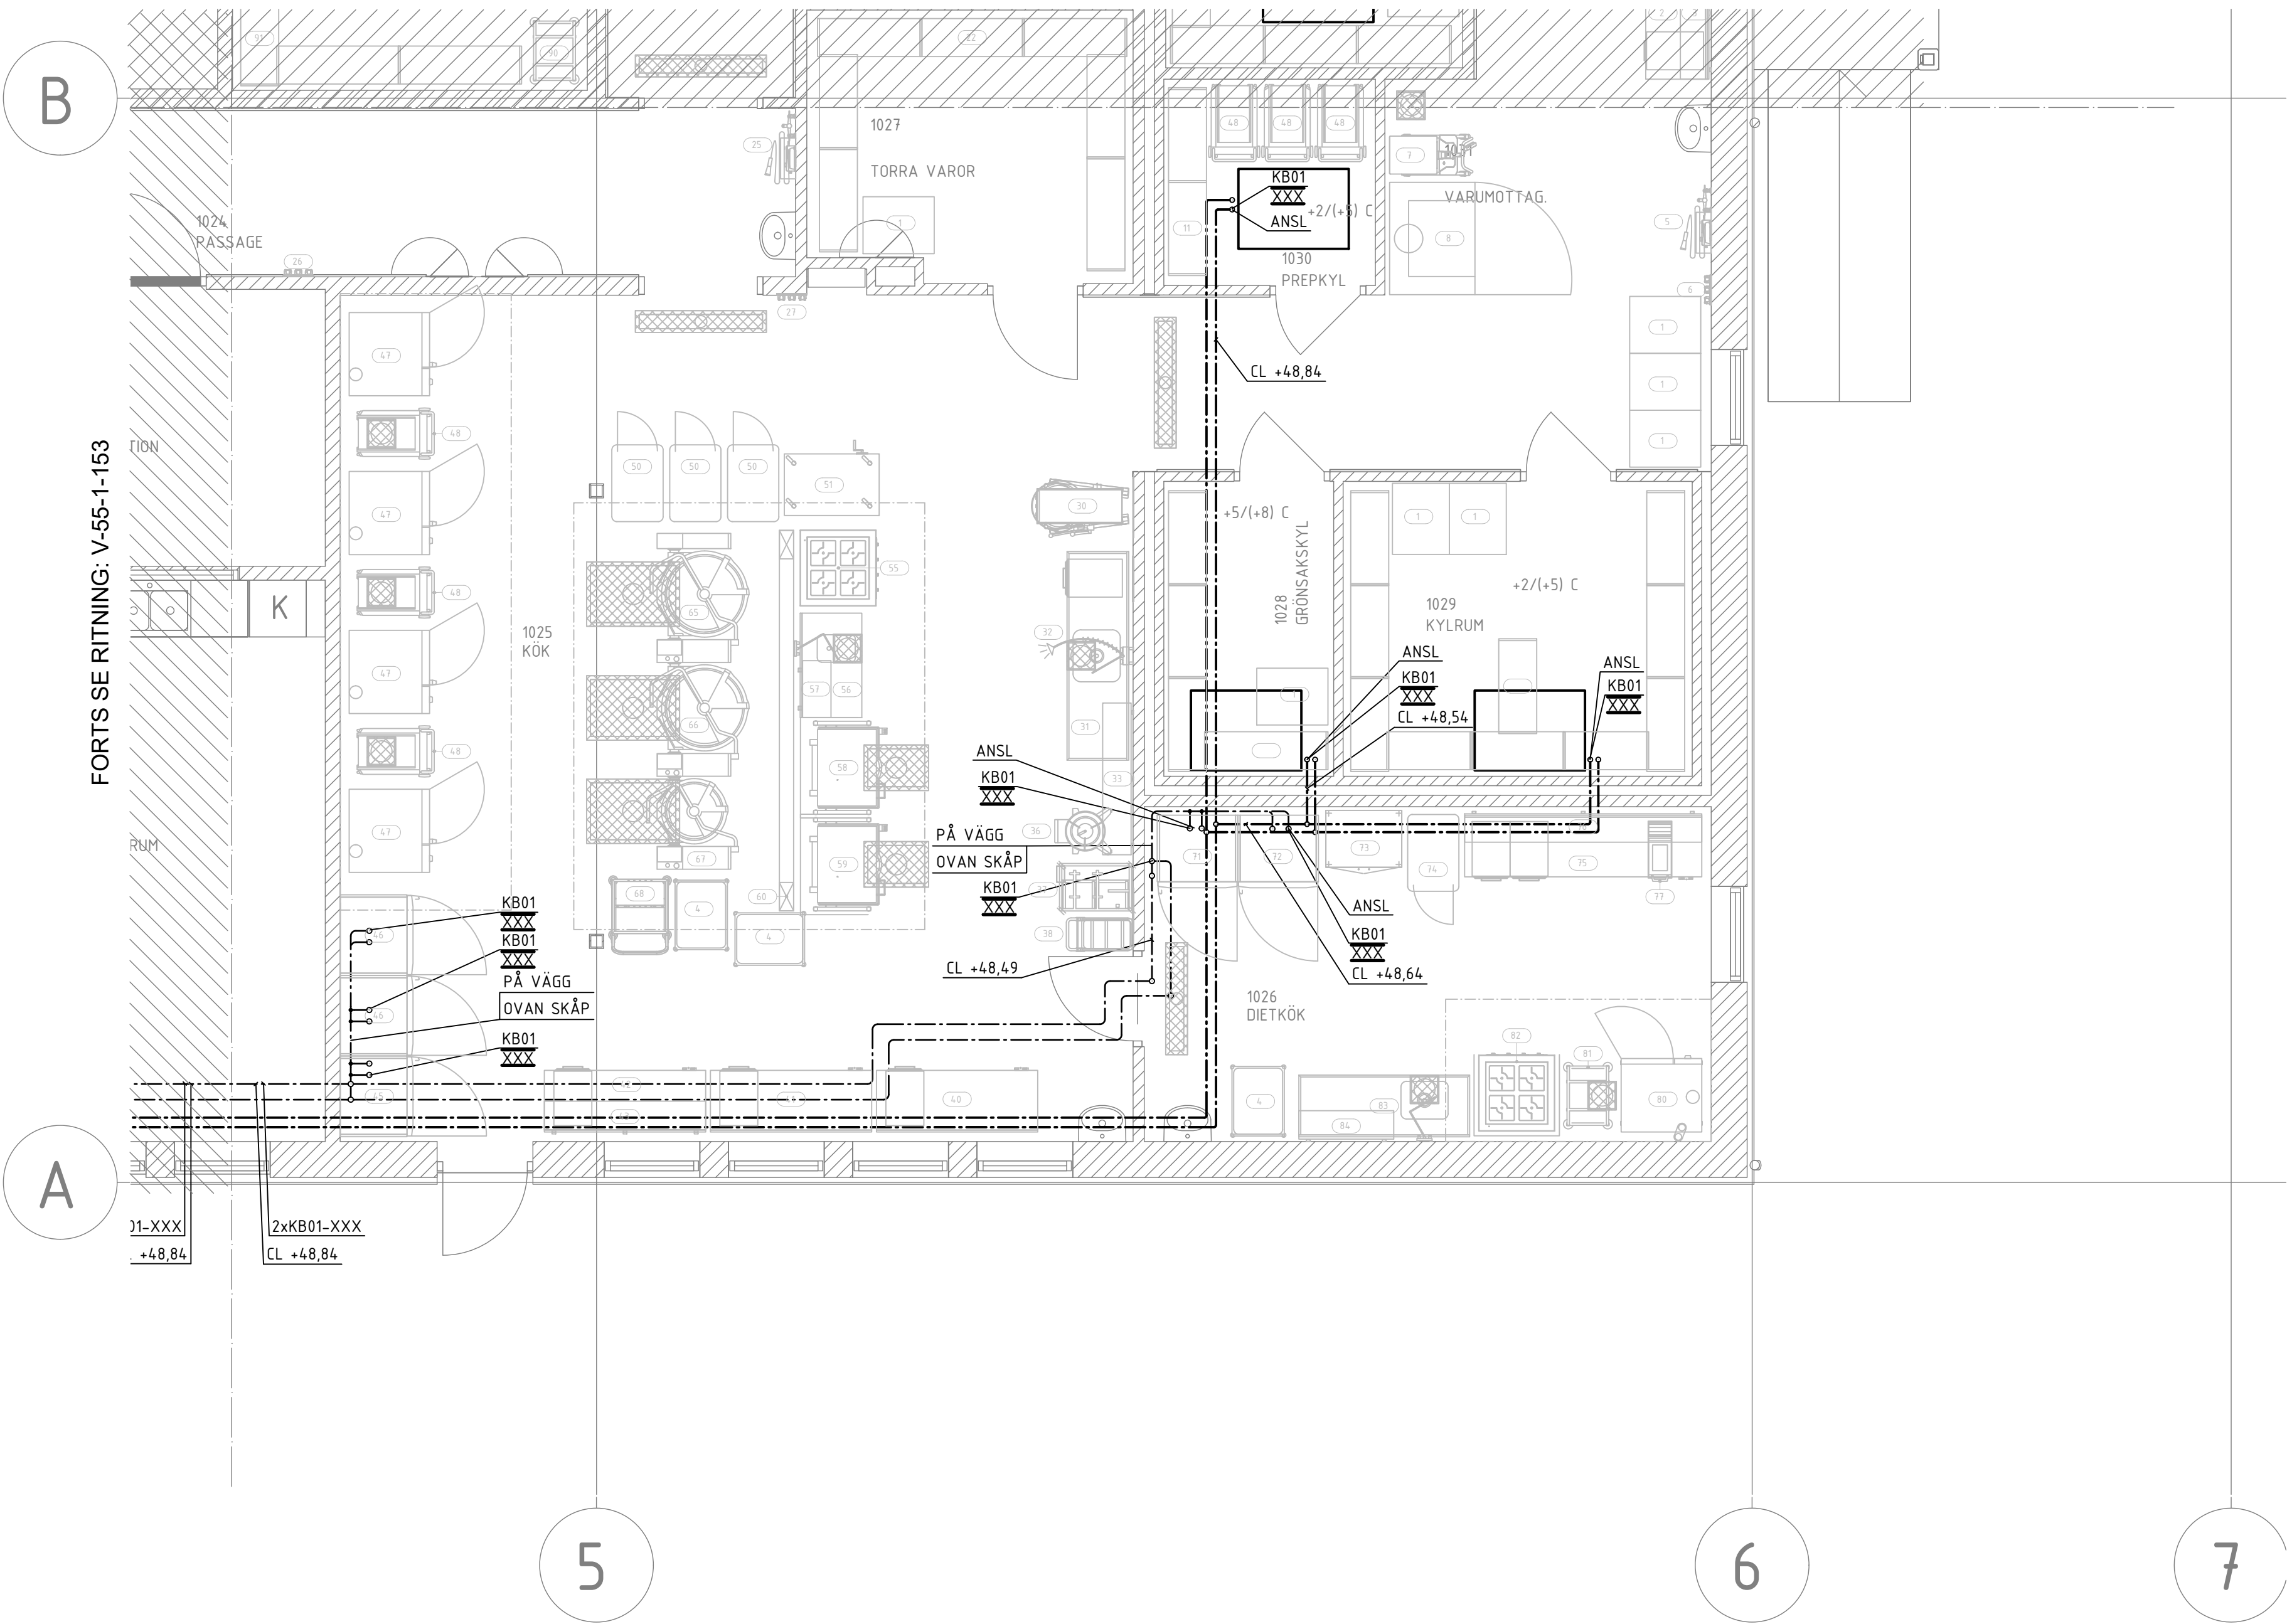