
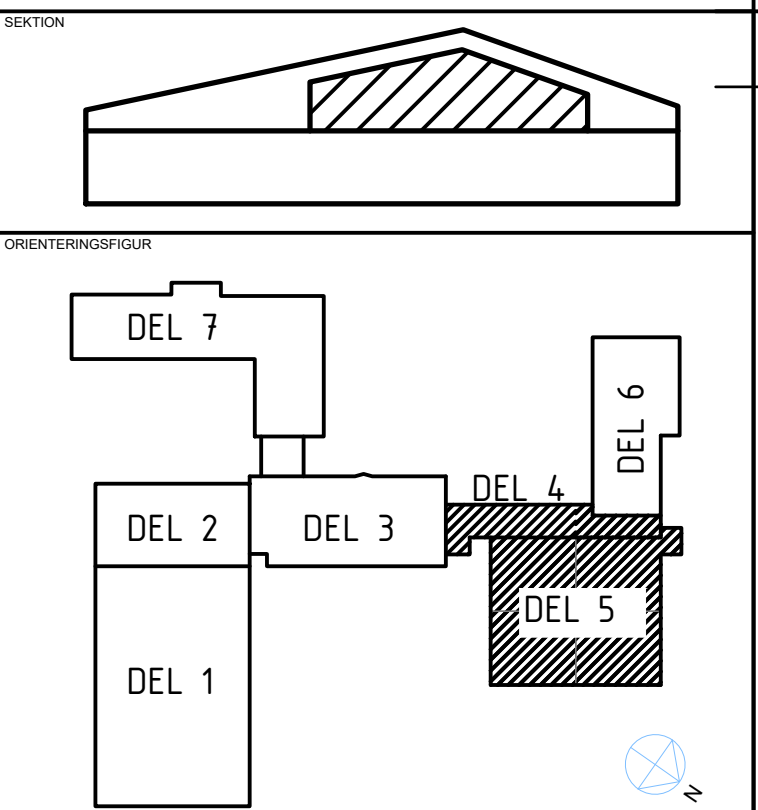
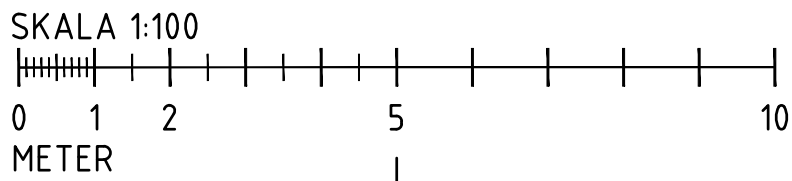


FÖRKLARINGSTEXT  
SE RITNING V-50-0-001

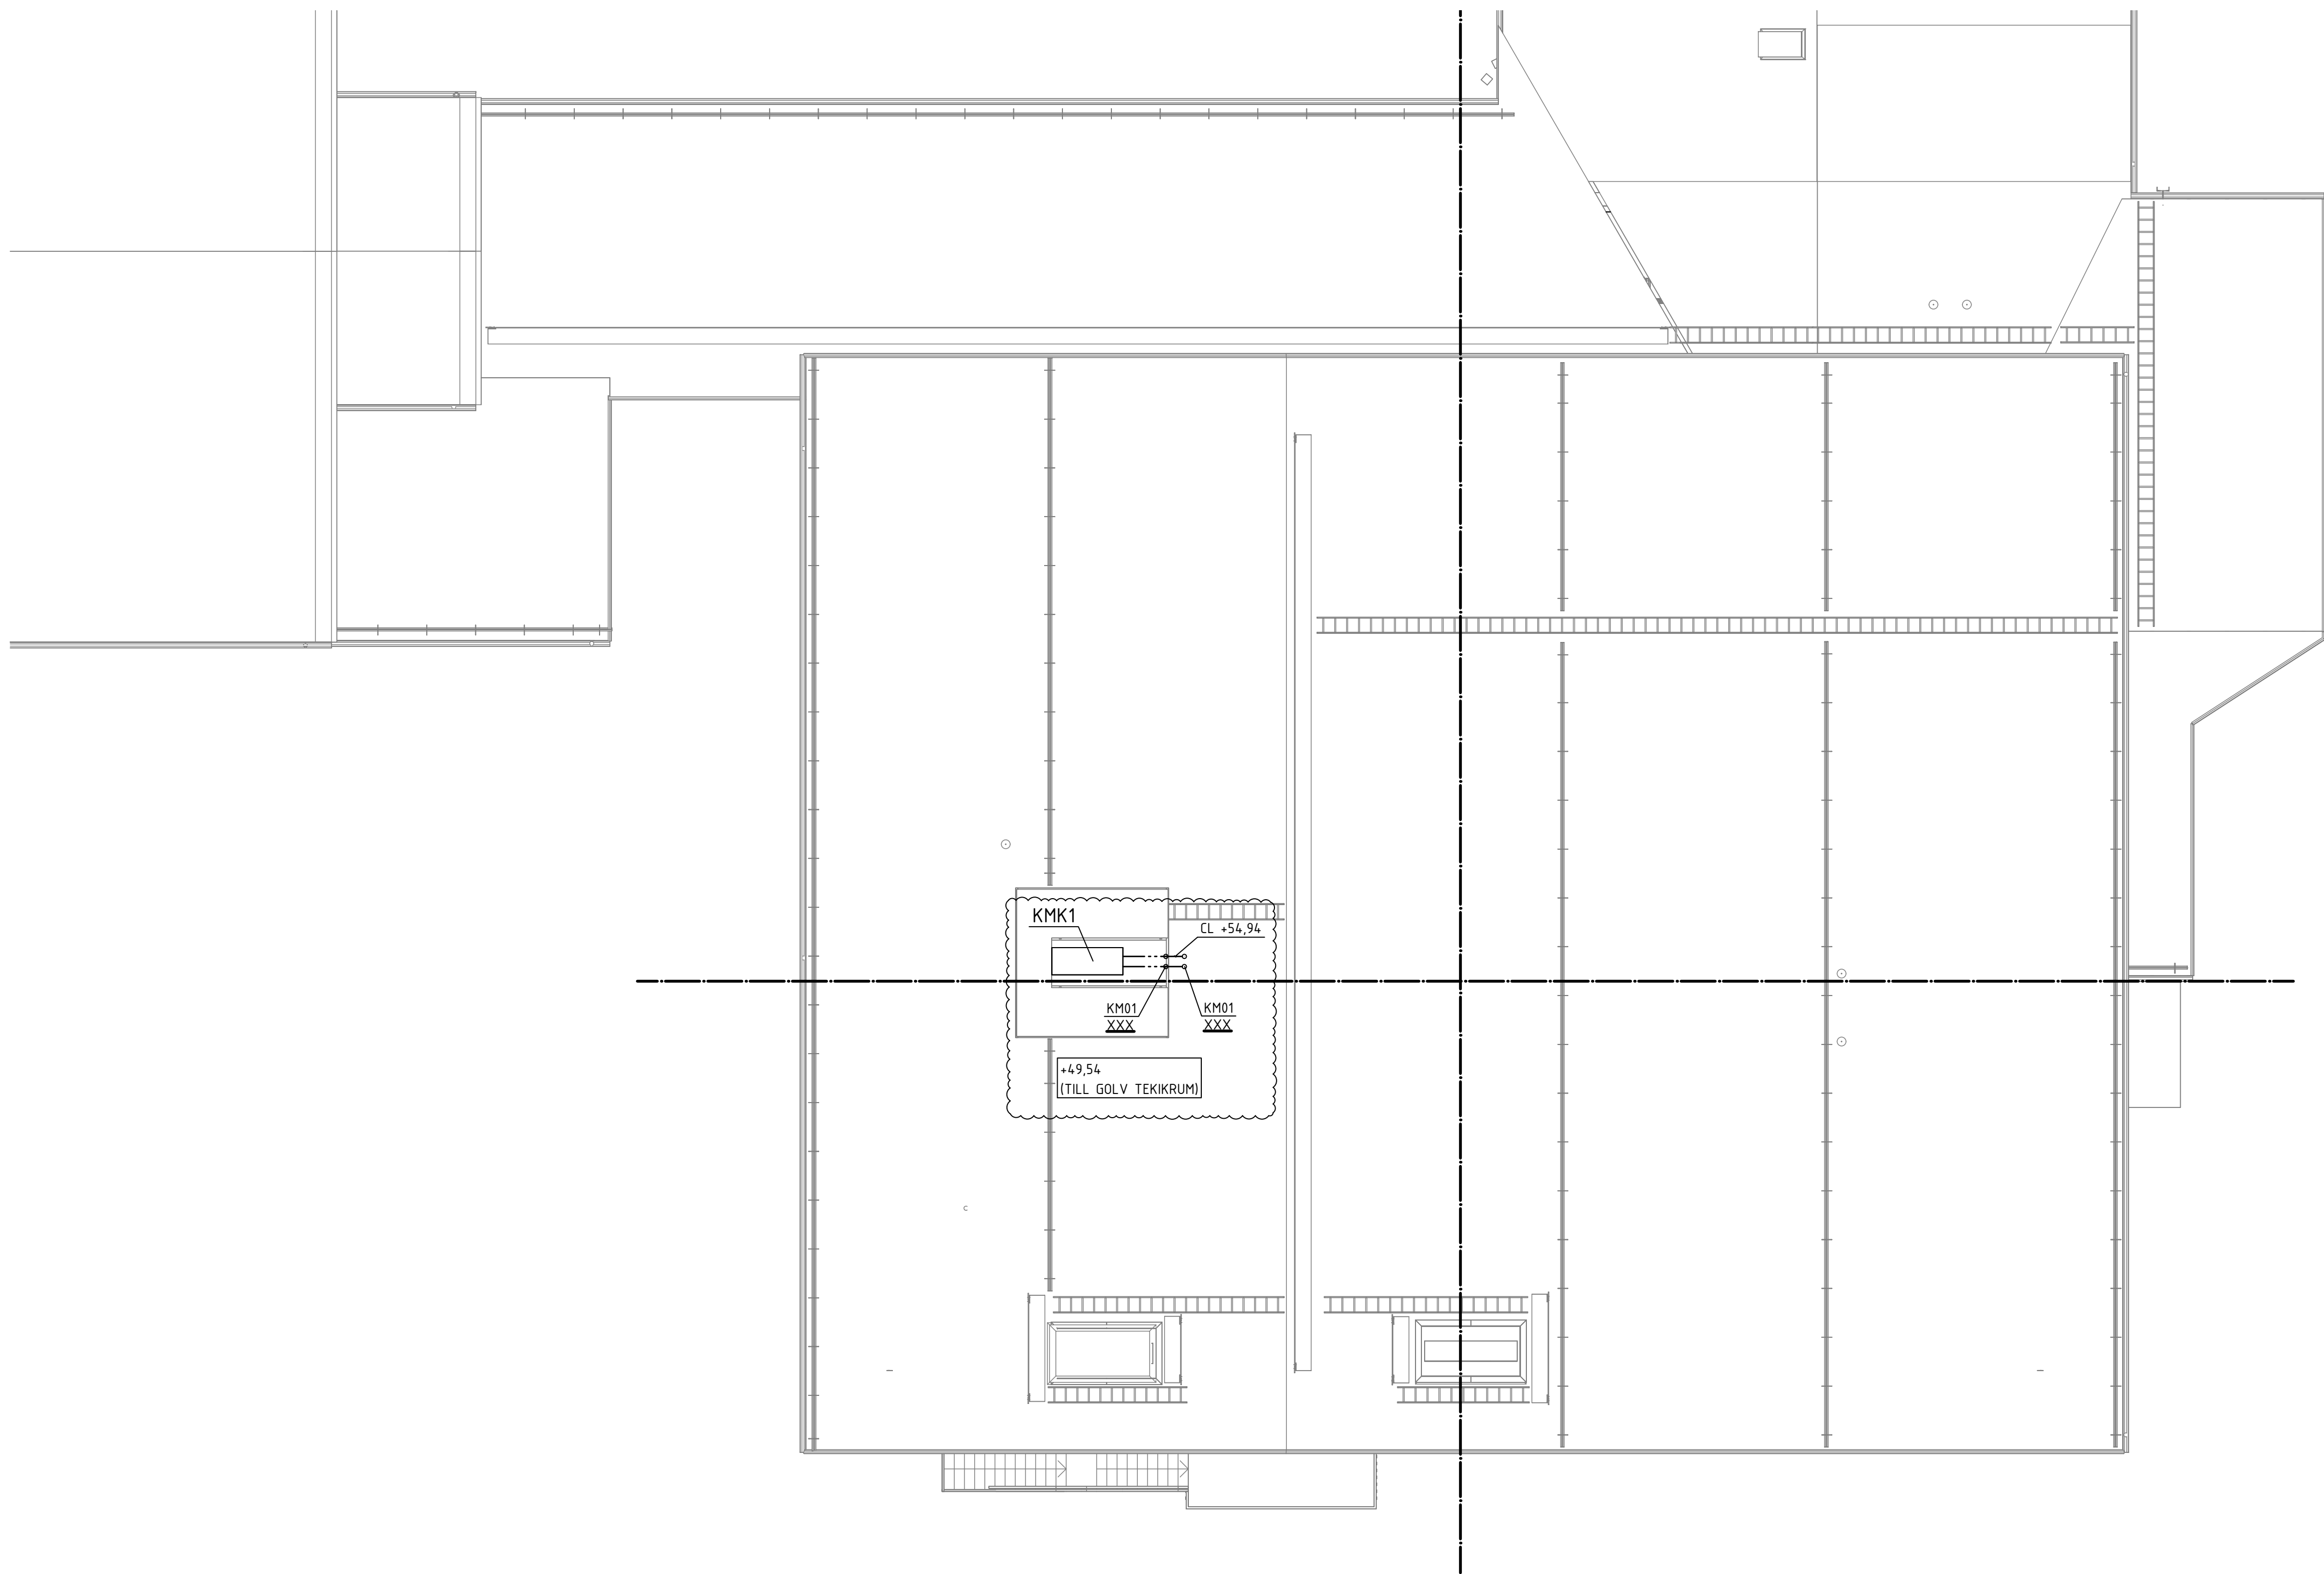

|                                                                                       |                       |                       |             |
|---------------------------------------------------------------------------------------|-----------------------|-----------------------|-------------|
| STATUS                                                                                |                       | FÖRFRÅGNINGSUNDERLAG  |             |
| HANDLING                                                                              |                       | BYGGHANDLING          |             |
| DATUM                                                                                 | 2025-01-31            | GODKÄND AV            | ÄNDRINGS PM |
| BESTÄLLARE                                                                            |                       | T.BERGSTRÖM           |             |
|  |                       | ROBERTSFORS<br>KOMMUN |             |
| PROJEKTNAMN                                                                           |                       |                       |             |
| CENTRALKÖK                                                                            |                       |                       |             |
| OMRÅDE                                                                                |                       |                       |             |
| ROBERTSFORS KOMMUN                                                                    |                       |                       |             |
| PROJEKTNUMMER                                                                         | ADRESS                |                       |             |
|                                                                                       | YTIRE RINGVÄGEN 4     |                       |             |
| DIARIENUMMER                                                                          | FÖRETAG               |                       |             |
|                                                                                       | FÖRDONET 1            |                       |             |
| DISCIPLIN                                                                             | FÖRETAG               |                       |             |
| VS                                                                                    | NORCONSULT SVERIGE AB |                       |             |
| OPPFÖRINGSNUMMER                                                                      | SKAPAD AV             |                       |             |
| 108 83 71                                                                             | MAN                   |                       |             |
| TELEFON                                                                               | KONTAKTPERSON         |                       |             |
| 010 141 80 00                                                                         | JONAS JOHANSSON       |                       |             |
| BYGGNADSVÄRDE                                                                         | (KLUBBHOJ RM 2000)    |                       |             |
|                                                                                       | +49,54 (FG)           |                       |             |
| VÄNINGSPLAN                                                                           | VÄNINGSDEL            | DELOMRÅDE             |             |
| 3                                                                                     |                       | DEL 4, 5              |             |
| SYSTEM                                                                                |                       |                       |             |
| 55 KYLINSTALLATIONER                                                                  |                       |                       |             |
| BESKRIVNING                                                                           |                       |                       |             |
| PLAN 3 - ÖVERSIKT                                                                     |                       |                       |             |
| RITNINGSKATEGORI                                                                      | SKALA                 |                       | FORMAT      |
| PLAN                                                                                  | 1:100                 |                       | A1          |
| DOKUMENTNUMMER                                                                        |                       |                       | ÄNDRING     |
| V-55-1-301                                                                            |                       | A                     |             |