

ALLMÄNT	
LUFTMÄNGDER ANGIVNA I l/s	
A	AVLUFT
U	UTELUFT
F	FRÅNLUFT
T	TILLUFT
LA	LUFTBEHANDLINGSAGGREGAT
KF	KANALFLÄKT
INKL	INKLÄDNAD AV KANAL





KANALTYPEN	
11	FÖRZINKAD STÅLPLÅT, TÄTHET 0
14	KANALER AV STÅLPLÅT I VÄTSKETÄT UTFÖRANDE,

TILLUFTSDON/FRÅNLUFTSDON
TD201 TAKDON, TILLUFT
TD801 TAKRIKSVENTIL, TILLUFTSDON
FD101 KONTROLLVENTIL
FD201 INFÄLLT TAKDON, FRÅNLUFT
FD301 TRÄDNÄTSGALLER, FRÅNLUFT
FD401 TRÄDNÄTSGALLER, CIRKULÄRT
IK201.1-2,-3 IMKÅPA, KÖK
IK202 IMKÅPA, DIET
IK401 DISKÅPA, TUNNELDISK
IK402 DISKÅPA, GROVDISK
OD101/102 ÖVERLUFTSDON

UTEFLUFTS/AVFLUFTSÄGALLER/HUVAR	
AD101	AVFLUFTSVÄGGALLER
AD102	AVFLUFTSVÄGGHUV
AD103	AVFLUFTSVÄGGALLER
AD201	AVFLUFTSHUV TAKPLACERAD FÖR LA01
UD101	UTEFLUFTSVÄGGALLER
UD102	UTEFLUFTSVÄGGHUV
UD201	UTEFLUFTSHUV TAKPLACERAD
AUD201	KOMBIHUV

ÖVRIGT	
LD101	LUDDÄMPARE, CIRKULÄR ANSLUTNING
LD201	REKTANGULÄR LUDDÄMPARE MED INV. BAFFLAR
LD202	REKTANGULÄR LUDDÄMPARE MED INV. BAFFLAR
LD501	FLEXIBEL KANAL LUDDÄMPARE
RL101	RENSLUCKA CIRKULÄR
RL102	RENSLUCKA REKTANGULÄR
SP101	VRIDSPJÄLL, MANUELLT
SP201	INJUSTERINGSPJÄLL TYP IRIS
SP401	REKTANGULÄR SPJÄLL, MANUELLT
SP701	CIRKULÄRT SPJÄLL MED HYLLO FÖR MOTOR
SP702	REKTANGULÄRT SPJÄLL MED HYLLO FÖR MOTOR
SP8XX	SPJÄLL MED MOTOR

ISOLERING	
/K403	KONDENSISOLERING 30mm
/K405	KONDENSISOLERING 50mm
/K713	CELLGUMMI, ULTIMA 13 MM
/V315	VÄRMEISOLERING, 150mm
/B106	E160 ISOLERING

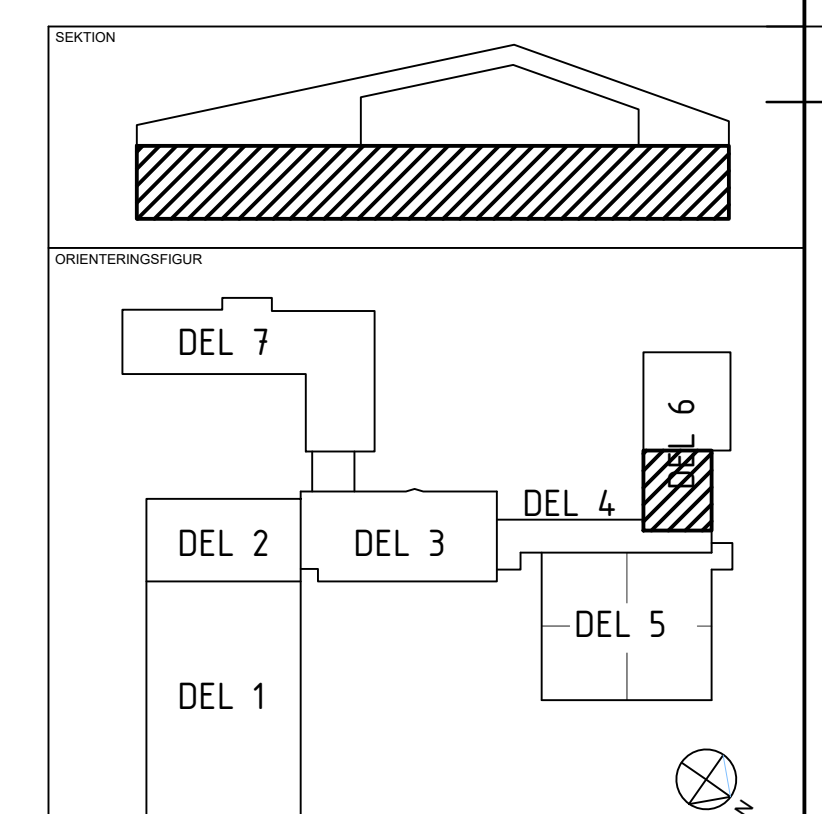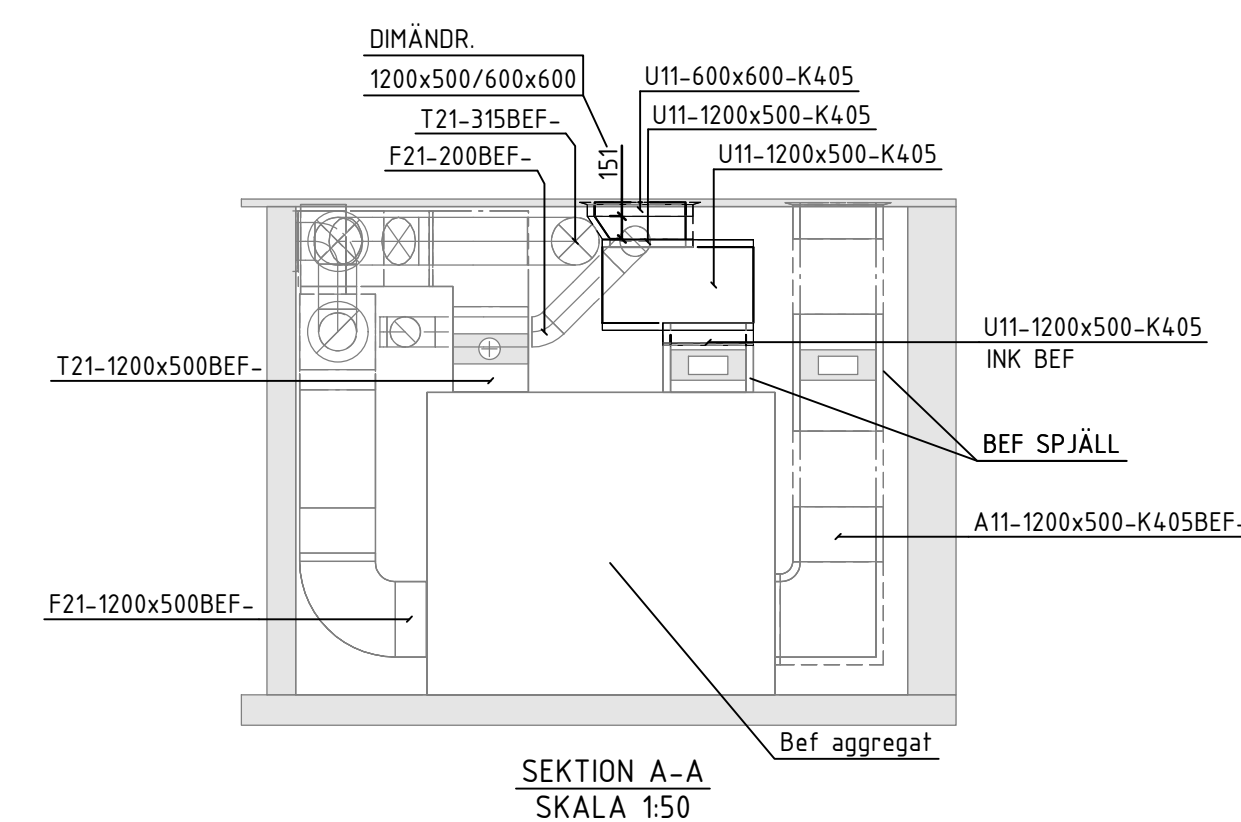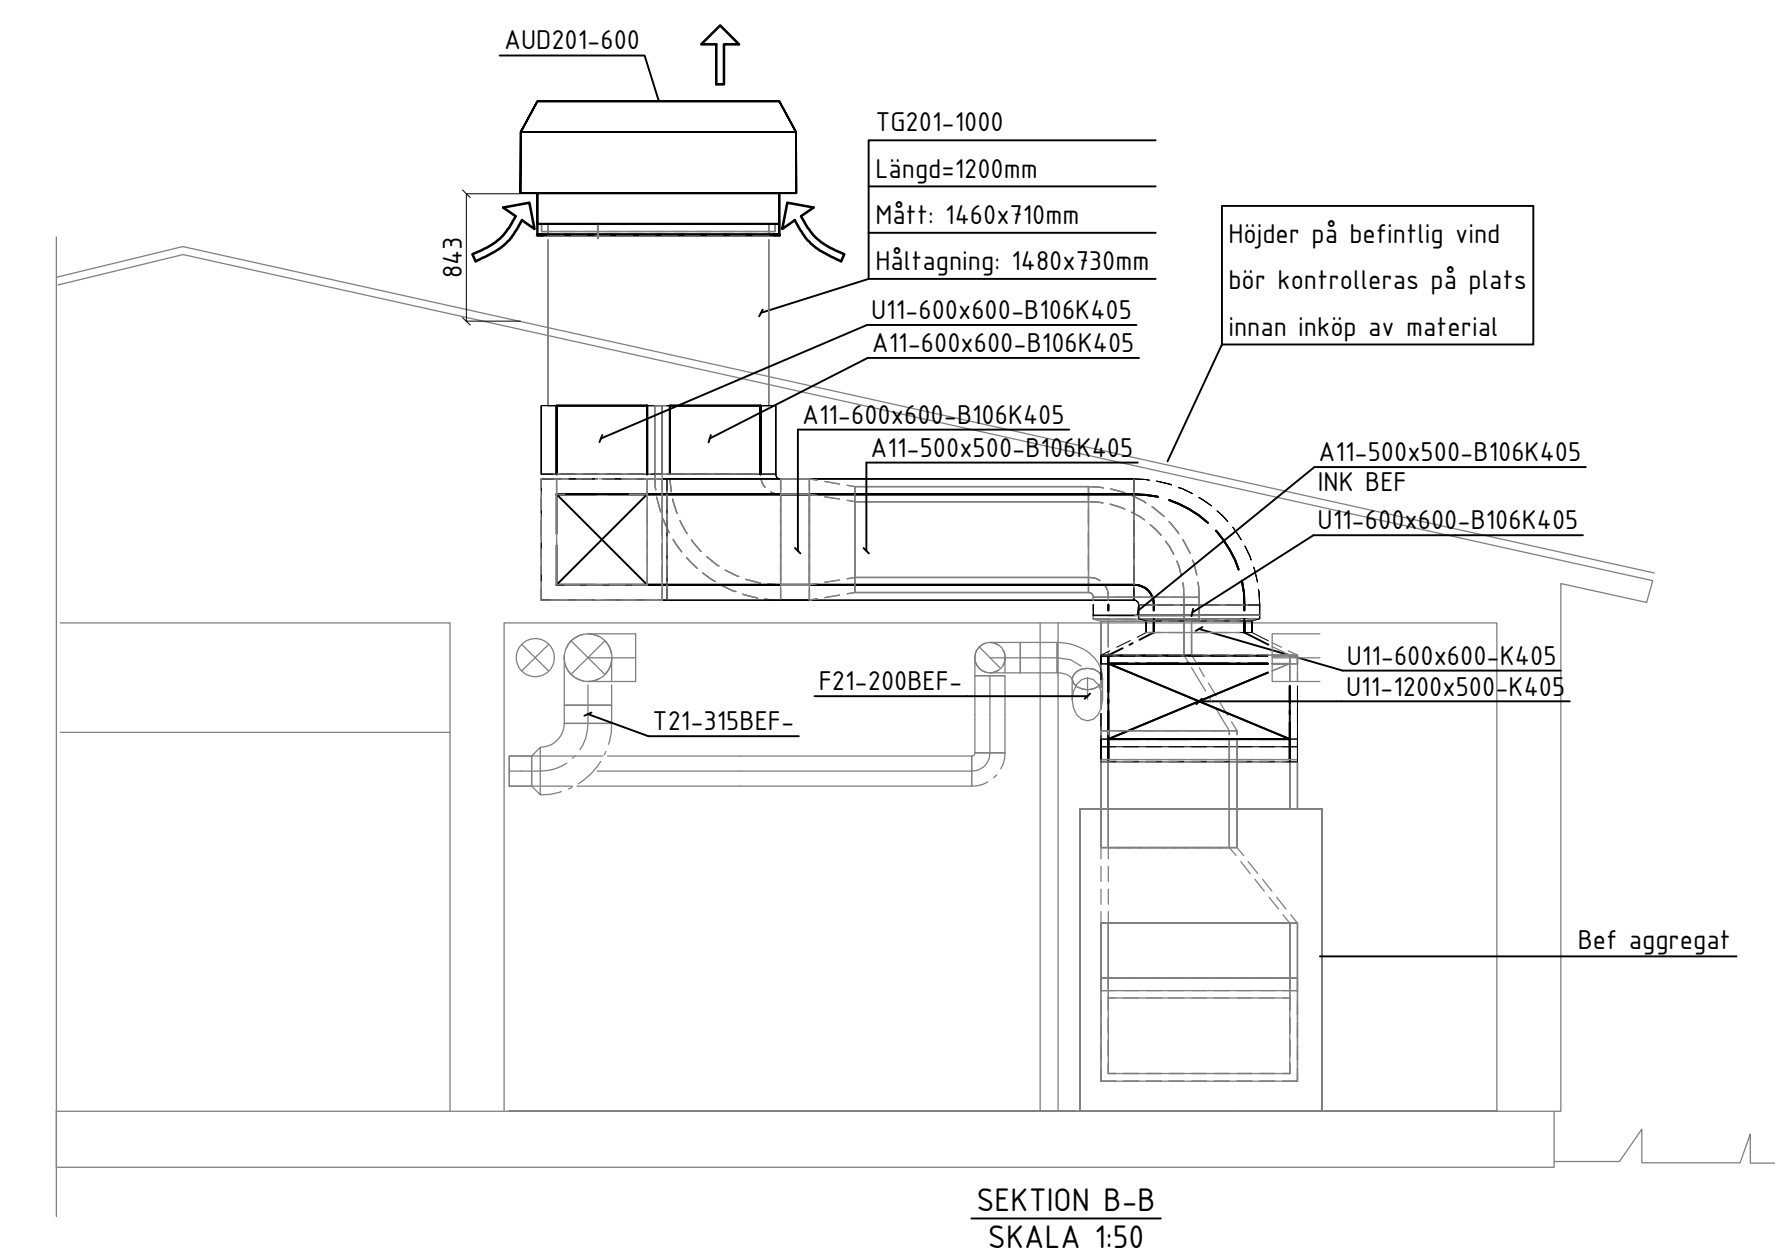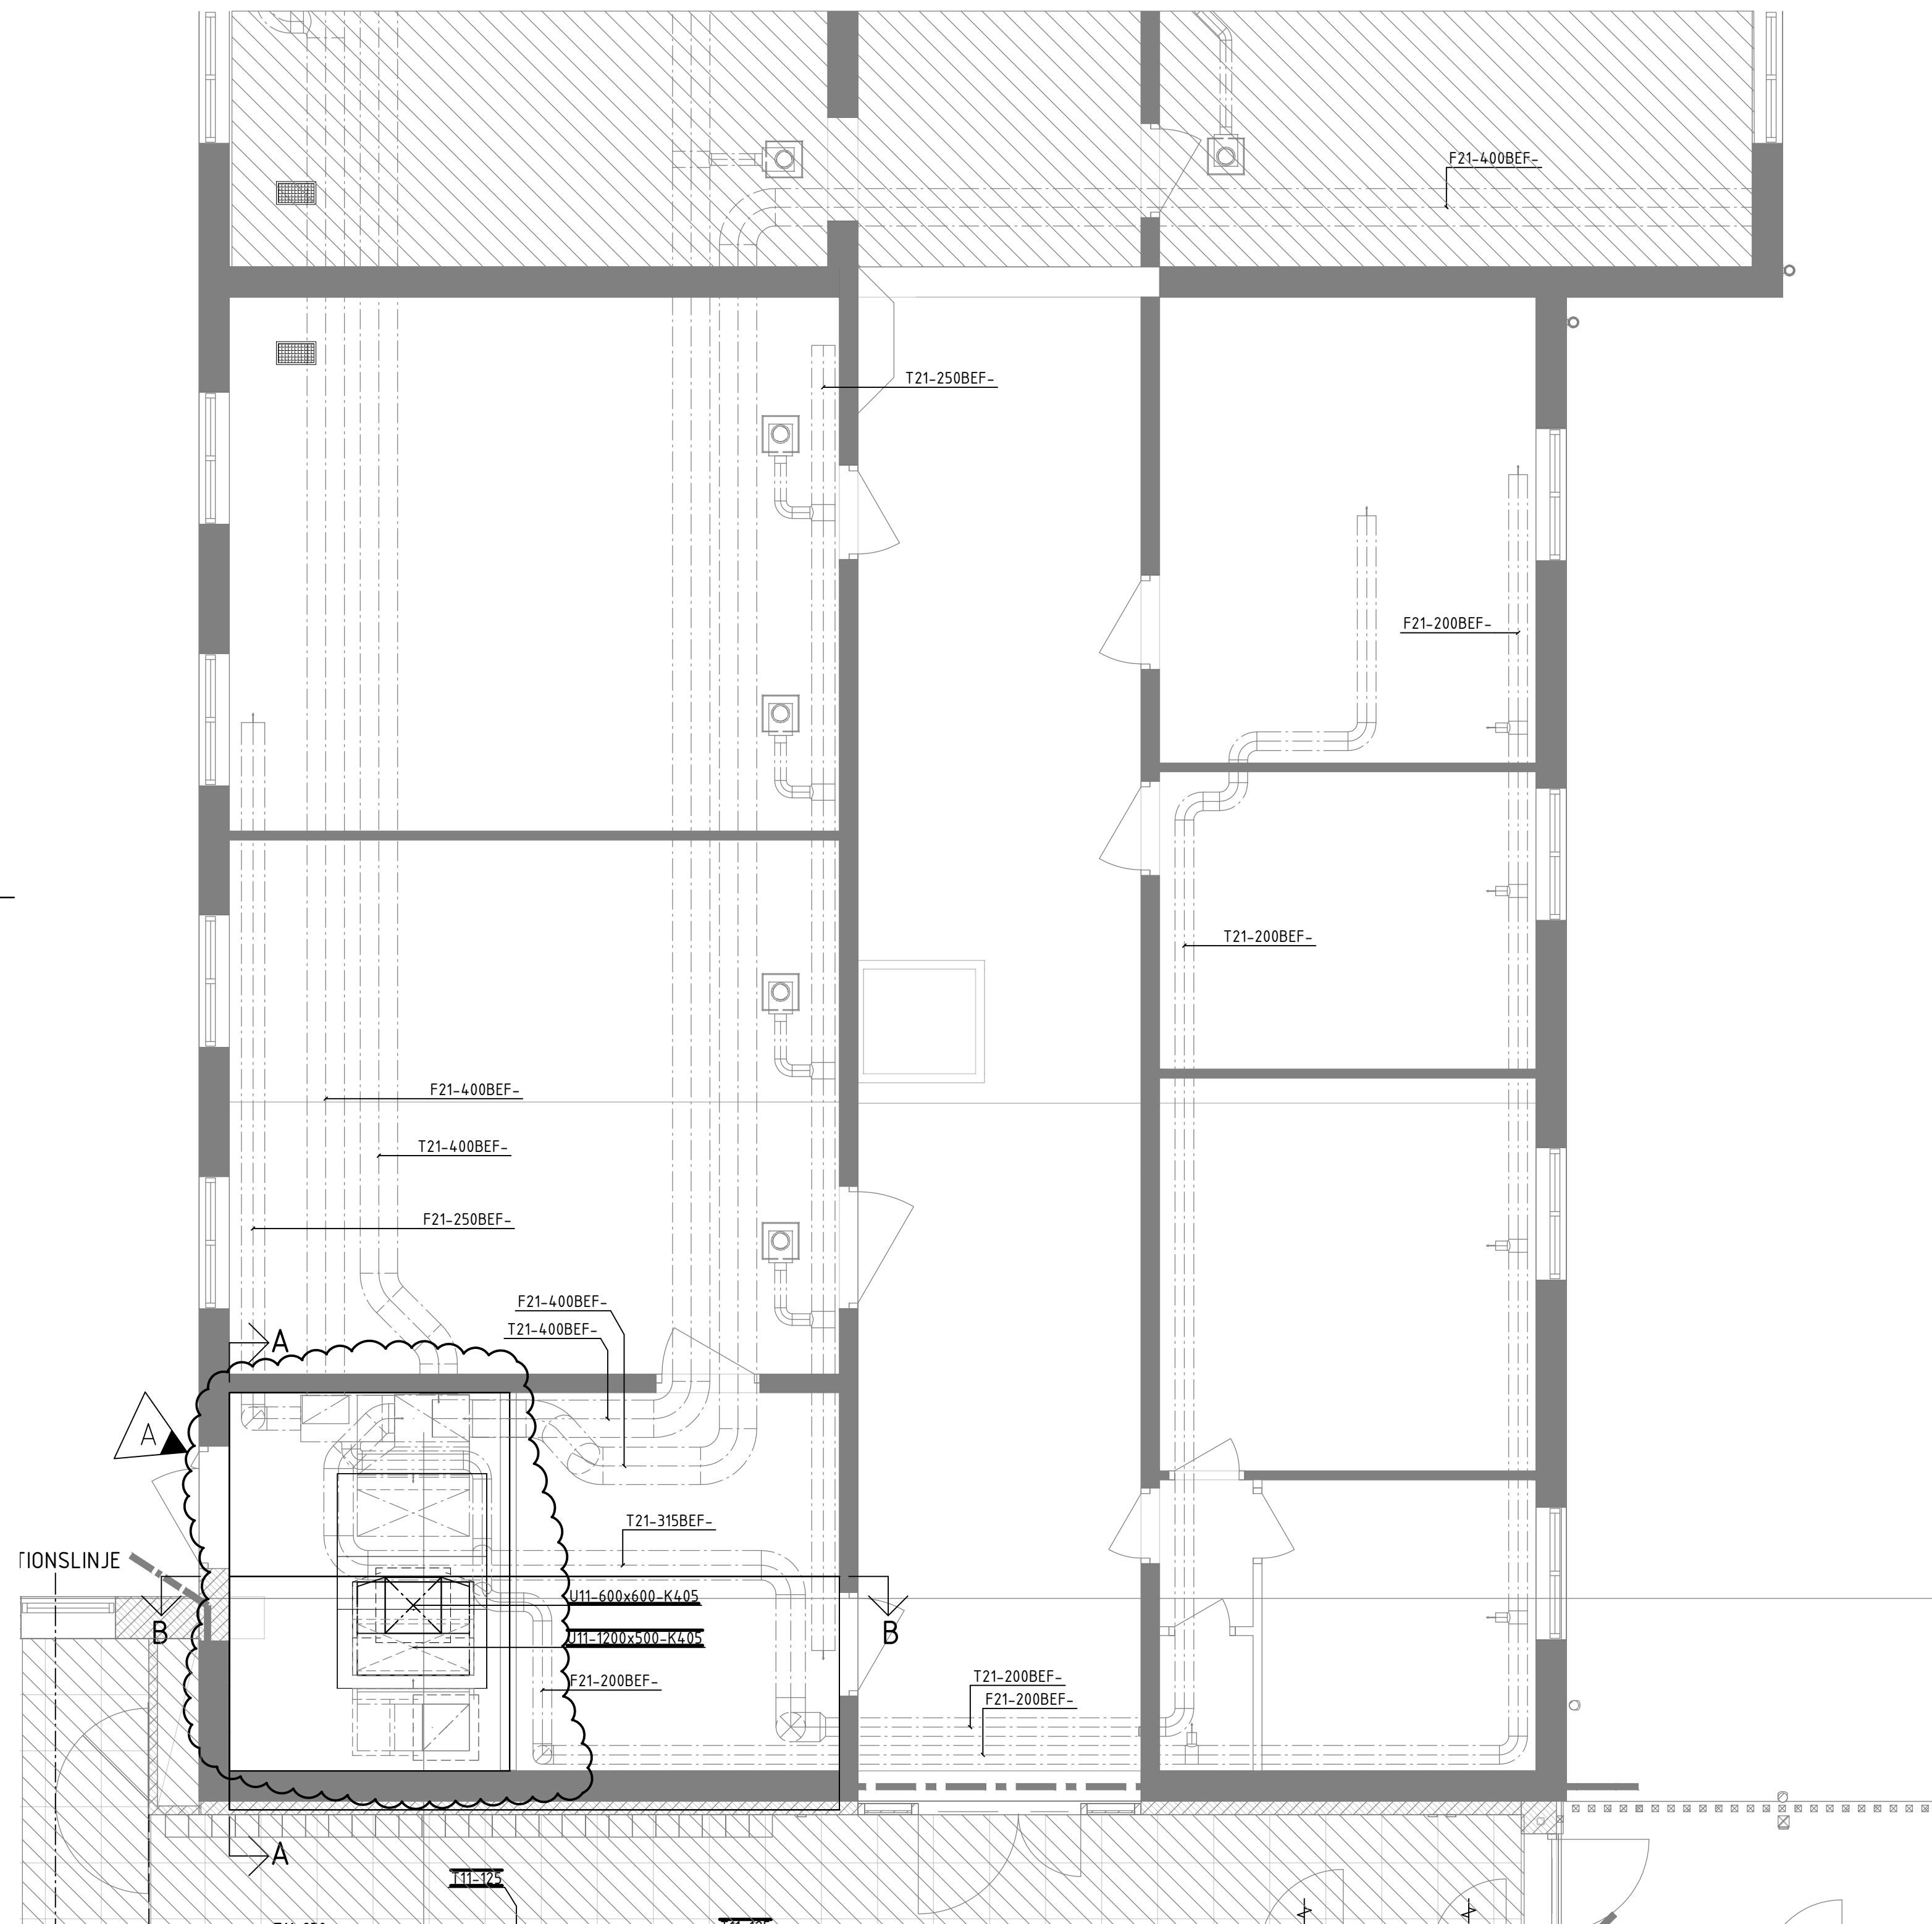

STATUS	FÖRFRÅGNINGSUNDERLAG
--------	----------------------

HANDLING		
-		
DATUM 2025-01-31	GÖDKÄND AV DAVID N.BACKMAN	ÄNDRINGS PM KFU01



ROBERTSFORS KOMMUN
PROJEKTNAMN
CENTRALEKÖK
OMRADE
ROBERTSFORS KOMMUN

PROJEKTNUMMER	ADRESS
-	YTTRRE RINGVANG 4
DIARENUMMER	PÅSTYGT
-	FÖRDET 1
ORGAN	BYGGFÄRD
LE	NORCONSULT SVERIGE AB
UPPDRAGSNUMMER	SKAFTAD AV
108 83 71	PLT
TELEFON	KONTAKTPERSON
010 141 80 00	DAVID NYMAN BACKMAN
BYGGANSÄTTER	PRISER I KRÖNOR
-	+44,60, +45,07, +45,54 (FG)
VÄRNINGSPÅN	DELCEMÅDE
1	4, 5

SYSTEM		57 SAMMANSATT LUFTBEHANDLING	
SPEDIKATION			
DELPLAN			
RITNINGSKATEGORI		SKALA	FORMAT
PLAN		1:50	A1
DOKUMENTNUMMER		ANDRING	
V-57-1-161		A	

SKALA 1:200

0 1 2 5 10 15 20

METER

FILNAMN: FL: N\108\83\108837\5 ARBETSMATERIAL\02 BM\VV\20\MODELLUMPIDWG PLOTTAD: 2025-01-31 15:42 AV ANVÄNDARE: PETELU