

FÖRKLARINGAR:

ALLMÄNT	
LUFTMÄNGDER ANGIVNA I l/s	
A	AVLUFT
U	UTELUFT
F	FRÅNLUFT
T	TILLUFT
LA	LUFTBEHANDLINGSAGGREGAT
KF	KANALFLÄKT
INKL	INKLÄDNAD AV KANAL

T-rör, X-rör, böj, T-rör med extra påstick ska vara fabriks tillverkade produkter.



KANALTYP	
11	FÖRZINKAD STÅLPLÅT, TÄTHET C
14	KANALER AV STÅLPLÅT I VÄTSKETÄT UTFÖRANDE,

TILLUFTSDON/FRÅNLUFTSDON	
TD201	TAKDON, TILLUFT
TD801	TALLRIKSVENTIL, TILLUFTSDON
FD101	KONTROLLVENTIL
FD201	INFALLT TAKDON, FRÅNLUFT
FD301	TRÄDNÄTSGALLER, FRÅNLUFT
FD401	TRÄDNÄTSGALLER, CIRKULÄRT
IK201-1,-2,-3	IMKÅPA, KÖK
IK202	IMKÅPA, DIET
IK401	DISKKÅPA, TUNNELDISK
IK402	DISKKÅPA, GROVDISK
OD101/102	ÖVERLUFTSDON

UTELUFTS/AVLUFTSGALLER/HUVAR	
AD101	AVLUFTSVÄGGALLER
AD102	AVLUFTSVÄGGHUV
AD103	AVLUFTSVÄGGALLER
AD201	AVLUFTSHUV TAKPLACERAD FÖR LA01
UD101	UTELUFTSVÄGGALLER
UD102	UTELUFTSVÄGGHUV
UD201	UTELUFTSHUV TAKPLACERAD
AUD201	KOMBIHUV

ÖVRIGT	
LD101	LJUDDÄMPARE, CIRKULÄR ANSLUTNING
LD201	REKTANGULÄR LJUDDÄMPARE MED INV. BAFFLAR
LD202	REKTANGULÄR LJUDDÄMPARE MED INV. BAFFLAR
LD501	FLEXIBEL KANALLJUDDÄMPARE
RL101	RENSLUCKA CIRKULÄR
RL102	RENSLUCKA REKTANGULÄR
SP101	VRIDSPJÄLL, MANUELLT
SP201	INJUSTERINGSSPJÄLL TYP IRIS
SP401	REKTANGULÄR SPJÄLL, MANUELLT
SP701	CIRKULÄRT SPJÄLL MED HYLLE FÖR MOTOR
SP702	REKTANGULÄRT SPJÄLL MED HYLLE FÖR MOTOR
SP8XX	SPJÄLL MED MOTOR

ISOLERING	
/K403	KONDENSISOLERING 30mm
/K405	KONDENSISOLERING 50mm
/K713	CELLGUMMI, ULTIMA 13 MM
/V315	VÄRMEISOLERING, 150mm
/B106	E160 ISOLERING

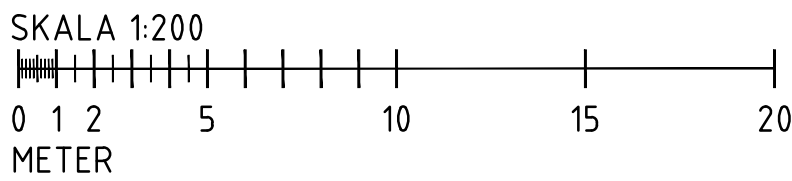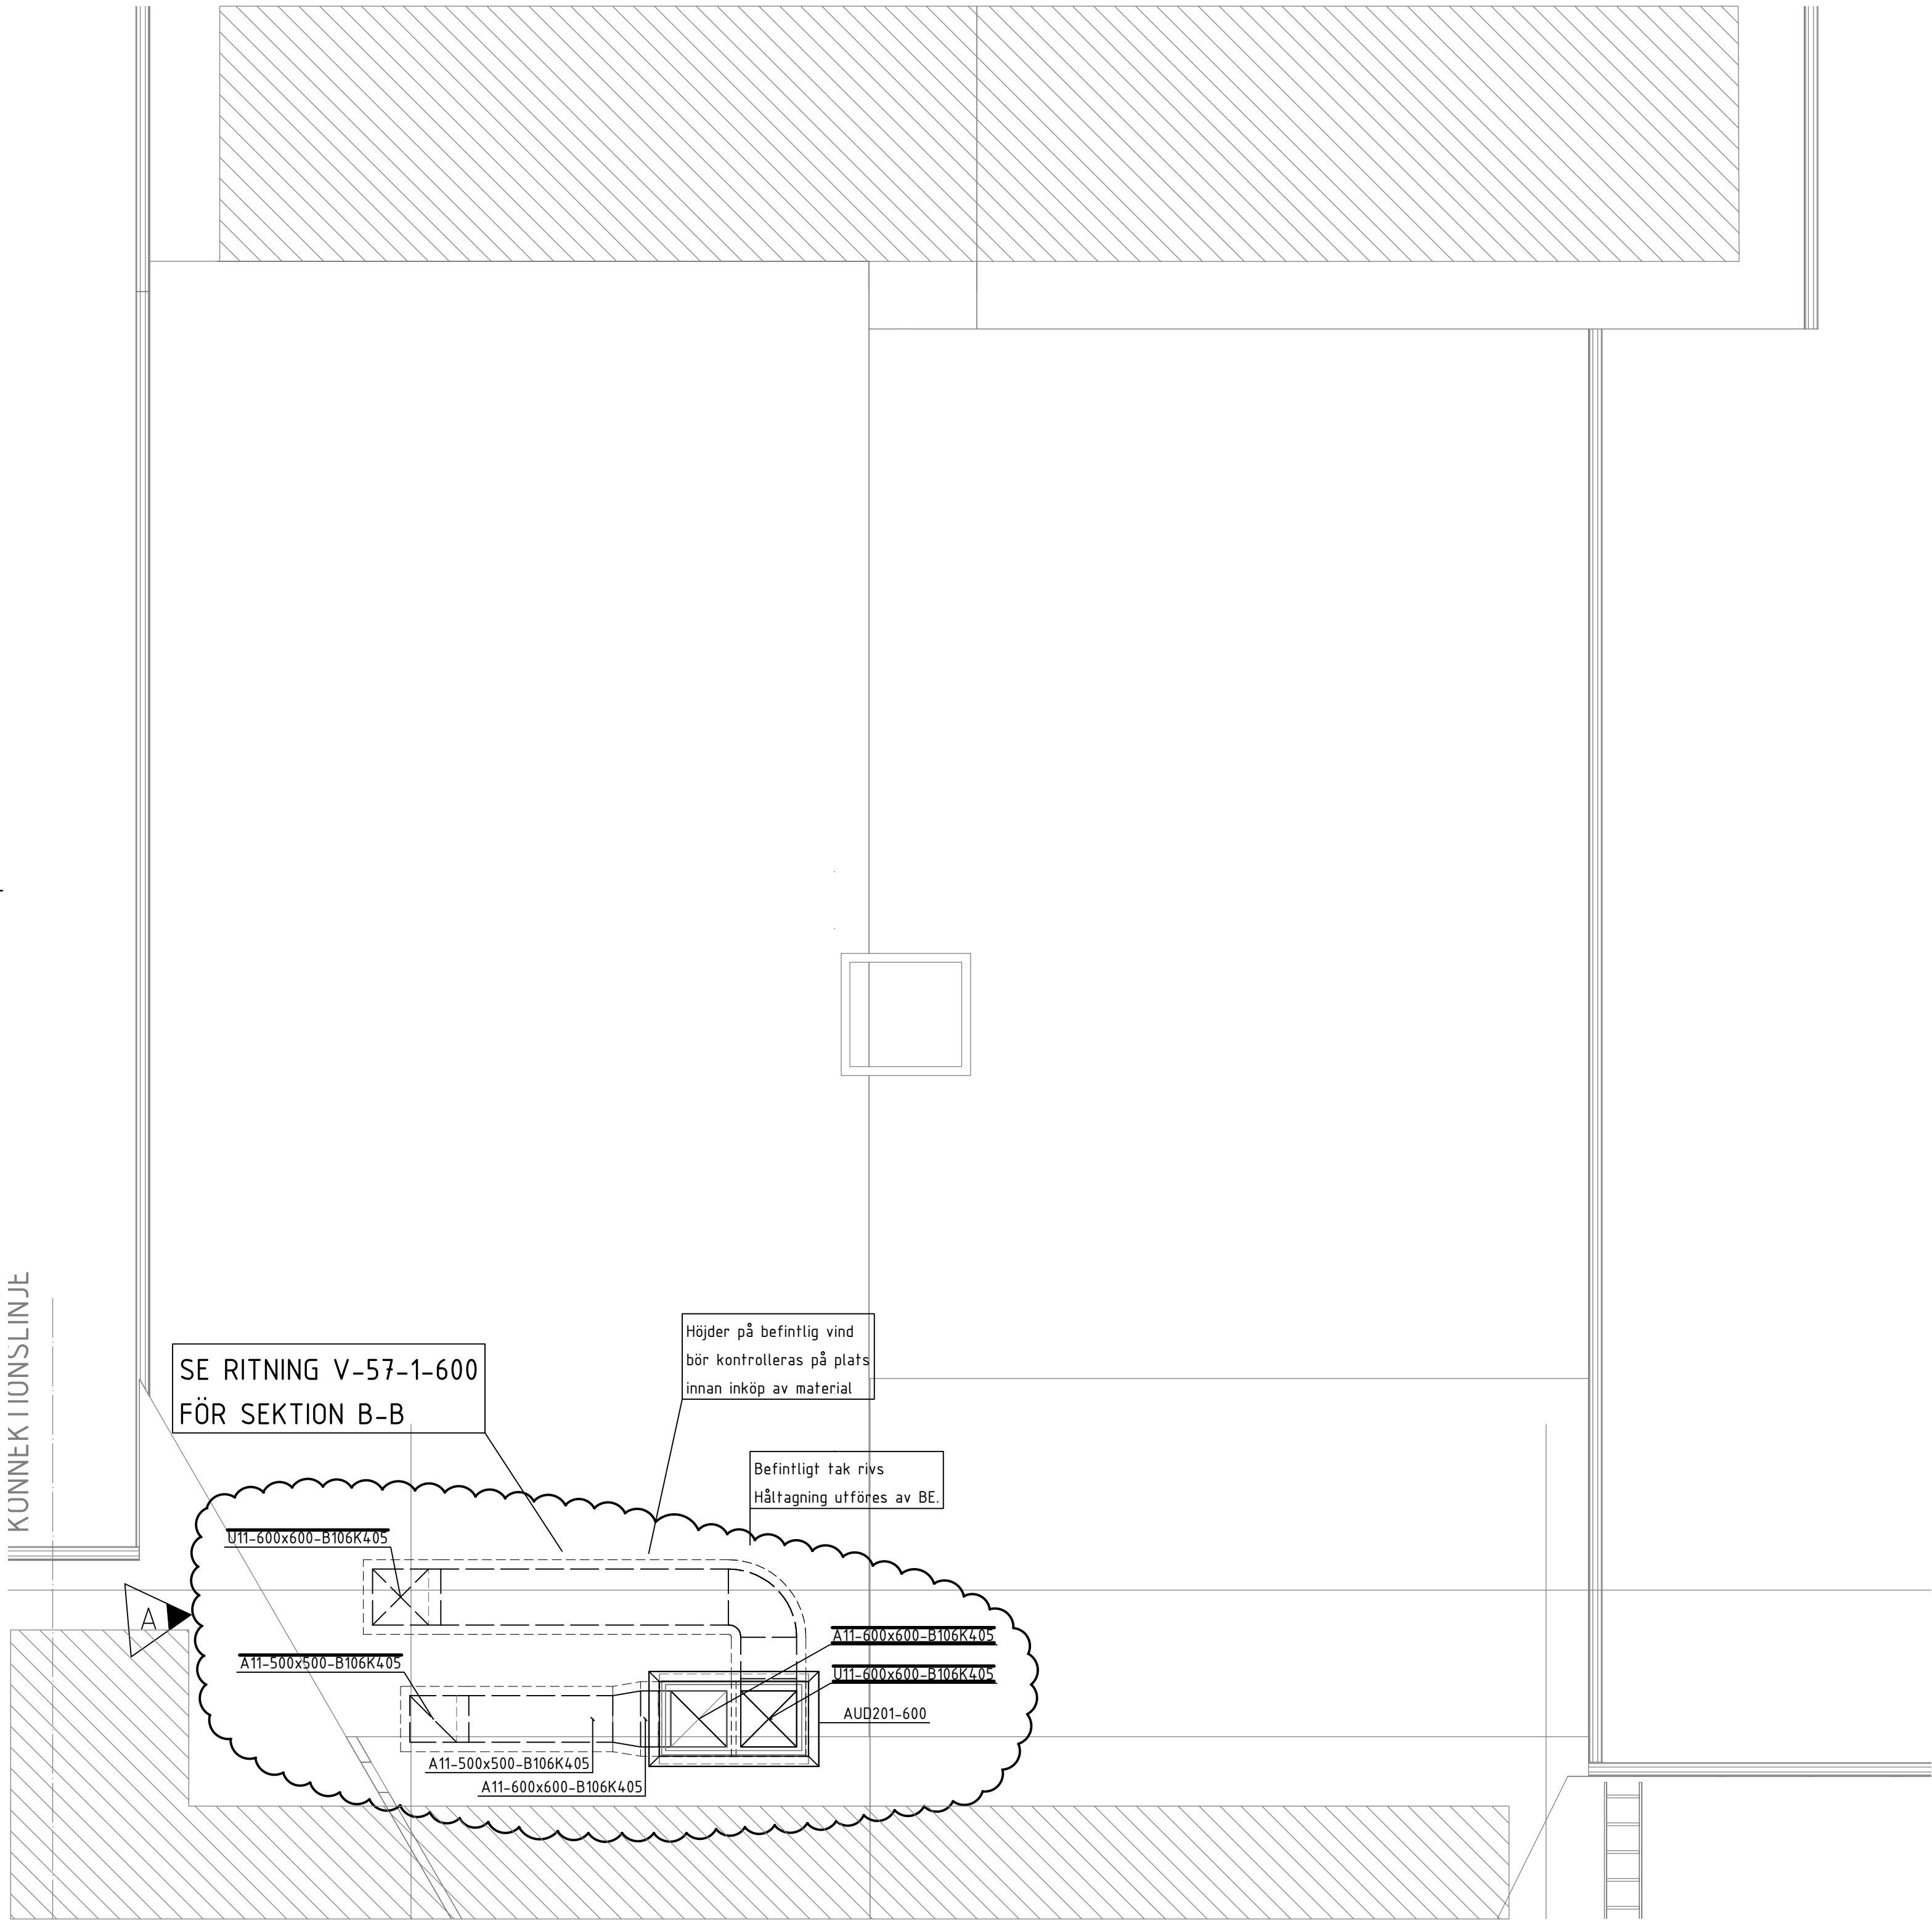

SEKTION

ORIENTERINGSPOLAR

STATUS

FÖRFRÅGNINGSUNDERLAG

HANDLING

-

DATUM

2025-01-31

GODKÄND AV

DAVID N.BACKMAN

ÄNDRINGS PM

KFU01

BESTÄLLARE

ROBERTSFORS KOMMUN

ROBERTSFORS KOMMUN

CENTRALKÖK

ROBERTSFORS KOMMUN

OMRADE

PROJEKTNAMN

PROJEKTNUMMER

DIARIENUMMER

DISCIPLIN

UPPDRAGSNUMMER

TELEFON

BYGGNADSVÄRKE

VÄNINGSPLAN

1

VÄNINGSDEL

-

DELOMRADE

DEL 4, 5

ADRESS

YTTRE RINGVÄGEN 4

FASTIGHET

FORDONET 1

FÖRETAG

NORCONSULT SVERIGE AB

SKAPAD AV

PLT

KONTAKTPERSON

DAVID NYMAN BACKMAN

PLUSHÖJD (RH 2000)

+44,60, +45,07, +45,54 (FG)

SYSTEM

57 SAMMANSATT LUFTBEHANDLING

SPESIFIKATION

DELPLAN

RITNINGSKATEGORI

PLAN

SKALA

1:50

FORMAT

A1

DOKUMENTNUMMER

V-57-1-261

ÄNDRING

A

FILNAMN: P:\1\100-03\ROBERTSFORS\ROBERTSFORS\CENTRALKÖK\2025-01-31\0305 AV ANVÄNDARE: FETU