
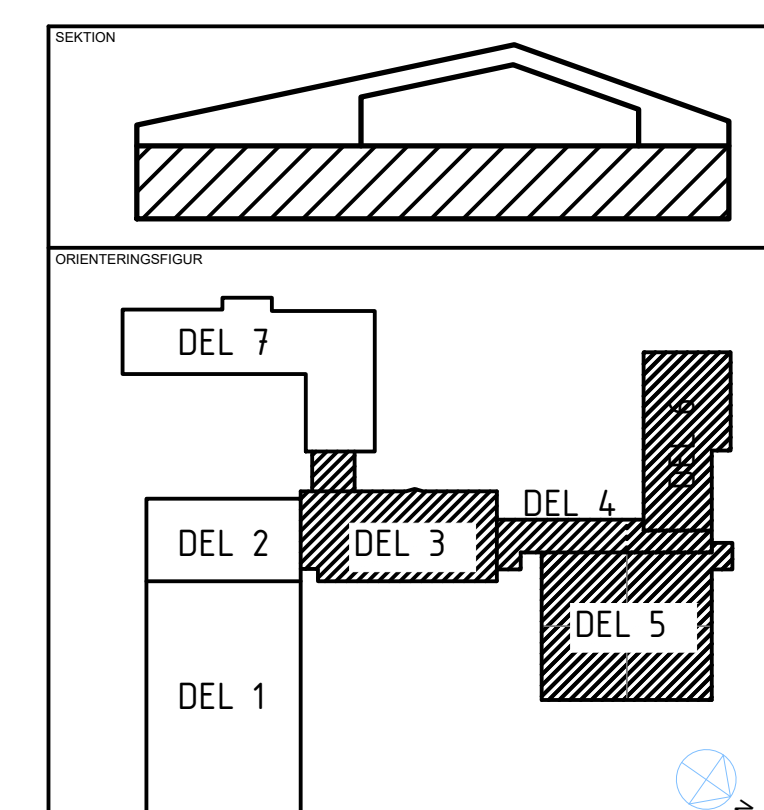


FÖRKLARINGSTEXT
SE RITNING V-50-0-001

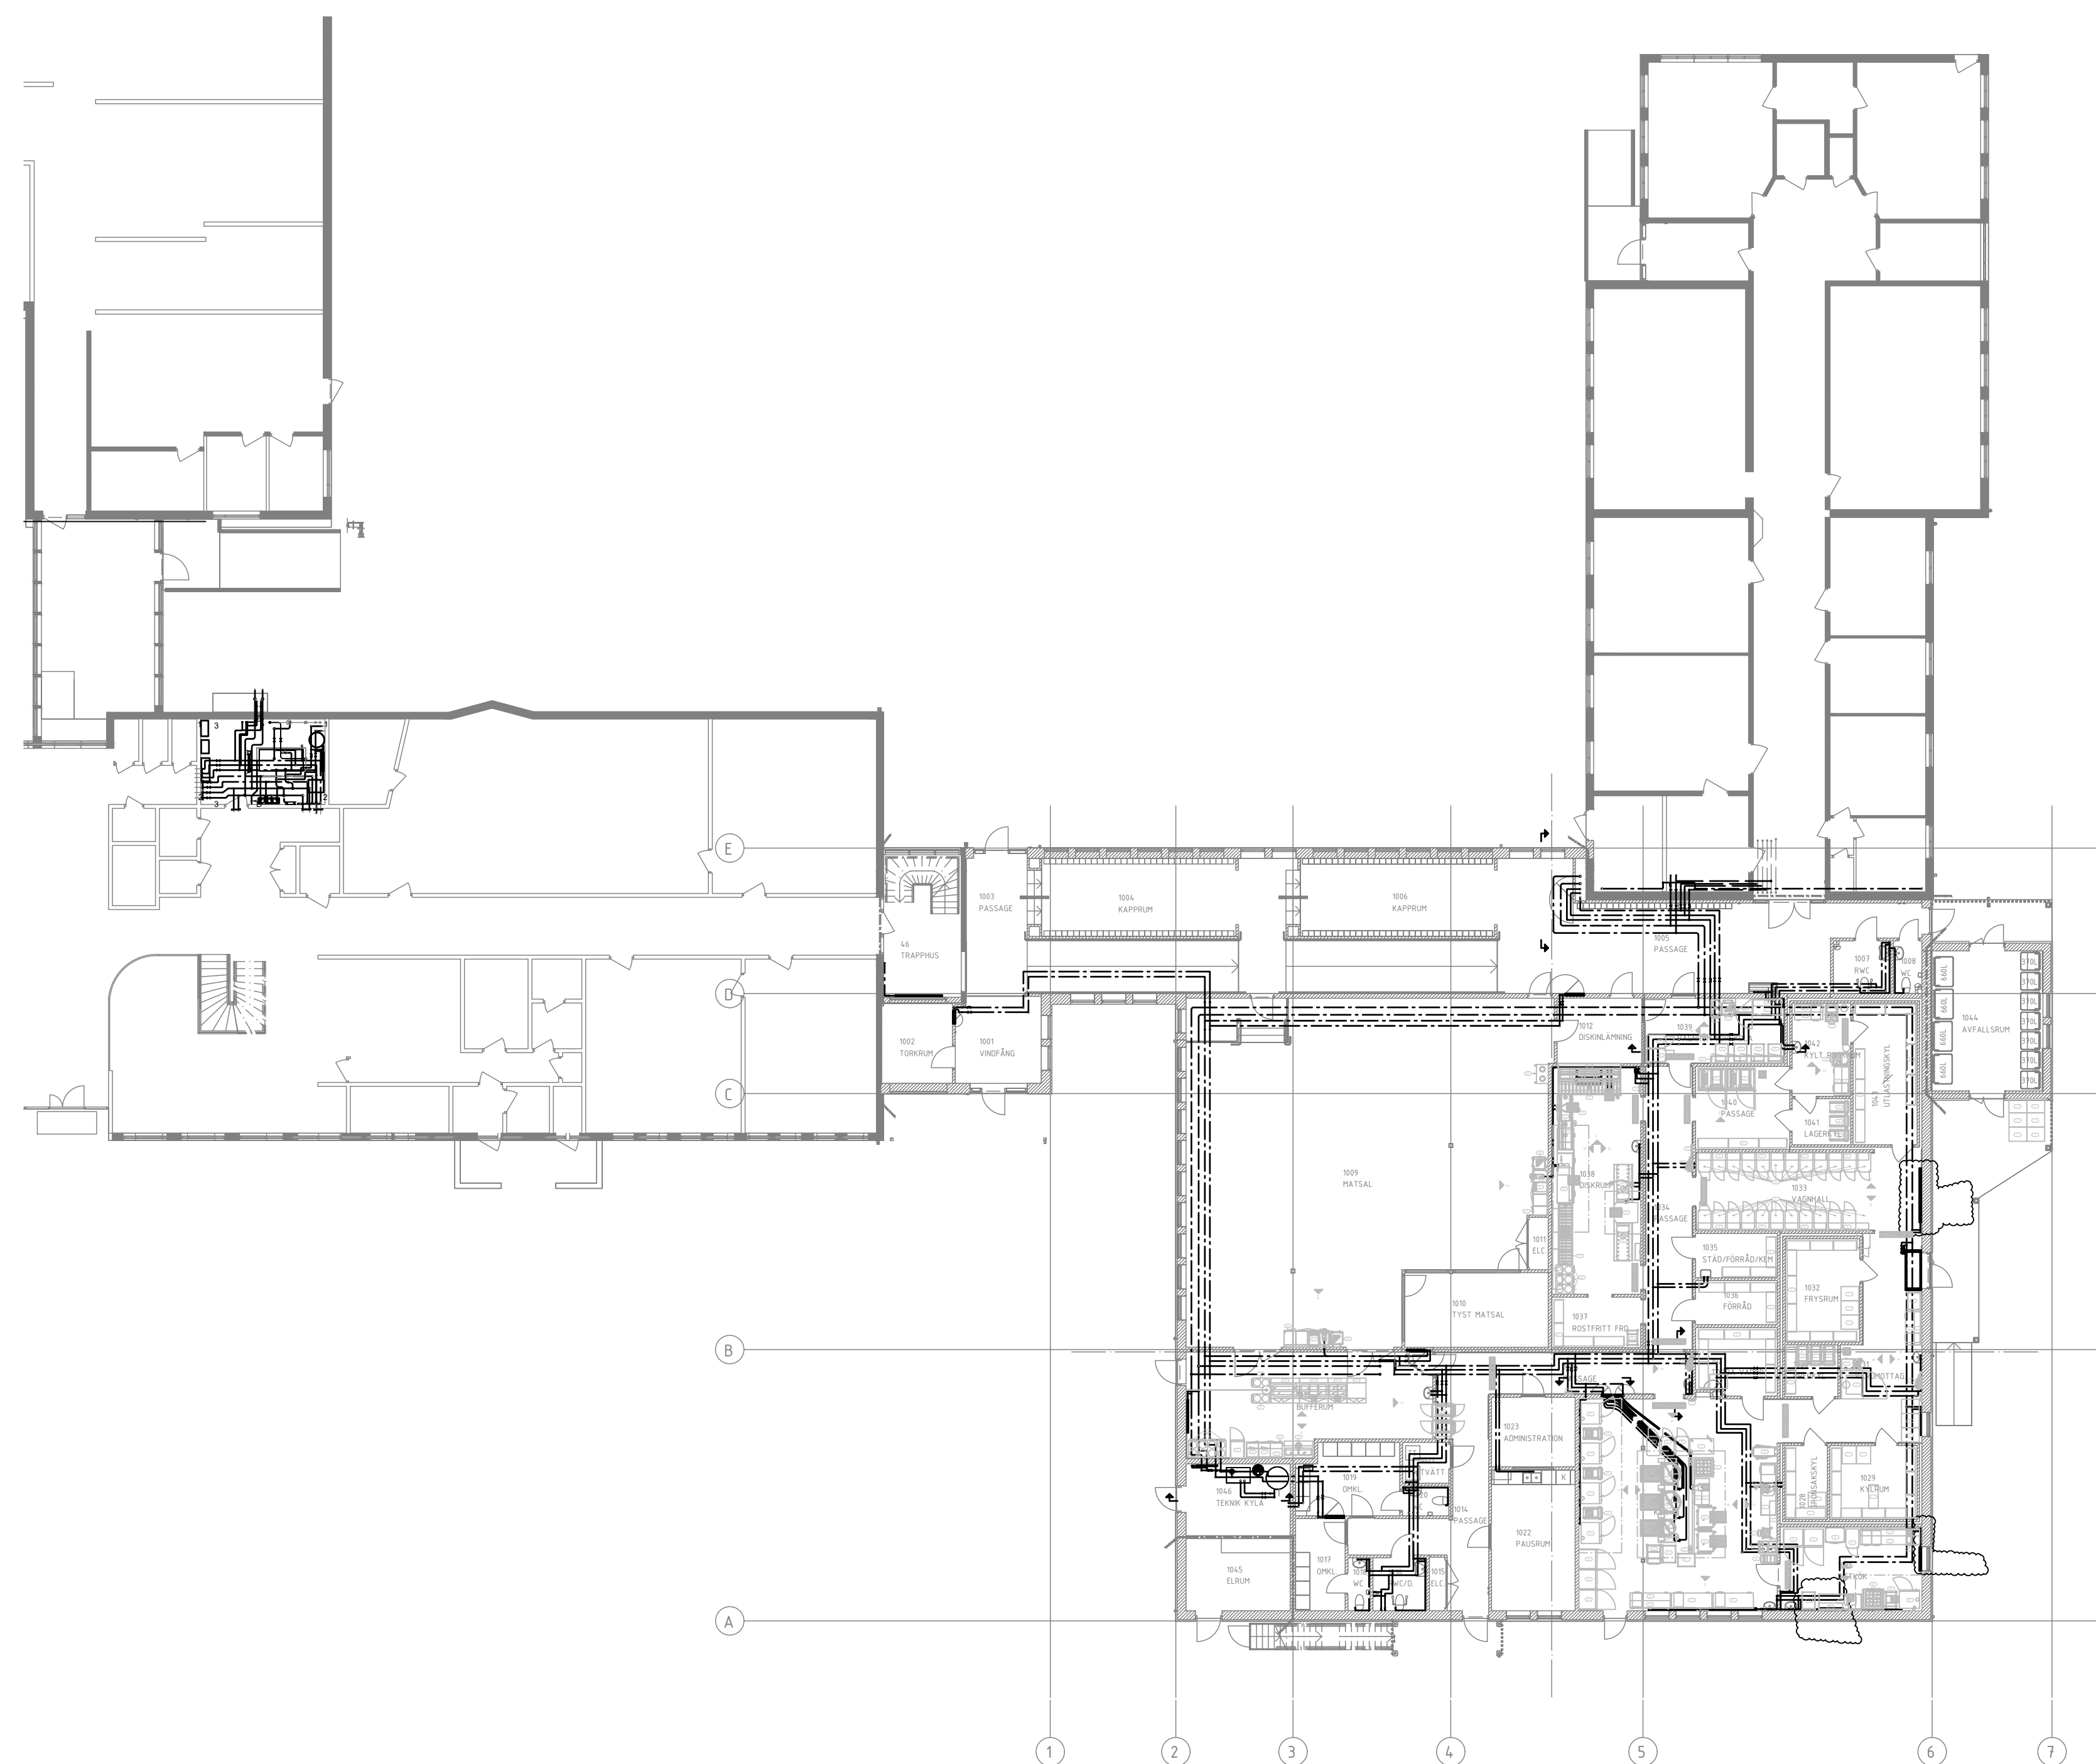

STATUS FÖRFRÅGNINGSUNDERLAG

HANDLING	BYGGHANDLING
----------	--------------

DATUM	GODKÄND AV	ÄNDRINGS I
2025-01-31	T.BERGSTRÖM	KFU0

2023-01-31	T. BERGSTRÖM	RI 00
BESTÄLLARE		



PROJEKTNAMN

CENTRALEKÖK

OMRÅDE

PROJEKTNUMMER	ADRESS
	YTTRE RINGVÄGEN 4

DIARIENUMMER	FASTIGHET FORDONET 1
--------------	-------------------------

DISCIPLIN	FÖRETAG
VS	NORCONSULT SVERIGE AB

V5	NORCONSULT SVERIGE AB
UPPDRAGSNUMMER	SKAPAD AV
108 83 71	MAN

108 85 71	MAN
TELEFON	KONTAKTPERSON
010 141 80 00	JONAS JOHANSSON

010 141 80 00	JONAS JOHANSSON
BYGGNADSVÄRK	PLUSHÖJD (RH 2000) +44.60. +45.07. +45.54 (FG)

		+44,60, +45,07, +45,54 (FG)
VÄNINGSPLAN	VÄNINGSDEL	DELOMRÅDE
1		DFI 3 4 5 6

1	DEL 3, 4, 5, 6
SYSTEM	
50 RÖRINSTALLATIONER	

50 RÖRINSTALLATIONER

PLAN 1 - OVERSIKT		
RITNINGSKATEGORI	SKALA	FORMAT
PLAN	1:200	A1

PLAN	1:200	A1
DOKUMENTNUMMER		ÄNDERUNG
V. 50. 1. 101		A

V-50-1-101	A
------------	---

SKALA 1:200

0 1 2 5 10 15 20

METER

11