

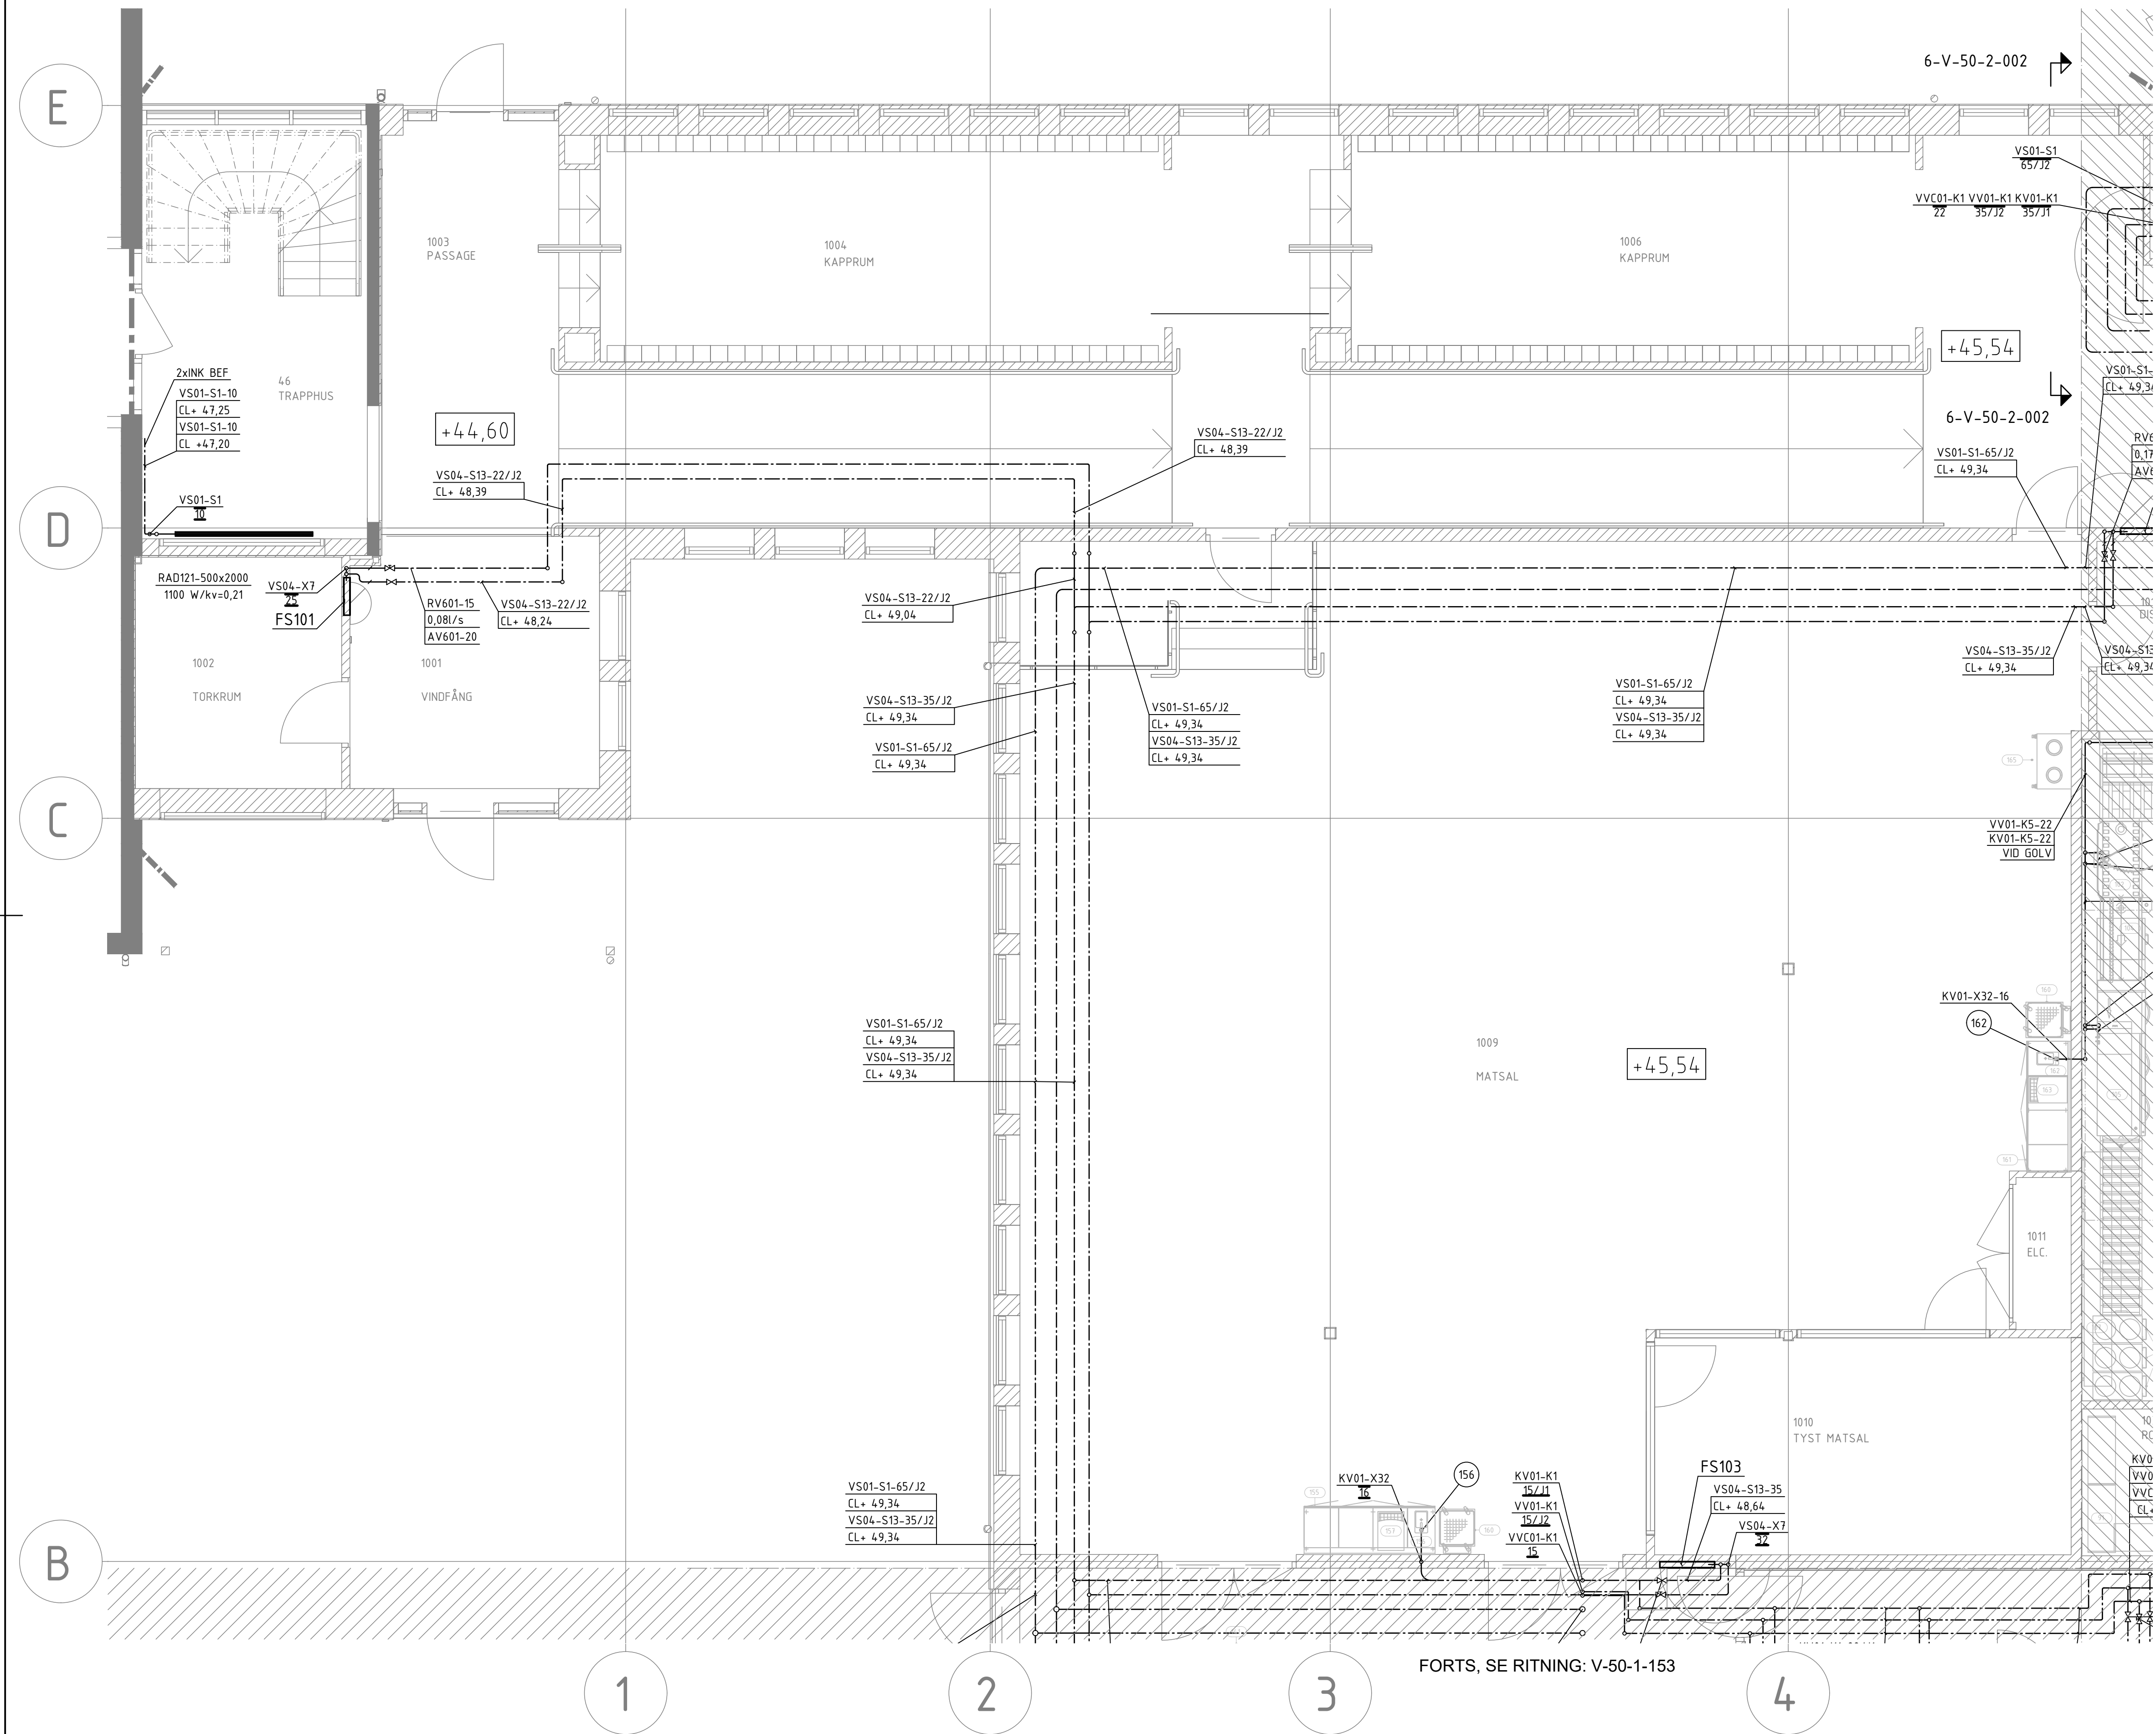


FÖRKLARINGSTEXT
SE RITNING V-50-0-001

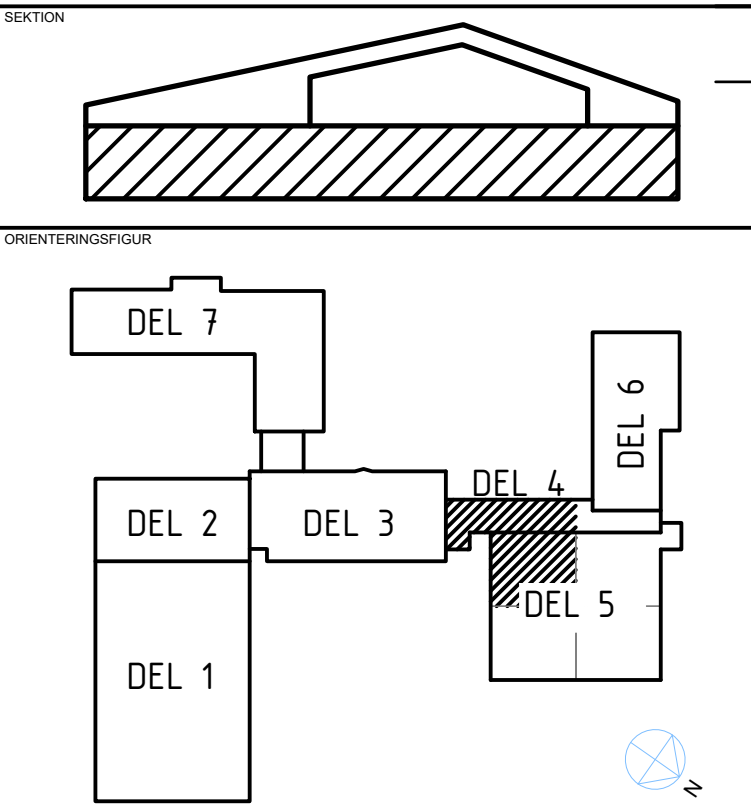

FORTS SE RITNING: V-50-1-152

FORTS, SE RITNING: V-50-1-153

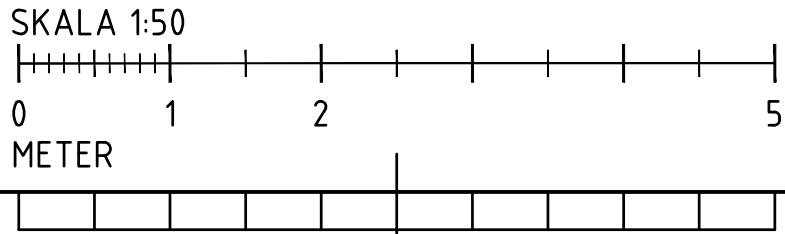

SEKTION		
ORIENTERINGSPÅR		
STATUS		
HÄNDLING		
DATUM	GODKÄND AV	ÄNDRINGS PM
2025-01-31	T.BERGSTRÖM	KFU01
BESTÄLLARE		
PROJEKTNAMN		
OMRÅDE		
PROJEKTNUMMER	FÖRRETT	
DARIENUMMER	FÖRORDNET 1	
DISCIPLIN	FÖRETAG	
OPPRÄGGSNUMMER	SKAPAD AV	
TELEFON	KONTAKTPERSON	
BYGGNADSVÄRDE	BYGGNADSVÄRDE (RM 2000)	
VÄNINGSPLAN	VÄNINGSDEL	DELOMRÅDE
1		DEL 4.1, 5.1
SYSTEM		
RÖRINSTALLATION		
PLAN 1 - DEL 4.1, 5.1		
RITNINGSKATEGORI	SKALA	FORMAT
PLAN	1:50	A1
DOKUMENTNUMMER	ÄNDRING	
V-50-1-151	A	

FILNAMN: