
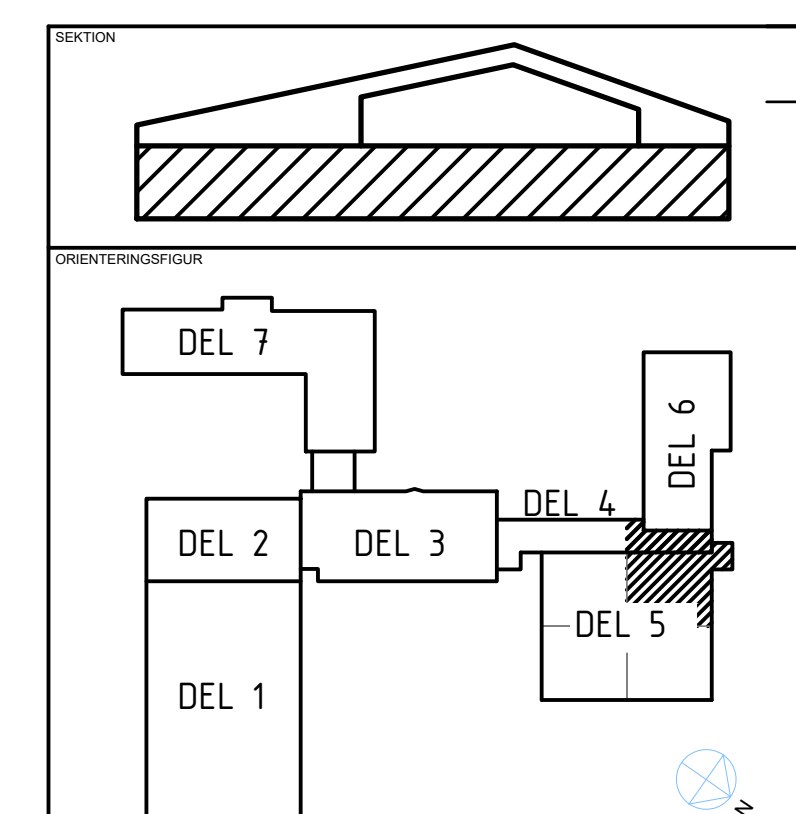


FÖRKLARINGSTEXT
SE RITNING V-50-0-001

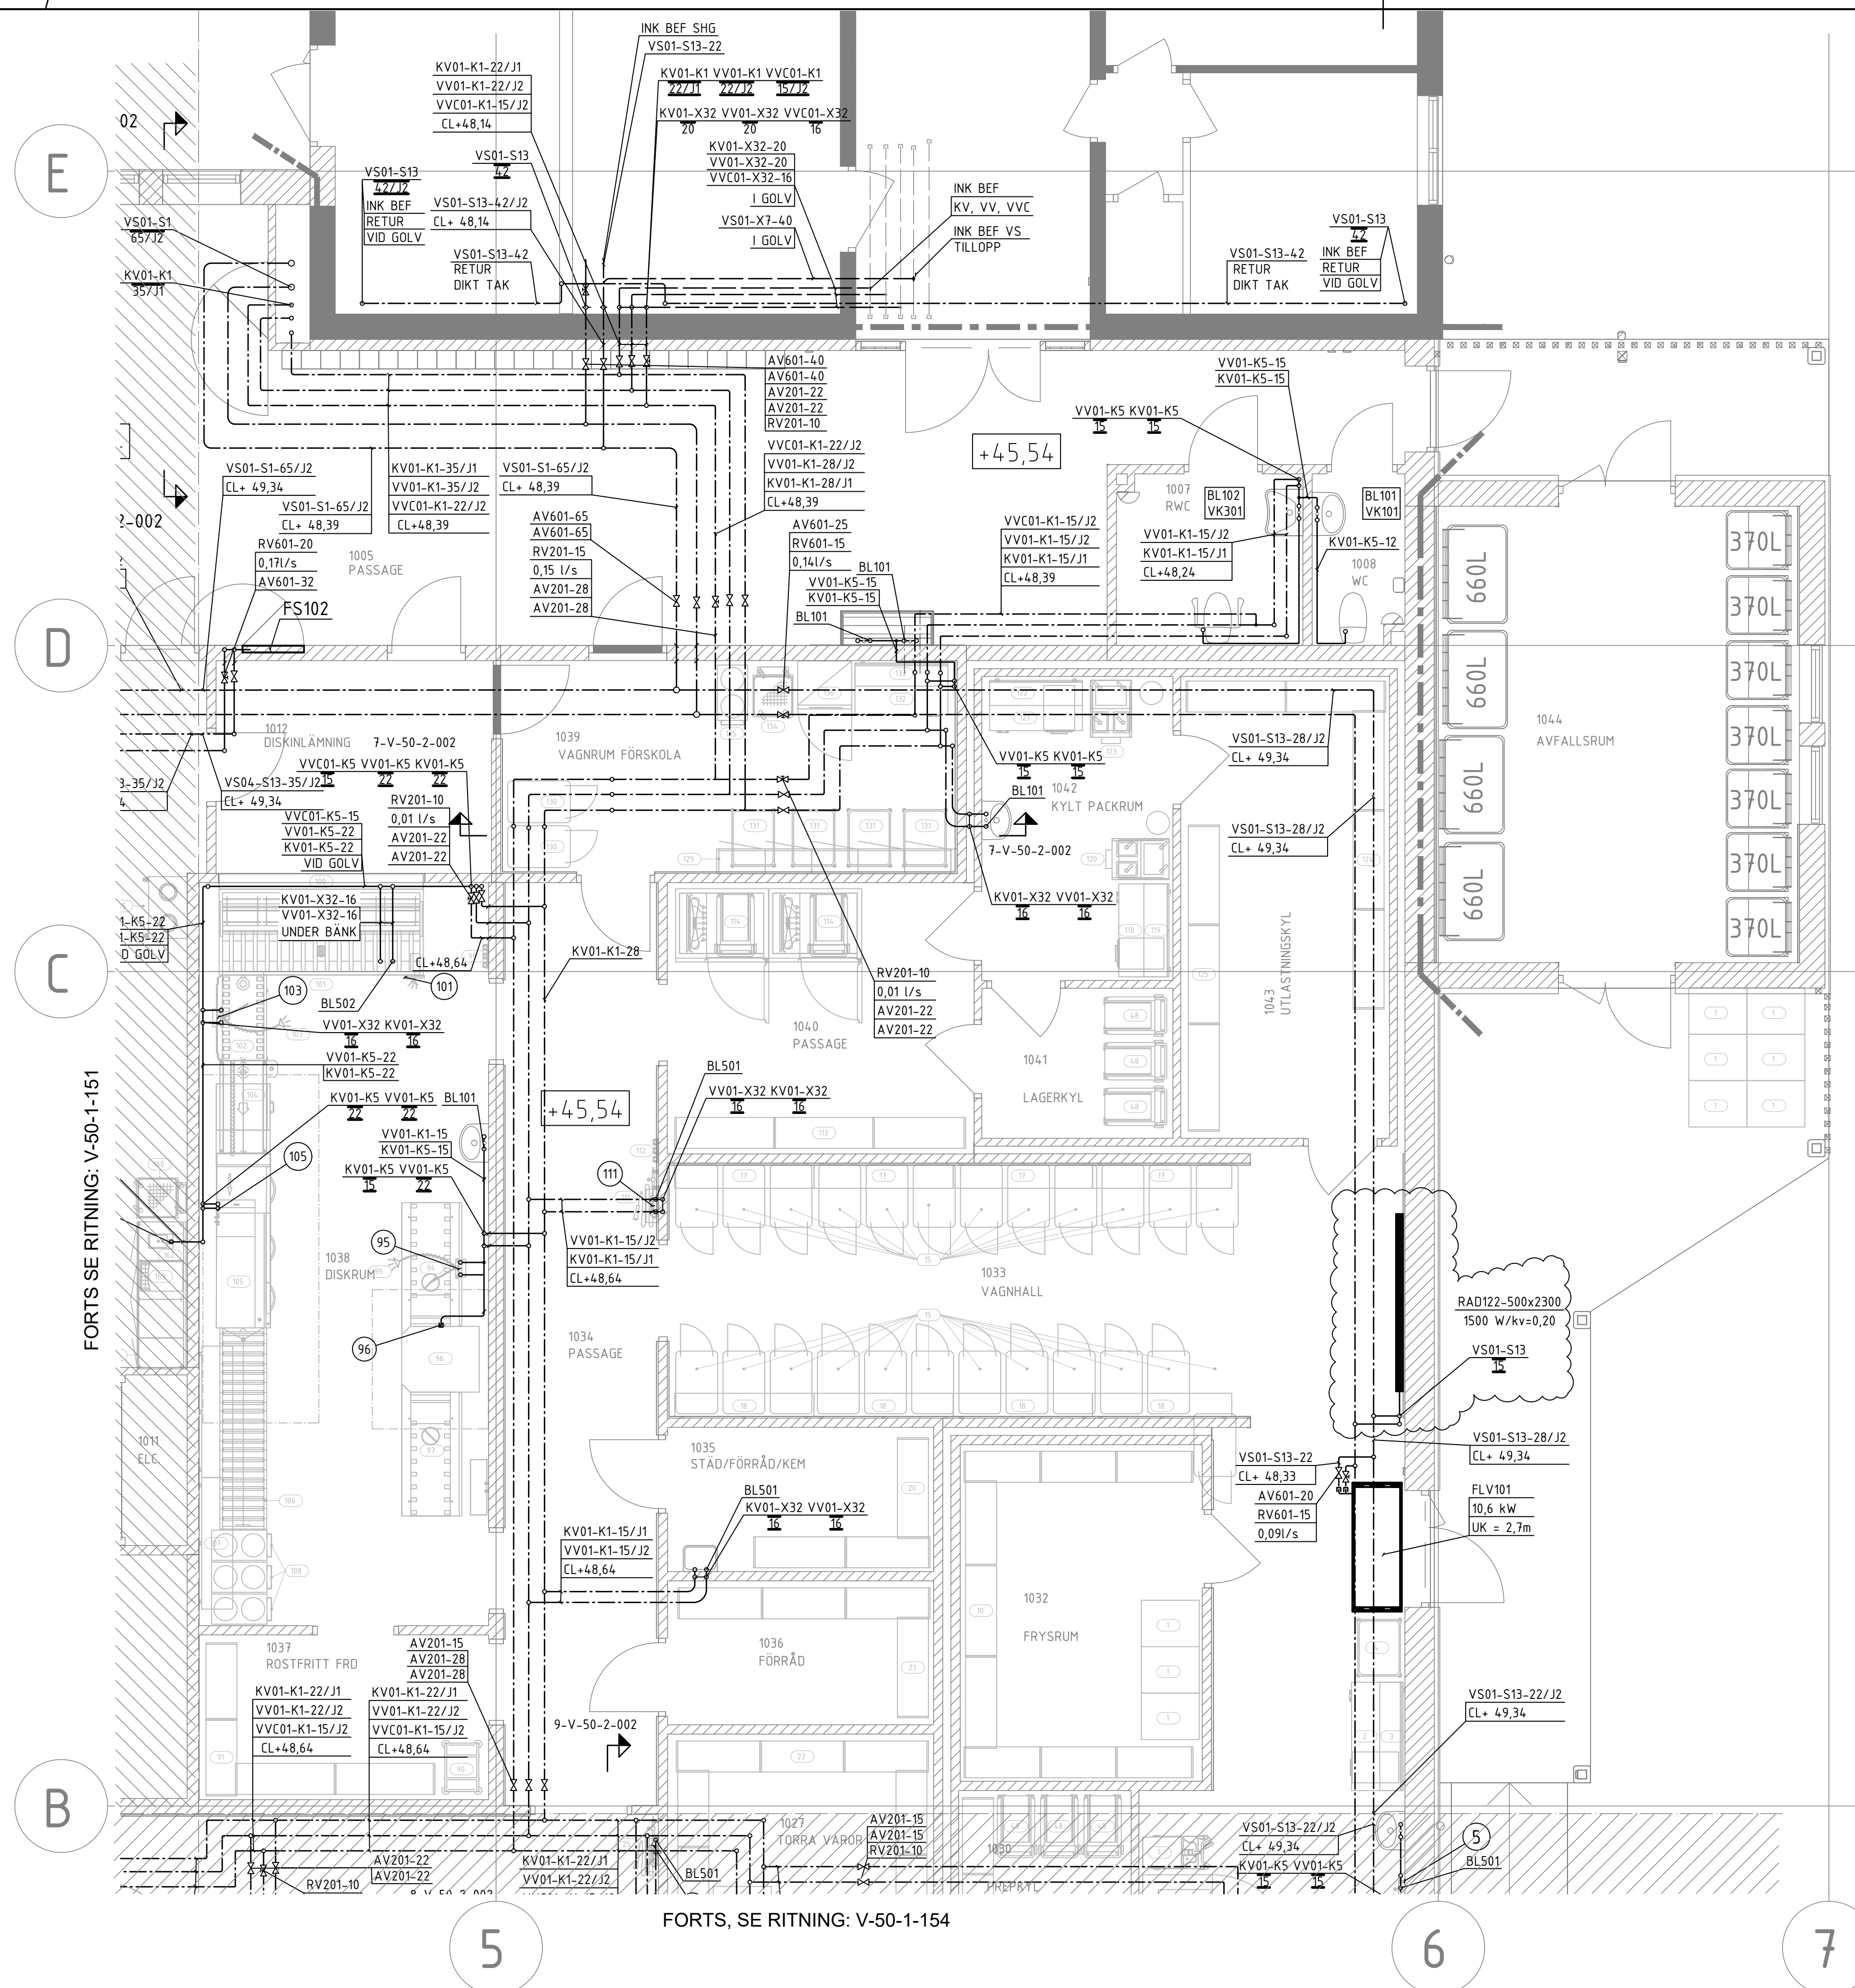

STATUS FÖRFRÅGNINGSUNDERLAG

HANDLING	BYGGHANDLING
----------	--------------

DATUM	GODKÄND AV	ANDRINGS PM
2025-01-31	T.BERGSTRÖM	KFU01

BESTÄLLARE	
------------	--



PROJEKTNAMN

CENTRAKKÖK

OMRADE ROBERTSFORS KOMMUN

PROJEKTNUMMER	ADRESS
	YTTRE RINGVÄGEN 4

DIARIENUMMER	FASTIGHET FORDONET 1
--------------	-------------------------

DISCIPLIN	FÖRETAG
VS	NORCONSULT SVERIGE AB

UPPDRAGSNUMMER	SKAPAD AV
108 83 71	MAN
TELEFON	KONTAKTPERSON

TELEFON	KONTAKTPERSON
010 141 80 00	JONAS JOHANSSON
RYGGMÄSSIGHET	GL. LISMÅ ID. (RM 2000)

BYGGNADSVÄRDE		PLUSHÖJD (RH 2000)
		+45,54 (FG)
VÄNINGSPLAN	VÄNINGSDEJ	DELOMRÅDE

VÄNINGSPLAN	VÄNINGSDEL	DELOMRÅDE
1		DEL 4.2, 5.2
SYSTEM		

50 RÖRINSTALLATIONER

SPECIFICATION		
PLAN 1 - DEL 4.2, 5.2		
RITNINGSKATEGORI	SKALA	FORMAT

ÄNDRINGSKATEGORI	SKALA	FORMAT
PLAN	1:50	A1
DOKUMENTNUMMER	ÄNDRING	

V-50-1-152	A
------------	---

SKALA 1:50

0 1 2 5
METER

THE ALABAMA	THE ALABAMA
-----------------------------	-----------------------------