


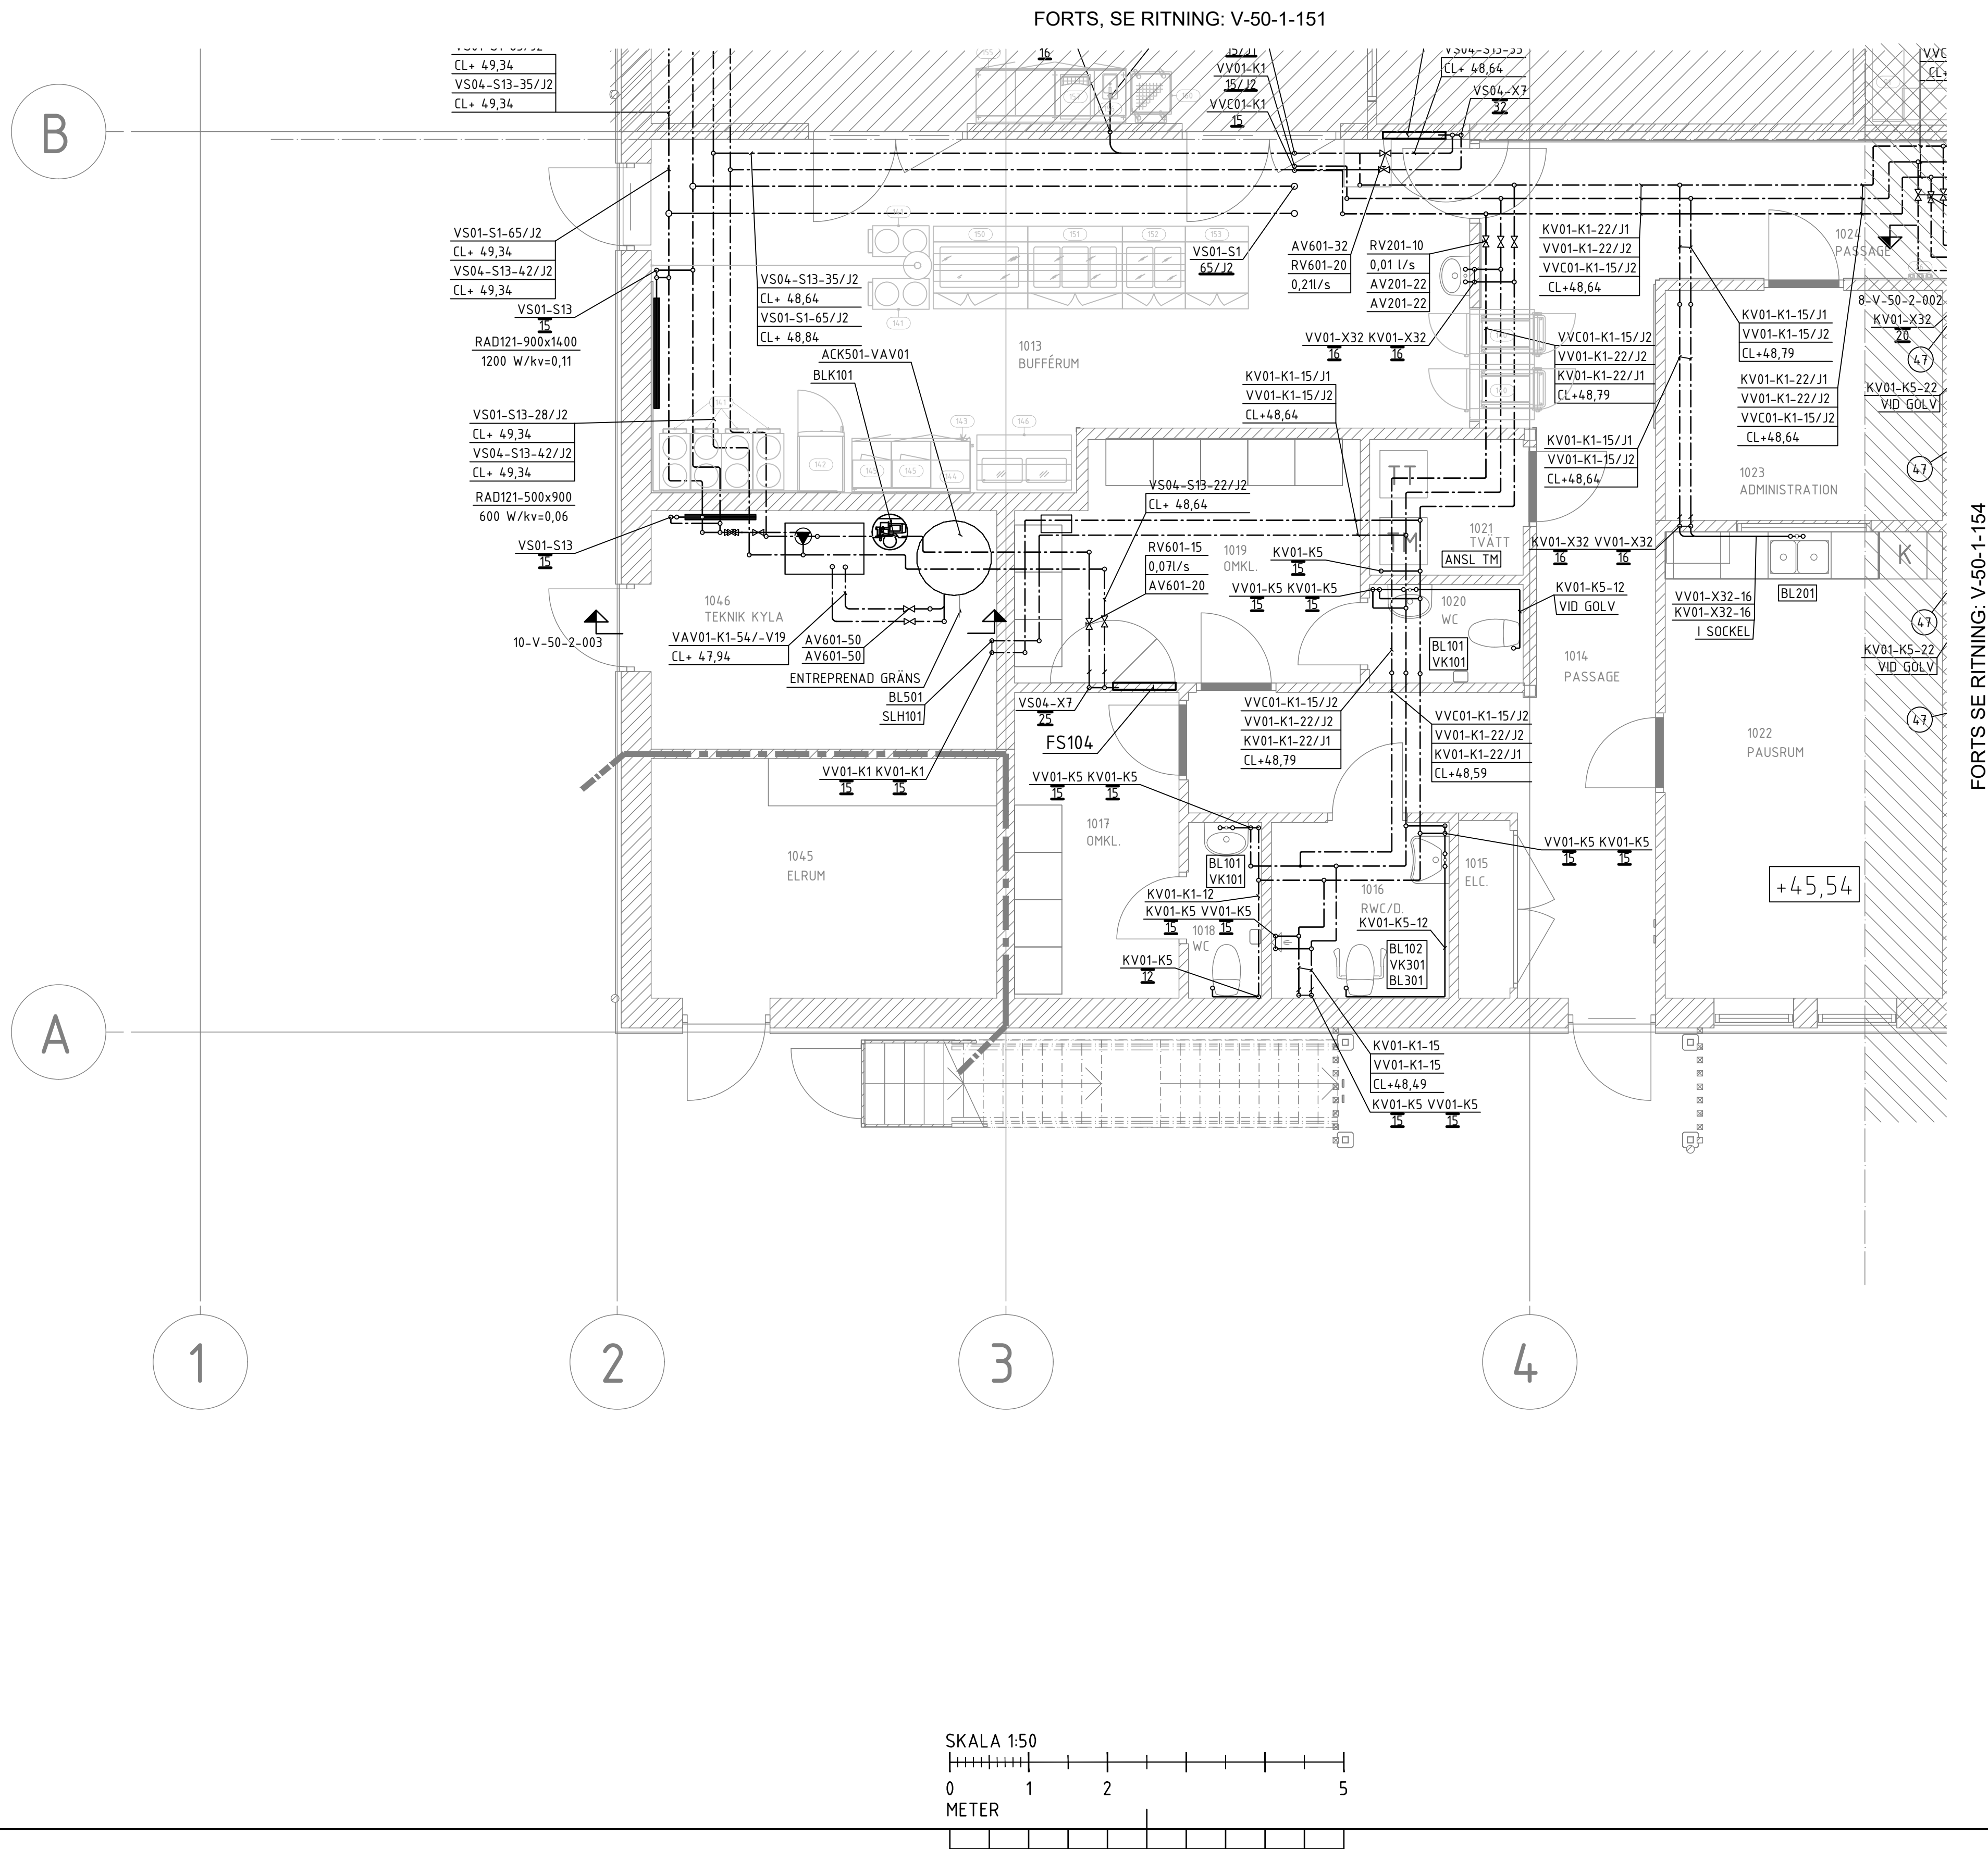

FORTS SE RITNING: V-50-1-154

SEKTION

ORIENTERINGSPÅR

STATUS

FÖRFRÅGNINGSUNDERLAG

HANDLING

BYGGHANDLING

DATUM

2025-01-31

GODKÄND AV

T.BERGSTRÖM

ANDRINGS PM

KFU01

BESTÄLLARE

ROBERTSFORS KOMMUN

PROJEKTNAMN

CENTRALKÖK

OMRADE

ROBERTSFORS KOMMUN

PROJEKTNUMMER

YTTRE RINGVÄGEN 4

DARIENUMMER

FORDONET 1

DISCIPLIN

NORCONSULT SVERIGE AB

OPPRÄGGSNUMMER

MAN

TELEFON

010 141 80 00

JONAS JOHANSSON

BYGGNADSVÄRDE

+45,54 (FG)

VÄNINGSPLAN

1

VÄNINGSDEL

DEL 5.3

SYSTEM

50 RÖRINSTALLATIONER

PRESENTATION

PLAN 1 - DEL 5.3

RITNINGSKATEGORI

PLAN

SKALA

1:50

FORMAT

A1

ANDRNING

A

DOKUMENTNUMMER

V-50-1-153