
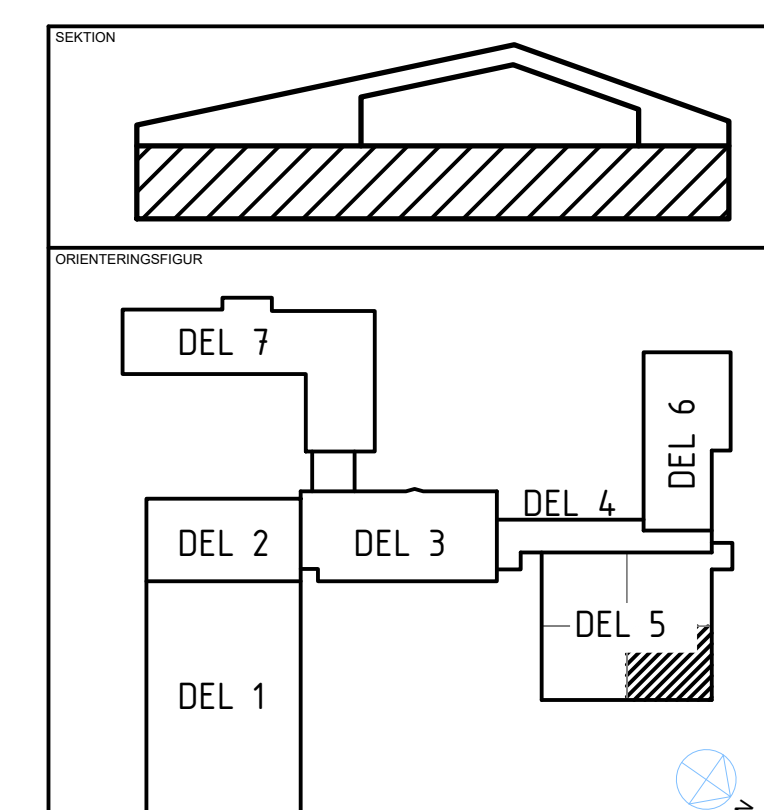


FORTS. SE RITNING: V-50-1-152

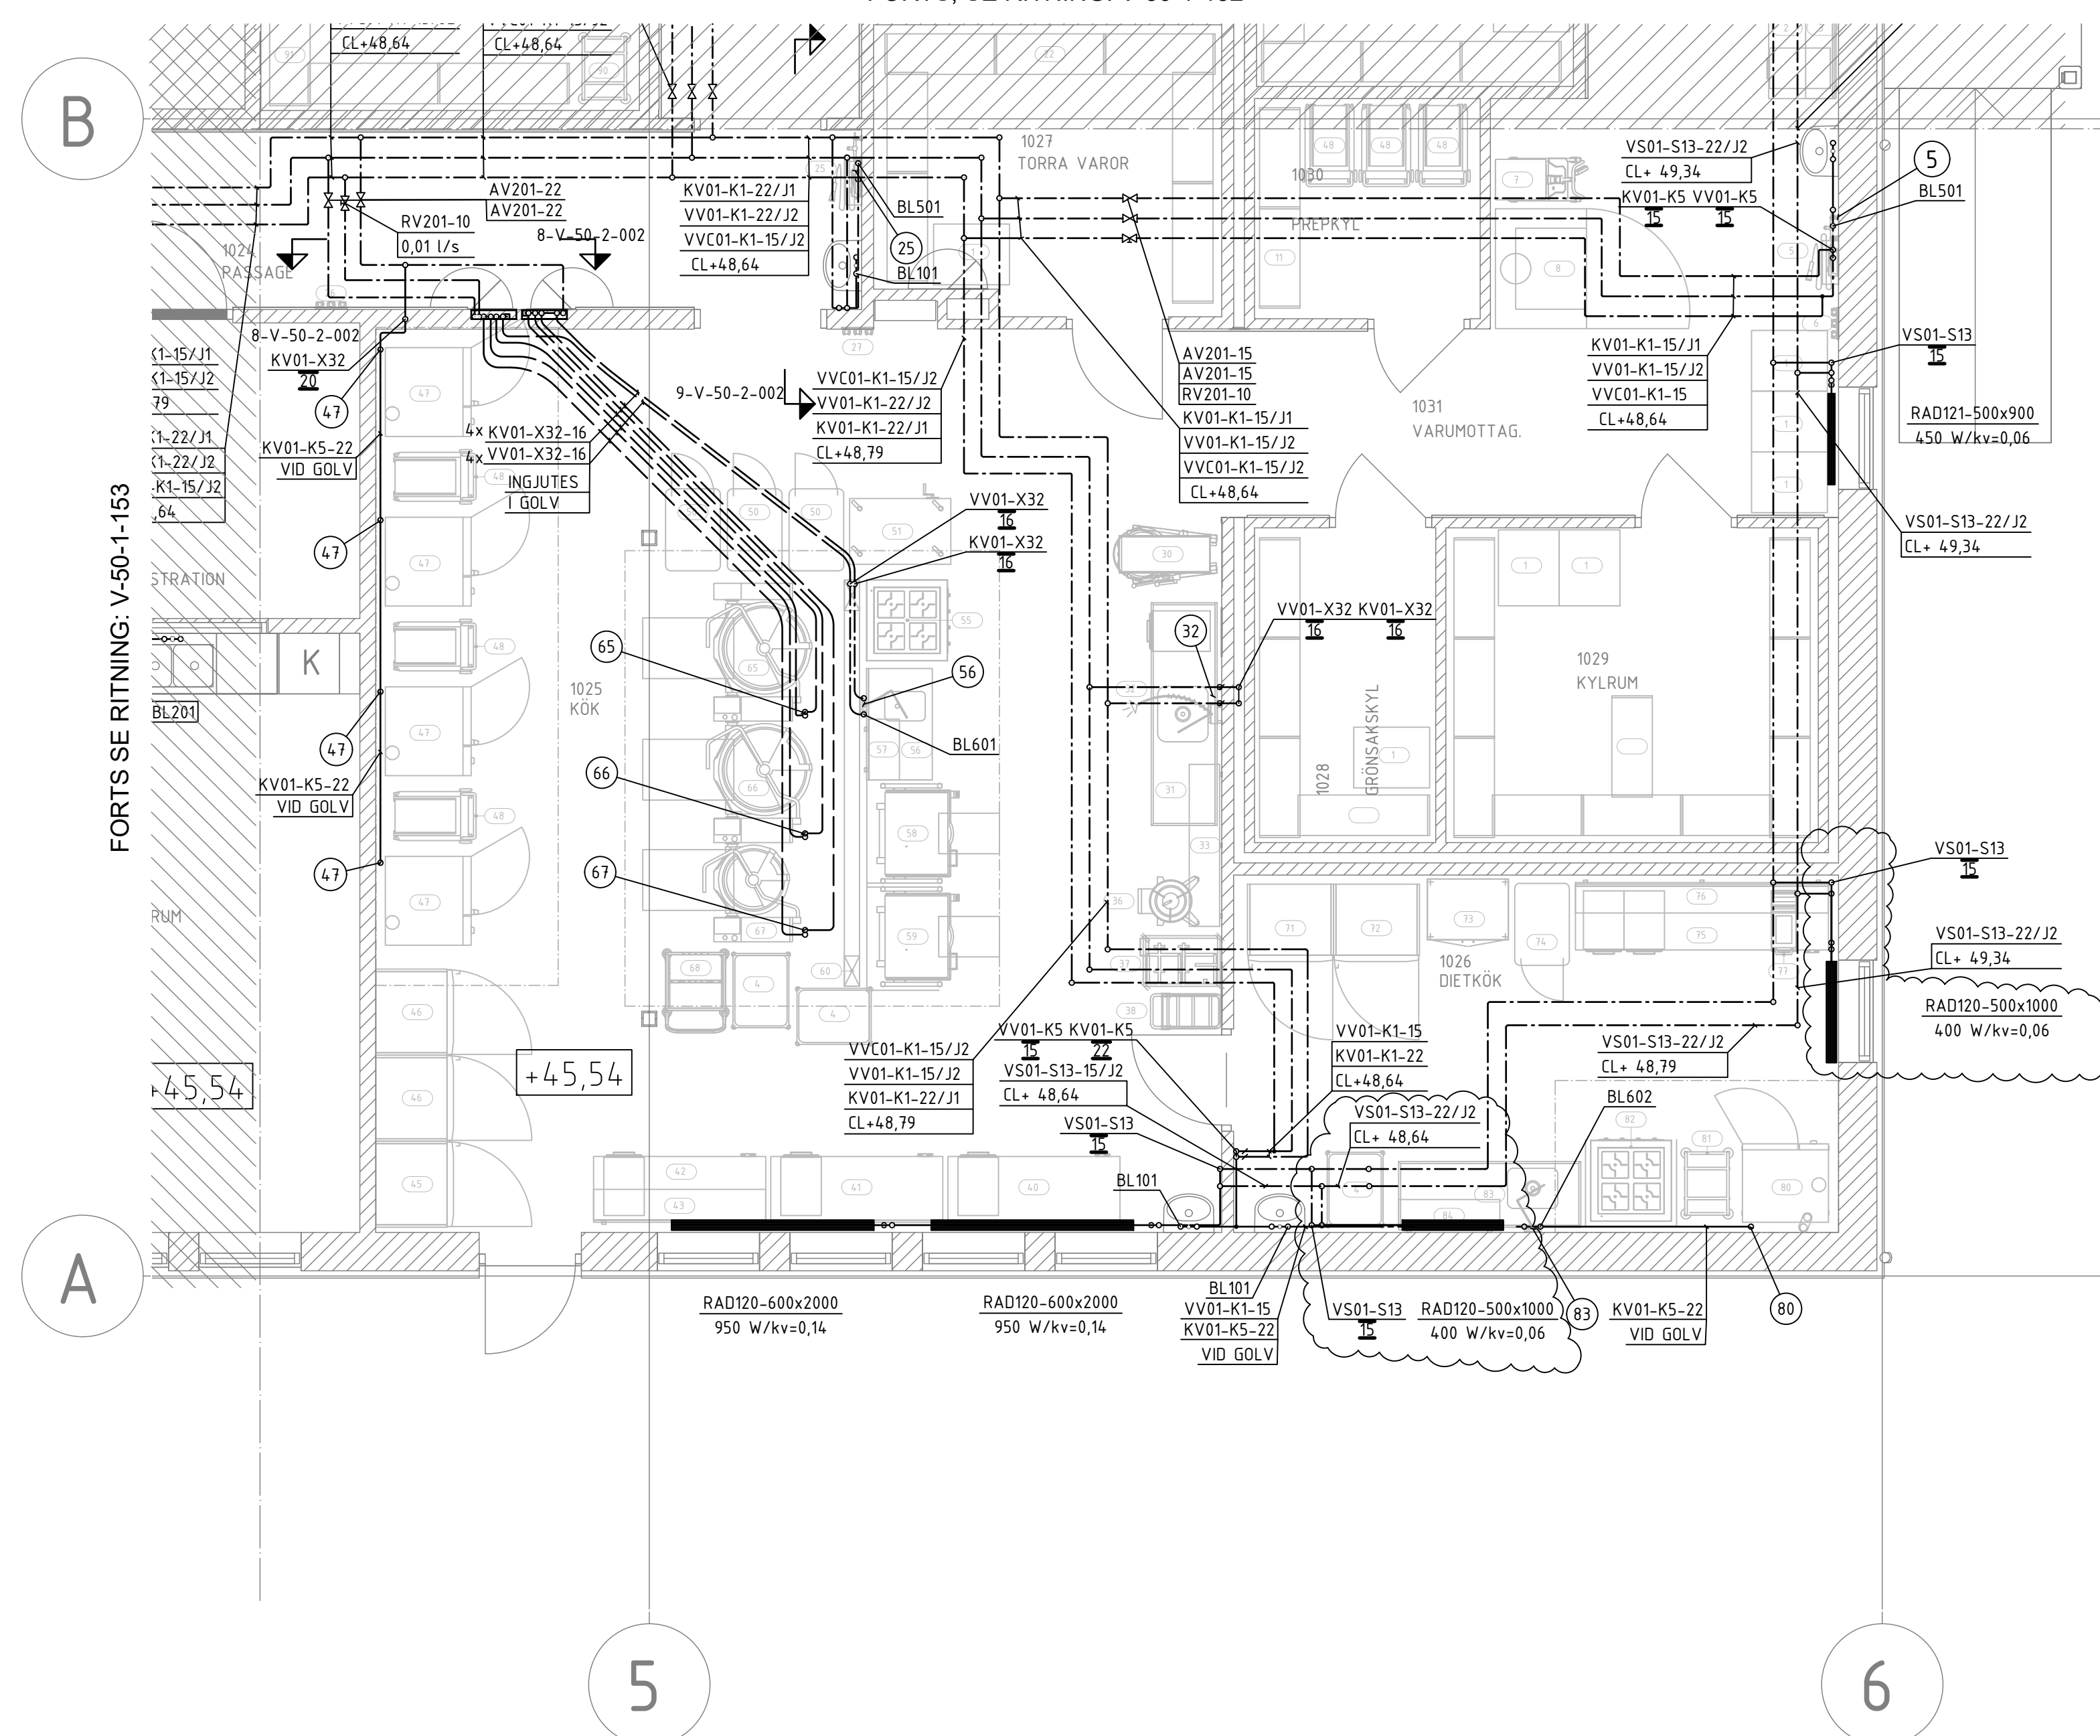

STATUS FÖRFRÅGNINGSUNDERLAG

HANDLING	BYGGHANDLING
----------	--------------

DATUM	GODKÄND AV	ÄNDRINGS
2025-01-31	T.BERGSTRÖM	KFU0

2023-01-31	T. BERGSTRÖM	RI 00
BESTÄLLARE		



PROJEKTNAMN

CENTRAALKÖK

OMRADE

ROBERTSFORS KOMMUN

PROJEKTNUMMER	ADRESS
	YTTRE RINGVÄGEN 4

DIARIENUMMER	TITRE RINGVALEN 4 FASTIGHET FORDONET 1
--------------	--

DISCIPLIN	FÖRETAG
VS	NORCONSULT SVERIGE AB

VS	NORCONSULT SVERIGE AB
UPPDRAGSNUMMER	SKAPAD AV
108 83 71	MAN

108 83 71	MAN
TELEFON	KONTAKTPERSON
010 141 80 00	IONAS JOHANSSON

010 141 80 00	JUNAS JOHANSSON
BYGGNADSVÄRK	PLUSHÖJD (RH 2000) +45 54 (EG)

		+45,54 (FG)
VÄNINGSPLAN	VÄNINGSDEL	DELOMRÅDE
1		DEL 5 /

1	DEL 5.4
SYSTEM FÖR INSTALLATIONEN	

50 RORINSTALLATIONER

PLAN 1 - DEL 5.4		
RITNINGSKATEGORI	SKALA	FORMAT
PLAN	1:500	A3

PLAN	1:50	A1
DOKUMENTNUMMER		ÄNDERUNG

V-50-1-154	A
------------	---

SKALA 1:50



0 1 2 3 4 5

METER

THE NAME	
----------	--