


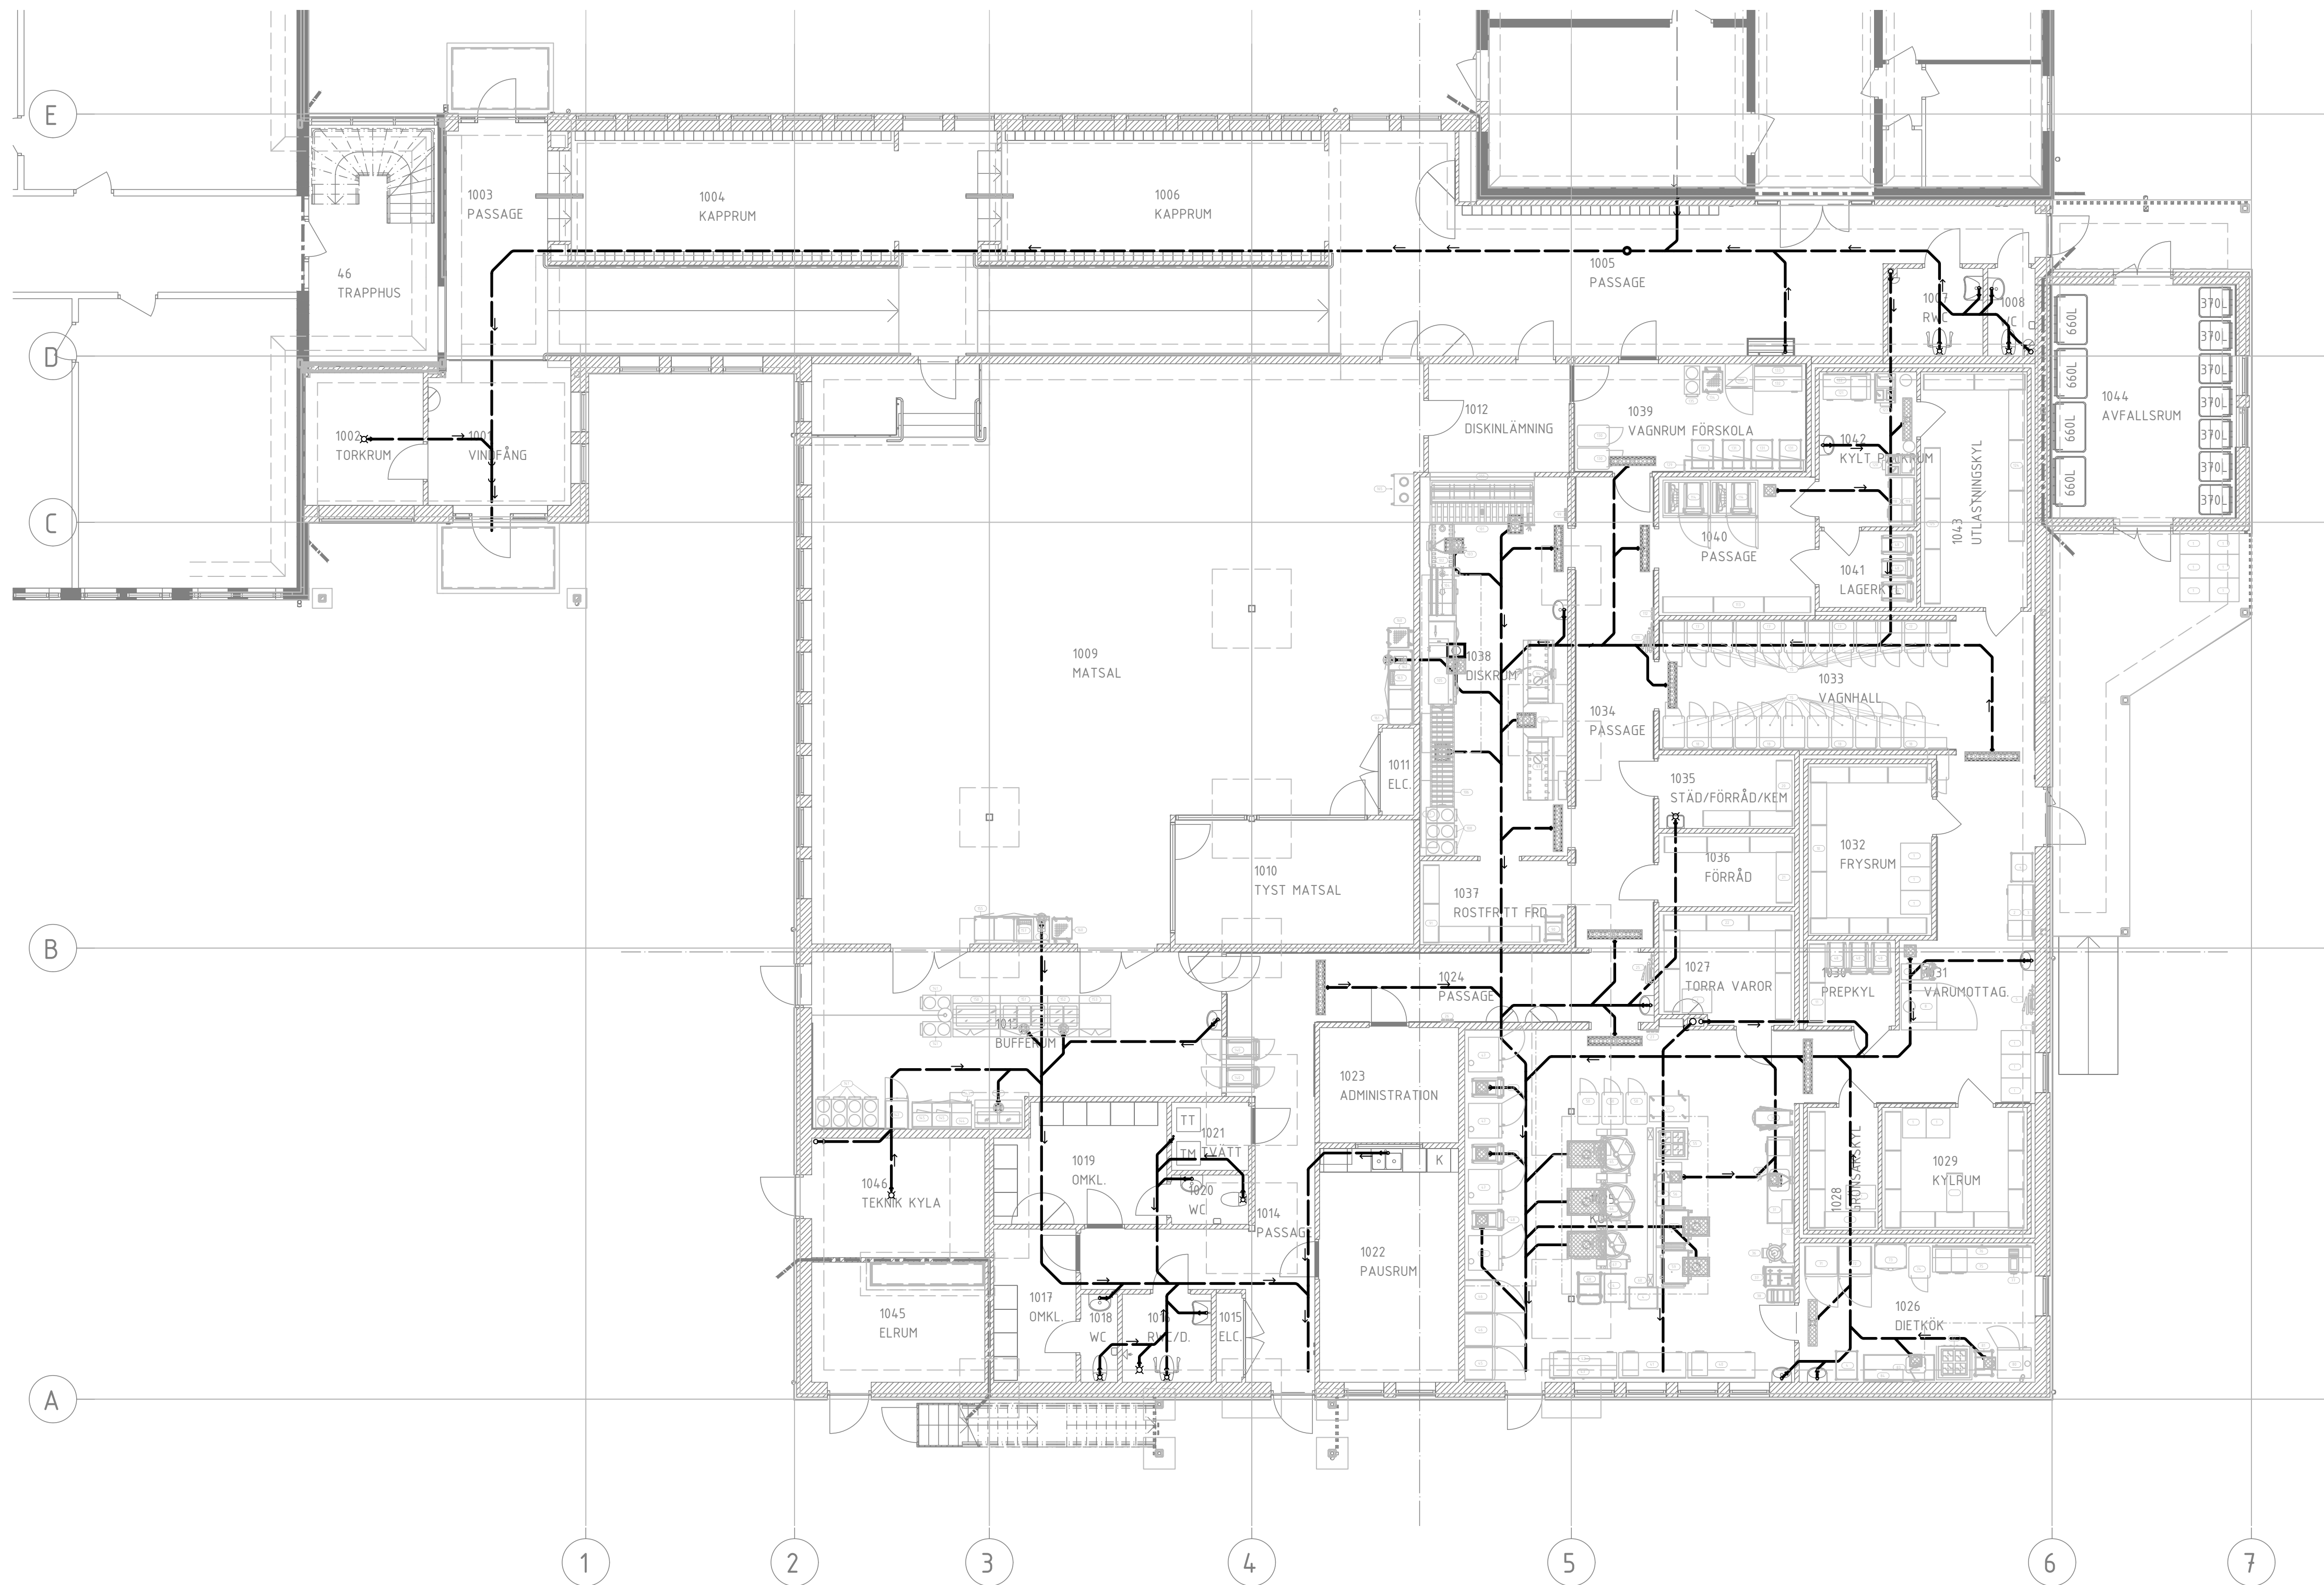

SEKTION

ORIENTERINGSDIAGRAM

STATUS

FÖRFRÅGNINGSUNDERLAG

HANDLING

BYGGHANDLING

DATUM

2025-01-31

ODOKAND AV

T.BERGSTRÖM

ANDRINGS PM

KFU01

BESTÄLLARE

ROBERTSFORS KOMMUN

PROJEKTNAMN

CENTRALKÖK

OMRADE

ROBERTSFORS KOMMUN

PROJEKTNUMMER

YTTRE RINGVÄGEN 4

DARIENUMMER

FÖRORDNET 1

DISCIPLIN

NORCONSULT SVERIGE AB

OPPFÖRINGSNUMMER

MAN

TELEFON

010 141 80 00

JONAS JOHANSSON

BYGGNADSVÄRDE

+44,60, +45,07, +45,54 (FG)

VÄNINGSPLAN

1

VÄNINGSDEL

DEL 4, 5

SYSTEM

53 SPILLVATTENINSTALLATIONER

BESEKATION

PLAN 0 - ÖVERSIKT, UNDER PLATTA

RITNINGSKATEGORI

PLAN

SKALA

1:100

FORMAT

A1

ANDRING

A

DOKUMENTNUMMER

V-53-1-001

