



FÖRKLARINGSTEXT
SE RITNING V-50-0-001

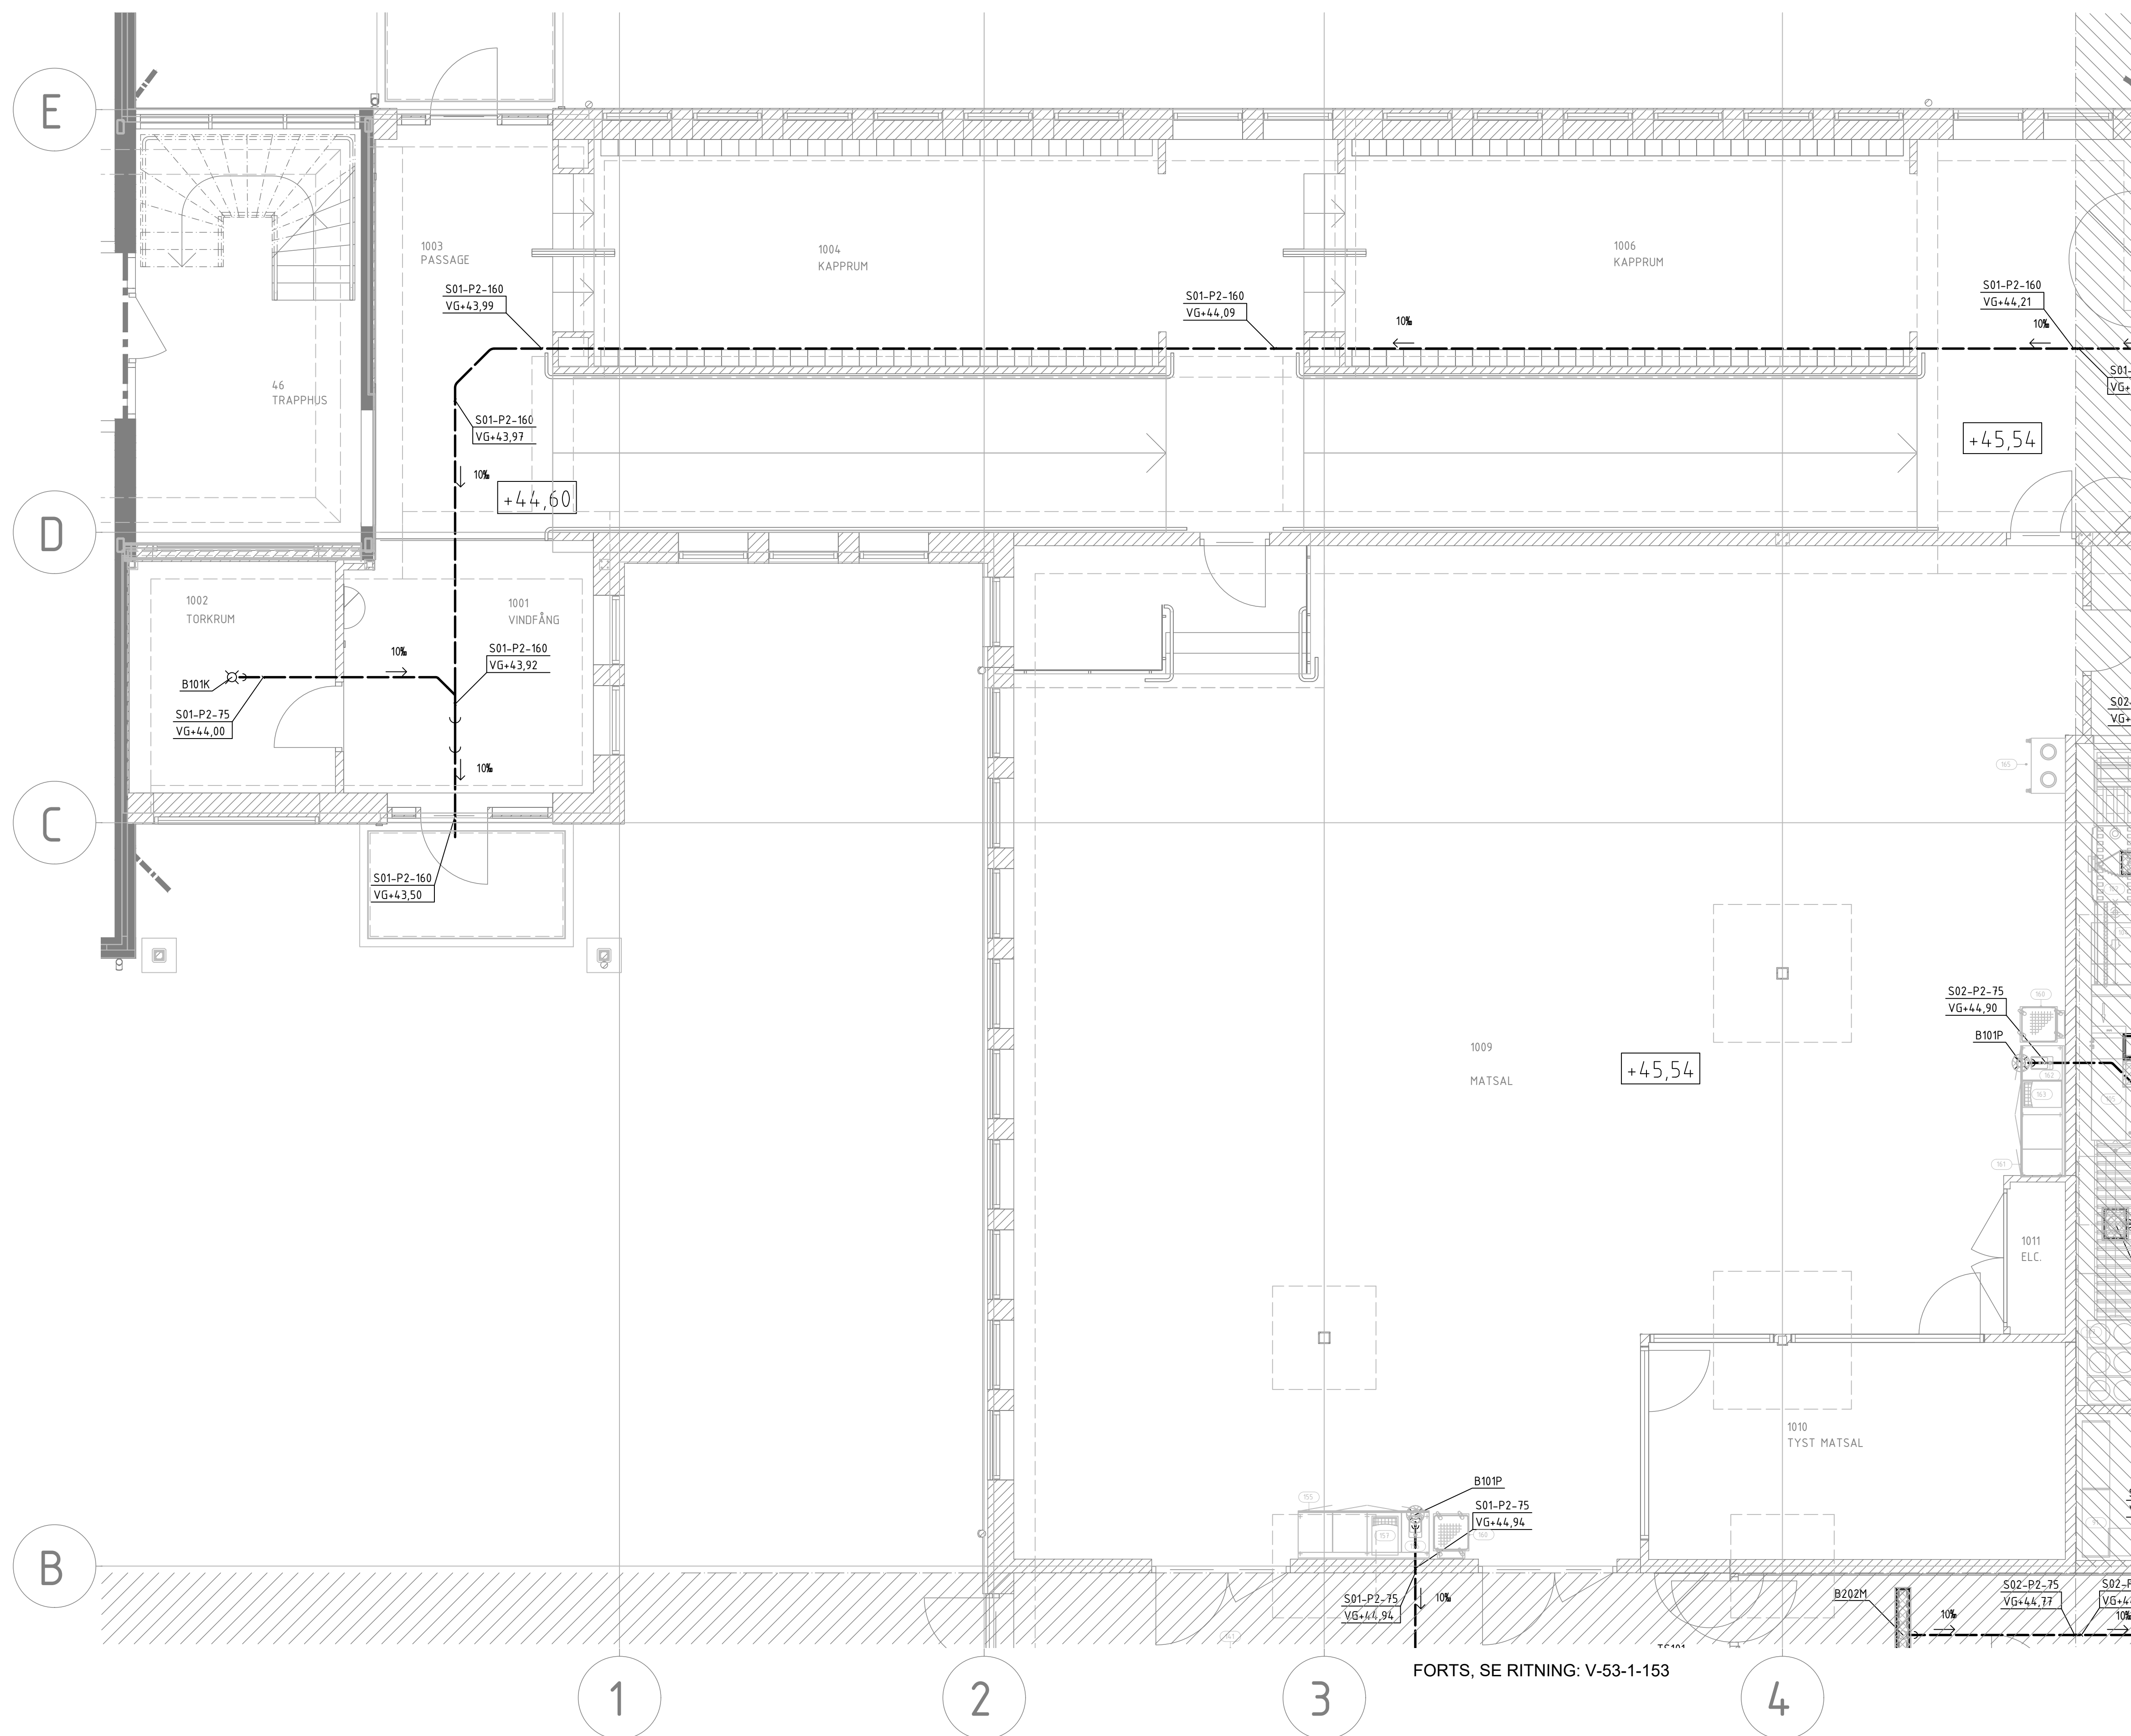

FORTS SE RITNING: V-53-1-152

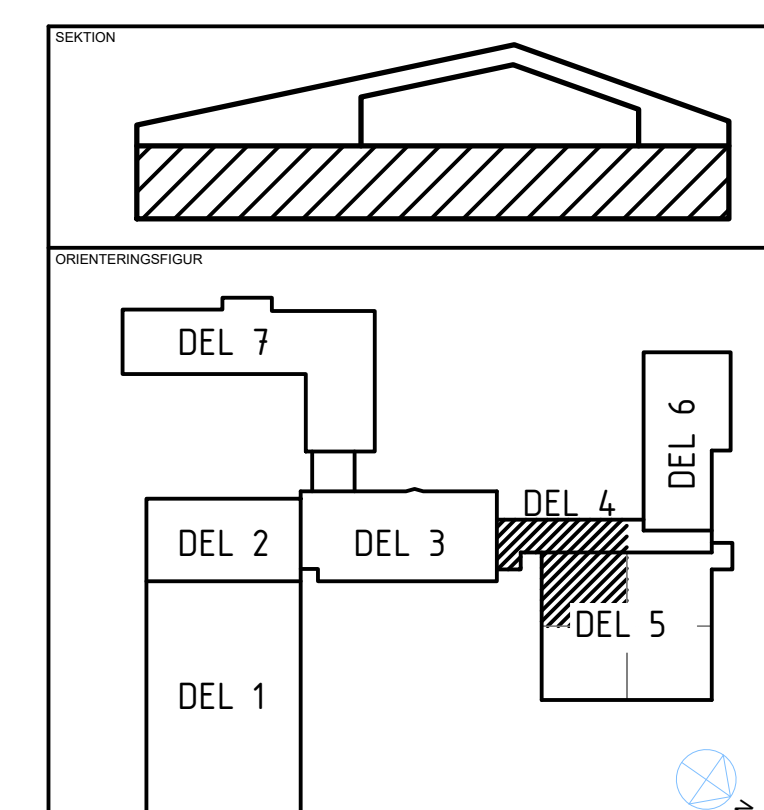

STATUS FÖRFRÅGNINGSUNDERLAG

HANDLING	BYGGHANDLING
----------	--------------

DATUM	GÖDKAND AV	ÄNDRINGS PM
2025-01-31	T.BERGSTRÖM	KFU01

2023-01-31	T. BERGSTRÖM	RI 501
BESTÄLLARE		



PROJEKTNAMN CENTRALEKÖK

OMRADE ROBERTSFORS KOMMUN

PROJEKTNUMMER	ADRESS
	YTTRE RINGVÄGEN 4

DIARIENUMMER	FASTIGHET FORDONET 1
--------------	-------------------------

DISCIPLIN	FÖRETAG
VS	NORCONSULT SVERIGE AB

UPPDAGSNUMMER	SKAPAD AV
108 83 71	MAN

TELEFON	KONTAKTPERSON
010 141 80 00	JONAS JOHANSSON

BYGGNADSVÄRK	PLUSHÖJD (RH 2000) +45 54 (EG)
--------------	-----------------------------------

		445,54 (FÖ)
VÄNINGSPLAN	VÄNINGSDEL	DELOMRÅDE
1		DEL 4.1 5.1

1	DEL 4.1, 5.1
SYSTEM	53 SPI VATTENINSTALLATIONER

SPECIFIKATION

RITNINGSKATEGORI	SKALA	FORMAT
PLAN	1:50	A1

PLAN	1:50	A1
DOKUMENTNUMMER		ANDR.
V. E3. 1. 051		A

V-53-1-051	A
------------	---

FILE NAME:	
------------	--

SKALA 1:50

0 1 2
METER