
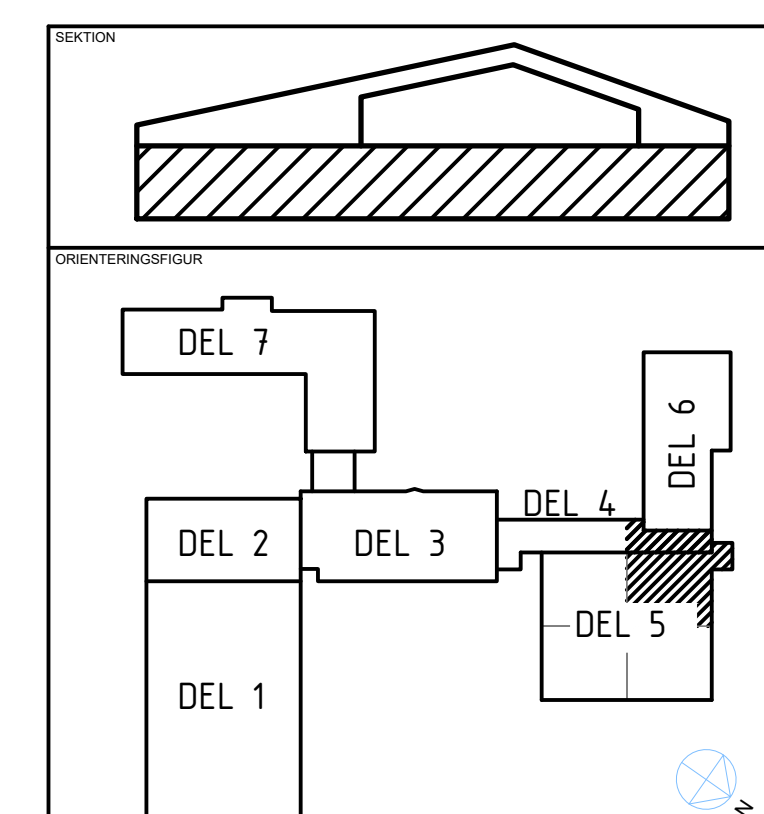


FÖRKLARINGSTEXT  
SE RITNING V-50-0-001

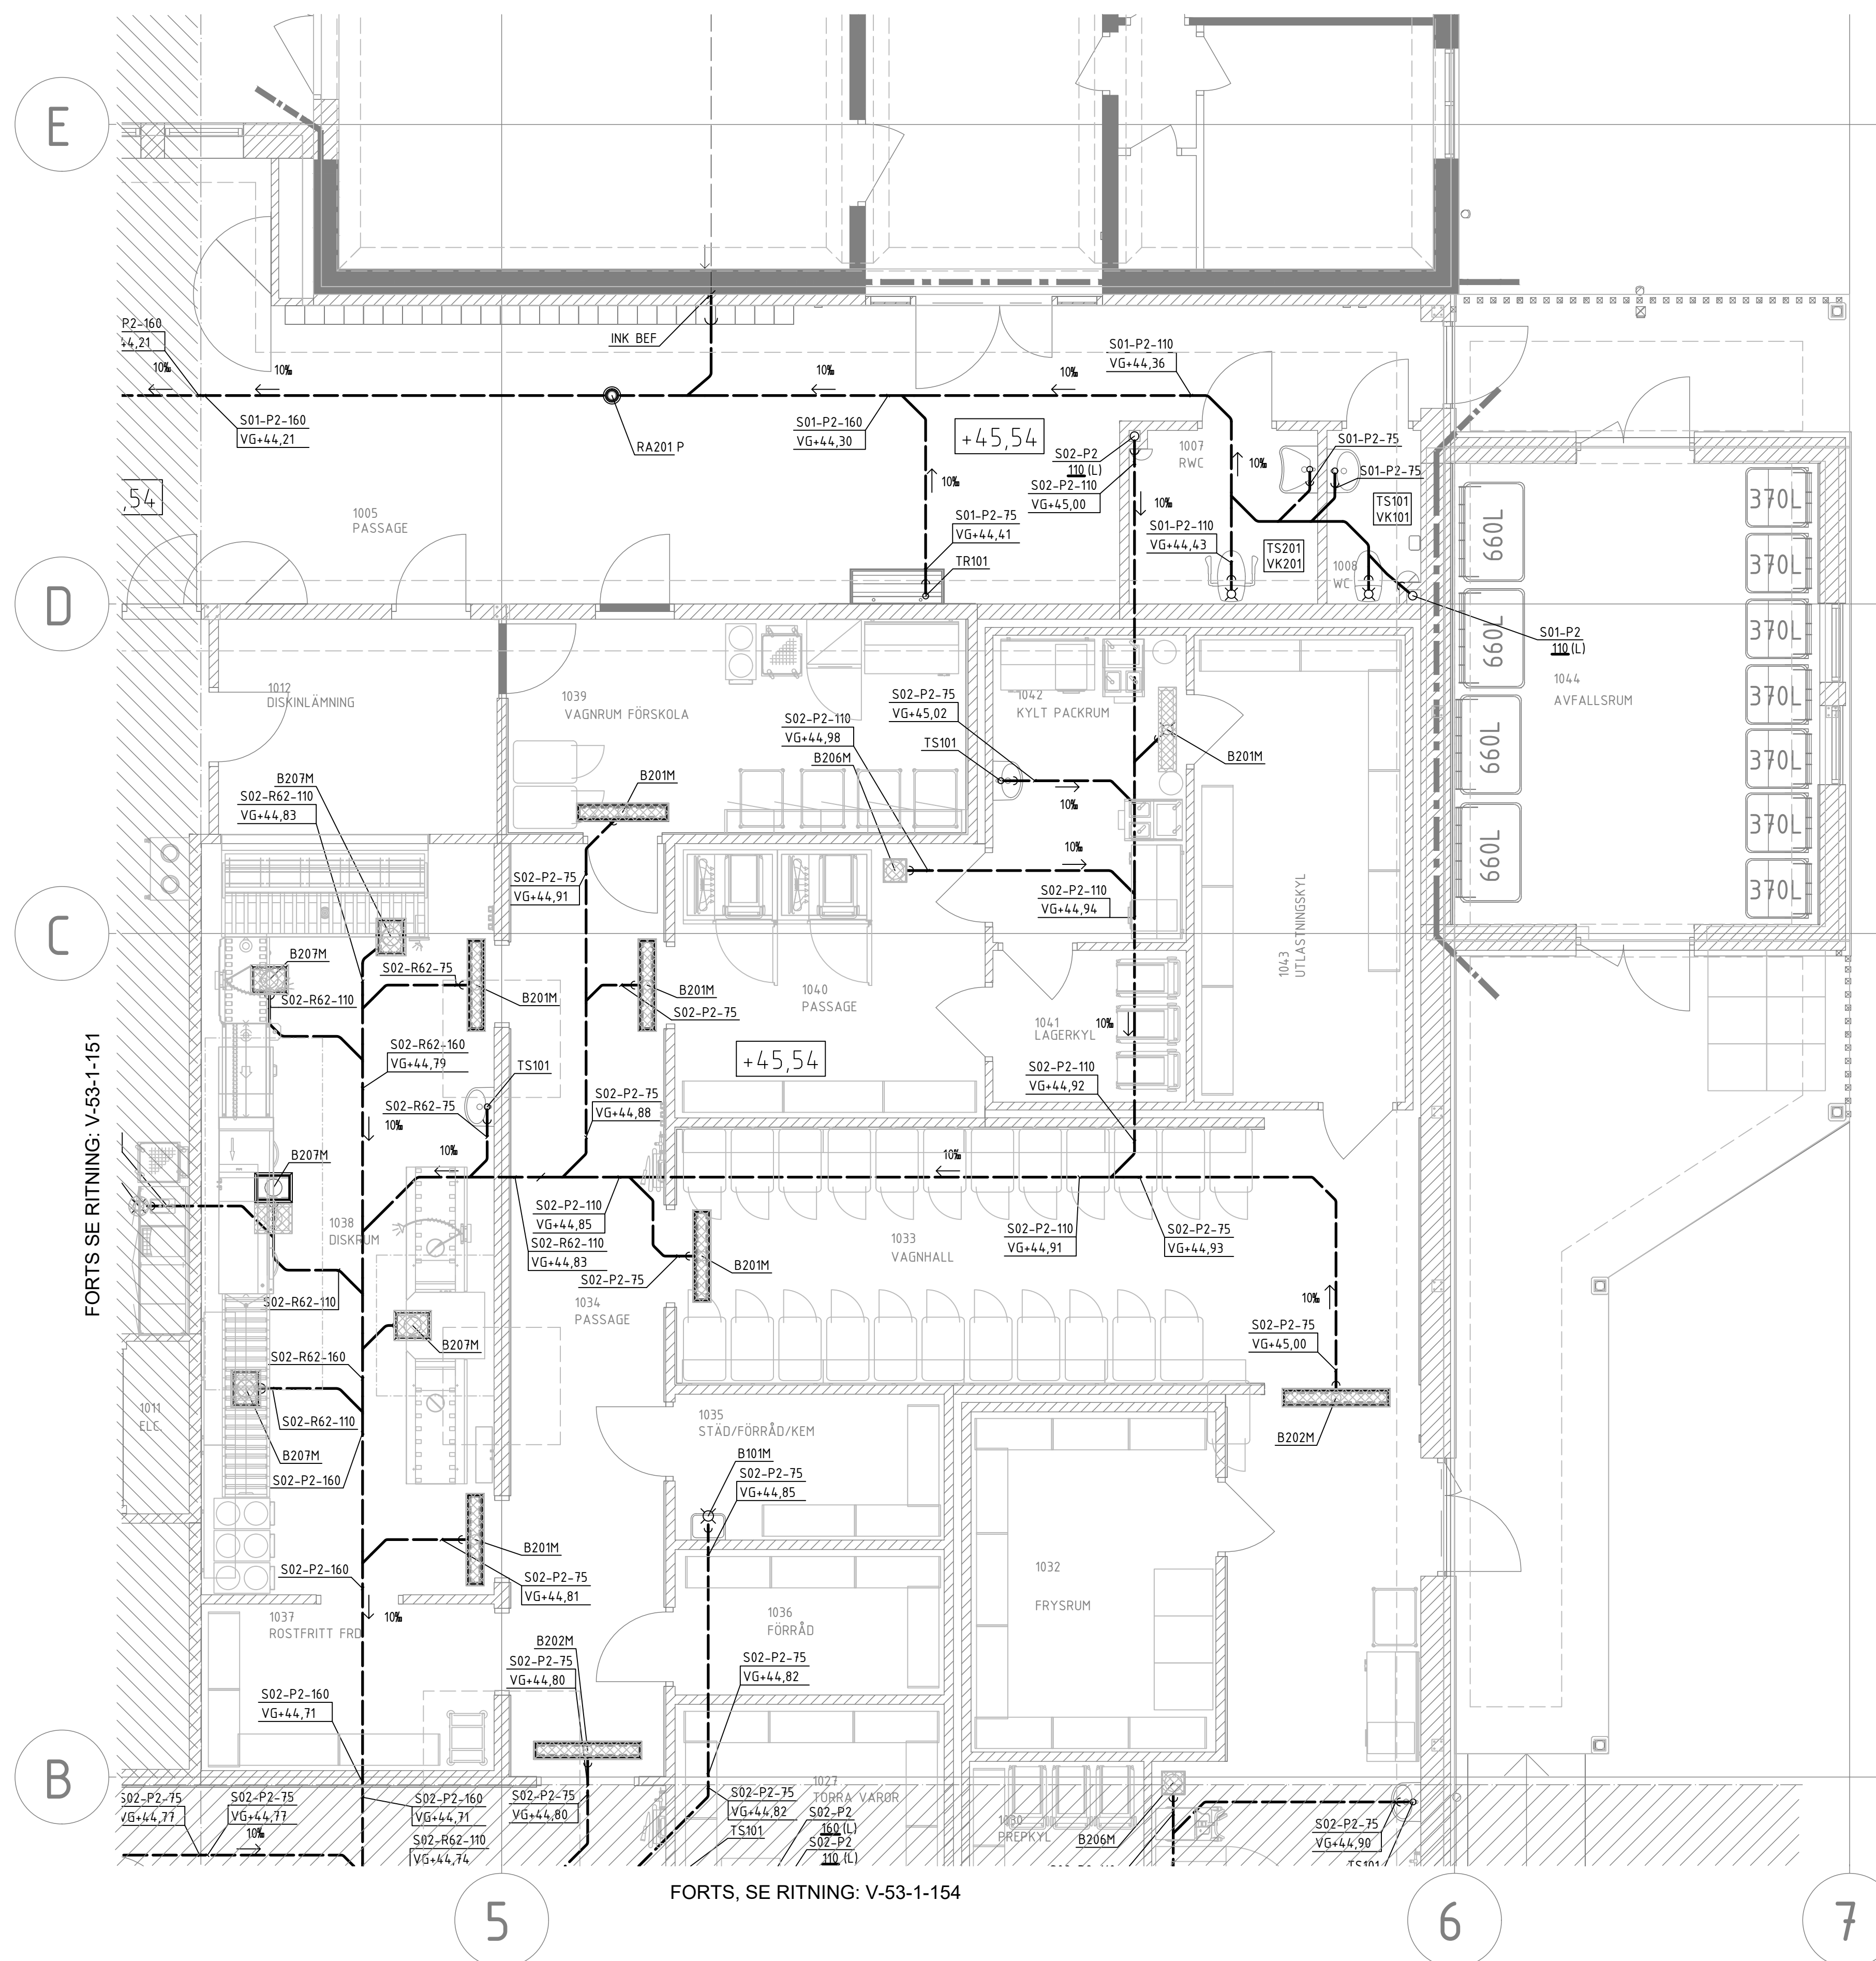

STATUS FÖRFRÅGNINGSUNDERLAG

|          |              |
|----------|--------------|
| HANDLING | BYGGHANDLING |
|----------|--------------|

|            |             |            |
|------------|-------------|------------|
| DATUM      | GODKÄND AV  | ÄNDRINGS I |
| 2025-01-31 | T.BERGSTRÖM | KFU0       |

|            |            |       |
|------------|------------|-------|
| 2023-01-31 | FIBERGLASS | RF 00 |
| BESTÄLLARE |            |       |



PROJEKTNAMN

CENTRAALKÖK

OMRADE  
ROBERTSFORS KOMMUN

|                |                   |
|----------------|-------------------|
| PROJEKTNUMMER  | ADRESS            |
|                | YTTRE RINGVÄGEN 4 |
| BÄDDRUMSNUMMER | BÄDDRUMSADRESS    |

|              |                         |
|--------------|-------------------------|
| DIARIENUMMER | FASTIGHET<br>FORDONET 1 |
| DISCIPLIN    | FÖRETAG                 |

|                |                       |
|----------------|-----------------------|
| DISCIPLIN      | FORETAG               |
| VS             | NORCONSULT SVERIGE AB |
| UPPDRAGSNUMMER | SKAPAD AV             |

|                             |                  |
|-----------------------------|------------------|
| UPPDRAGSNUMMER<br>108 83 71 | SKAPAD AV<br>MAN |
| TELEFON                     | KONTAKTPERSON    |

|               |                    |
|---------------|--------------------|
| 010 141 80 00 | JONAS JOHANSSON    |
| BYGGNADSVÄRK  | PLUSHÖJD (RH 2000) |

|             |            |             |
|-------------|------------|-------------|
|             |            | +45,54 (FG) |
| VANINGSPLAN | VANINGSDEL | DELOMRÅDE   |
| 1           |            | DEL 1 2 5 3 |

|                              |  |              |
|------------------------------|--|--------------|
| 1                            |  | DEL 4.2, 5.2 |
| SYSTEM                       |  |              |
| 53 SPILLVATTENINSTALLATIONER |  |              |

53 SPILLVATTENINSTALLATIONER

| SPECIFIKATION                       |
|-------------------------------------|
| PLAN 0 - DEL 4.2, 5.2, UNDER PLATTA |

|                  |       |        |
|------------------|-------|--------|
| RITNINGSKATEGORI | SKALA | FORMAT |
| PLAN             | 1:50  | A1     |

|                |        |
|----------------|--------|
| DOKUMENTNUMMER | ADRING |
| V-53-1-052     | A      |

SKALA 1:50

0 1 2 5

METER

THE BOARD: