
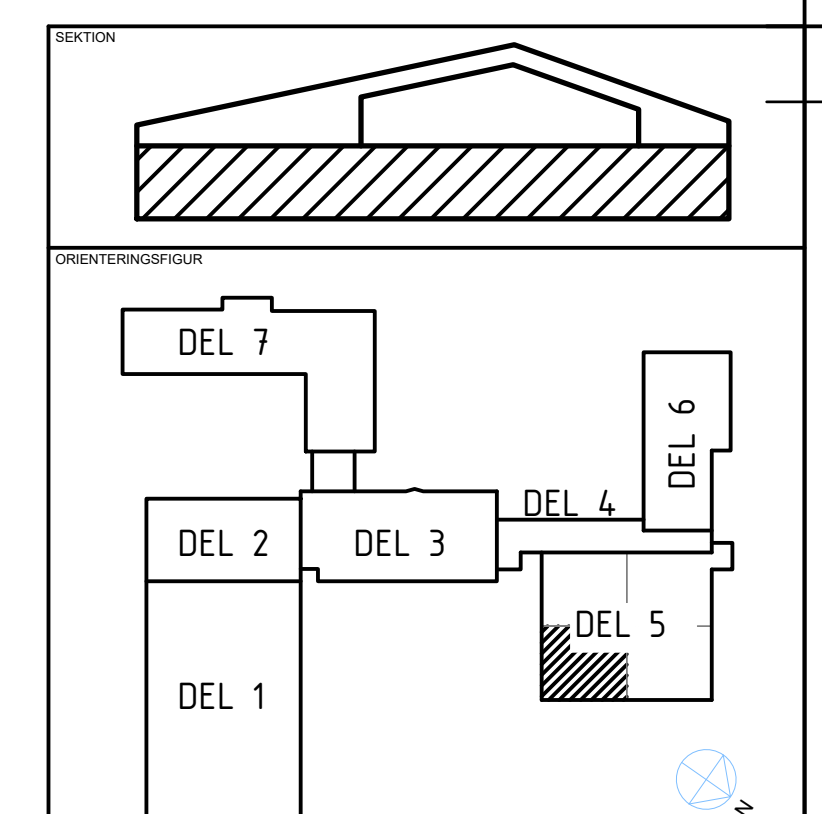


FÖRKLARINGSTEXT
SE RITNING V-50-0-001

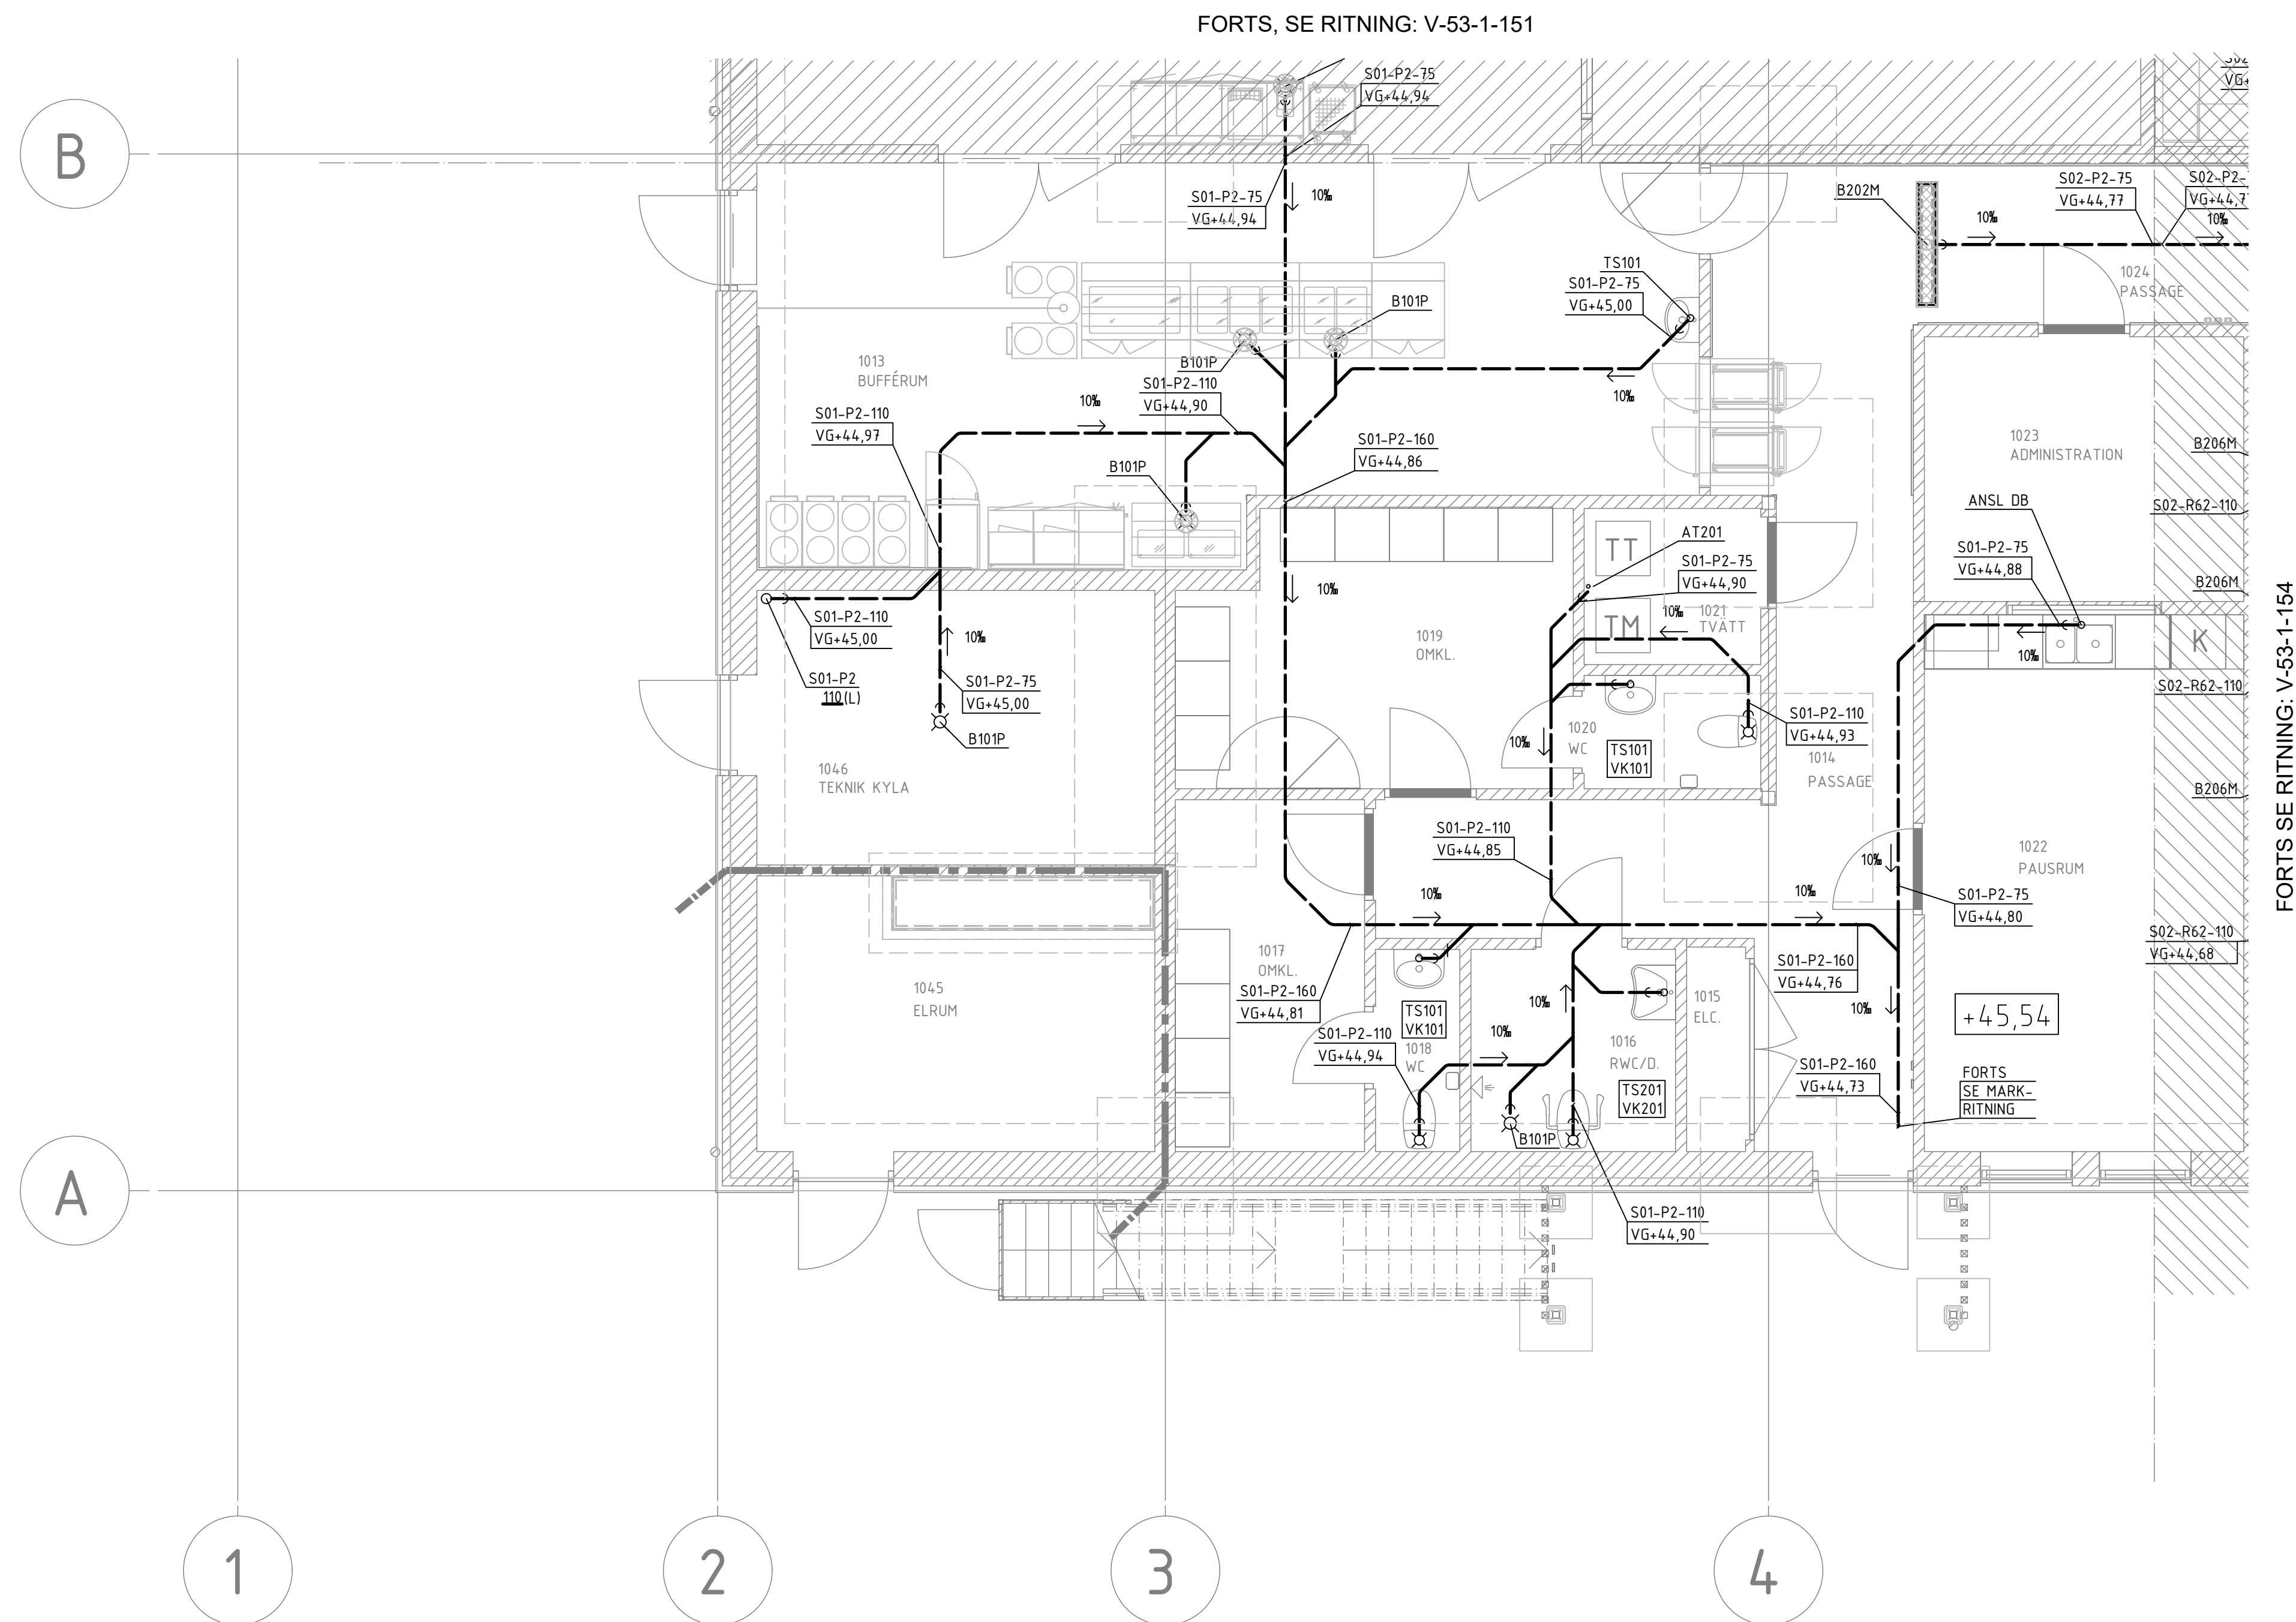

STATUS
FÖRFRÅGNINGSUNDERLAG

HANDLING	BYGGHANDLING
----------	--------------

DATUM	GODKÄND AV	ÄNDRINGS PM
2025-01-31	T.BERGSTRÖM	KFU01

2025-01-31	FIBERGLASSFRONT	RF 001
BESTÄLLARE		



PROJEKTNAMEN

OMRADE **ROBERTSFORS KOMMUN**

PROJEKTNUMMER	ADRESS
	NYTTRE BINGVÄGEN 1

	YTTRE RINGVAGEN 4
DIARIENUMMER	FASTIGHET FORDONET 1

DISCIPLIN	FÖRETAG
VS	NORCONSULT SVERIGE AB

UPPDRAGSNUMMER 108 83 71	SKAPAD AV MAN
-----------------------------	------------------

TELEFON	KONTAKTPERSON
010 141 80 00	JONAS JOHANSSON

BYGGNADSVÄRK	PLUSHÖJD (RH 2000) +45,54 (FG)
--------------	-----------------------------------

VÄNINGSPLAN 1	VÄNINGSDEL	DELOMRÅDE DEL 5.3
------------------	------------	----------------------

SYSTEM
53 SPILLVATTENINSTALLATIONER
SPECIFIKATION

SPECIFIKATION		
PLAN 0 - DEL 5.3, UNDER PLATTA		
RETURNKATEGORI	SKALA	FORMAT

RITNINGSKATEGORI	SKALA	FORMAT
PLAN	1:50	A1
DOKUMENTNUMMER	ÄNDRING	

DOKUMENTNUMMER	V-53-1-053	ÄNDRING	A
----------------	------------	---------	---

NAME: _____ DATE: _____ PERIOD: _____ TEACHER: _____ CLASS: _____	TEACHER'S SIGNATURE: _____ DATE: _____
---	--