
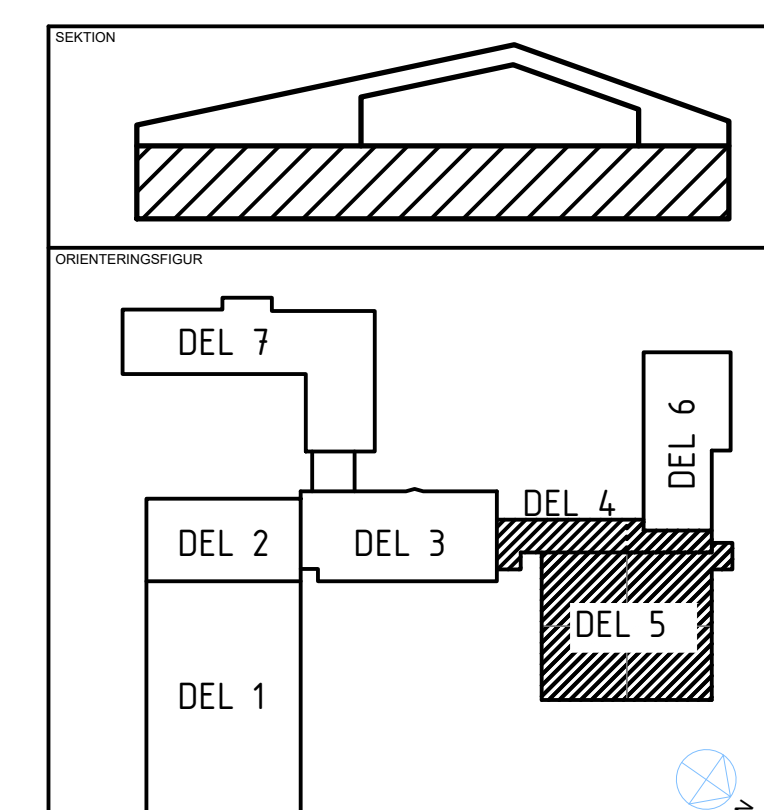


FÖRKLARINGSTEXT
SE RITNING V-50-0-001

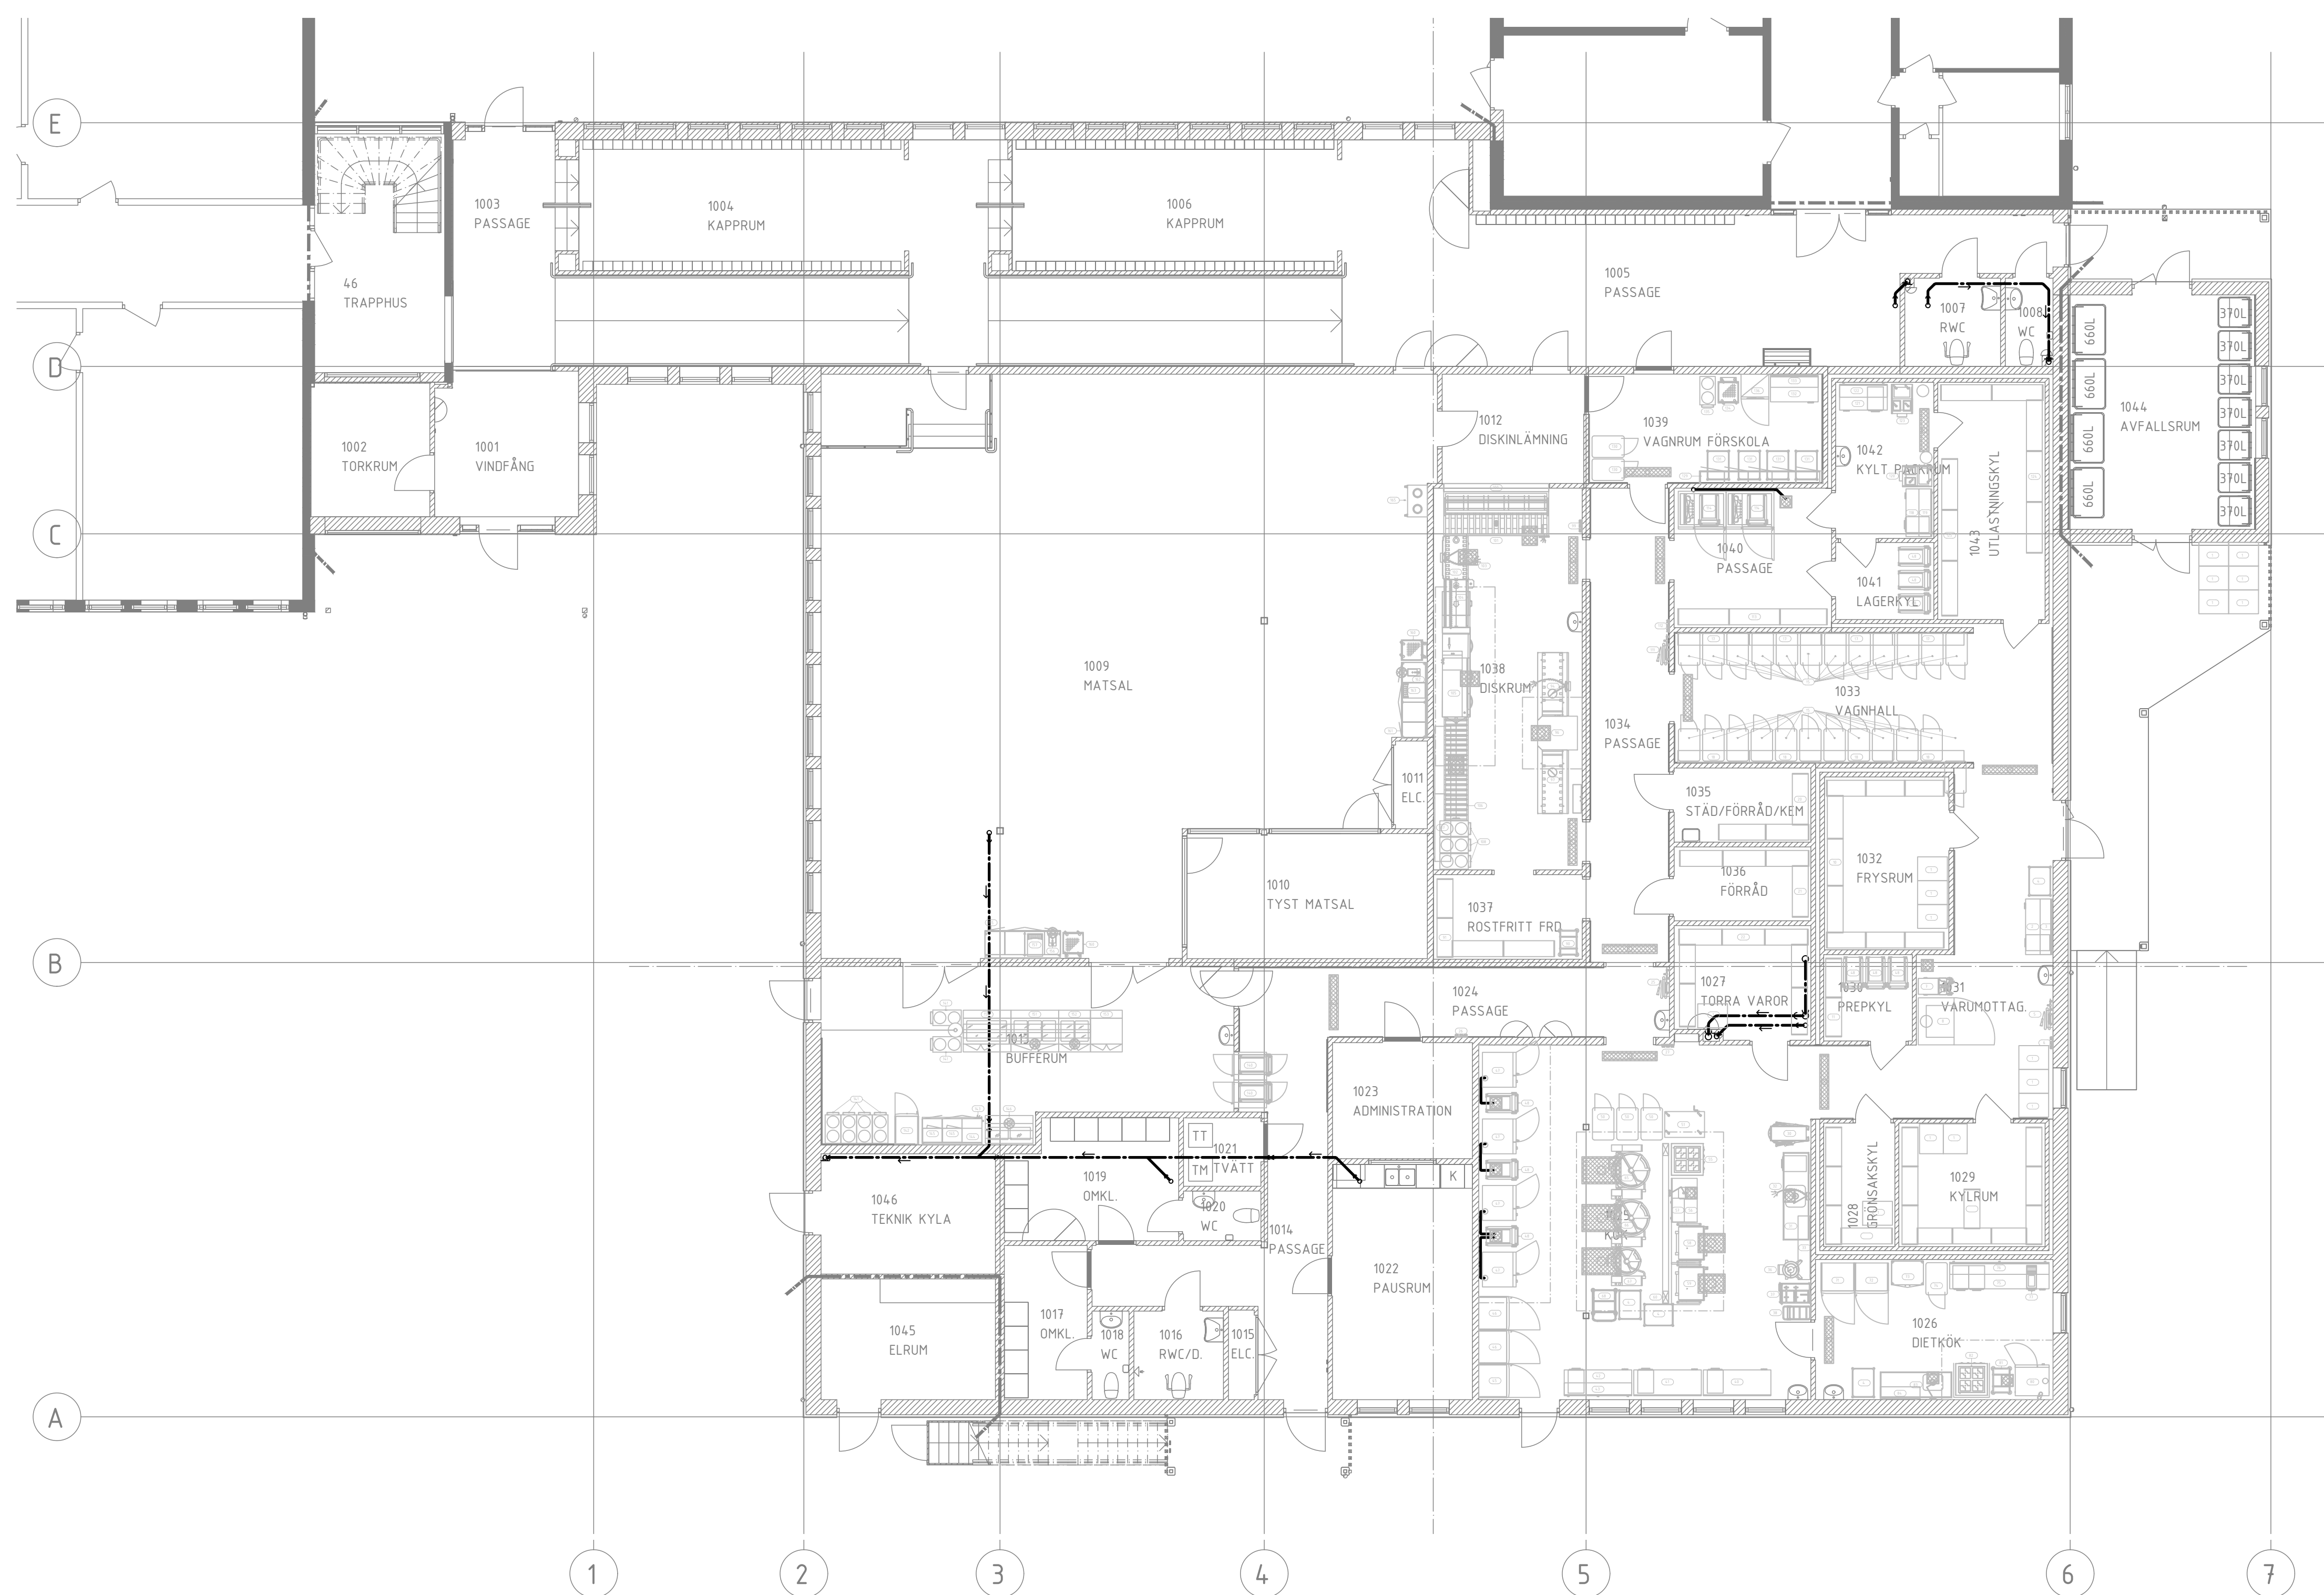

STATUS FÖRFRÅGNINGSUNDERLAG

HANDLING	BYGGHANDLING
----------	--------------

DATUM	GODKÄND AV	ÄNDRINGS I
2025-01-31	T.BERGSTRÖM	KFU0

2023-01-31	T. BERGSTRÖM	RI 00
BESTÄLLARE		



PROJEKTNAMN

CENTRAALKÖK

OMRADE
ROBERTSFORS KOMMUN

PROJEKTNUMMER	ADRESS
	YTTRE RINGVÄGEN 4

	YTIRE RINGVAGEN 4
DIARIENUMMER	FASTIGHET FORDONET 1

DISCIPLIN	FÖRETAG
VS	NORCONSULT SVERIGE AB

UPPDRAKTSNUMMER	SKAPAD AV
108 83 71	MAN

TELEFON	KONTAKTPERSON
010 141 80 00	JONAS JOHANSSON

BYGGNADSVÄRK	PLUSHÖJD (RH 2000)
	+44,60, +45,07, +45,54 (FG)

VÄNINGSPLAN	VÄNINGSDEL	DELOMRÅDE
1		DEL 4, 5

53 SPILLVATTENINSTALLATIONER

SPECIFIKATION		
PLAN 1 - ÖVERSIKT		
RETNINGSKATEGORI	OMFÄTTNING	FORMAT

RITNINGSKATEGORI	SKALA	FORMAT
PLAN	1:100	A1
DOKUMENTNUMMER	ÄNDRING	

DOKUMENTNUMMER	ÄNDERUNG
V-53-1-101	A

SKALA 1:100

0 1 2 5 10
METER

FILE NAME:	
------------	--