


FÖRKLARINGSTEXT
SE RITNING V-50-0-001

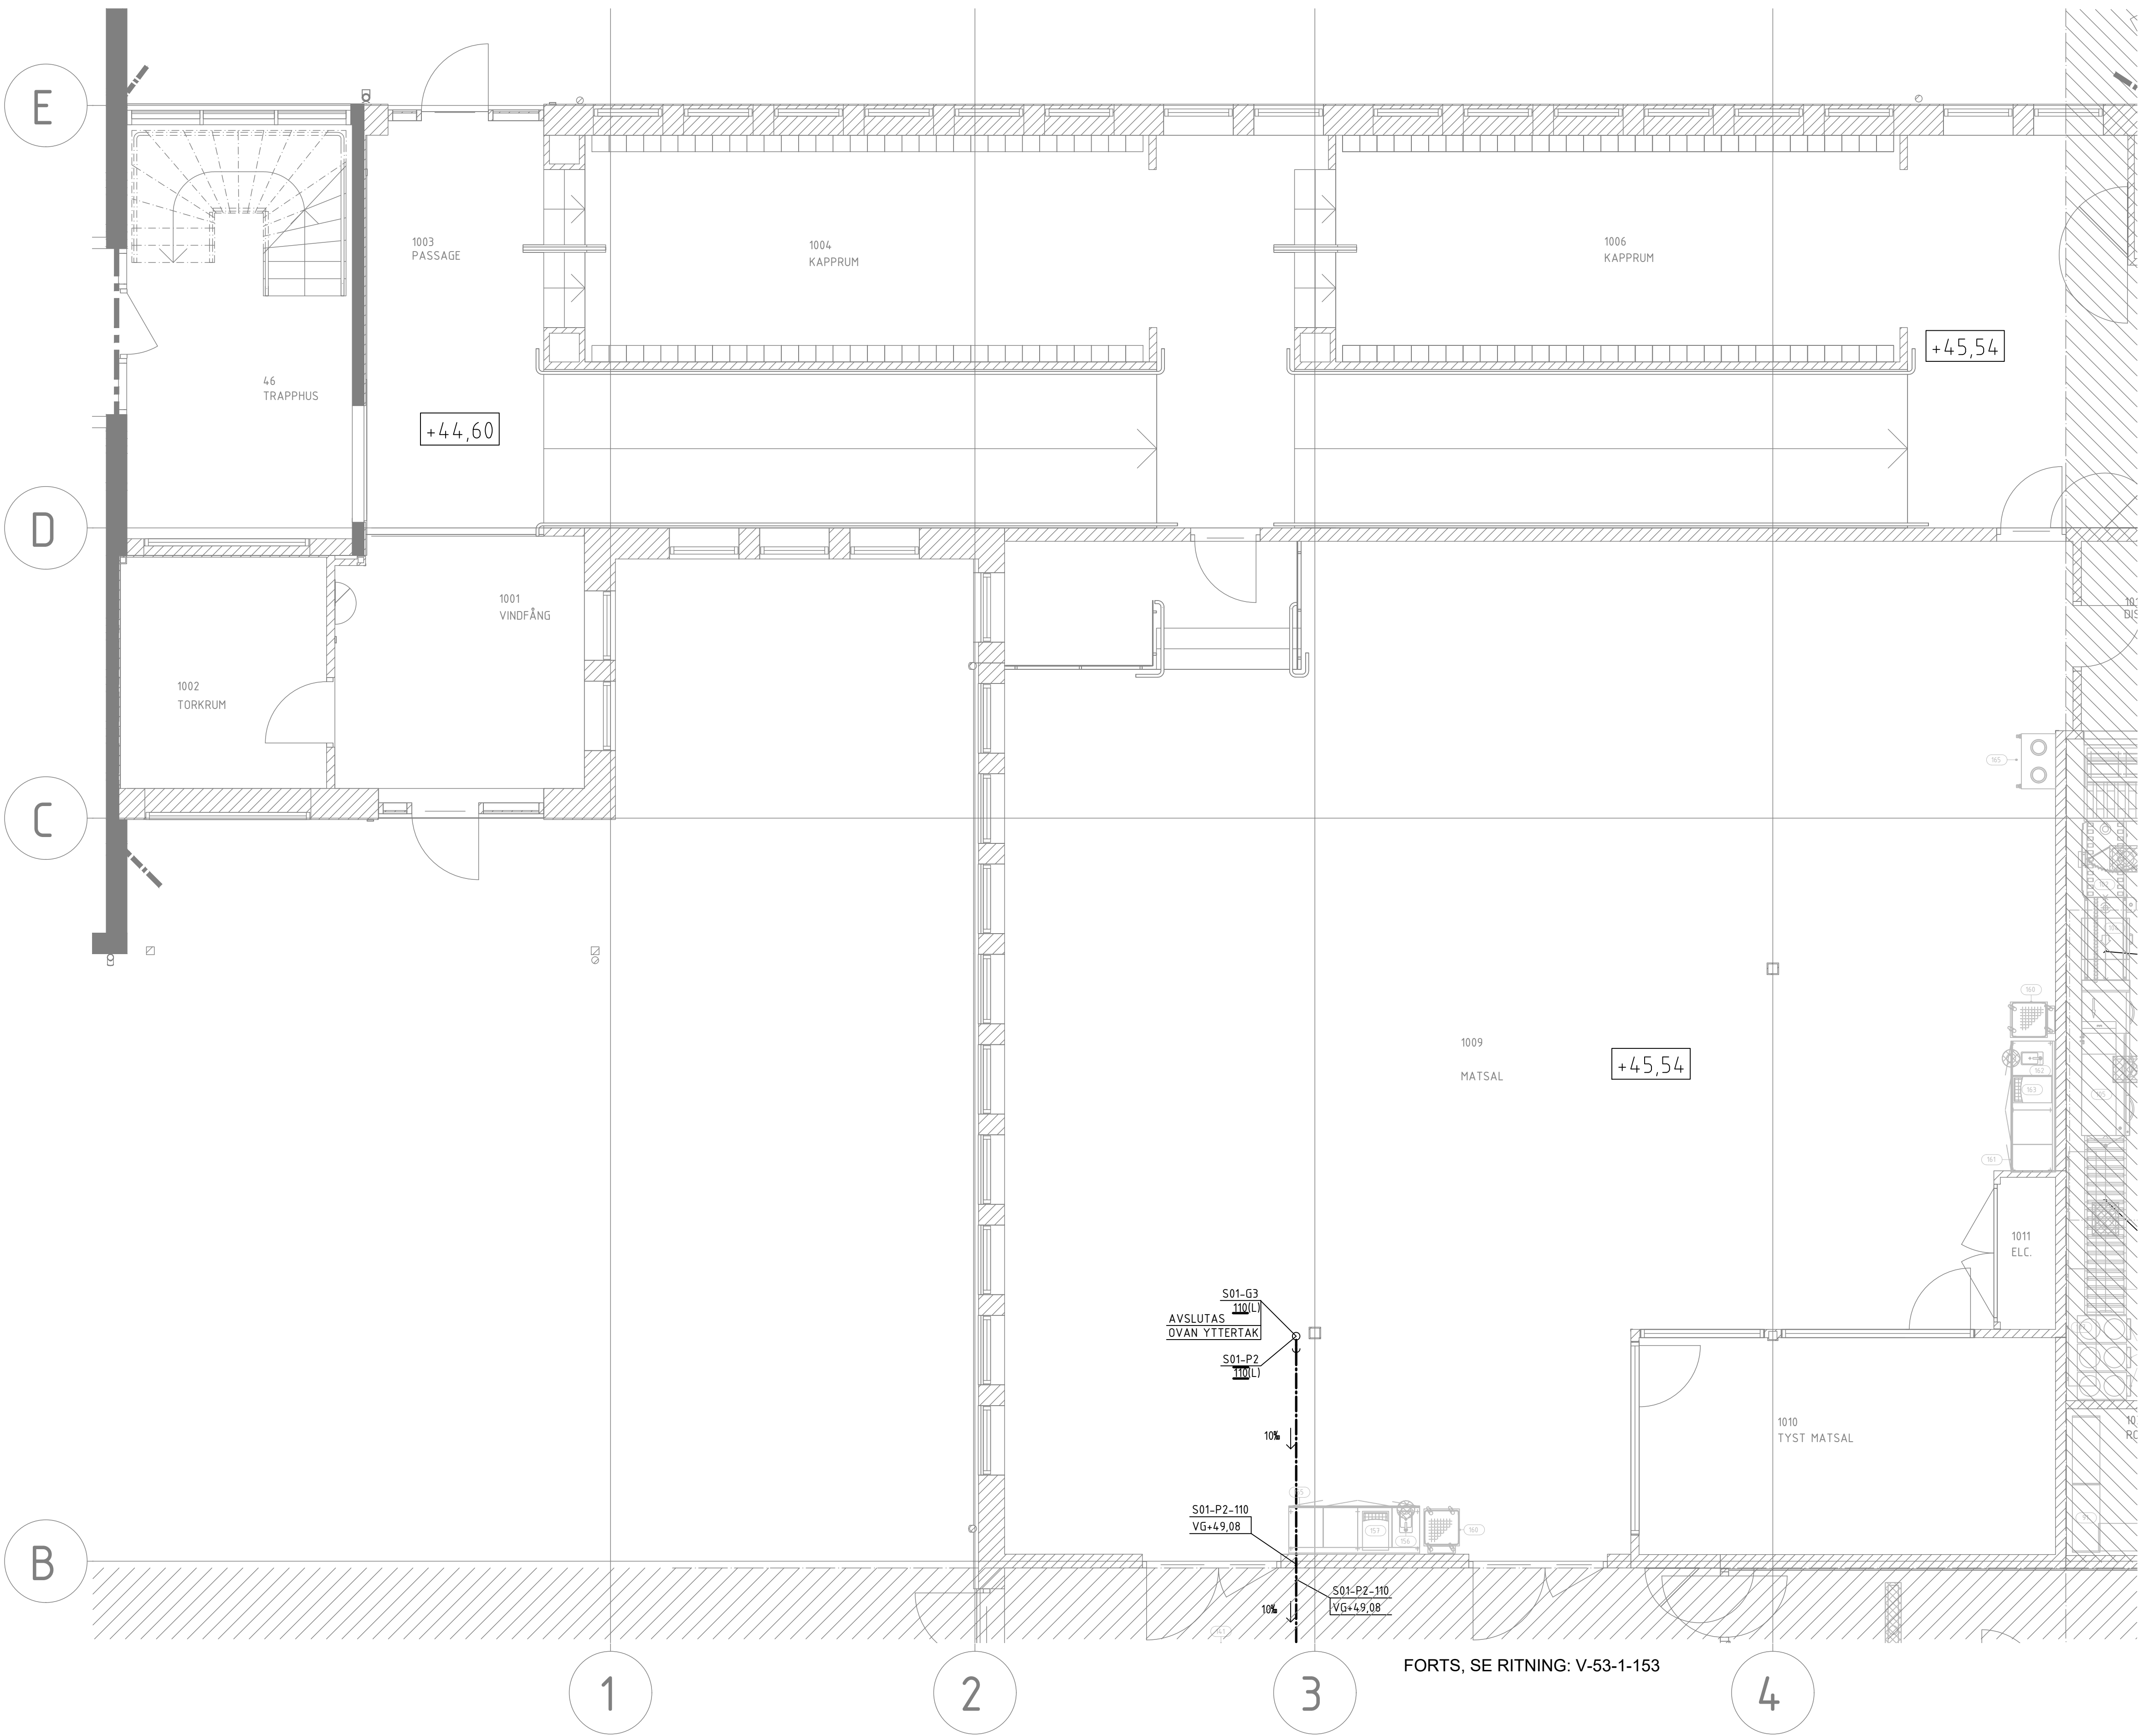

FORTS SE RITNING: V-53-1-152

SEKSTION

ORIENTERINGSPOL

DEL 1 DEL 2 DEL 3 DEL 4 DEL 5 DEL 6 DEL 7

STATUS

FÖRFRÅGNINGSUNDERLAG

HANDLING

BYGGHANDLING

DATUM 2025-01-31 GODKÄND AV T.BERGSTRÖM ANDRINGS PM KFU01

BESTÄLLARE

ROBERTSFORS KOMMUN

PROJEKTNAMN

CENTRALEKÖK

OMRADE

ROBERTSFORS KOMMUN

PROJEKTNUMMER

YTTRE RINGVÄGEN 4

DARIENUMMER

FÖRORDNET 1

DISCIPLIN

NORCONSULT SVERIGE AB

OPPRORAGNUMMER

MAN

TELEFON

010 141 80 00

BYGGNADSVÄRKE

JONAS JOHANSSON

PLANINGSPLAN

1

SYSTEM

53 SPILLVATTENINSTALLATIONER

RITNINGSKATEGORI

PLAN

DOKUMENTNUMMER

V-53-1-151

SKALA


1:50

FORMAT

A1

ANDRING

A

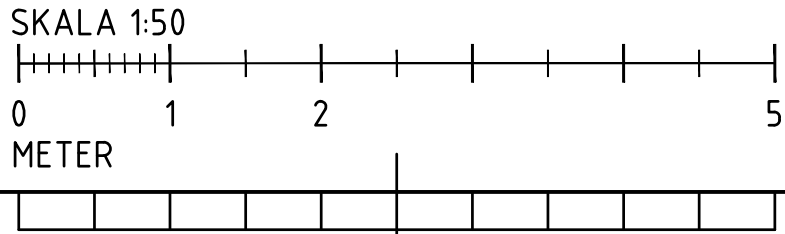

FORTS, SE RITNING: V-53-1-153

FILNAMN: