
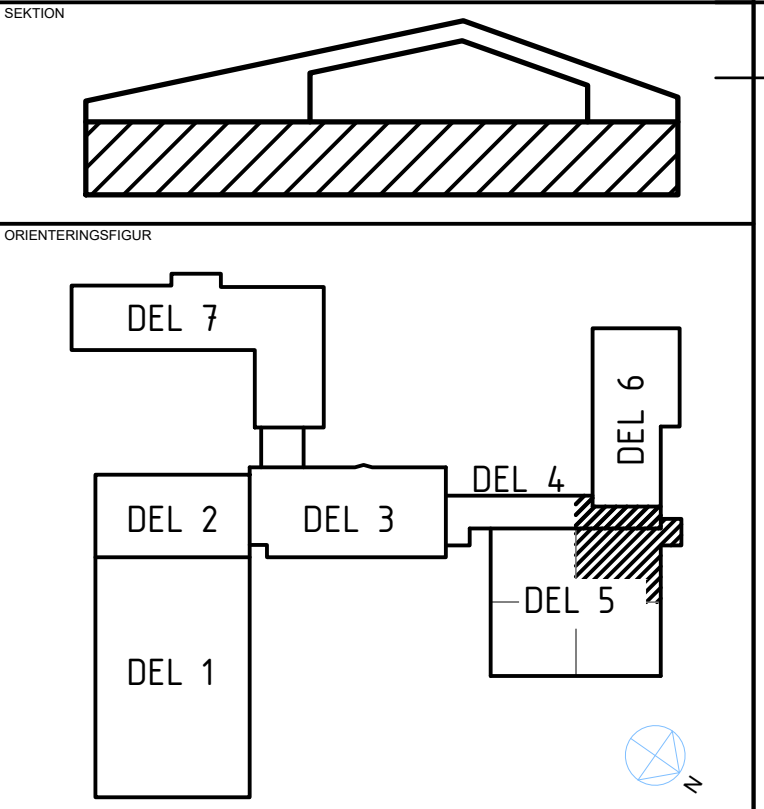
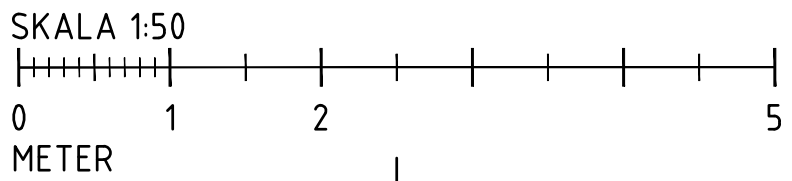


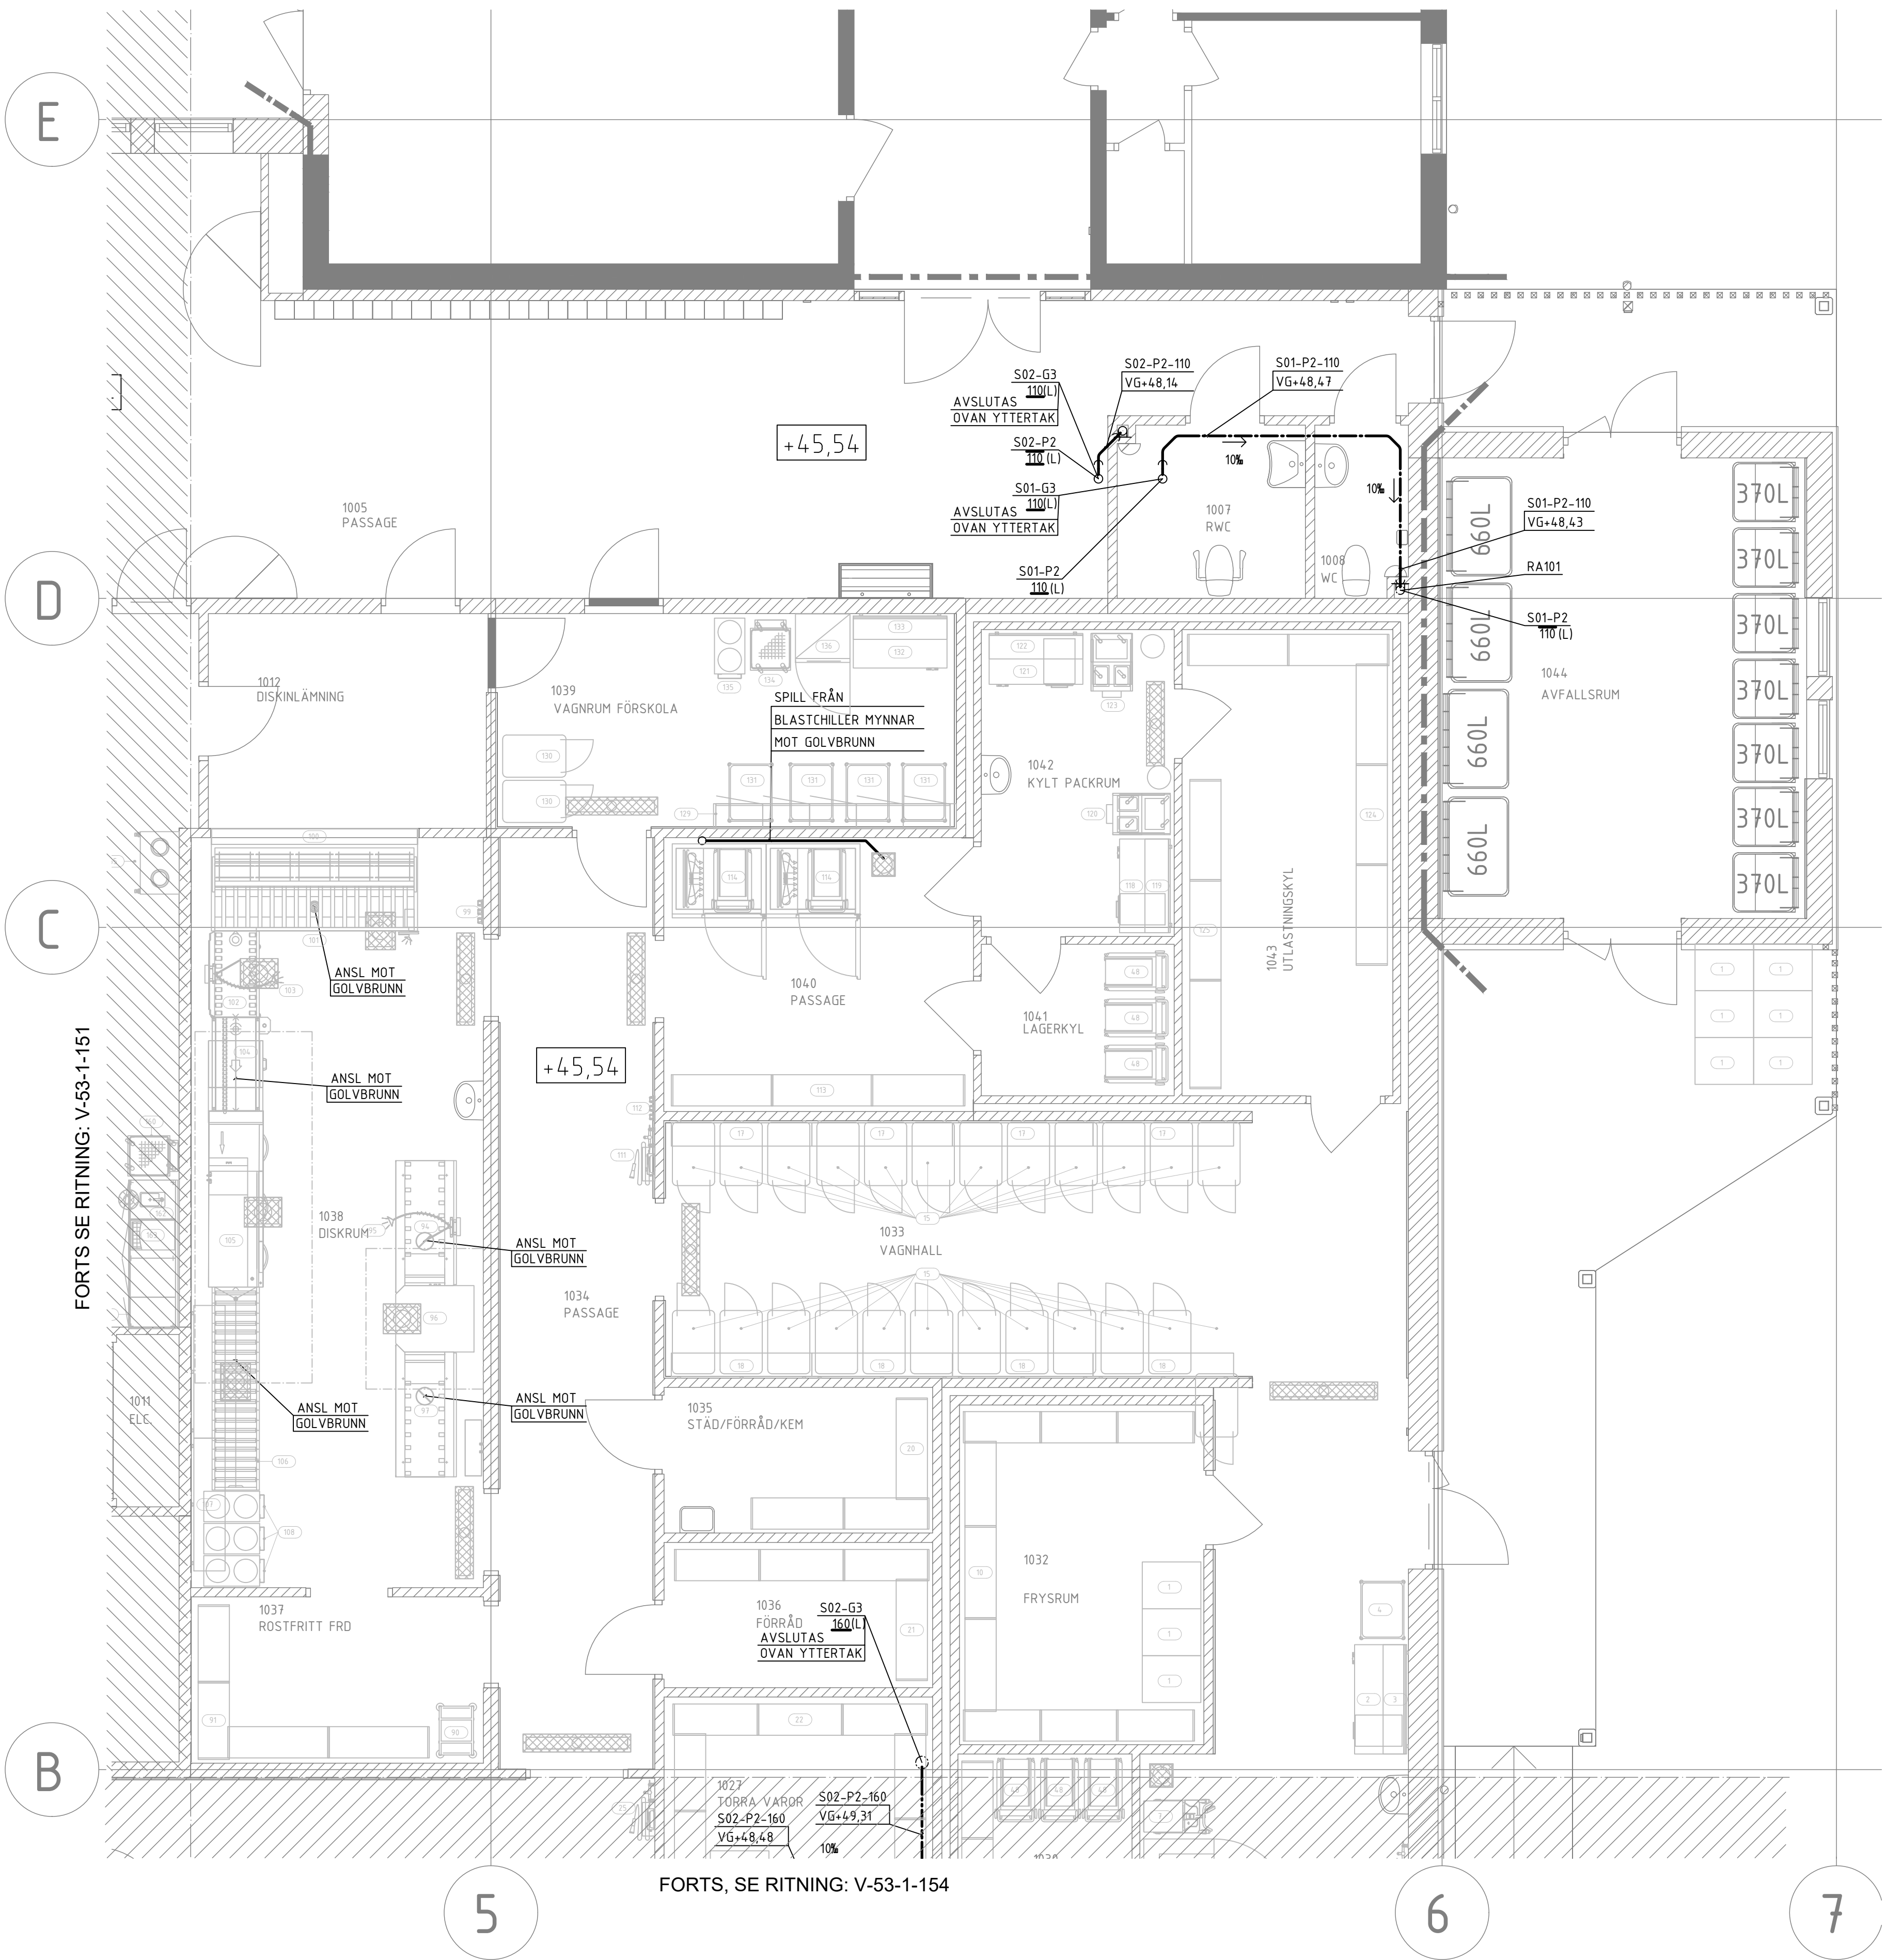

SEKTION		
ORIENTERINGSDIAGRAM		
STATUS		
FÖRFRÅGNINGSUNDERLAG		
HANDLING		
BYGGHANDLING		
DATUM	GODKÄND AV	ÄNDRINGS PM
2025-01-31	T.BERGSTRÖM	KFU01
BESTÄLLARE		
ROBERTSFORS KOMMUN		
PROJEKTNAMN		
CENTRALEKÖK		
OMRÅDE		
ROBERTSFORS KOMMUN		
PROJEKTNUMMER	FÖRRETT	
108 83 71	YTTRE RINGVÄGEN 4	
DARIENUMMER	FÖRRETT	
108 83 71	FÖRRETT	
DISCIPLIN	FÖRETAG	
108 83 71	NORCONSULT SVERIGE AB	
UPPDRAGSNUMMER	SKAPAD AV	
108 83 71	MAN	
TELEFON	KONTAKTPERSON	
010 141 80 00	TOMAS BERGSTRÖM	
BYGGNADSVÄRDE	KULSHÖJD (RM 2000)	
108 83 71	+45,54 (FG)	
VÄNINGSPLAN	VÄNINGSDEL	DELOMRÅDE
1	1	DEL 4.2, 5.2
SYSTEM		
53 SPILLVATTENINSTALLATIONER		
BESKRIVNING		
PLAN 1 - DEL 4.2, 5.2		
RITNINGSKATEGORI	SKALA	FORMAT
PLAN	1:50	A1
DOKUMENTNUMMER	ÄNDRING	
V-53-1-152	A	