




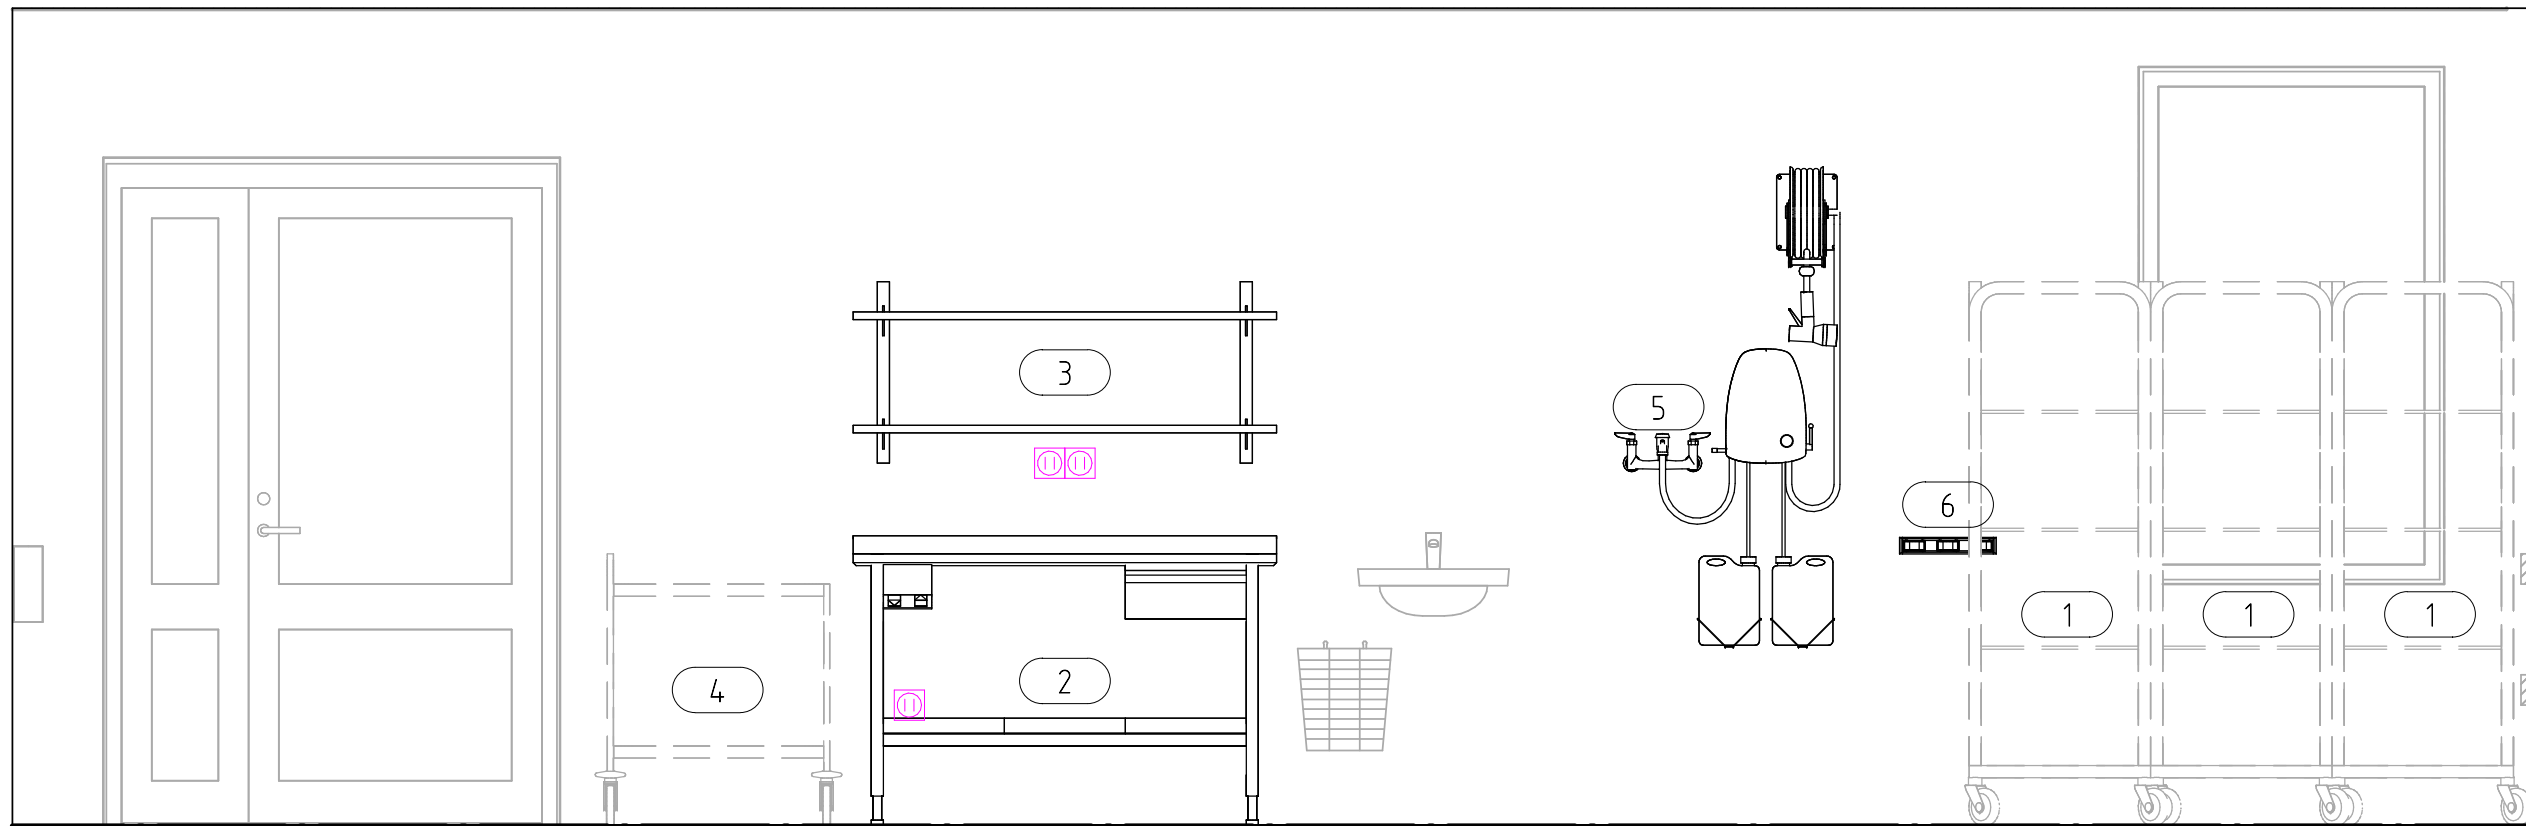


A

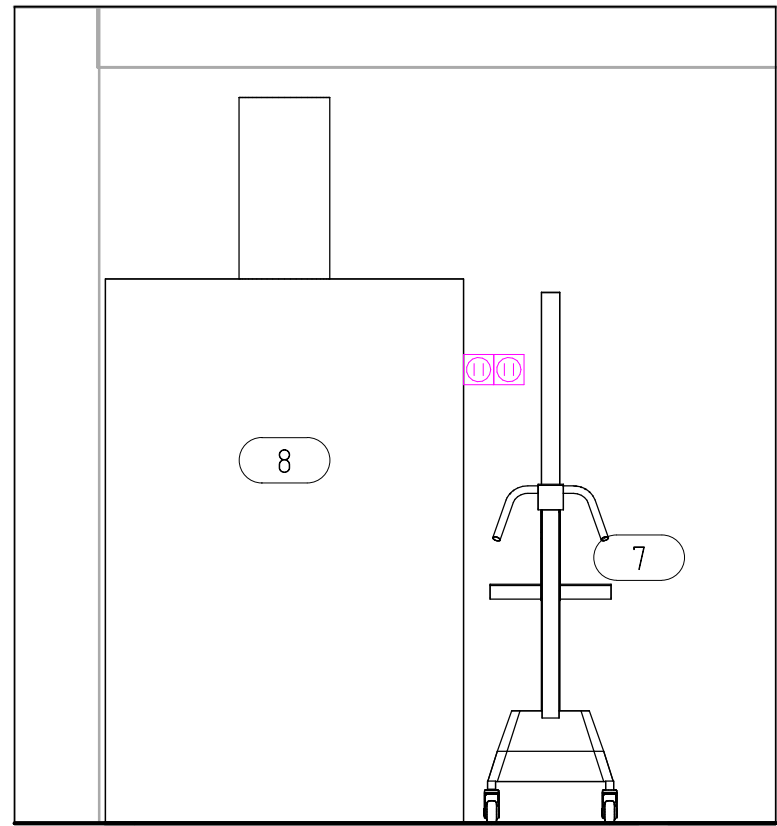


B

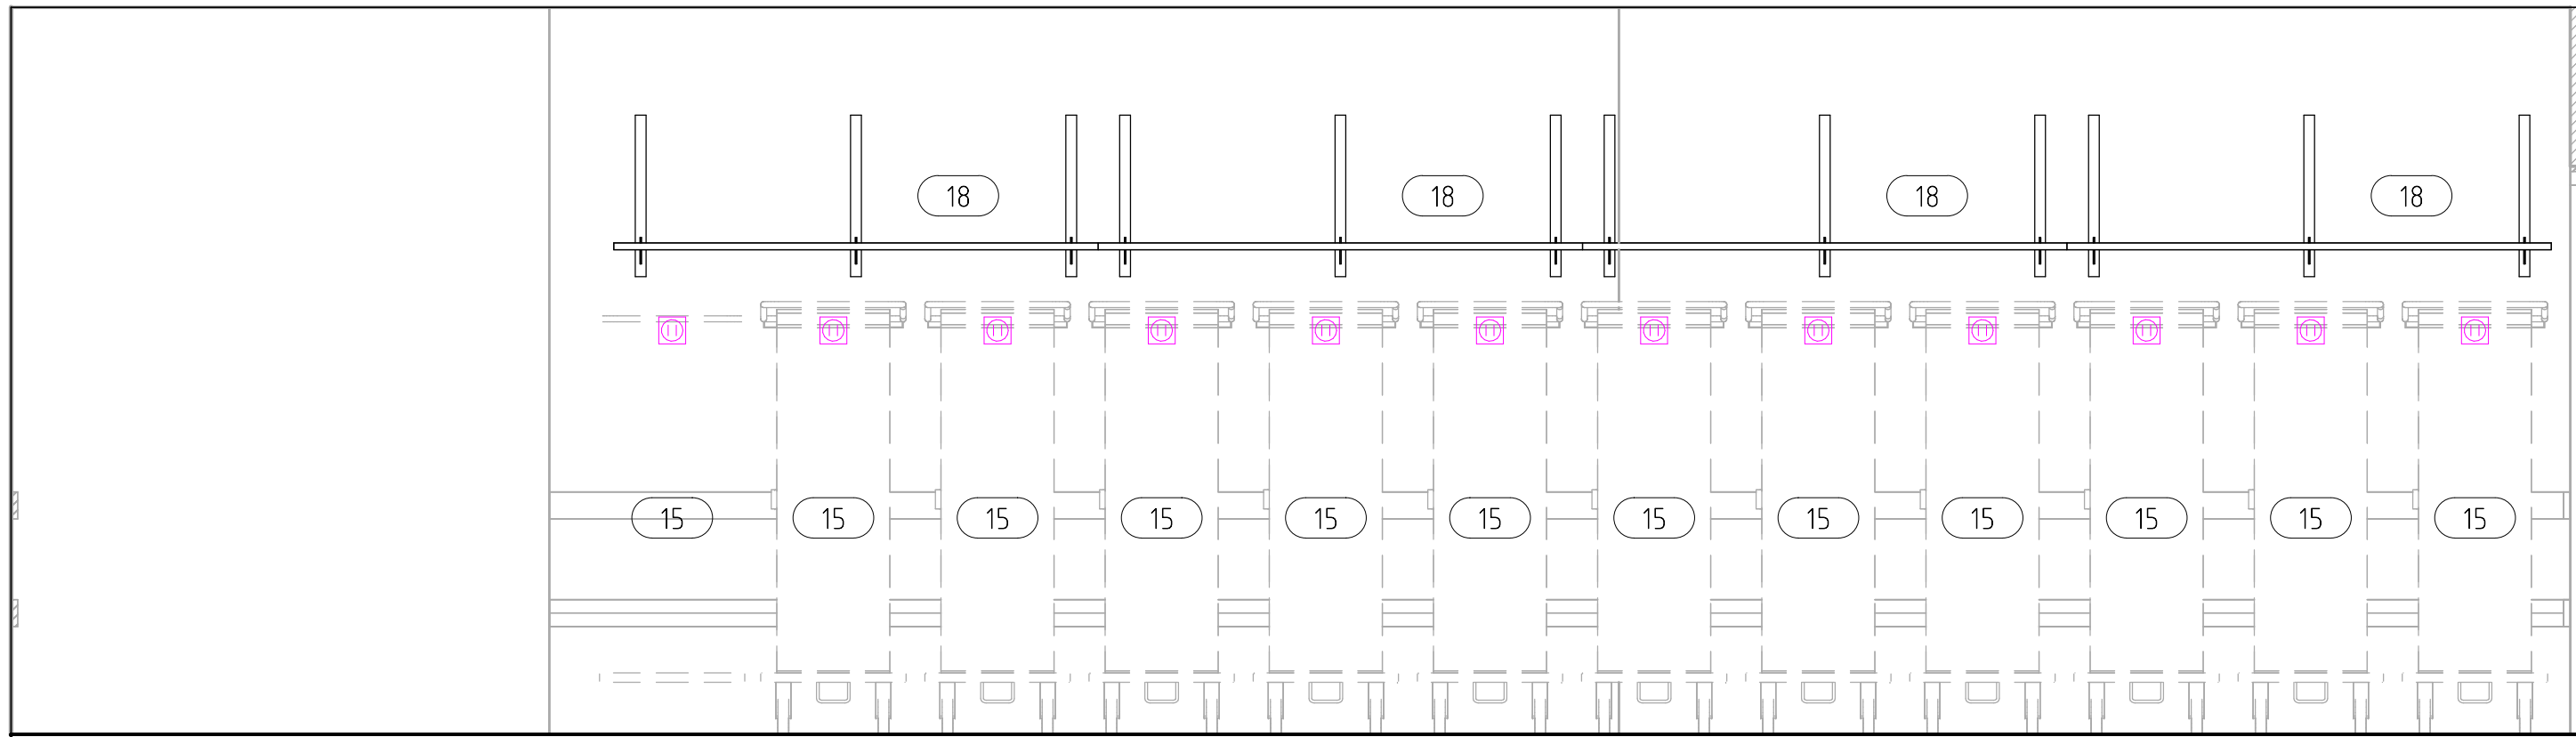


D

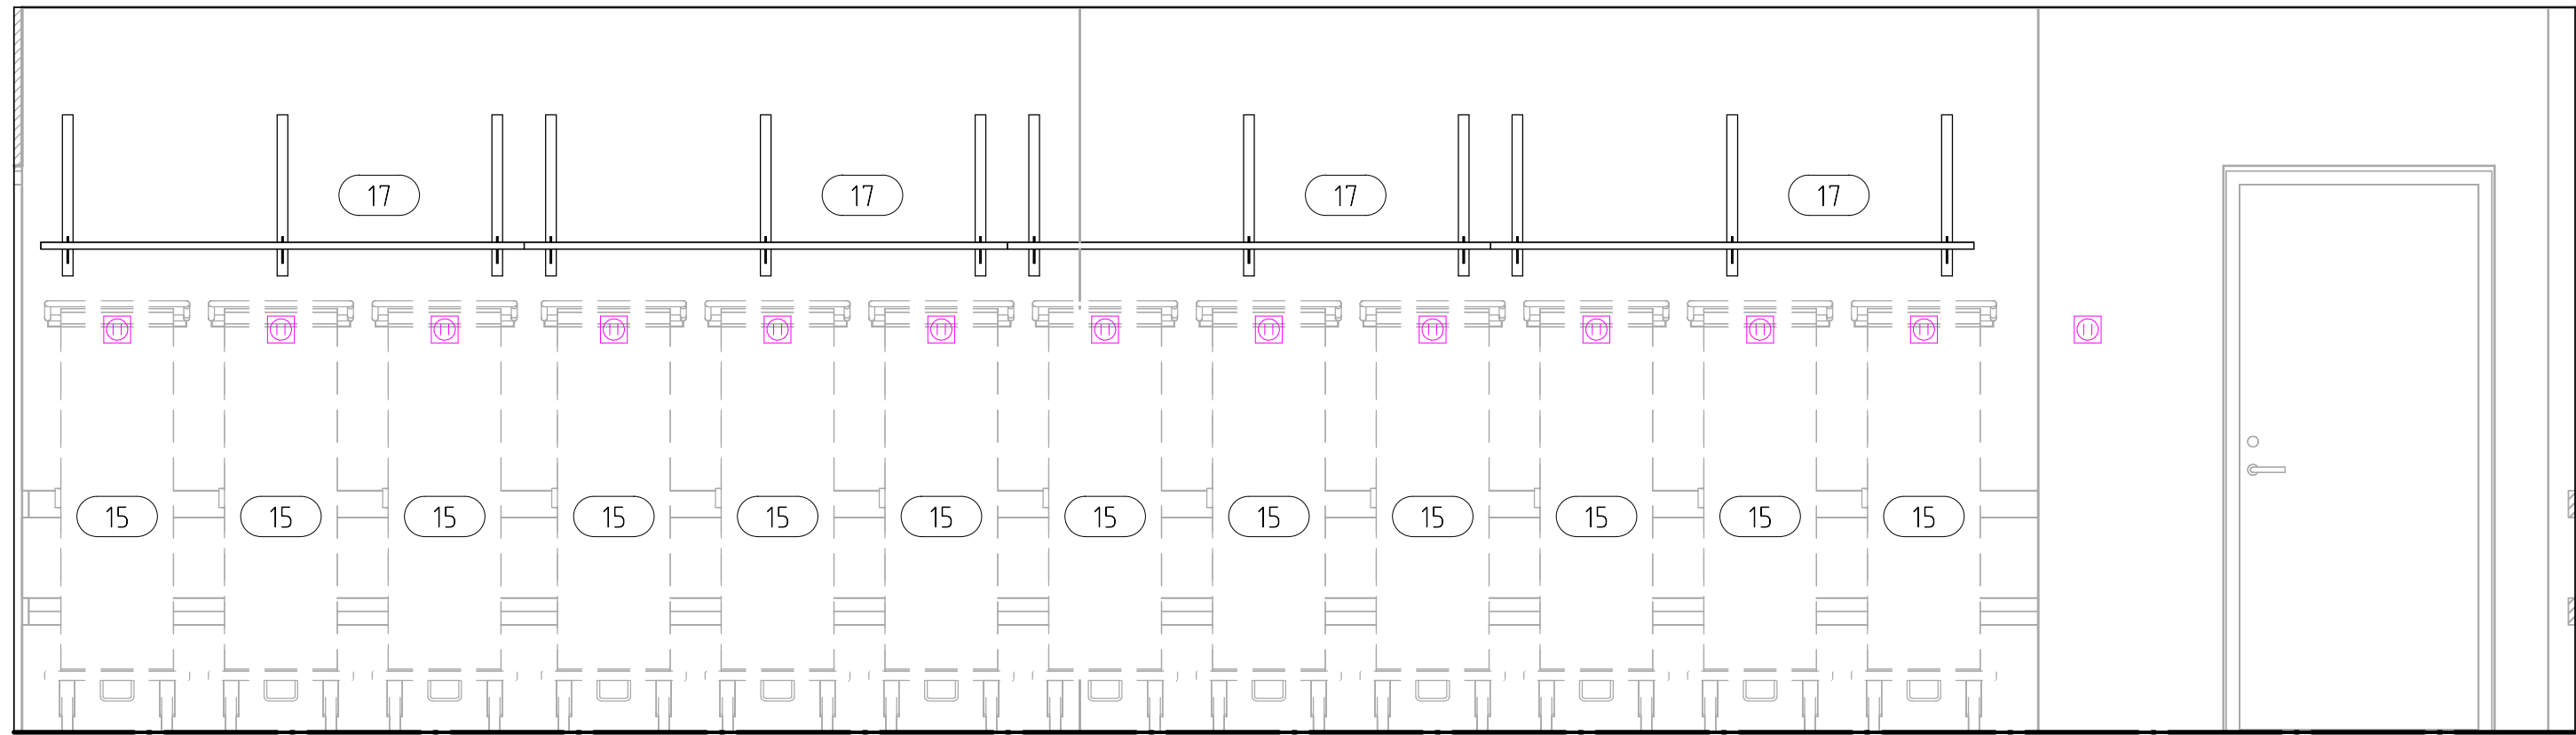


E

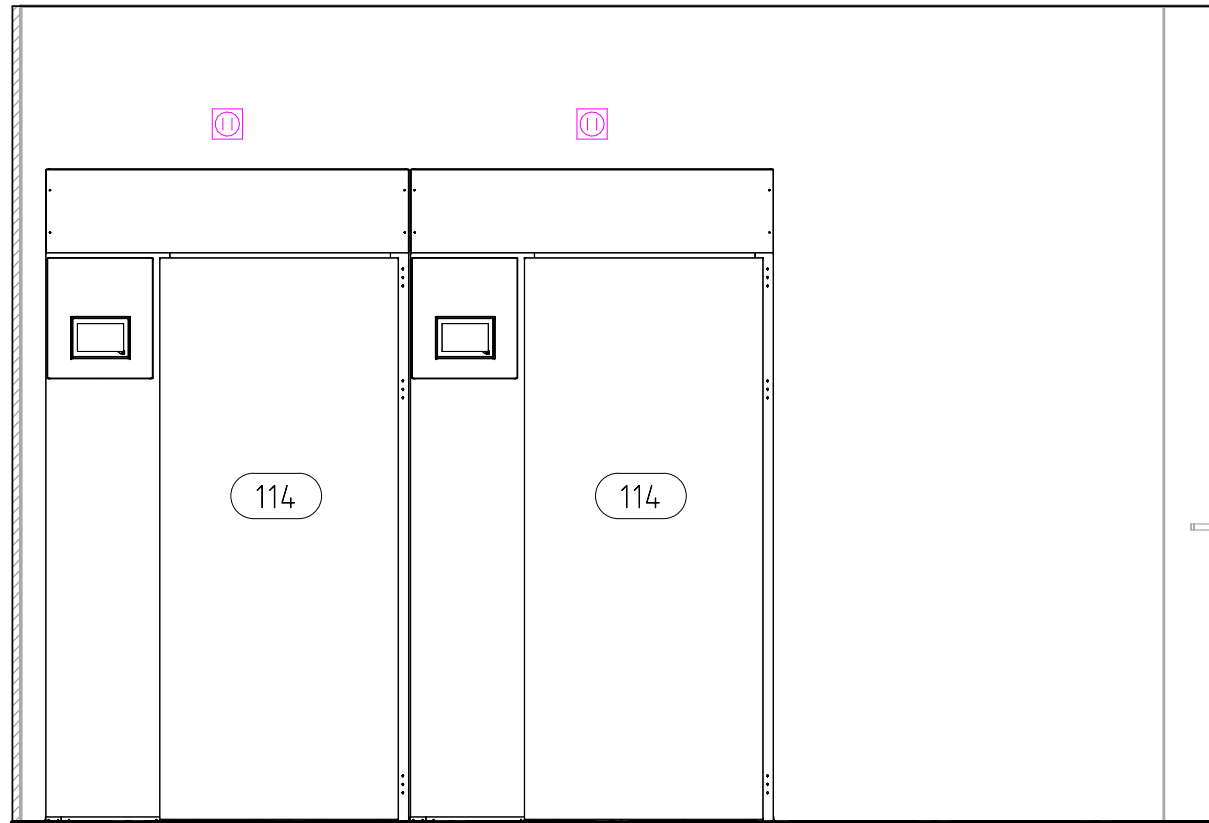


F

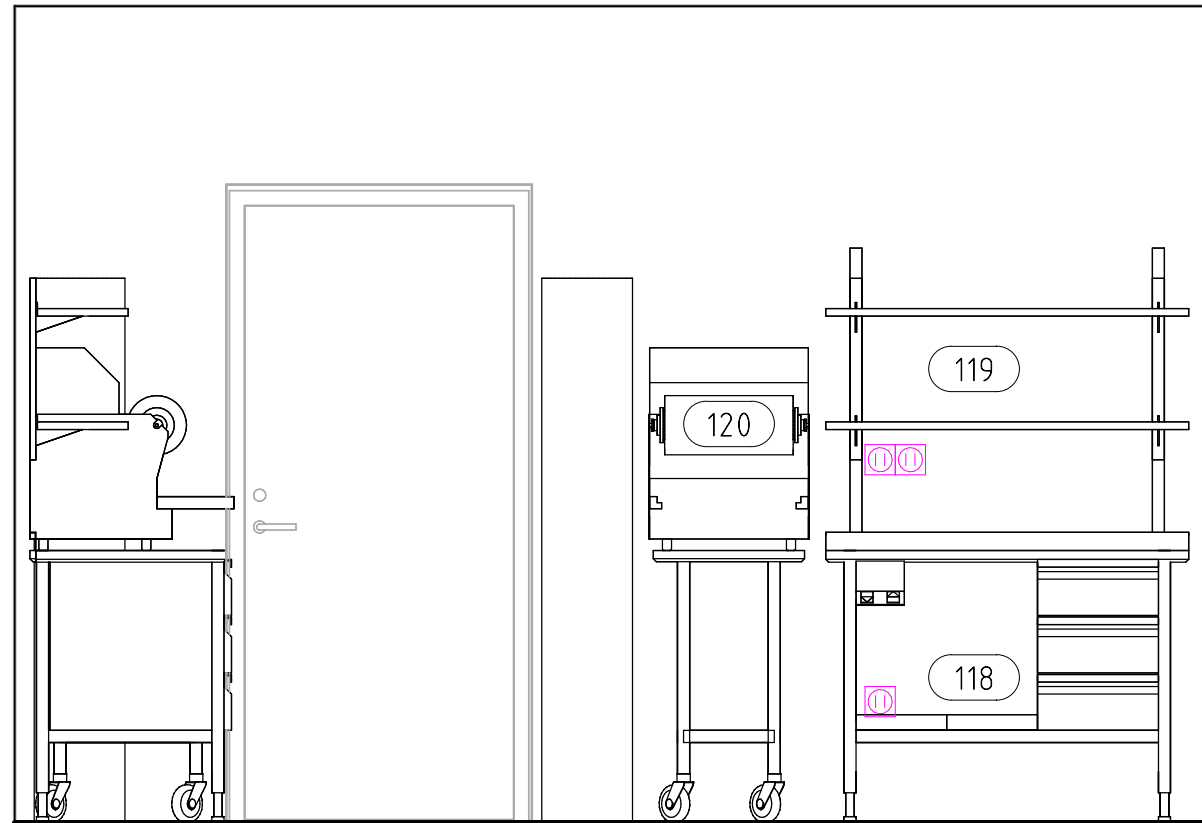


G

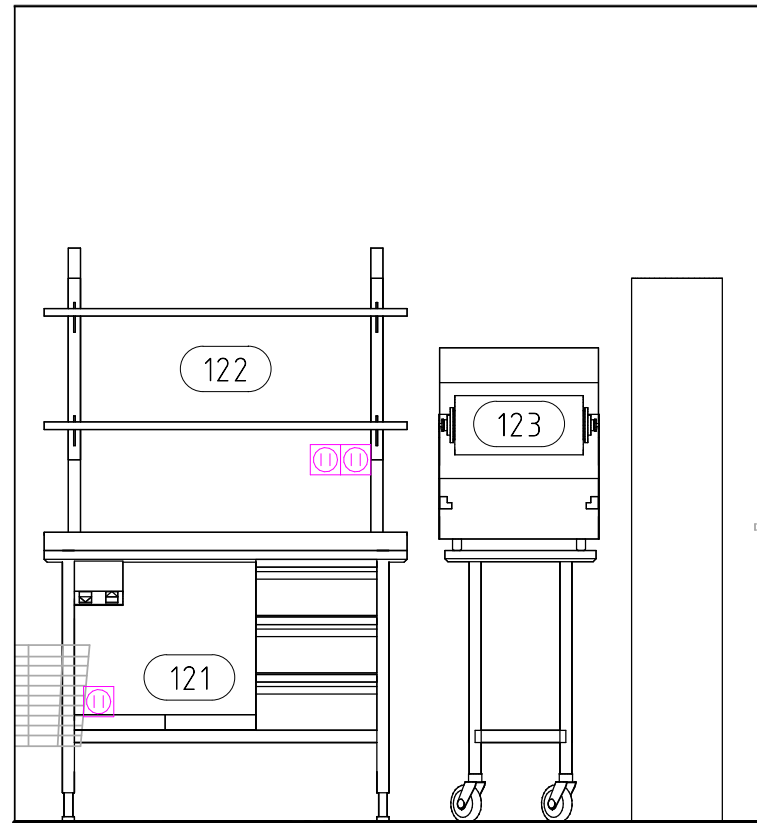


H

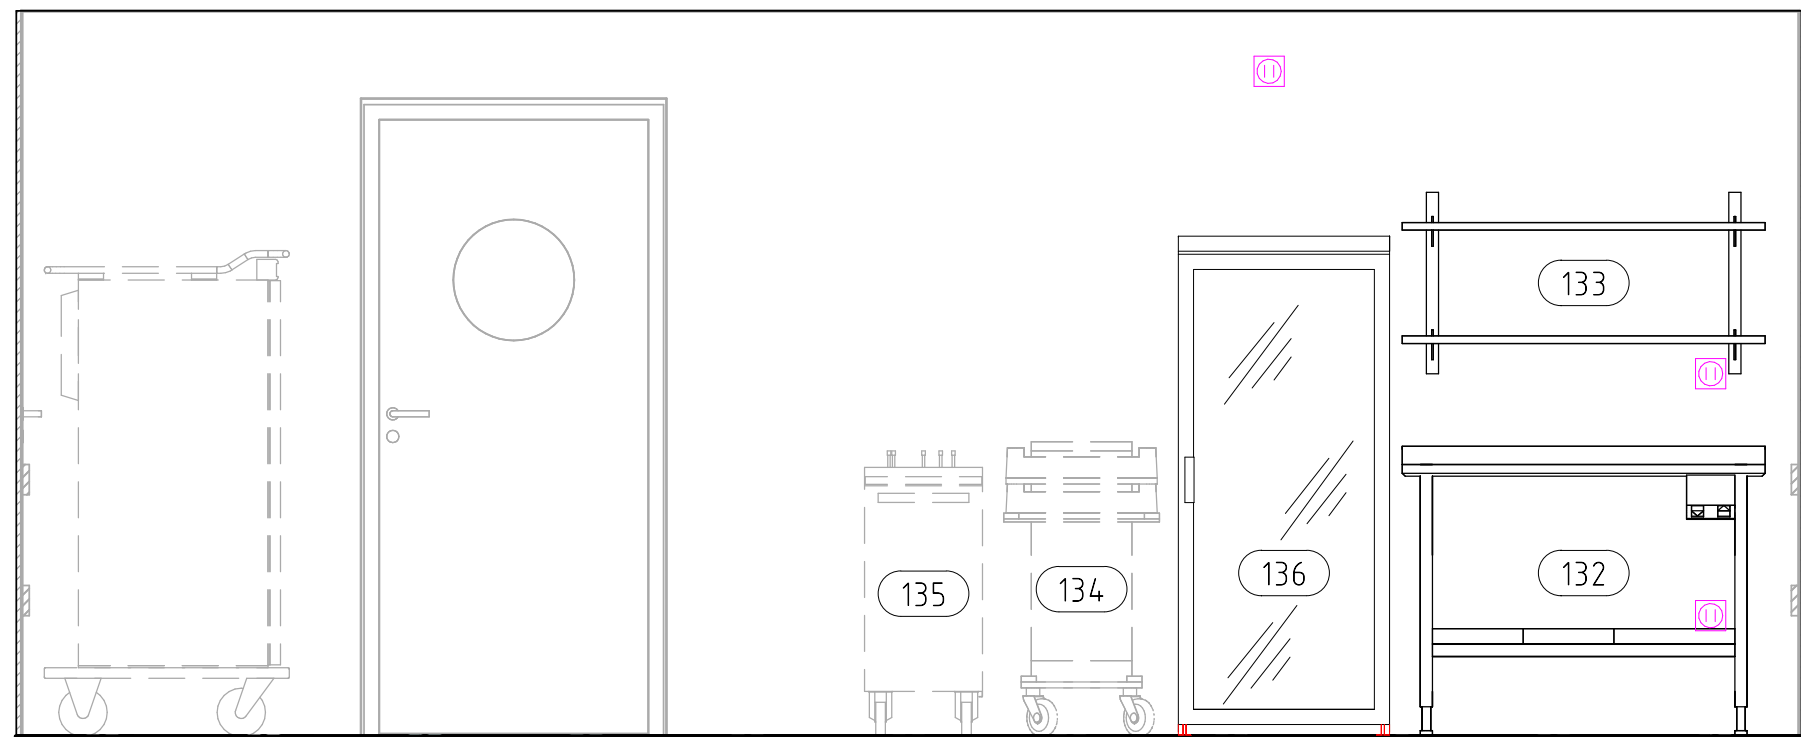



I

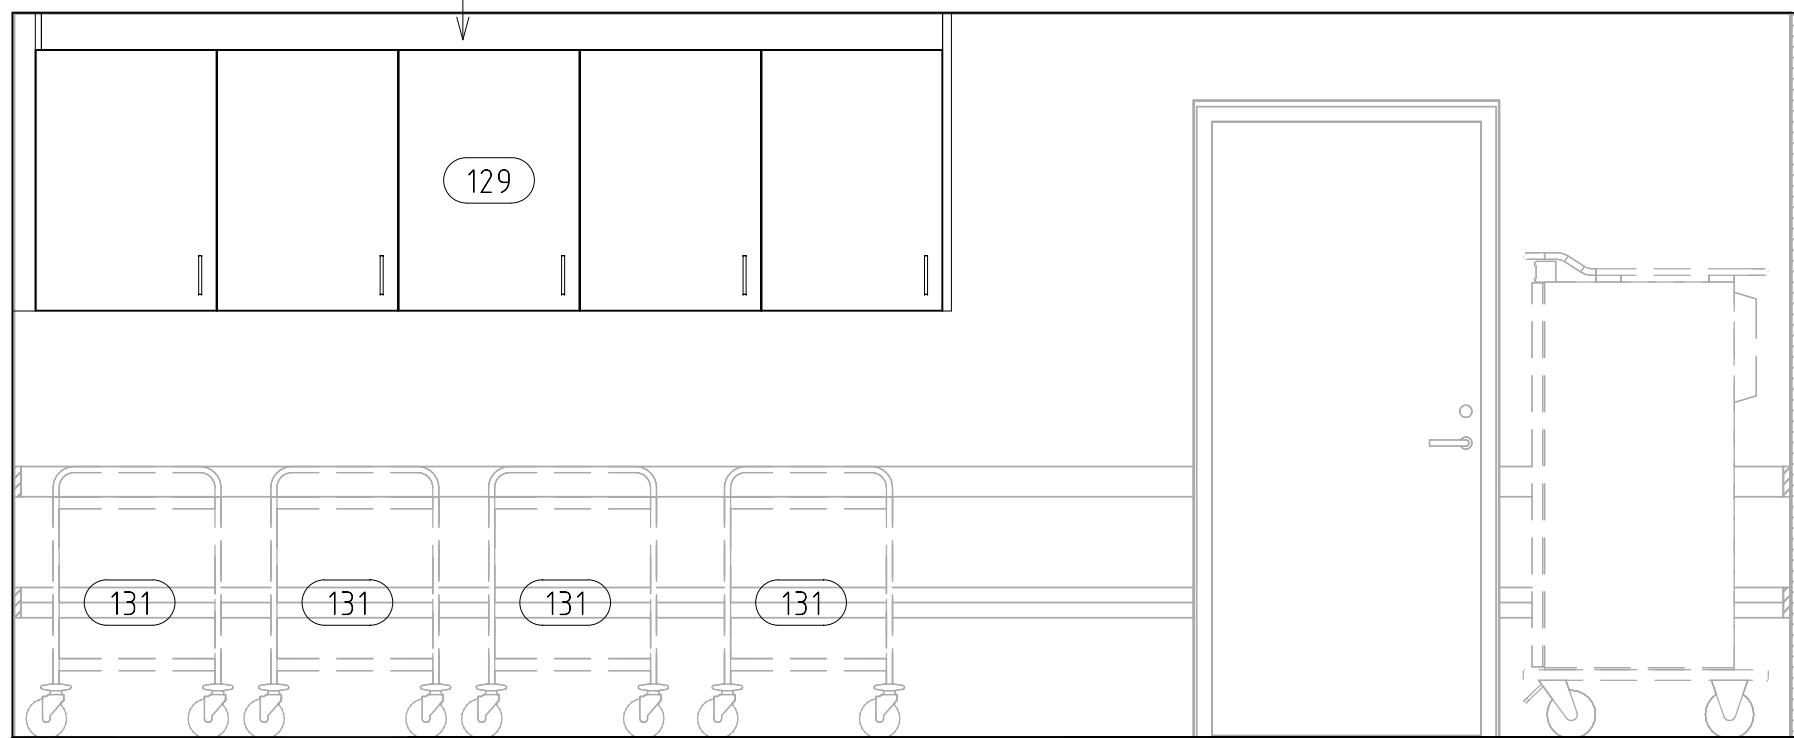

J

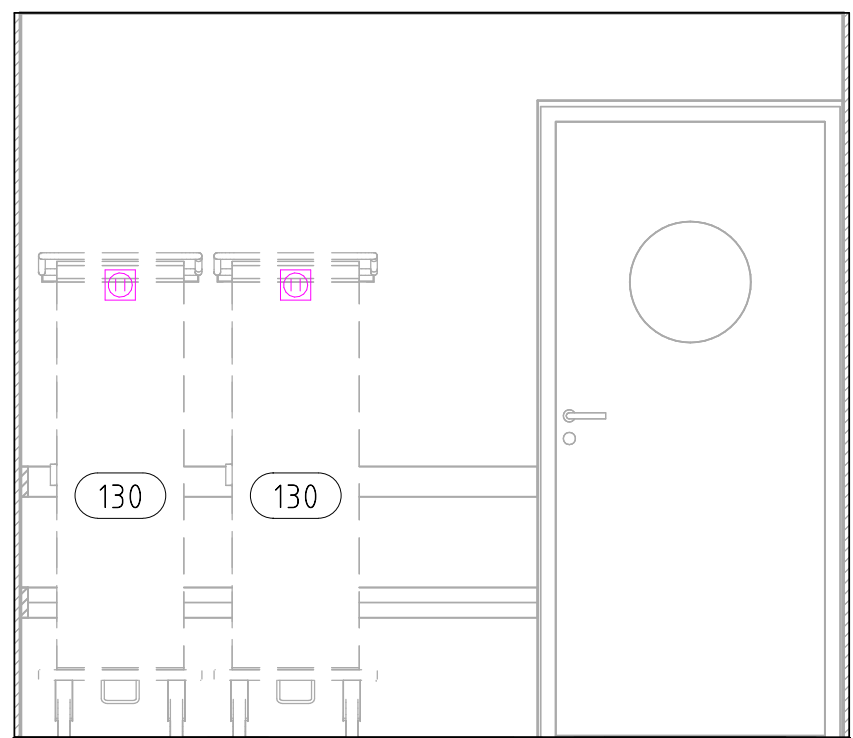

K

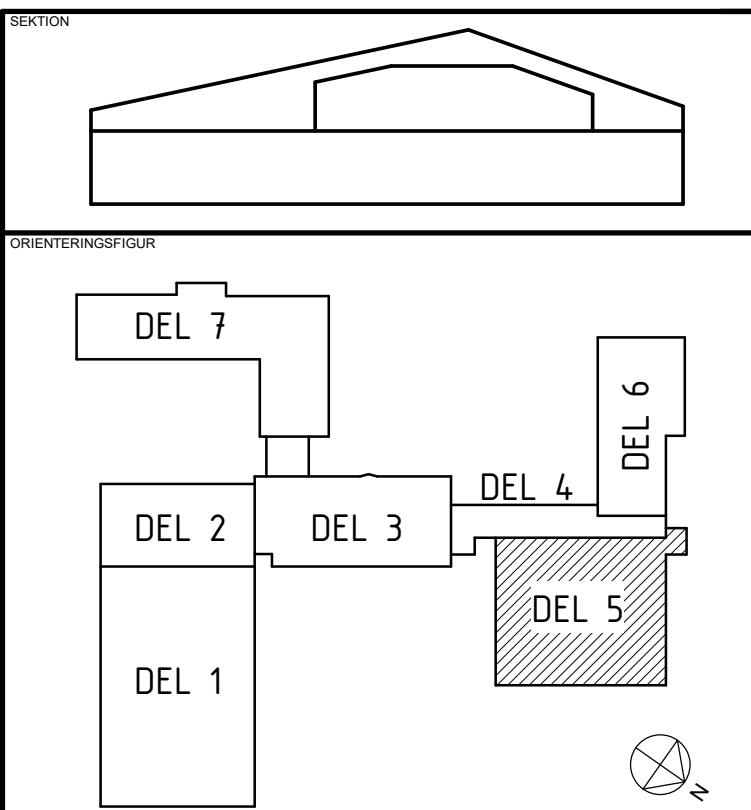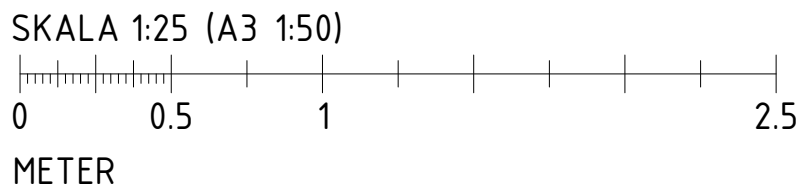

BERTTON		
ORIENTERINGSDIAGRAM		
DEL 7		
DEL 2	DEL 3	DEL 4
DEL 1		DEL 5
DEL 6		
STATUS		
FÖRFRÅGNINGSUNDERLAG		
HANDLING		
BYGGHANDLING		
DATUM	DISKAD AV	ÄNDRINGAR PM
2025-01-31	T. BERGSTRÖM	KFU01
BESTÄLLARE		
ROBERTSFORS KOMMUN		
PROJEKTNAMN		
CENTRALKÖK		
ORSADE		
ROBERTSFORS KOMMUN		
PROJEKTNUMMER	FASTIGHET	
	YTTRE RINGVÄGEN 4	
ÖVERLÄNNING	FORDONET 1	
DISCIPLIN	FÖRETAG	
SK	NORCONSULT SVERIGE AB	
UPPDRAGSNUMMER	SKAPAD AV	
108 83 71	ALG	
TELEFON	KONTAKTPERSON	
070-55 55 221	ANDREAS LAGERSKOG	
BYGGKONSTRUKTION	FÖLJESKED (PM 2006)	
VÄNINGSPLAN	DELOMRÅDE	
1	5	
SYSTEM		
46.4 UPPSTÄLLNINGAR		
SPECIFIKATION		
UPPSTÄLLNINGAR A-K		
RIKTNINGSKATEGORI	SKALA	FORMAT
		A1
DOCUMENTNUMMER	ÄNDRING	
SK-46-4-150	A	