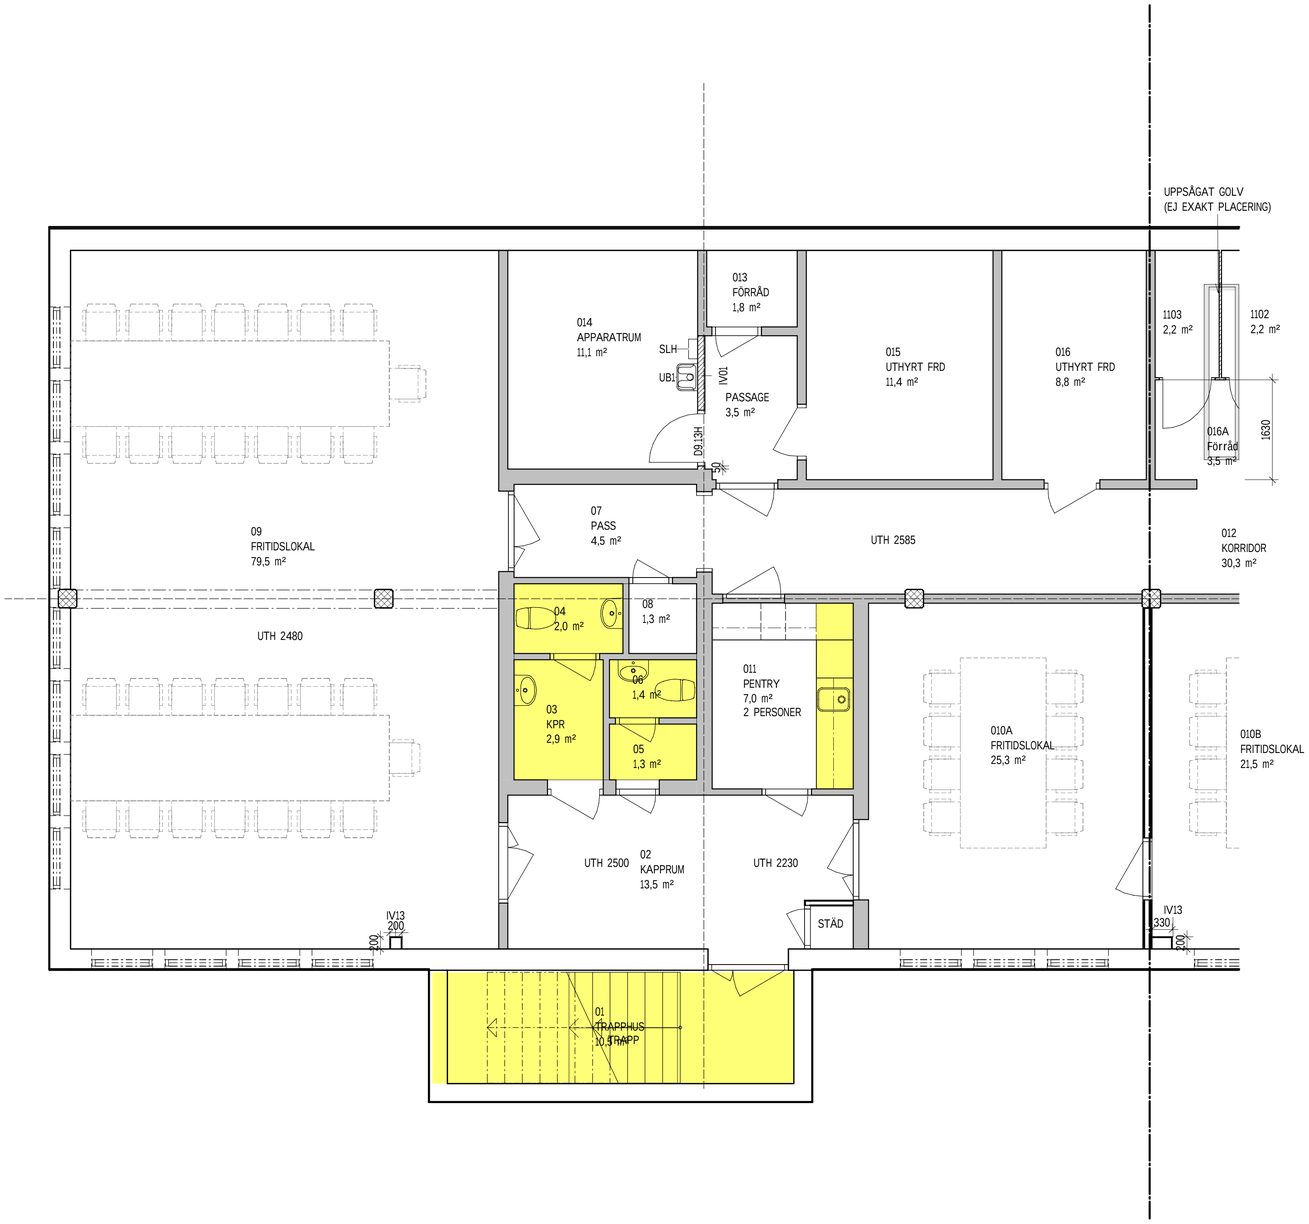

FÖRKLARINGAR

NYA BYGGDELAR

BEFINTLIGA BYGGDELAR

KONNEKTIONSLINJE

BRANDCELLSGRÄNSER:
EI15
E30
EI30
EI60

+ 12,34 PLUSHÖJD

FG + 1,000 PLUSHÖJD - FÄRDIGT GOLV

ASBEST/ETERNIT
SANERAS

LITTERA:
G GARDEROB
H HÖGSKÅP
L LINNESKÅP
ST STÄDSKÅP
K KYLSKÅP
F FRYS
KF KYL/FRYS
DM DISKMASKIN
KM KOMBIMASKIN
UB1 UTSLAGSBACK
SLH SLANGHÅLLARE
DRS DÖRRSTOPP .ANPASSAS MOT STÅENDE GOLVVENTILATION
AK ARMBÅGSKONTAKT ,KONTRASTMARKERAS

FÖRESKRIFTER

BRAND:
VÄGGAR SKA UTFÖRAS I BRANDKLASS EN1
BRANDSKYDDSBESKRIVNING OCH BRANDCELLSINDELNING PÅ BRANDSKYDDSRITNINGAR.
VID AVVIKELSER MELLAN A-RITNINGAR OCH BRANDSKYDDSRITNINGAR GÄLLER UTFÖRANDE ENLIGT BRANDSKYDDSRITNINGAR.

SKALA 1:50 0 1 2 5
METER

BET	ÄNDRING AVSER	DATUM	SIGN

STATUS: GRANSKNINGSHANDLING

HANDLING: BYGGHANDLING

DATUM: 2025-02-26

ÄNDRING:

PROJEKT:
CENTRUMHUSET HUS D
KRÅKAN 1, ROBERTSFORS

ANSVARIG PART:
AFRY
AFRY Ark Studio

KONTAKTPERSON	SKAPAD AV
J. Sjögren	L.Grubbström
GODKÄND AV	UPPDRAGSNUMMER
J. Sjögren	210550

RITNINGSKATEGORI:

INNEHÅLL	FORMAT
OMBYGGNAD BIBLIOTEK OCH LÄGENHETER	A1
PLAN 090 - DEL 1	SKALA 1:50
NUMMER A-40-1-D091	BET

Filen C:\Users\jmd534\OneDrive - AFRY\Documents\A-40-V-01_ludvig.grubbstrom.rvt