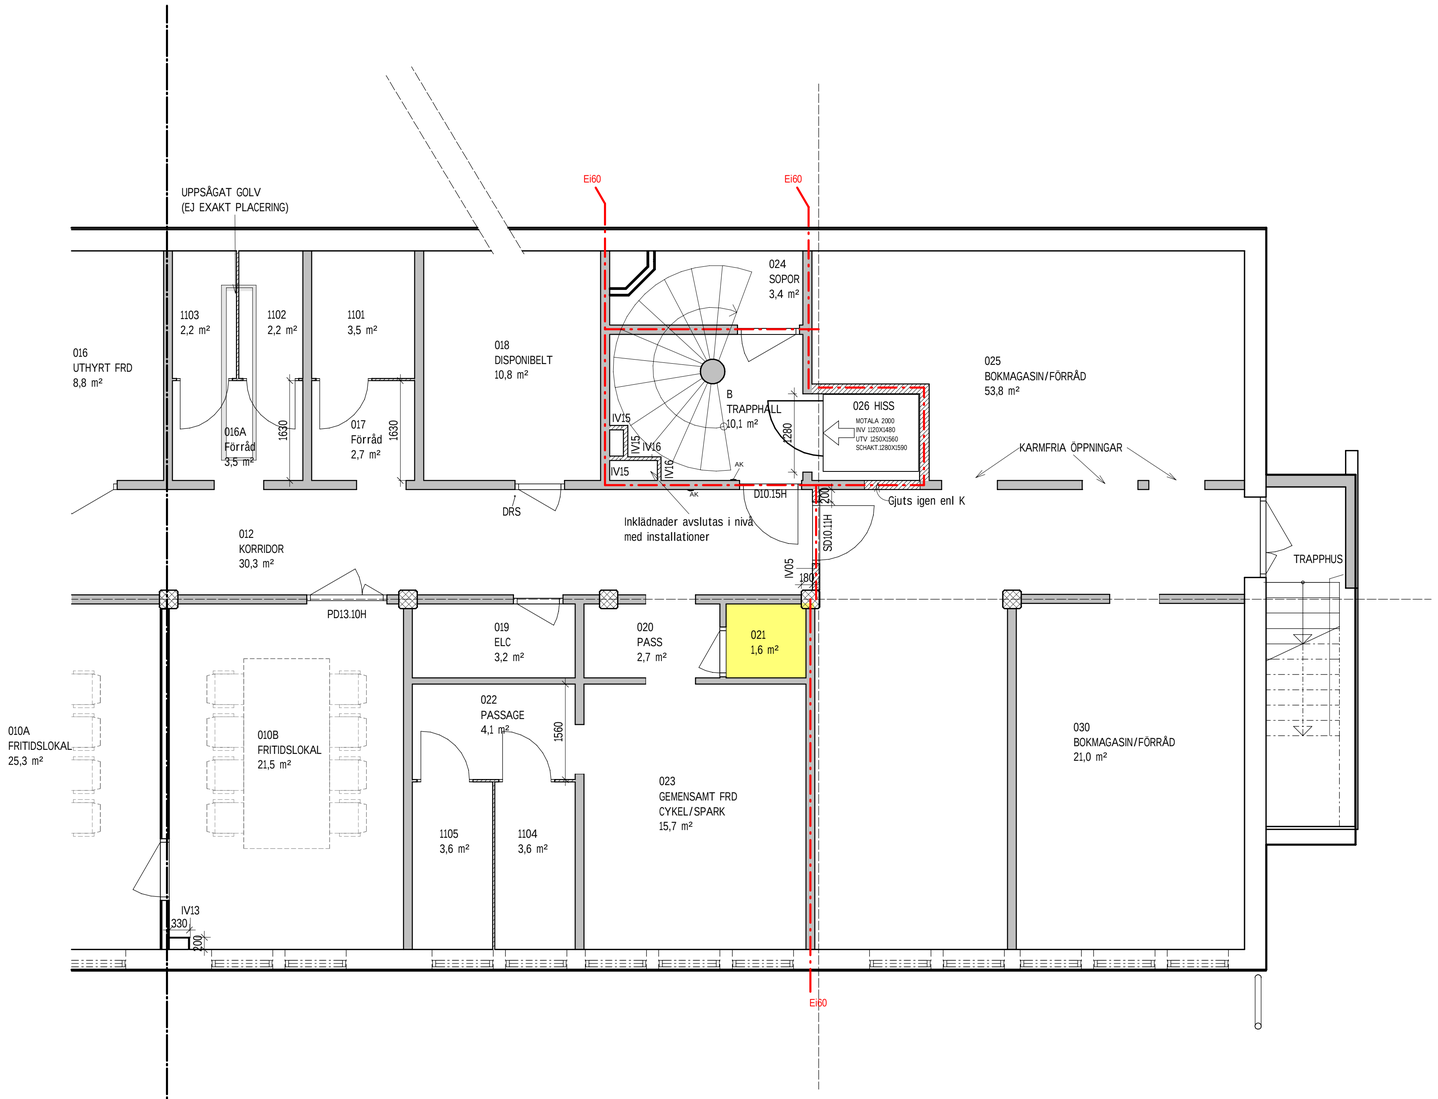


## FÖRKLARINGAR

NYA BYGGDELAR

BEFINTLIGA BYGGDELAR

KONNEKTIONSLINJE

BRANDCELLSGRÄNSER:
EI15
E30
EI30
EI60

+ 12,34 PLUSHÖJD

FG + 1,000 PLUSHÖJD - FÄRDIGT GOgolv

ASBEST/ETERNIT
SANERAS

LITTERA:

| | |
|---|---|
| G | GARDEROB |
| H | HÖGSKÅP |
| L | LINNESKÅP |
| ST | STÄDSKÅP |
| K | KYLSKÅP |
| F | FRYS |
| KF | KYL/FRYS |
| DM | DISKMASKIN |
| KM | KOMBIMASKIN |
| UB1 | UTSLAGSBACK |
| SLH | SLANGHÅLLARE |
| DRS | DÖRRSTOPP ,ANPASSAS MOT STÅENDE GOLVVENTILATION |
| AK | ARMBÅGSKONTAKT ,KONTRASTMARKERAS |

## FÖRESKRIFTER

BRAND:
VÄGGAR SKA UTFÖRAS I BRANDKLASS ENL
BRANDSKYDDSBESKRIVNING OCH BRANDCELLSINDELNING PÅ
BRANDSKYDDSRITNINGAR:
VID AVVIKELSER MELLAN A-RITNINGAR OCH
BRANDSKYDDSRITNINGAR GÄLLER
UTFÖRANDE ENLIGT BRANDSKYDDSRITNINGAR.

SKALA 1:50 0 1 2 5
METER

| BET | ÄNDRING AVSER | DATUM | SIGN |
|---|---|---|---|

STATUS: GRANSKNINGSHANDLING
HANDLING: BYGGHANDLING
DATUM: 2025-02-26
ÄNDRING:
PROJEKT: CENTRUMHUSET HUS D
KRÅKAN 1, ROBERTSFORS
ANSVARIG PART: AFRY / AFRY Ark Studio

| | |
|---|---|
| KONTAKTPERSON: J. Sjögren | SKAPAD AV: L.Grubbström |
| GODKÄND AV: J. Sjögren | UPPDRAGSNUMMER: 210550 |
| RITNINGSKATEGORI: | |
| INNEHÅLL: OMBYGGNAD BIBLIOTEK OCH LÄGENHETER<br>PLAN 090 - DEL 2 | FORMAT: A1<br>SKALA: 1:50 |
| NUMMER: A-40-1-D092 | BET |

Filen C:\Users\jmd5341\OneDrive - AFRY\Documents\A-40-V-01_ludvig.grubbstrom.rvt