
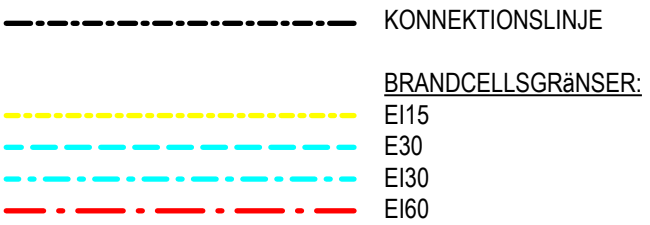


FÖRKLARINGAR

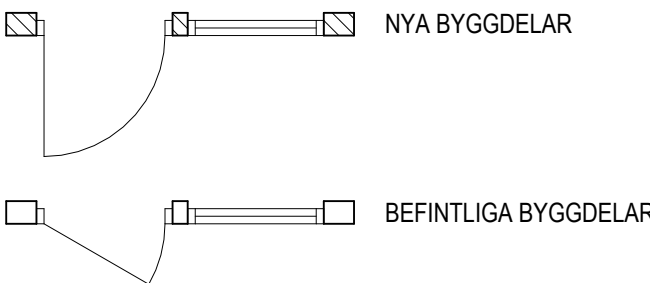


+ 12,34 PLUSHÖJD
FG + 1,000 PLUSHÖJD - Färdigt golv


- LITTERA:**
G GÅRDEROB
H HÖGSKÅP
L LINNESKÅP
ST STÅDSKÅP
K KYLSKÅP
F FRYSS
K/F KYLFRYS
DM DISKMASKIN
KM KOMBIMASKIN
AK ARMBÄGSKONTAKT
UB1 UTSLAGSBACK ENL VS
SLH SLANGHÅLLARE ENL VS

FÖRESKRIFTER

BRAND:
VÄGGAR SKA UTFÖRAS I BRANDKLASS ENL BRANDSKYDDSBESKRIVNING OCH BRANDCELLSINDELNING PÅ BRANDSKYDDSRITNINGAR.
VID AVVIKELSER MELLAN A-RITNINGAR OCH BRANDSKYDDSRITNINGAR GÄLLER UTFÖRANDE ENLIGT BRANDSKYDDSRITNINGAR.

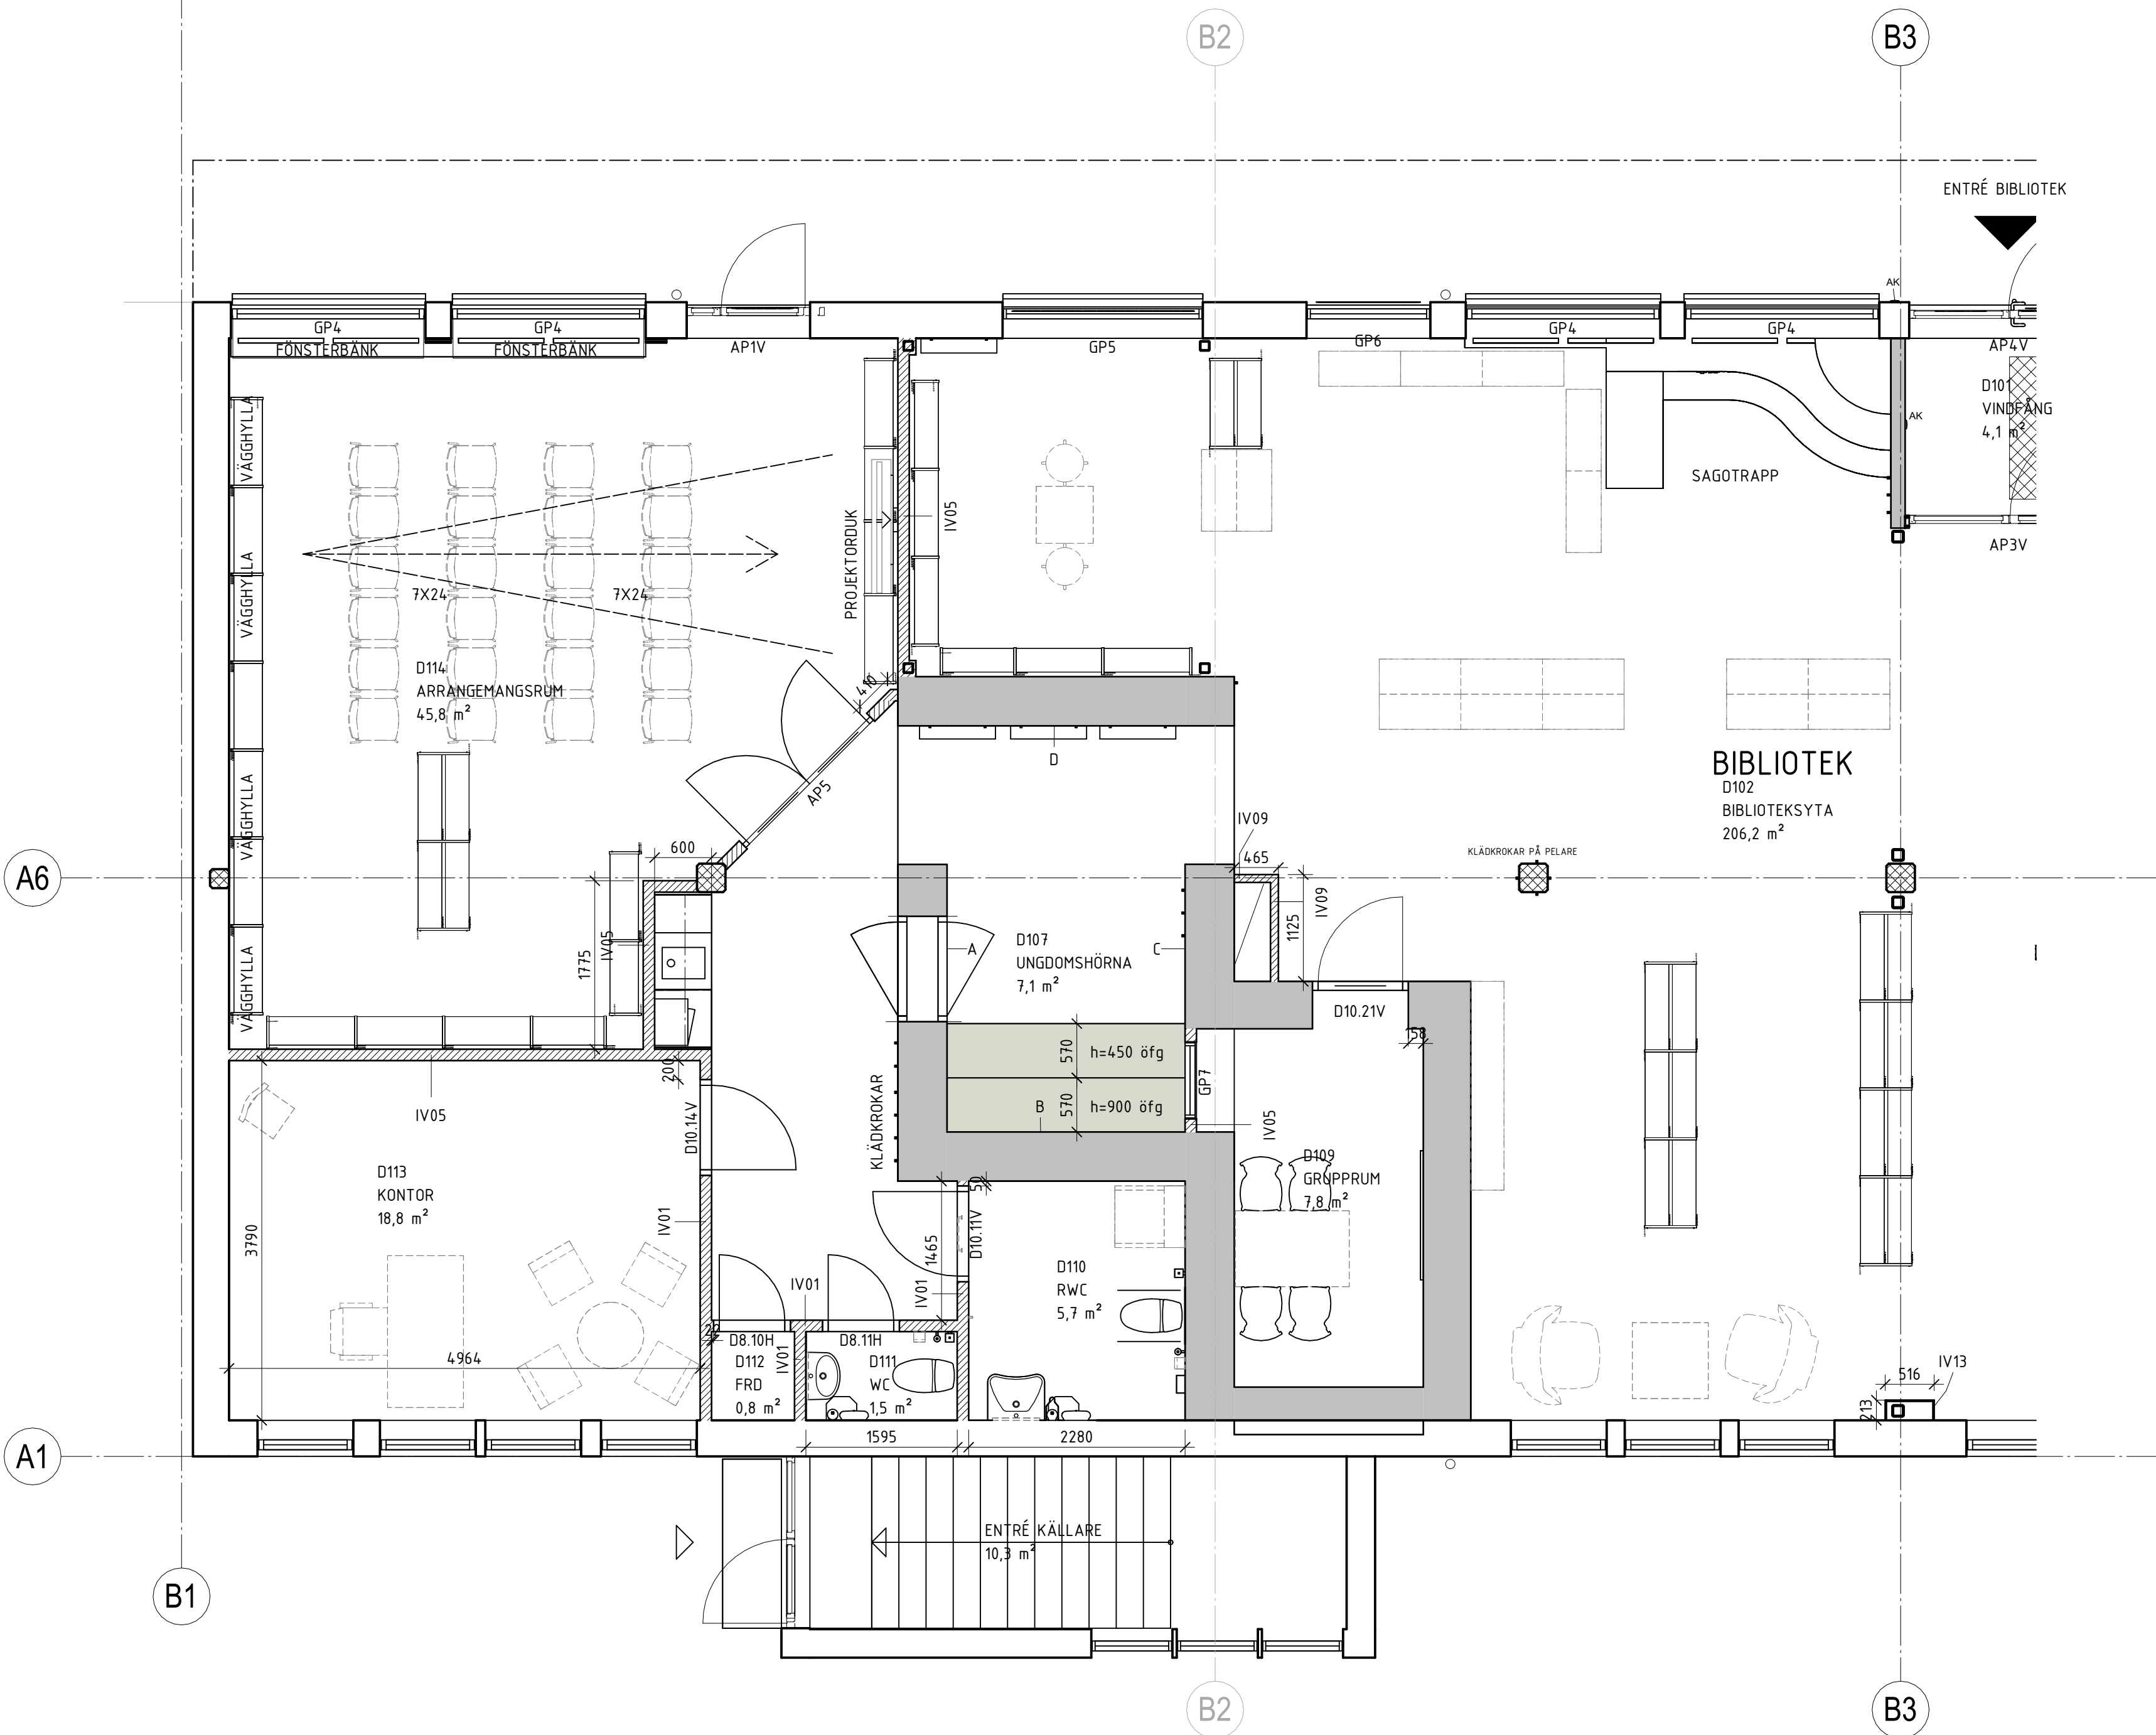

SKALA 1:50
0 1 2 5
METER

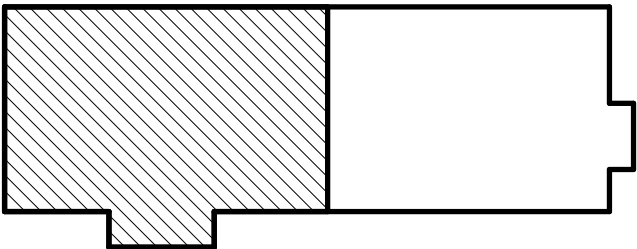

BET	ÄNDRING AVSER		DATUM	SIGN	STATUS
GRANSKNINGSHANDLING					
BYGGHANDLING					
2025-02-26		ANDRING			
CENTRUMHUSET HUS D					
KRÅKAN 1, ROBERTSFORS					
ANSVARIG PART					
AFRY Ark Studio					
 AFRY		AFRY Ark Studio			
J. Sjögren	KONTAKTPERSON	L.Grubbström		SKAPAD AV	
J. Sjögren	GODKÄND AV	210550		UPPERAENUMMER	
				RITNINGSKATEGORI	
OMBYGGNAD BIBLIOTEK OCH LÄGENHETER				INNEHÅLL	FORMAT
PLAN 100 - DEL 1				A1	SKALA
A-40-1-D101				1:50	BET