
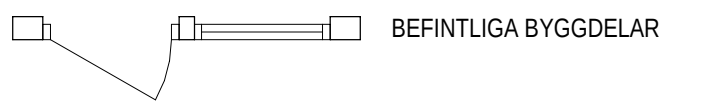


FÖRKLARINGAR

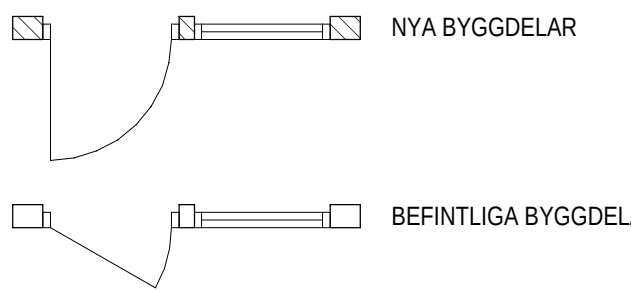

----- KONNEKTIONS LINJE

BRANDCELLSGRÄNSER:

-----	E15
-----	E30
-----	E130
-----	E160

+ 12,34 PLUSHÖJD


FG + 1,000 PLUSHÖJD - FÄRDIGT GOLV

LITTERA:

G GARDEROB
H HÖGSKÅP
L LINNESKÅP
ST STÅDSKÅP
K KYLSKÅP
F FRY
K/F KYL/FRYS
DM DISKMASKIN
KM KOMBIMASKIN
AK ARMBÅGSKONTAKT
UB1 UTSLAGSBACK ENL VS
SLH SLANGHÅLLARE ENL VS

FÖRESKRIFTER

BRAND:
VÄGGAR SKA UTFÖRAS I BRANDKASS ENL
BRANDSKYDDSBESKRIVNING OCH BRANDCELLSINDELNING PÅ
BRANDSKYDDSRITNINGAR.
VID AVVIKELSER MELLAN A-RITNINGAR OCH
BRANDSKYDDSRITNINGAR GÄLLER
UTFÖRANDE ENLIGT BRANDSKYDDSRITNINGAR.

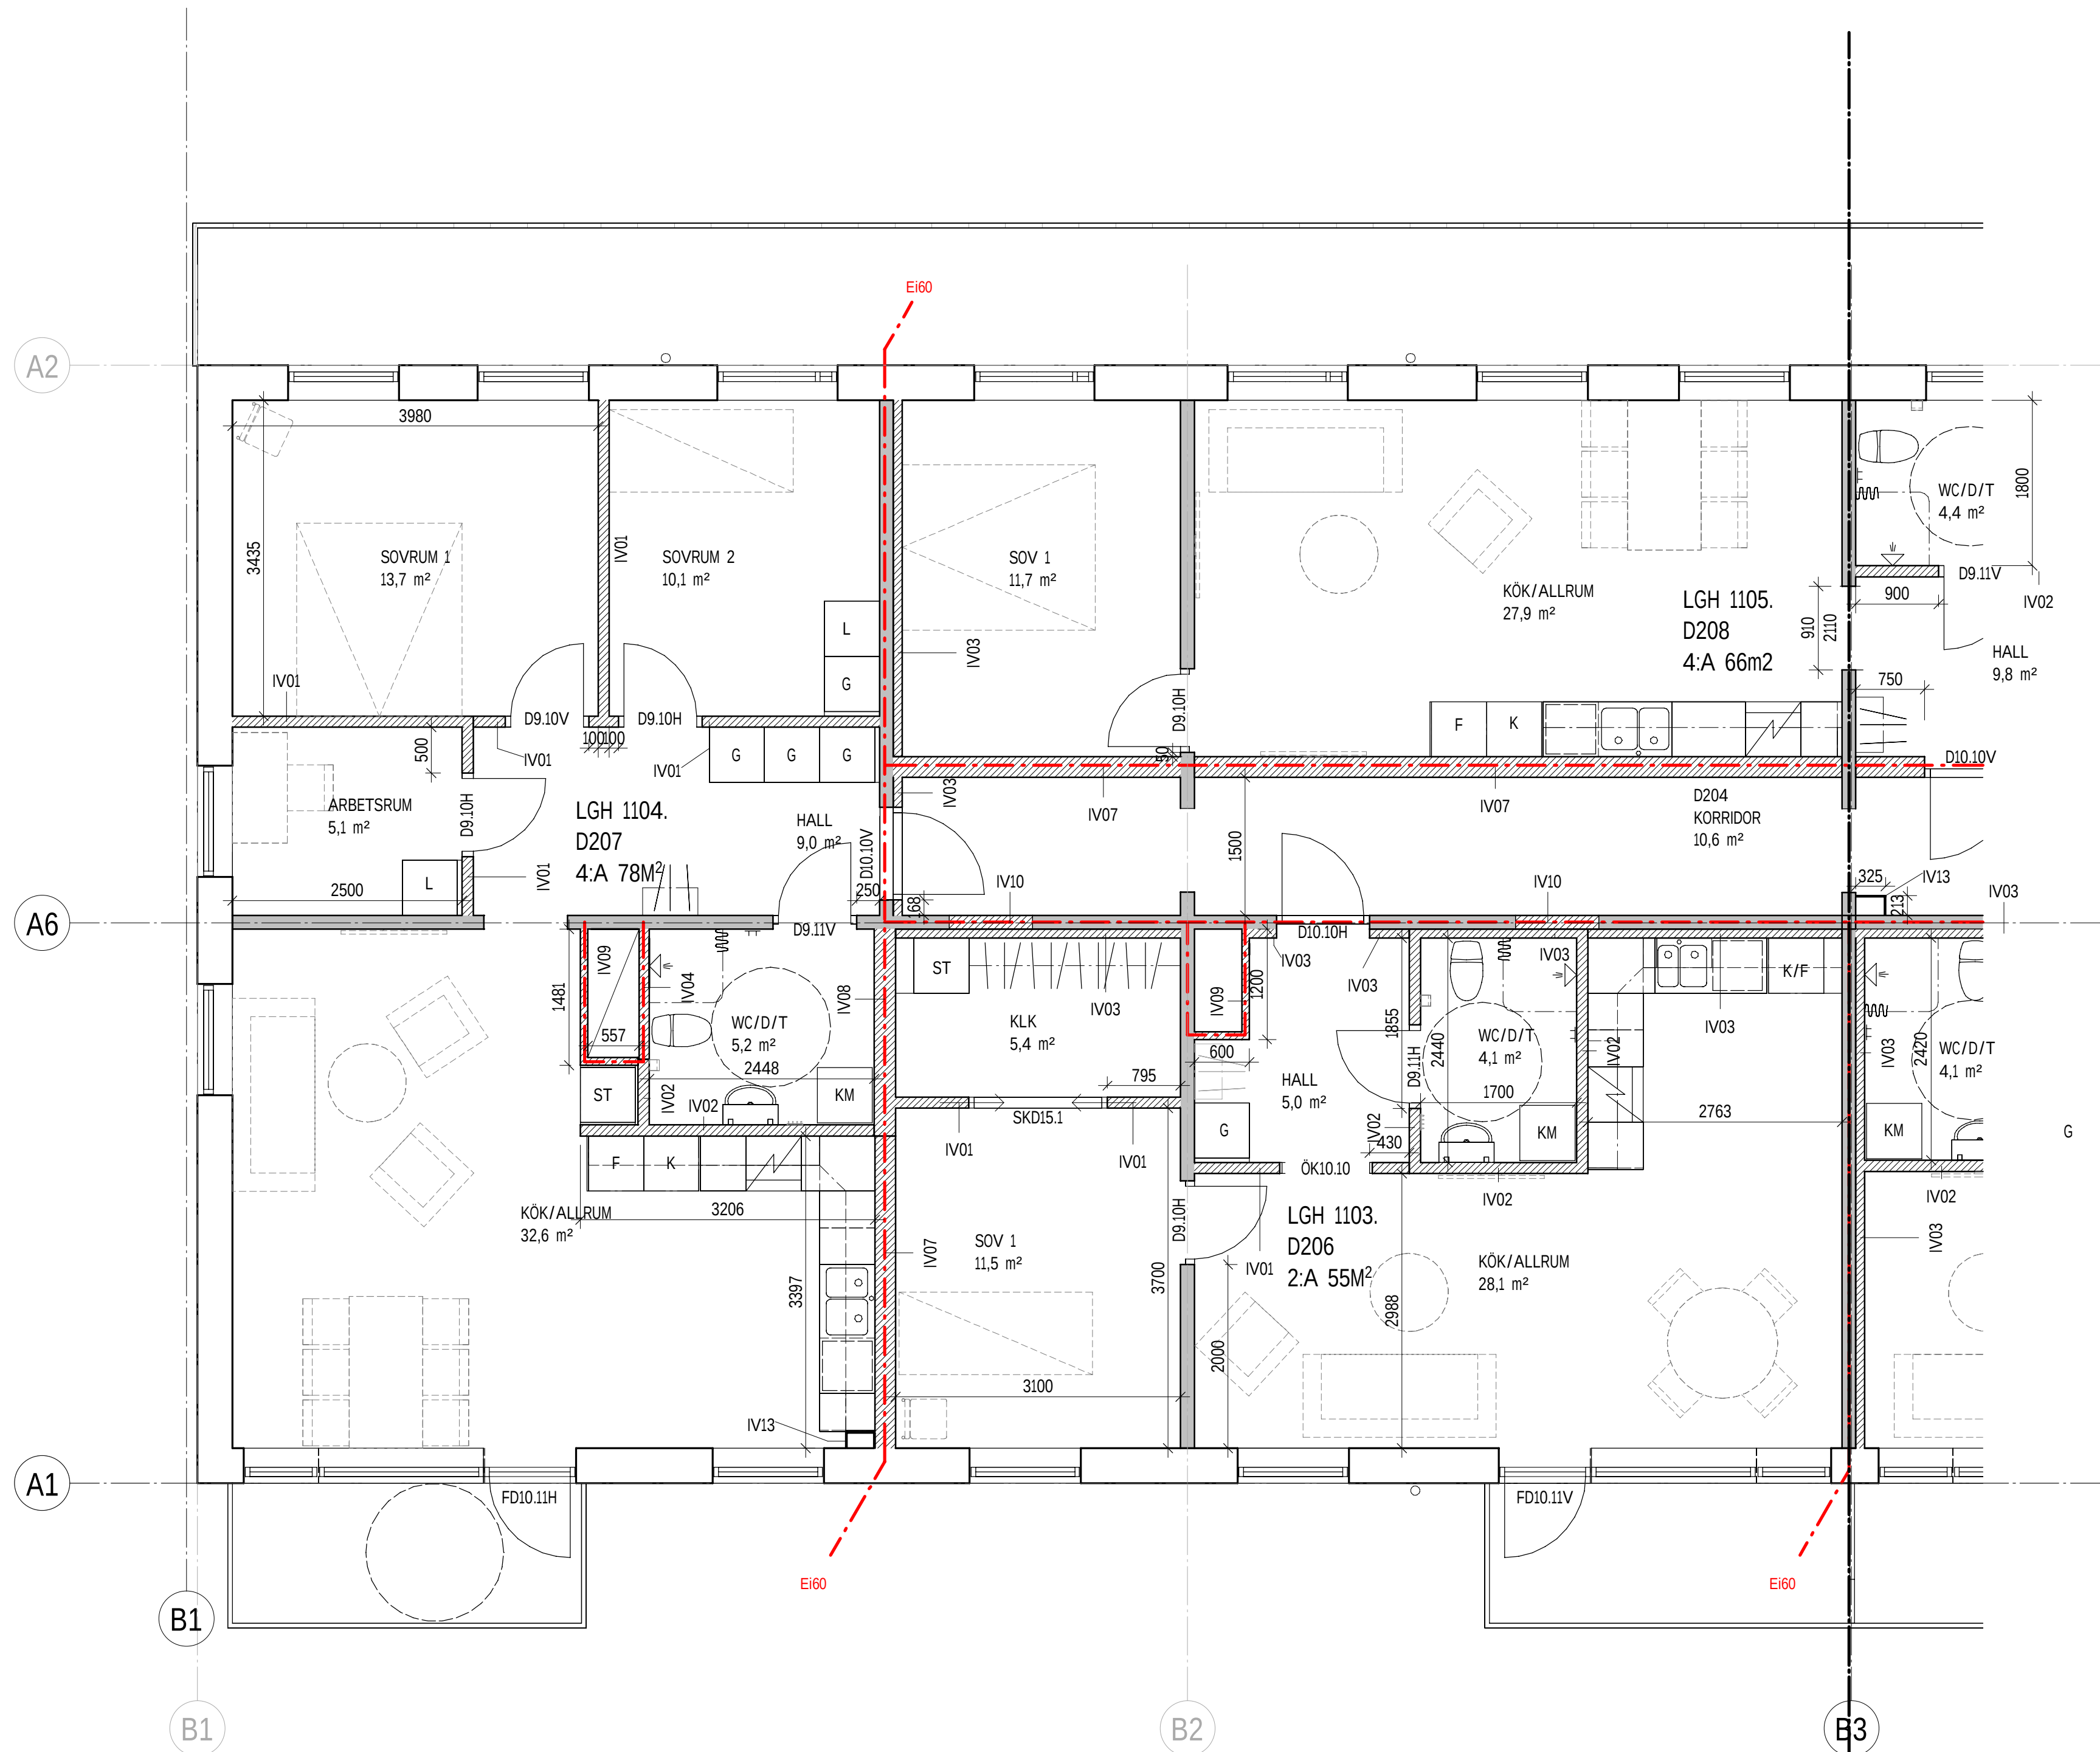

SET	ANDRING AVSER	DATUM	SIGN	STATUS
GRANSKNINGSHANDLING				HANDLING
BYGGHANDLING				ANDRING
2025-02-26		PROJEKT		
CENTRUMHUSET HUS D KRÅKAN 1, ROBERTSFORS				
ANSVARIG PART				
 AFRY		AFRY Ark Studio		
J. Sjögren	KONTAKTPERSON	L.Grubbström	SKAPAD AV	
J. Sjögren	GÖKÄND AV	210650	UPPDRAGNUMMER	
RITNINGSKATEGORI				
OMBYGGNAD BIBLIOTEK OCH LÄGENHETER		INNEHÅLL	A1	FORMAT
PLAN 200 - DEL 1			1:50	SKALA
A-40-1-D201		NUMMER		BET