


FÖRKLARINGAR

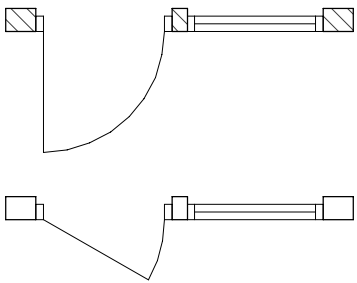

- KONNEKTIONSLINJE
- BRANDCELLSGRÄNSER:
- EI15
 - E30
 - EI30
 - EI60

+ 12,34 PLUSHÖJD

FG + 1,000 PLUSHÖJD - FÄRDIGT GOLV



- LITTERA:
- G GÄRDEROB
 - H HÖGSKÅP
 - L LINNESKÅP
 - ST STÄDSKÅP
 - K KYLSKÅP
 - F FRY
 - K/F KYL/FRY
 - DM DISKMASKIN
 - KM KOMBIMASKIN
 - AK ARMBÄGSKONTAKT
 - UB1 UTSLAGSBÄCK ENL VS
 - SLH SLANGHÅLLARE ENL VS

FÖRESKRIFTER

BRAND:

VÄGGAR SKA UTFÖRAS I BRANDKLASS ENL BRANDSKYDDSBESKRIVNING OCH BRANDCELLSINDELNING PÅ BRANDSKYDDSRITNINGAR.

VID AVVIKELSER MELLAN A-RITNINGAR OCH BRANDSKYDDSRITNINGAR GÄLLER UTFÖRANDE ENLIGT BRANDSKYDDSRITNINGAR.

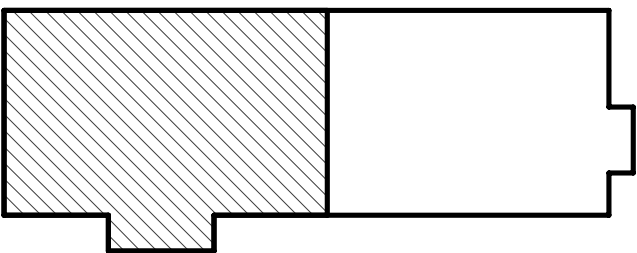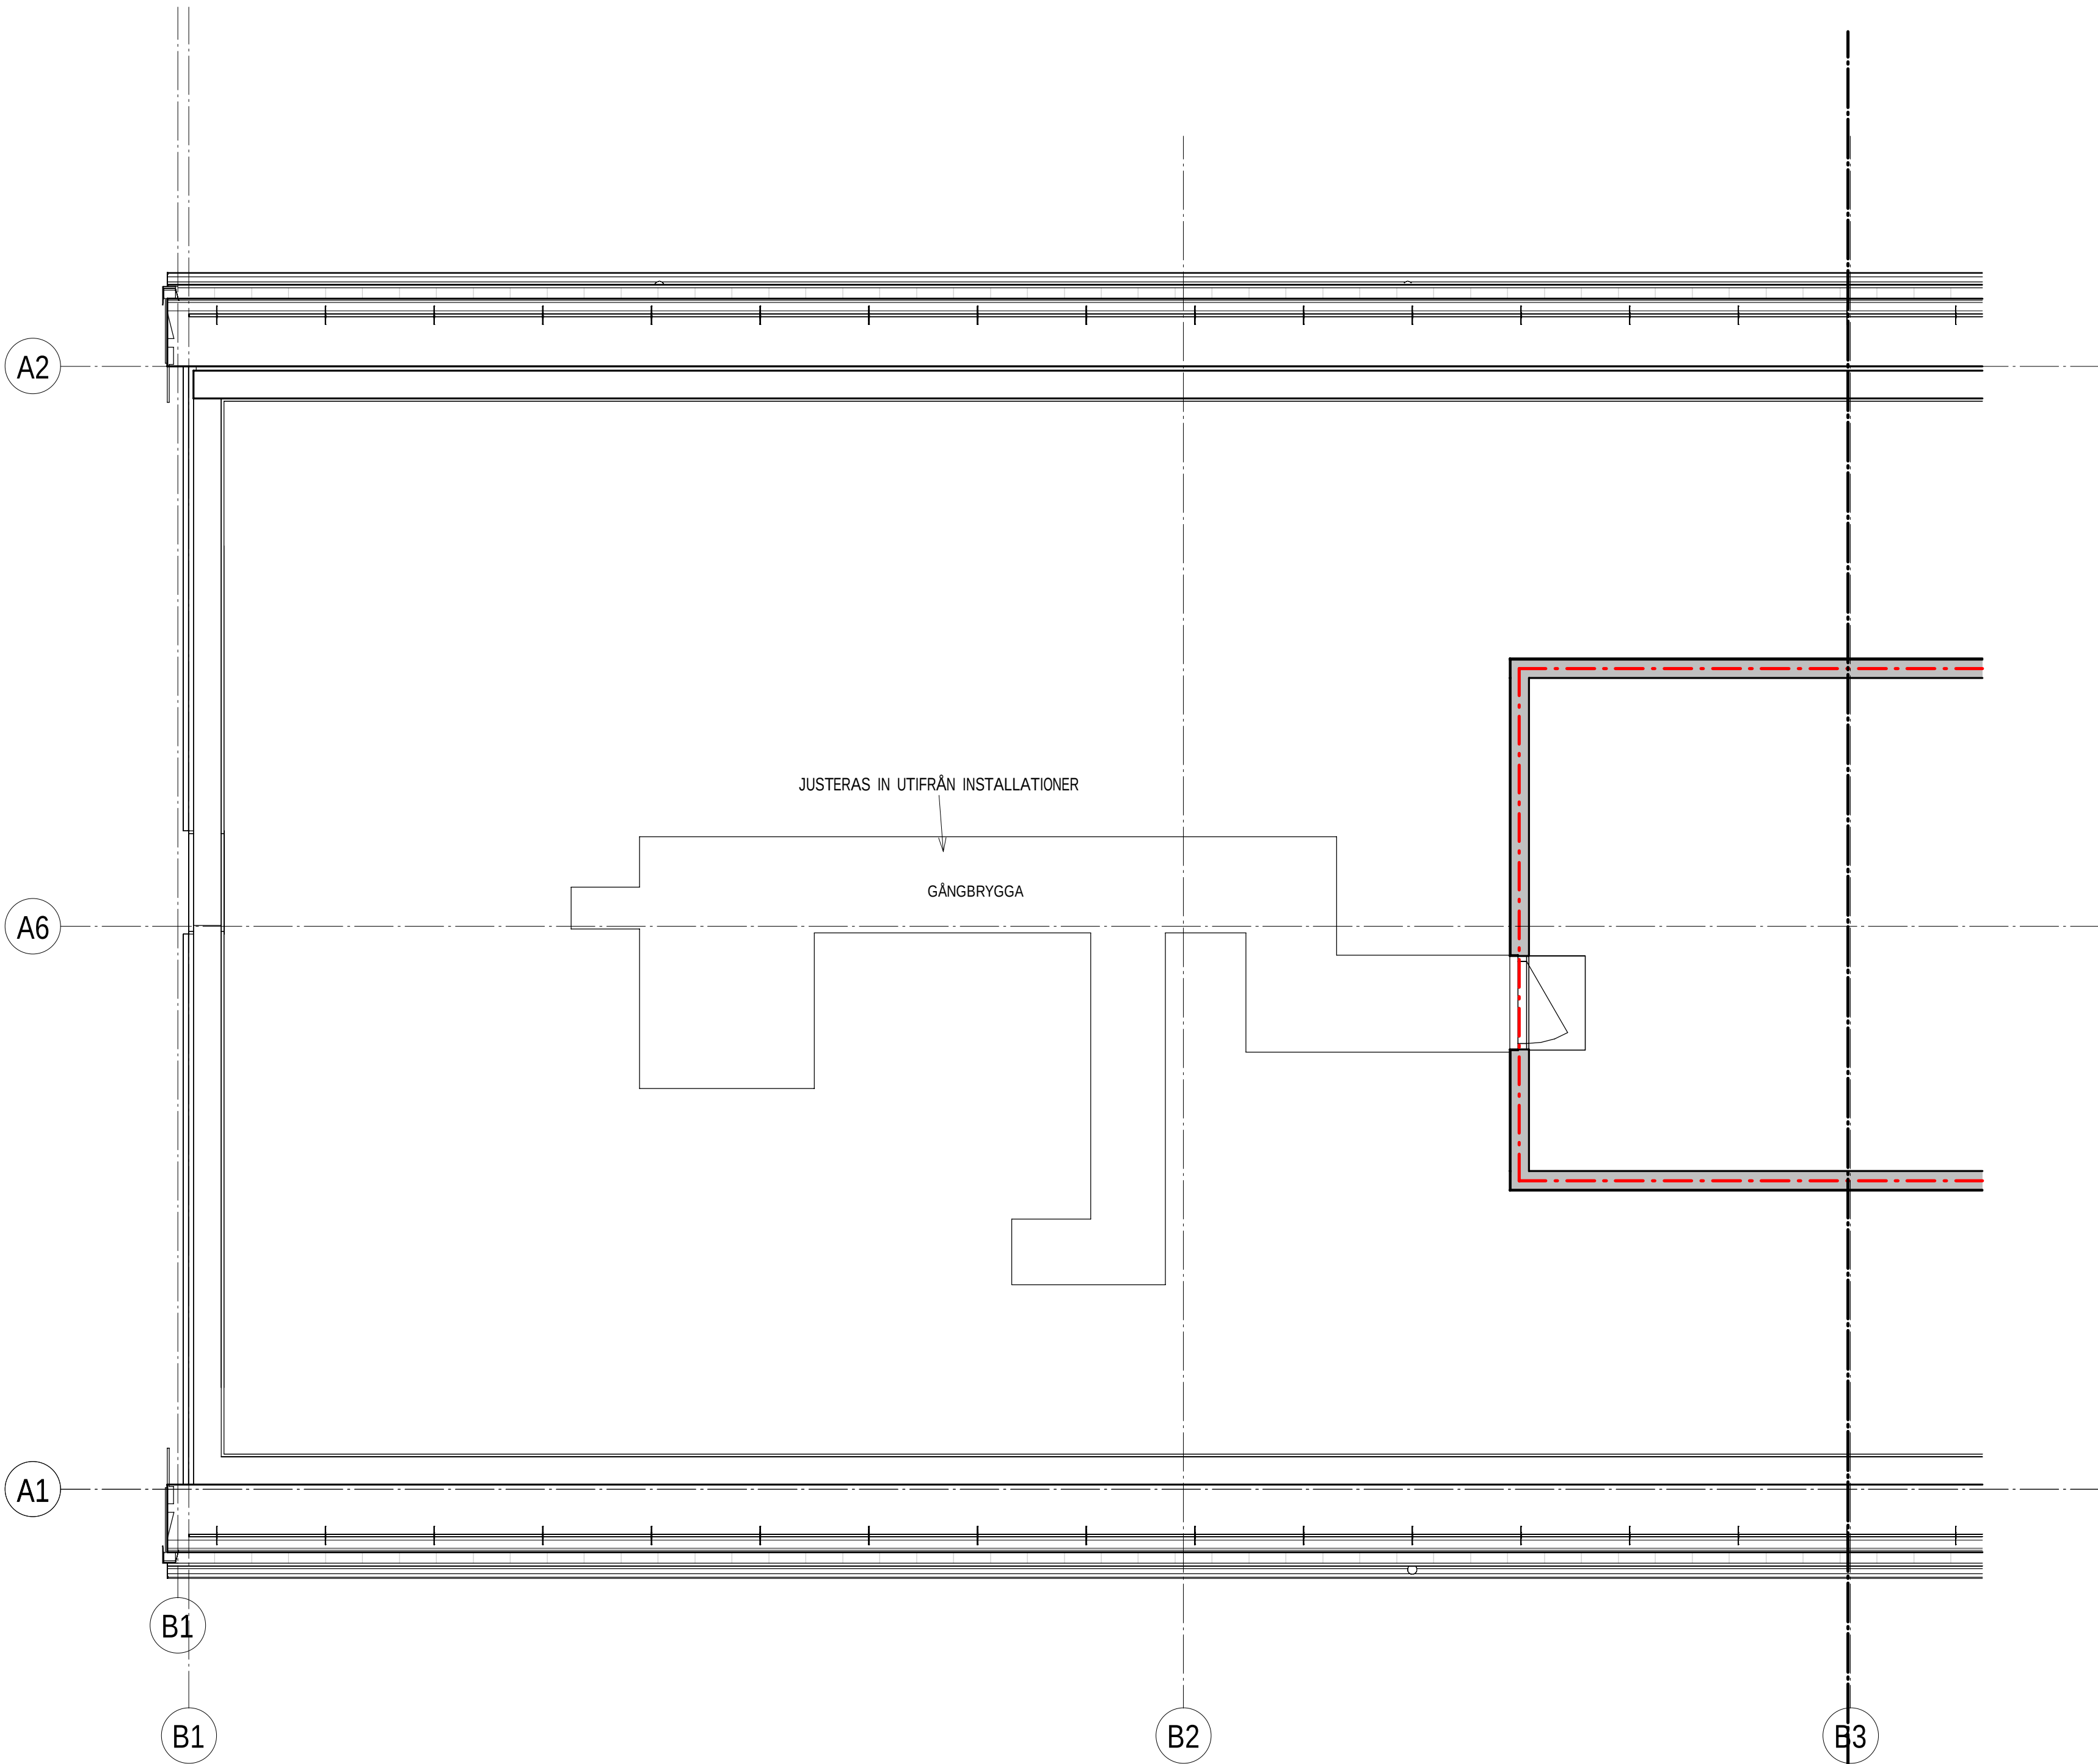

SKALA 1:50

0 1 2 5

METER

BET		ÄNDRING AVSER		DATUM		SIGN		STATUS	
GRANSKNINGSHANDLING									
BYGGHANDLING									
2025-02-26									
CENTRUMHUSET HUS D									
KRÅKAN 1, ROBERTSFORS									
ANSVARIG PART									
AFRY Ark Studio									
J. Sjögren		KONTAKTPERSON		L.Grubbström		SKAPAD AV			
J. Sjögren		GODKÄND AV		210550		UPPERAGSNUMMER			
RITNINGSKATEGORI									
OMBYGGNAD BIBLIOTEK OCH LÄGENHETER						INNEHÅLL		A1	
PLAN 300 - DEL 1						1:50		SKALA	
A-40-1-D301						NUMER		BET	