
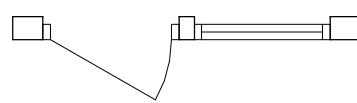


FÖRKLARINGAR

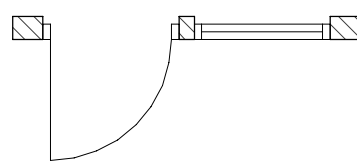

----- KONNEKTIONSLINJE

BRANDCELLSGRÄNSER:

	E115
	E30
	E130
	E160

+ 12,34 PLUSHÖJD


FG + 1,000 PLUSHÖJD - FÄRDIGT GOLV

LITTERA:

G	GARDEROB
H	HÖGSKÅP
L	LINNESKÅP
ST	STÅDSKÅP
K	KYLSKÅP
F	FRYS
K/F	KYL/FRYS
DM	DISKMASKIN
KM	KOMBIMASKIN
AK	ARMBÅGSKONTAKT
UB1	UTSLAGSBACKEN ENL VS
SLH	SLANGHÅLLARE ENL VS

FÖRESKRIFTER

BRAND:
VÄGGAR SKA UTFÖRAS I BRANDKASS ENL
BRANDSKYDDSBESKRIVNING OCH BRANDCELLSINDELNING PÅ
BRANDSKYDDSRITNINGAR.
VID AVVIKELSER MELLAN A-RITNINGAR OCH
BRANDSKYDDSRITNINGAR GÄLLER
UTFÖRANDE ENLIGT BRANDSKYDDSRITNINGAR.

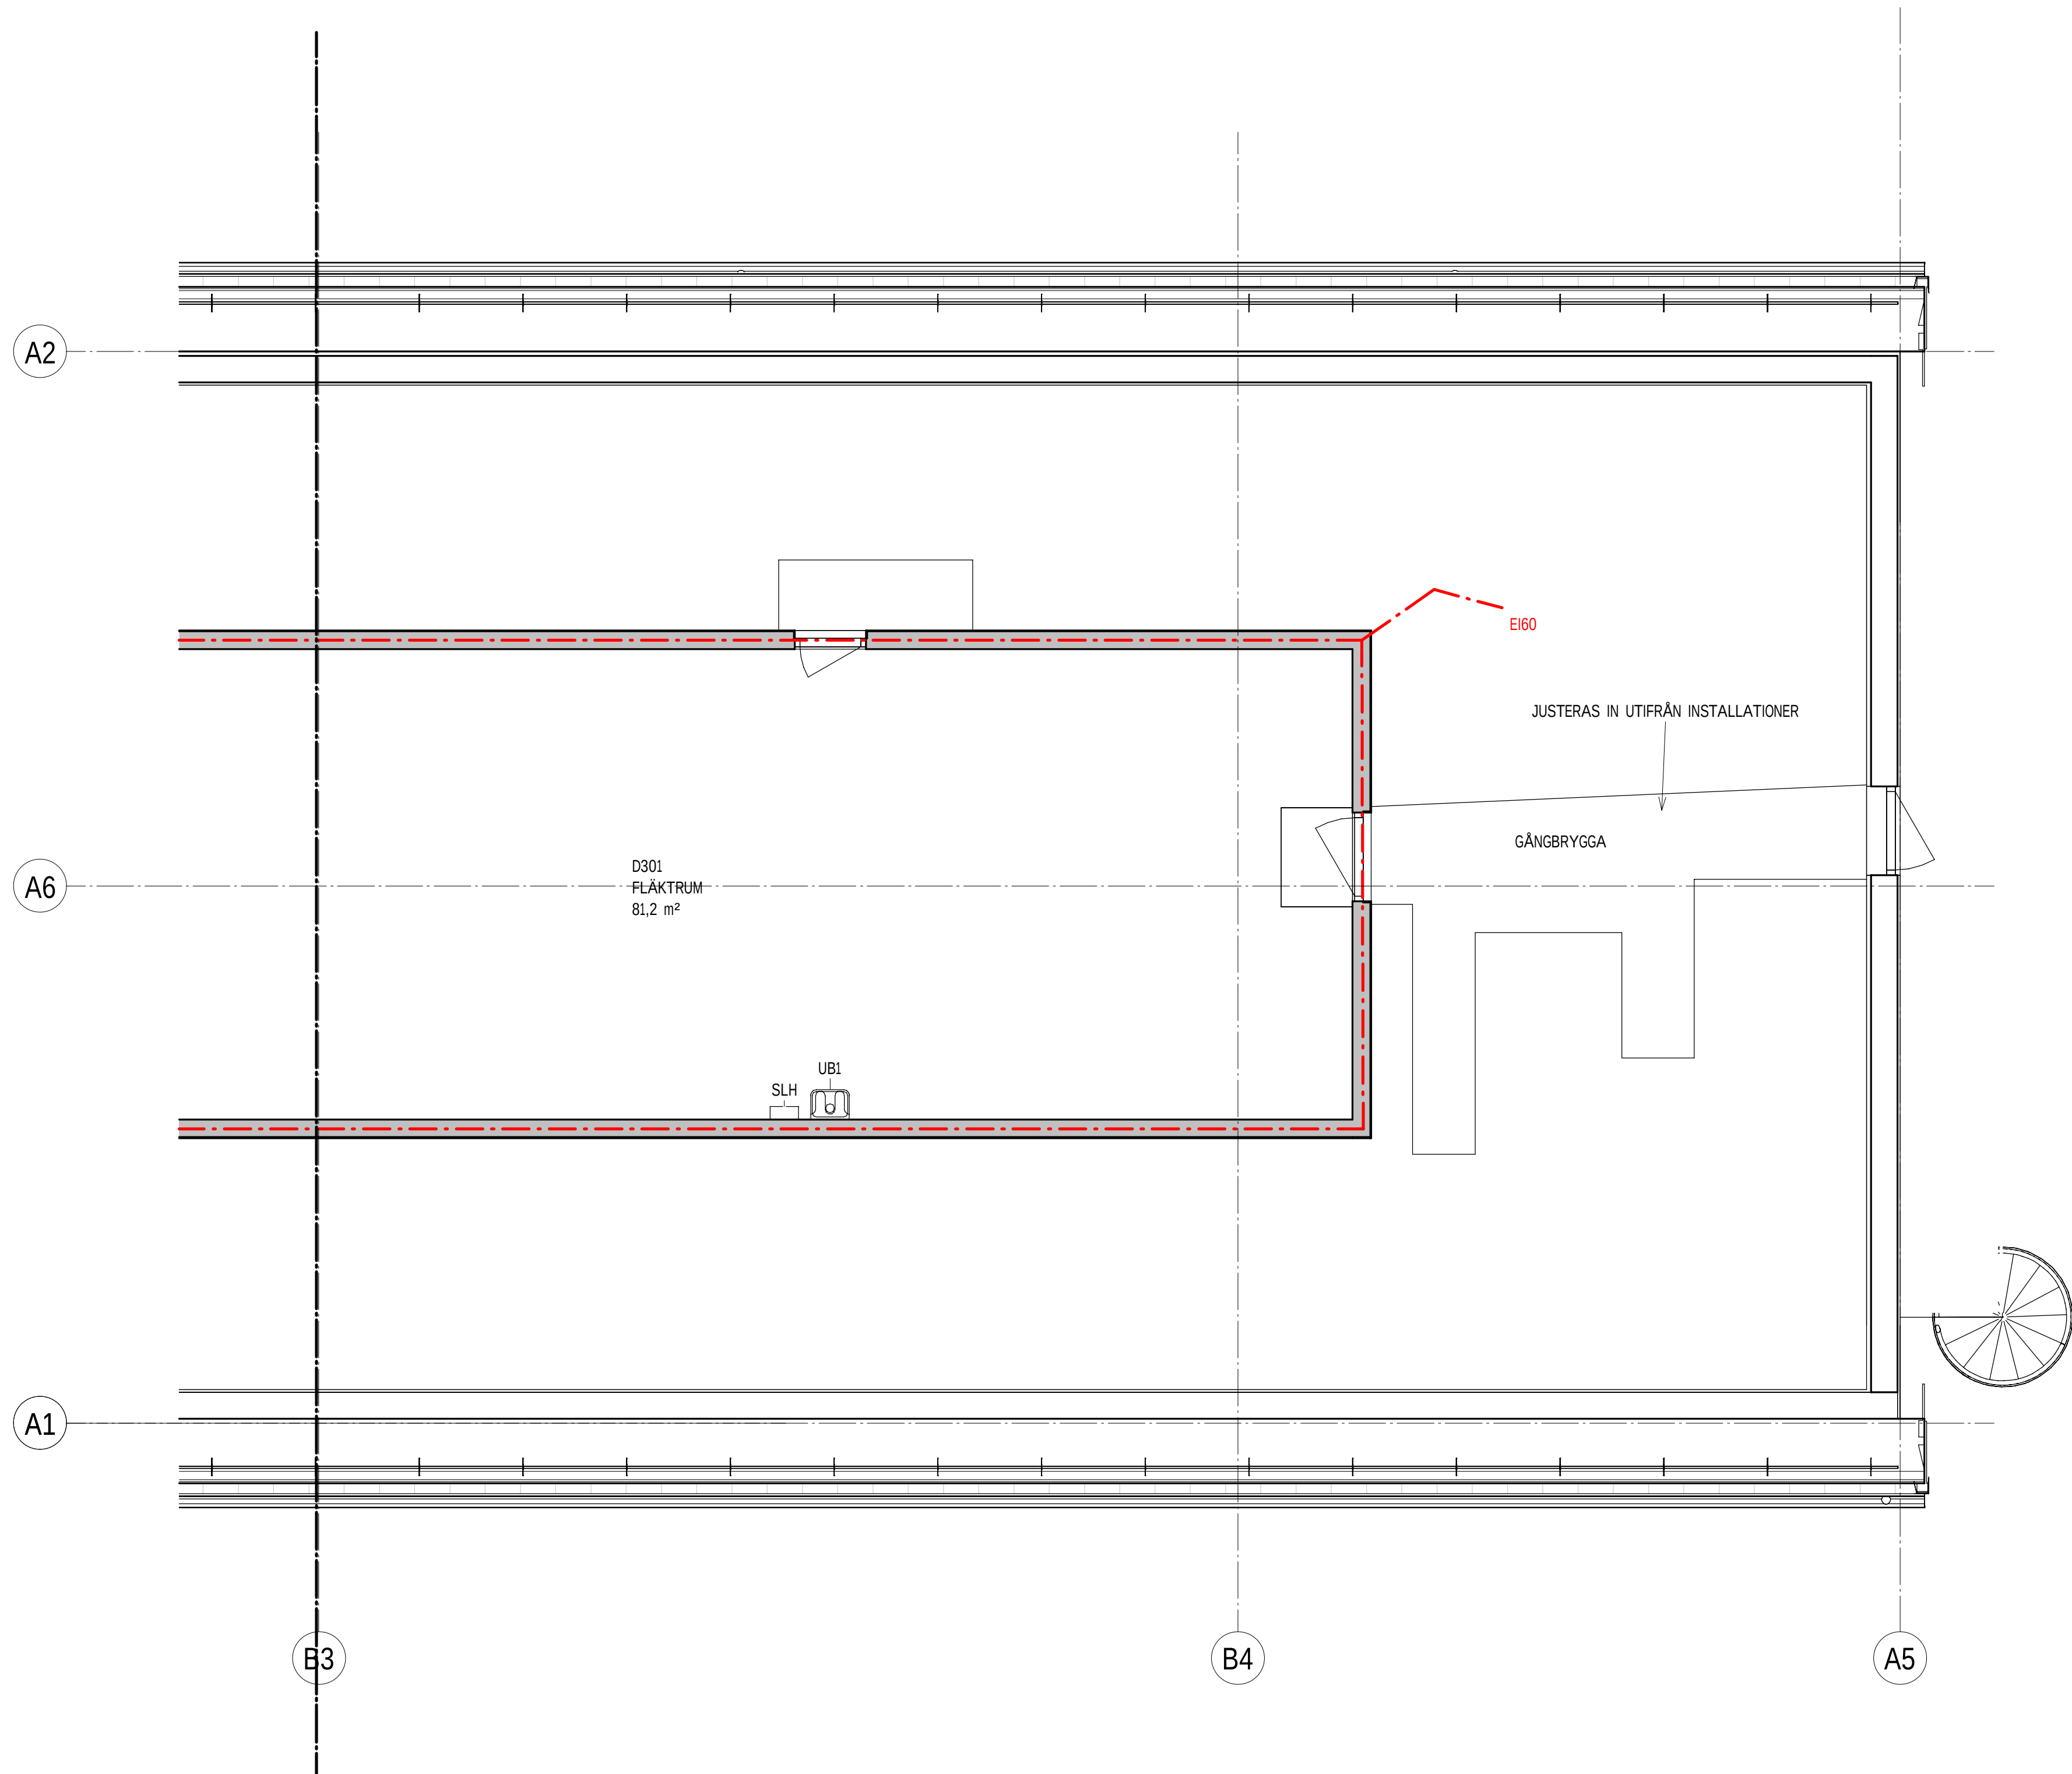

SKALA 1:50

0
METER

SET	ÄNDRING AVSER	DATUM	SIGN	STATUS
GRANSKNINGSHANDLING				HANDLING
BYGGHANDLING				ÄNDRING
2025-02-26		PROJEKT		
CENTRUMHUSET HUS D KRÅKAN 1, ROBERTSFORS				
ANSVARIG PART				
 AFRY		AFRY Ark Studio		
J. Sjögren	KONTAKTPERSON	L.Grubbström	SKRAPAD AV	
J. Sjögren	ÖSKÄND AV	210550	UPPERGÅNGSKART	
		RITNINGSKATEGORI		
OMBYGGNAD BIBLIOTEK OCH LÄGENHETER		INNEHÅLL	A1	FORMAT
PLAN 300 - DEL 2			1:50	SKALA
A-40-1-D302		NUMMER		BET