


2.

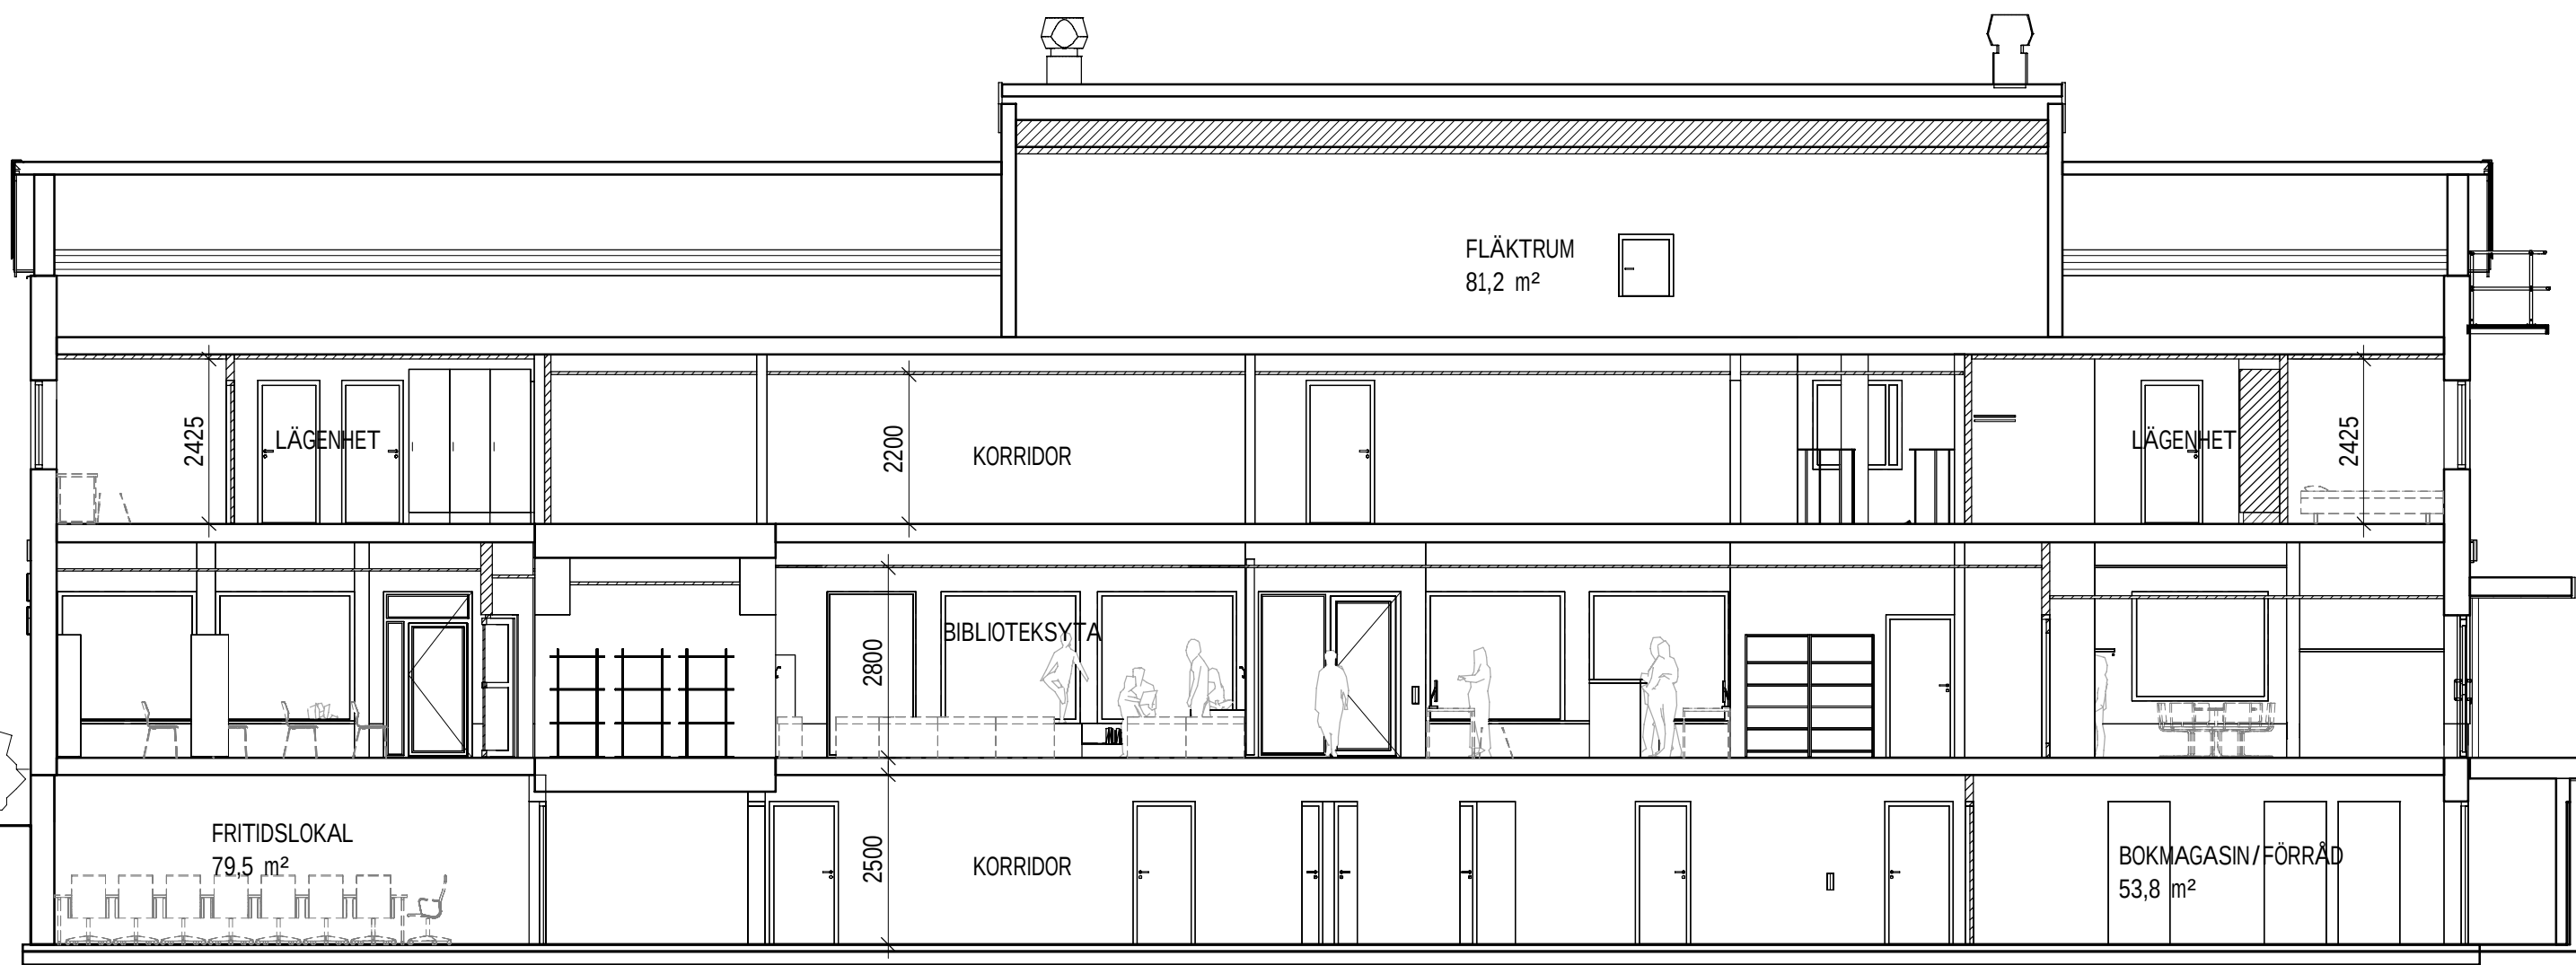

FÖRKLARINGAR

BRANDCELLSGRÄNSER:
E115
E30
E130
E160

+ 12,34 PLUSHÖJD
↑ FG + 1,000 PLUSHÖJD - FÄRDIGT GOLV
+ 2,700 ÖFG PLUSHÖJD - ÖVER FÄRDIGT GOLV

FÖRESKRIFTER

BRAND:
VÄGGAR SKA UTFÖRAS I BRANDKLASS ENL.
BRANDSKYDDSBESKRIVNING OCH BRANDCELLSINDELNING PÅ
BRANDSKYDDSRITNINGAR.
VID AVVIKELSER MELLAN A-RITNINGAR OCH
BRANDSKYDDSRITNINGAR GÄLLER
UTFÖRANDE ENLIGT BRANDSKYDDSRITNINGAR.

1.



SKALA 1:100
0 1 2 5 10
METER

BET	ÄNDRING AVSER	DATUM	SIGN	STATUS
GRANSKNINGSHANDLING				
BYGGHANDLING				
2025-02-26		ÄNDRING		
CENTRUMHUSET HUS D				
KRÅKAN 1, ROBERTSFORS				
ANSVARIG PART				
 AFRY		AFRY Ark Studio		
J. Sjögren	KONTAKTPERSON	L.Grubbström	SKAPAD AV	
J. Sjögren	GODKÄND AV	210550	UPPERAGSNUMMER	
PITNINGSSKIZZOR				
OMBYGGNAD BIBLIOTEK OCH LÄGENHETER		INNEHÅLL	A1	FORMAT
SEKTIONER			1:100	SKALA
A-40-2-01		NUMMER		BET