

## FÖRKLARINGAR

## FÖRESKRIFTER

FASAD:

**BALKONGER:**  
BALKONGDÖRRAR BYTS/BREDDAS 100 MM TILL D10  
BALKONGFRONTER OCH RÅKEN BYTS TILL NYA.  
BALKONGFRONT I KURRUGERAD PLÅT.  
KULÖR: KOPPARGRÖN LIKA BEF  
BALKONGGOLV HÖJS TILL FG LIKA LÄGENHET  
NY SKÄRMVÄGG I TRÅ TILL MITTBALKONG.  
KULÖR BEIGE LIKA BEF FASADPANEL/PUTS

DÖRRAR / FÖNSTER:  
FÖNSTER OCH ENTREPARTIER SOM BYTS TILL NYA.  
KULÖR: ANODIZERAD ALUMINIUM SVART

PLÅTBESLAG, KULÖR: ANODIZERAD SVART

TAK:  
MATERIAL / KULÖR: BEFINTLIG, BANDTÄCKT PLÅT, SVART

**TAKSÄKERHET:**  
**MATERIAL / KULÖR: BEFINTLIG VFZ**

TAKAVATTNING:  
MATERIAL / KULÖR: BEFINTLIG VIT

**GAVELSKYLT**  
SKYLT TYP P6. DJUPA FRISTÅENDE SJÄLVLYSANDE BOKSTÄVER  
(INV LED). BOKSTÄVER I KULÖR RAL 6026 OPAL GREEN.  
FOLIERING FRÅMSIDA AKRYL I RAL 6026 OPAL GREEN  
BOKSTÄVER MONTERAS PÅ ALUMINIUMSKENA.


TYPSNITT ARIAL, TECKENSTORLEK 400 MM

BEFINTLIG SKYLTTAVLA RIVS/DEMONTERAS


**ENTRÉSKYL**  
SKYL

**BEFINTLIGA SKYLtar LÄNGS ENTRÉSIDA RIVS/DEMONTAS**


**KONTRASTMARKERING**  
**KONTRASTMARKERING I TVÅ OLIKA HÖJDER**  
**UK 800 SAMT UK 1500**  
**KULÖR SVART/VIT**

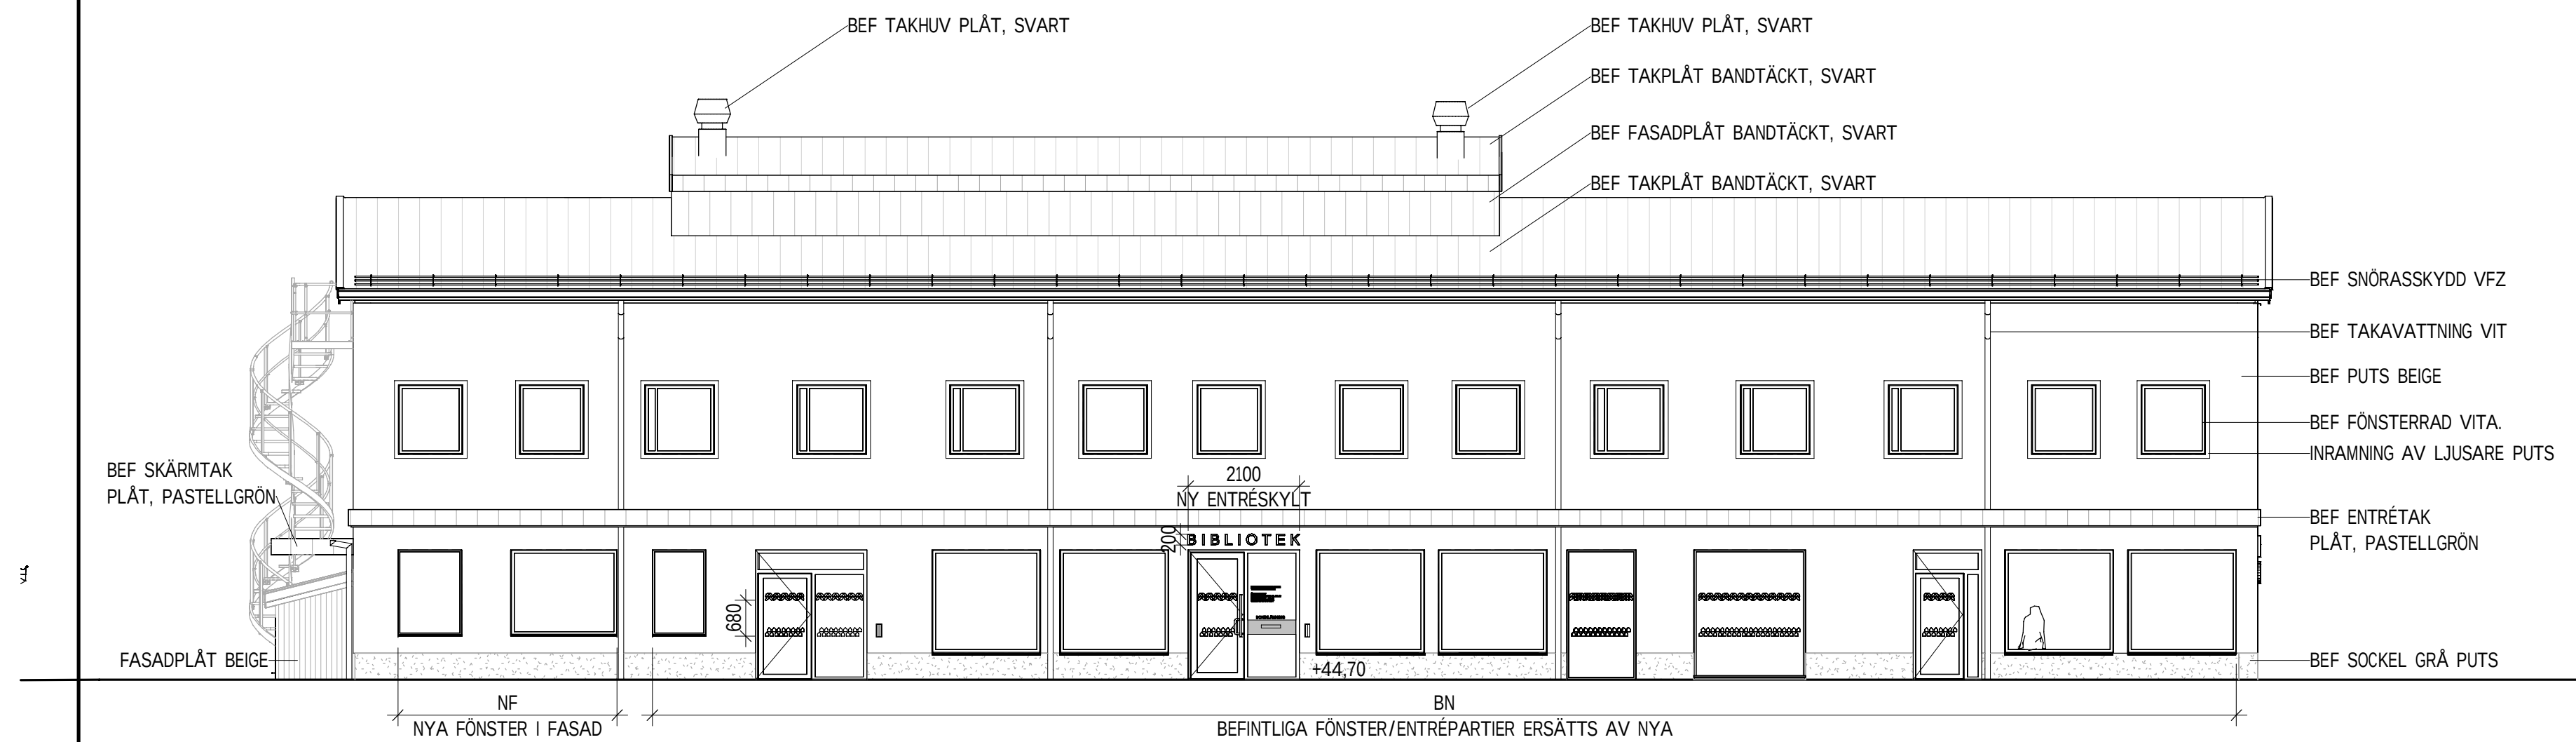


1/100 FASAD MOT NORDVÄST, ENTRÉSIDA

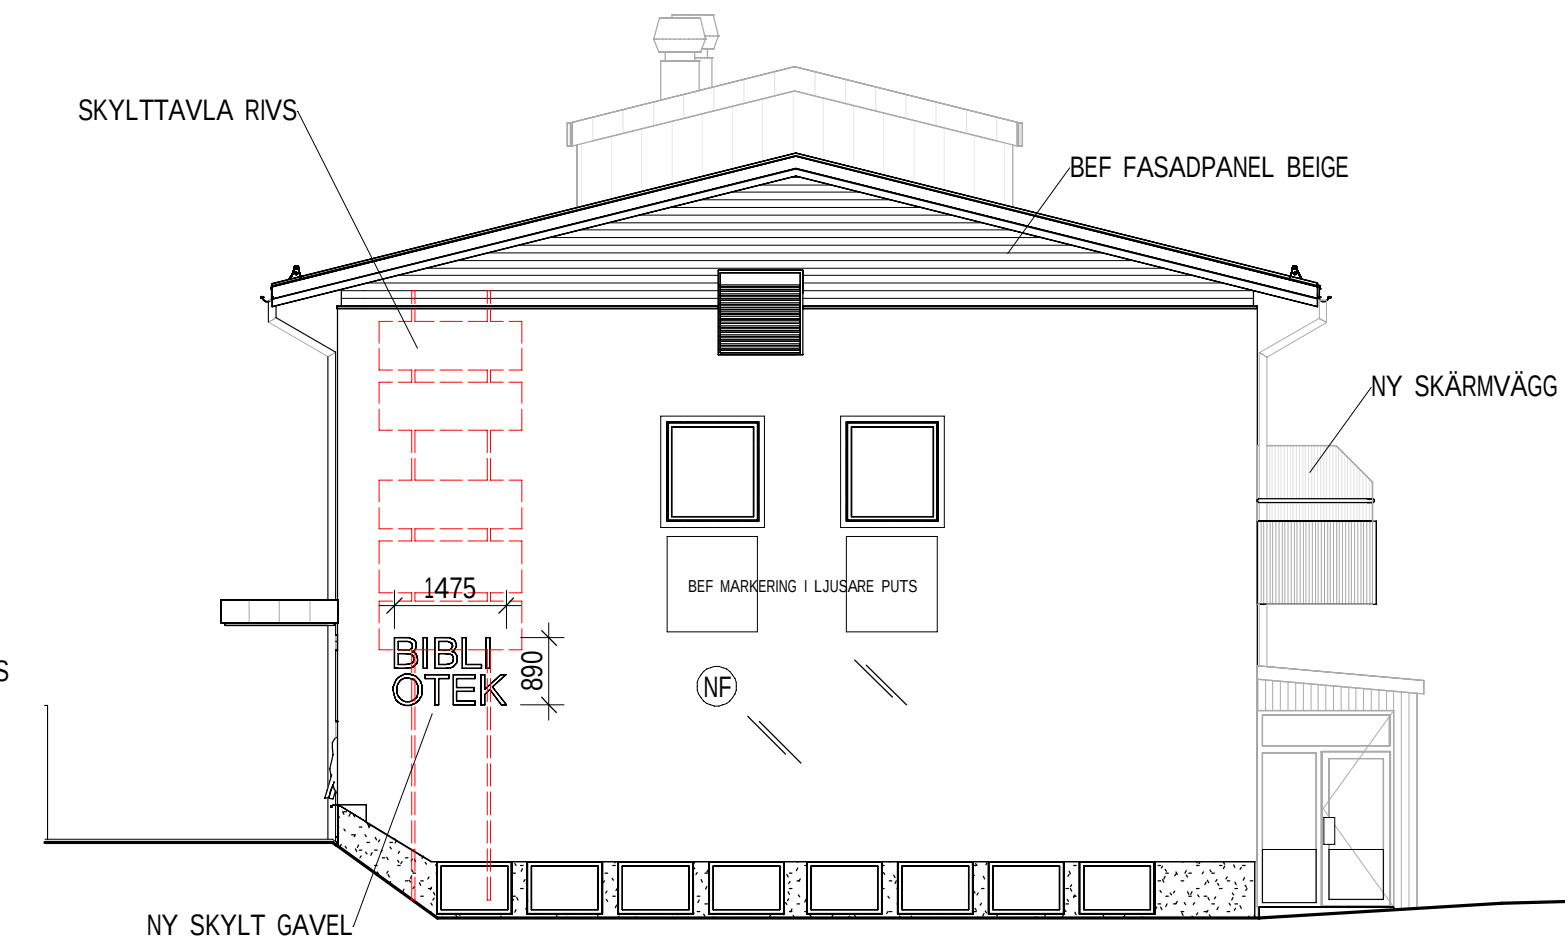


1/100 FASAD MOT SYDVÄST, STORGATAN

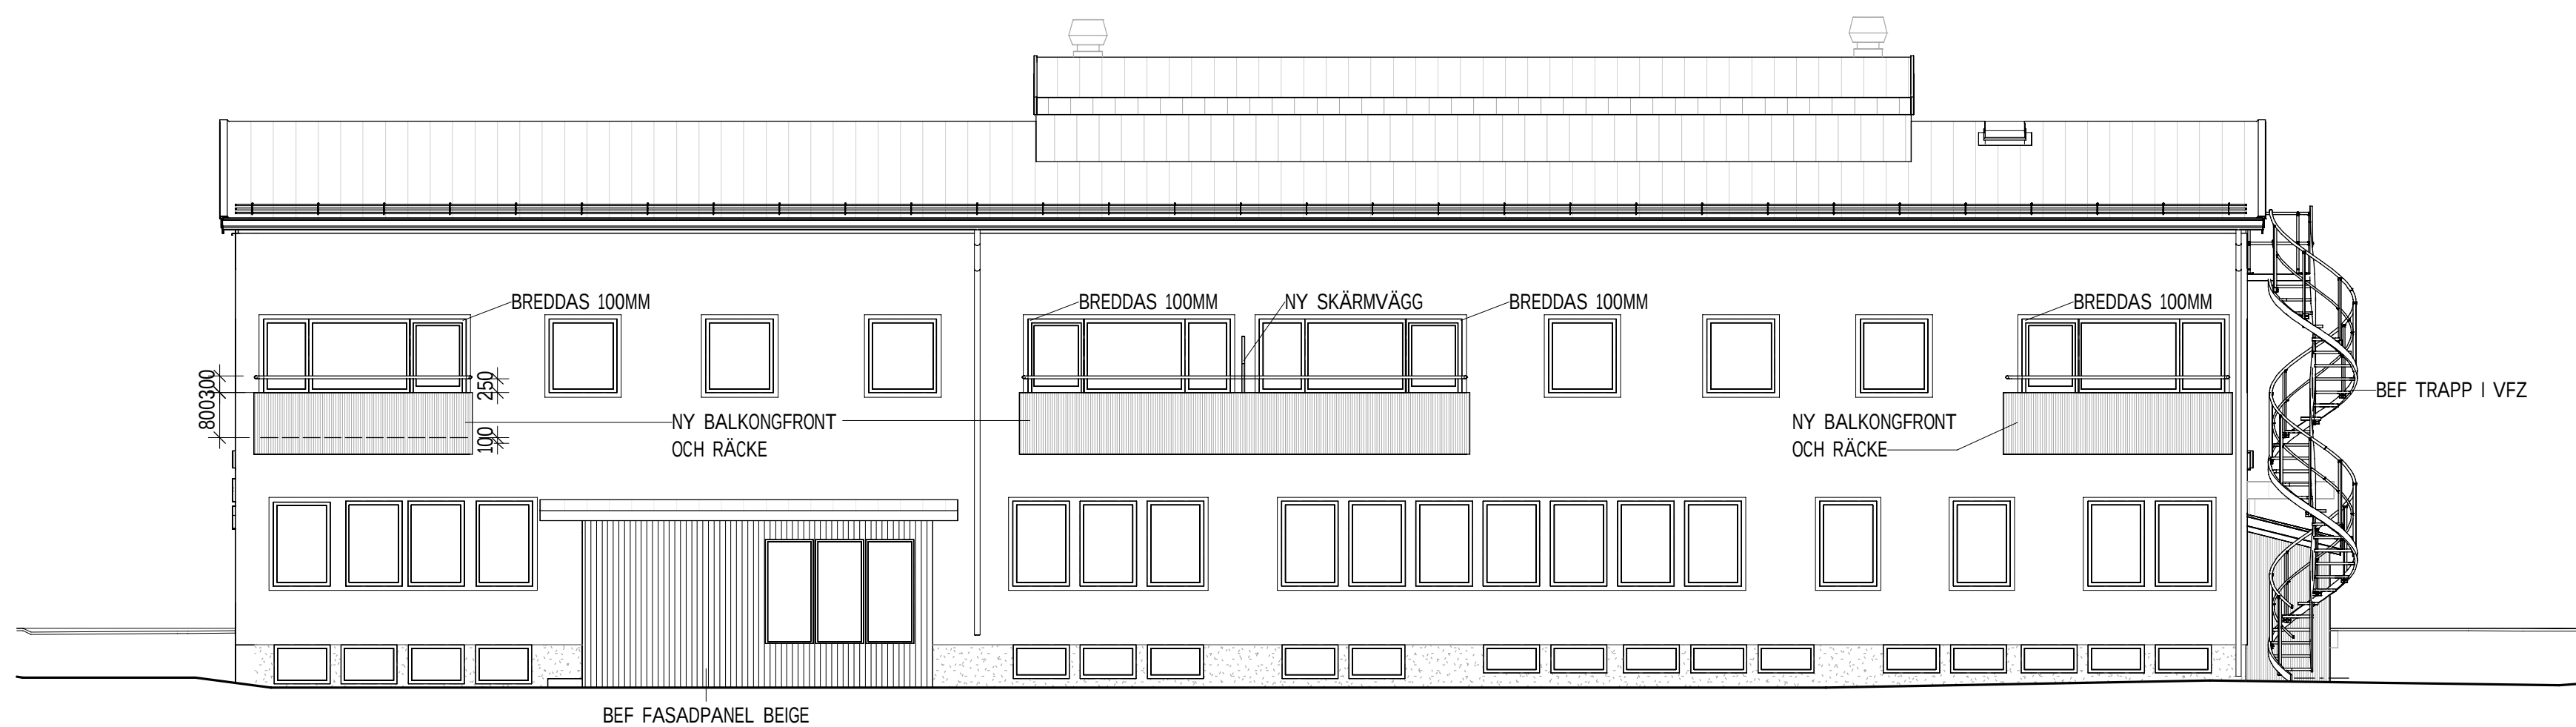

1/100 FASAD MOT SYDOST, BAKSIDA

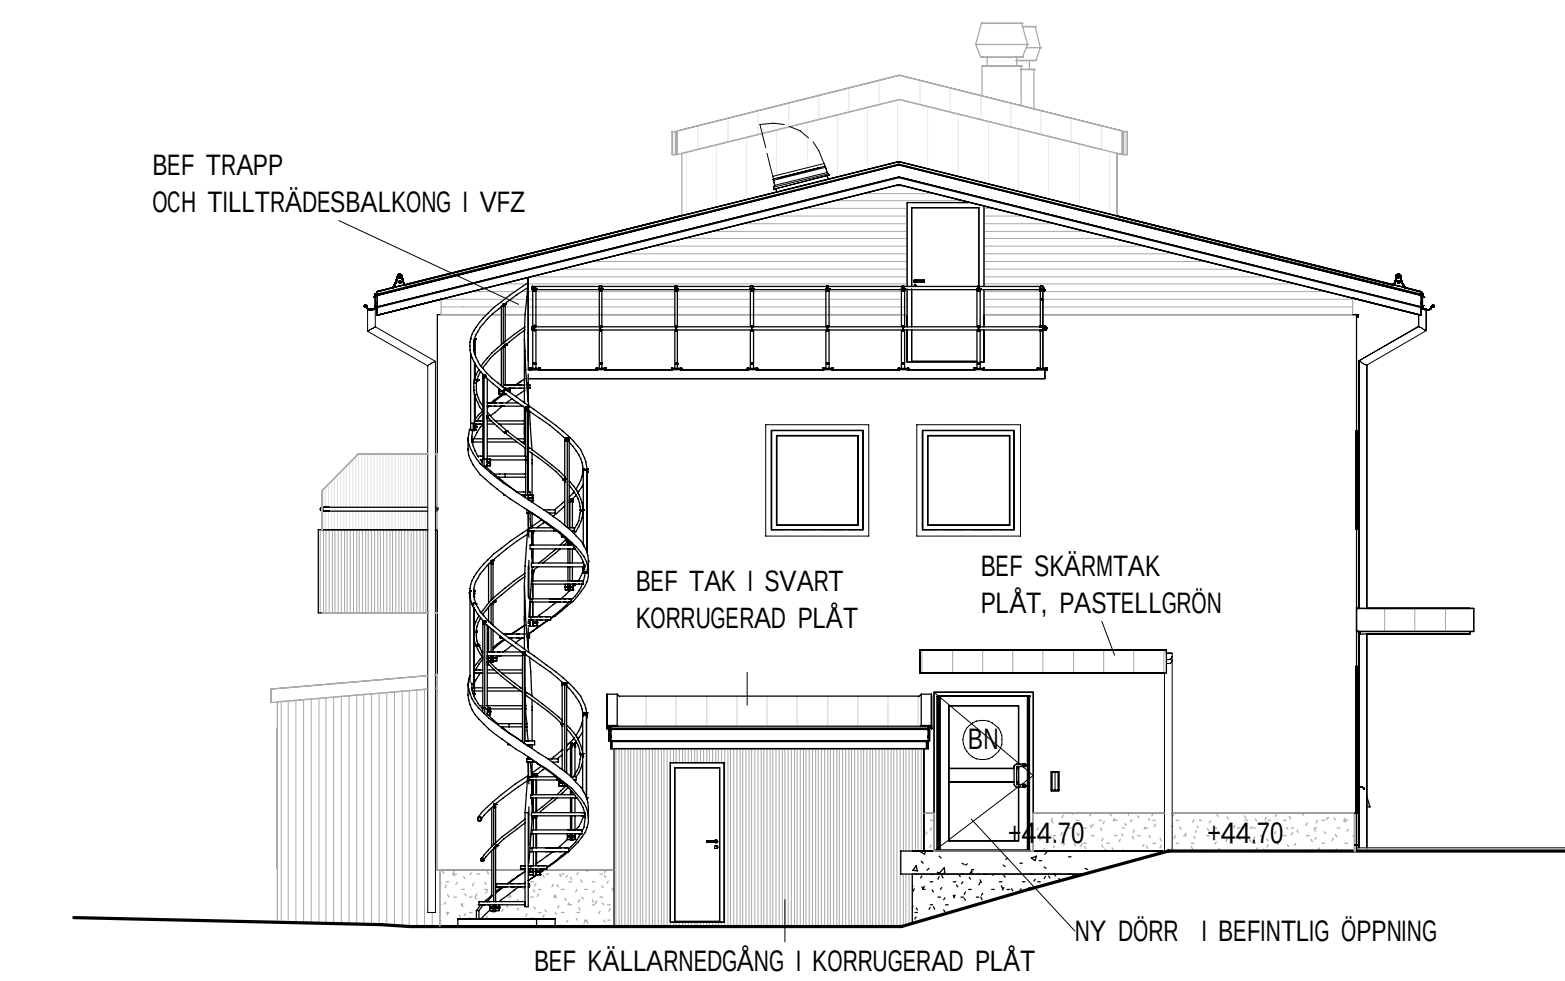

1/100 FASAD MOT NORDOST, PARKERING

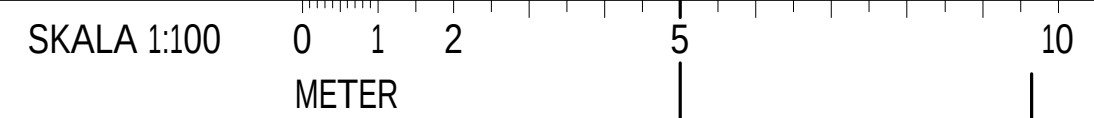

|                                                                                                   |               |                        |                  |        |
|---------------------------------------------------------------------------------------------------|---------------|------------------------|------------------|--------|
| SET                                                                                               | ÄNDRING AVSER | DATUM                  | SIGN             | STATUS |
| GRANSKNINGSHANDLING                                                                               |               |                        |                  |        |
| BYGGHANDLING                                                                                      |               |                        |                  |        |
| 2025-02-26                                                                                        |               | ÄNDRING                |                  |        |
| CENTRUMHUSET HUS D                                                                                |               |                        |                  |        |
| KRÅKAN 1, ROBERTSFORS                                                                             |               |                        |                  |        |
| ANSVARIG PART                                                                                     |               |                        |                  |        |
|  <b>AFRY</b> |               | <b>AFRY Ark Studio</b> |                  |        |
| J. Sjögren                                                                                        | KONTAKTPERSON | L.Grubbström           | SKAPAD AV        |        |
| J. Sjögren                                                                                        | ÖSKÄND AV     | 210550                 | UPPRÄKNINGSKOD   |        |
|                                                                                                   |               |                        | RITNINGSKATEGORI |        |
| OMBYGGNAD BIBLIOTEK OCH LÄGENHETER                                                                |               |                        | INNEHÅLL         | FORMAT |
| FASADER                                                                                           |               |                        | A1               | SKALA  |
| NORDVÄST, SYDVÄST, SYDOST, NORDOST                                                                |               |                        | 1:100            | BET    |
| A-40-3-01                                                                                         |               |                        | NUMMER           |        |