
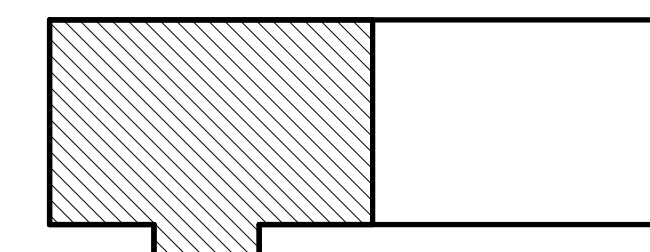


FÖRKLARINGAR

LITTERA:
VH - NY VENTILATIONSHUV

FÖRESKRIFTER

BRAND:
VÄGGAR SKA UTFÖRAS I BRANDKLASS ENL
BRANDSKYDDSBESKRIVNING OCH BRANDCELLSINDELNING PÅ
BRANDSKYDDSRITNINGAR.
VID AVVIKELSER MELLAN A-RITNINGAR OCH
BRANDSKYDDSRITNINGAR GÄLLER
UTFÖRANDE ENLIGT BRANDSKYDDSRITNINGAR.

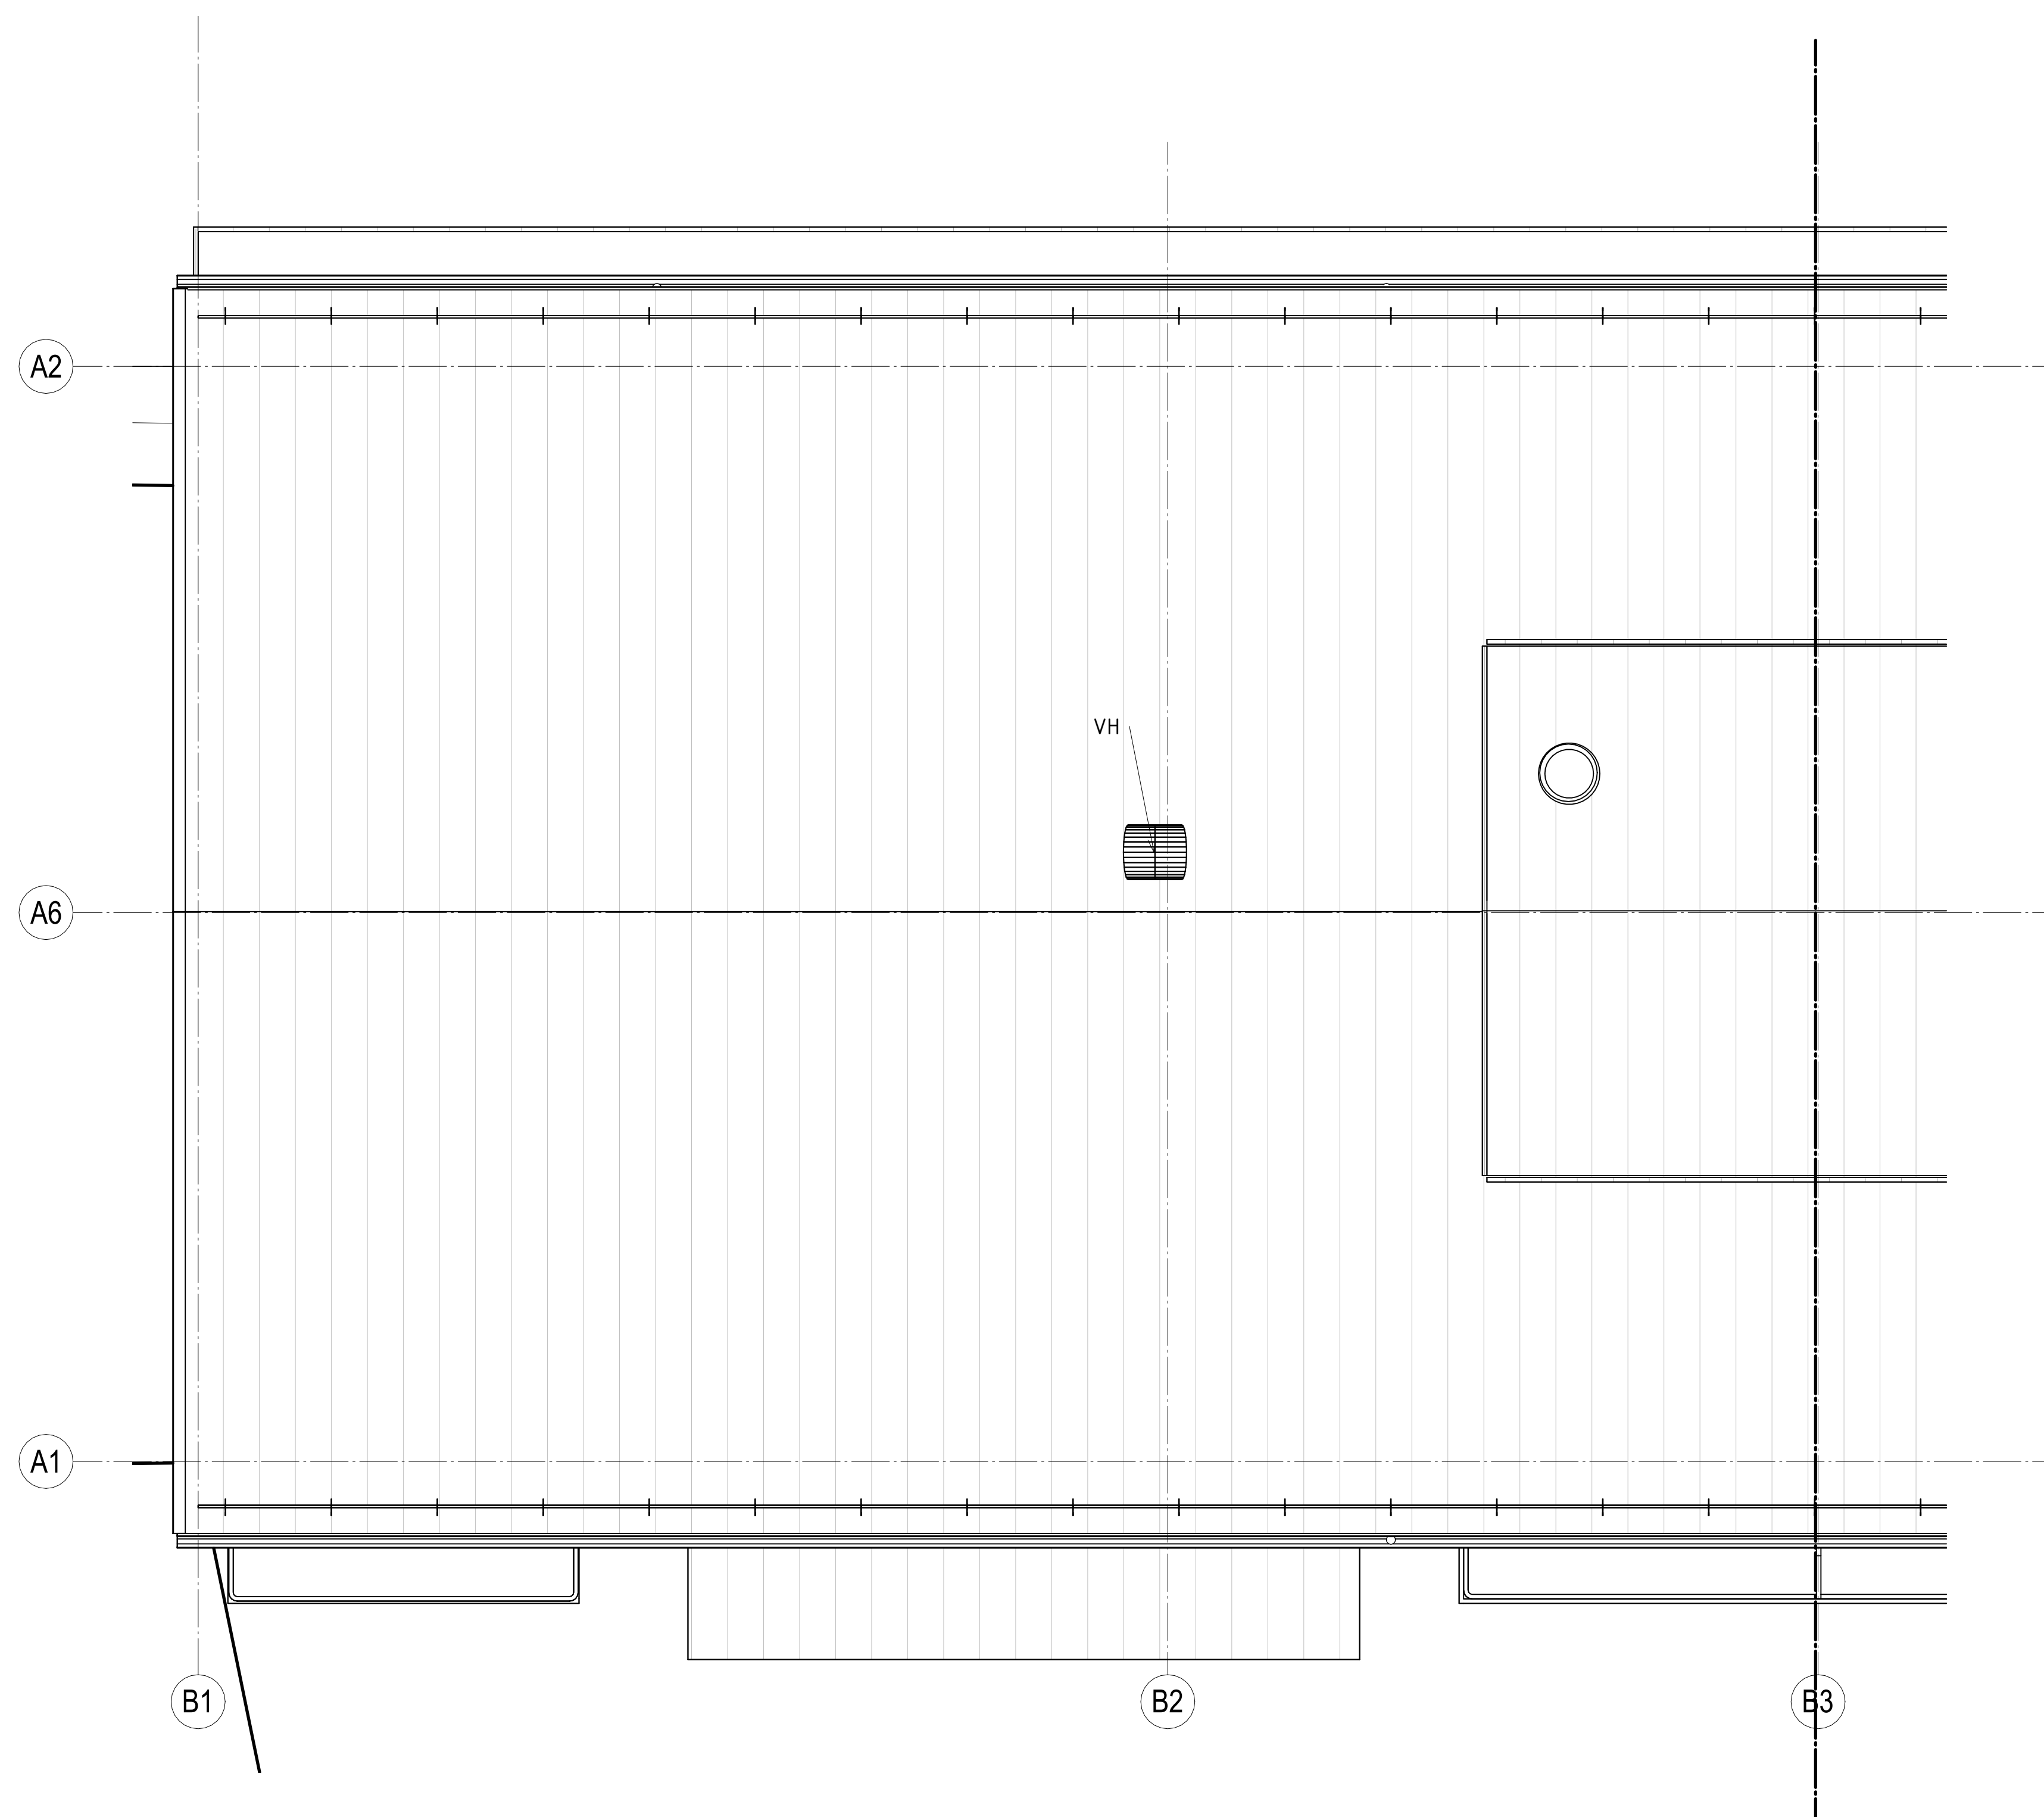

BET	ANDRING AVSEER	DATUM	SIGN	ST
GRÄNSKNINGSHANDLING				
BYGGHANDLING				
2025-02-26		DATUM	AN	
CENTRUMHUSET HUS D KRÅKAN 1, ROBERTSFORS				
ANSVARIG			AFRY Ark Studio	
		AFRY		
J. Sjögren	KONTAKTPERSON	L.Grubbström	SKAPA	
J. Sjögren	GÖRÄND AV	201550	UPPERGÅRAN	
			RITNINGSGRUPP	
OMBYGGNAD BIBLIOTEK OCH LÄGENHETER		INNEHÅLL	FÖR	
TAKPLAN DEL 1			A1	S
A-41-1-01		NUMMER		

STATUS	
BEFRIEDUNG	
BEFRIEDUNG	
OBJEKT	
PART	
DO AV	
CHMER	
REGORI	
FORMAT	
KALA	
BET	

Dateien C:\Users\jmd534\OneDrive - AFRY\Documents\A-4-0-V-01_ludwig.grubbsfrom.rvt

SKALA 1:50 0 1 2

METER