
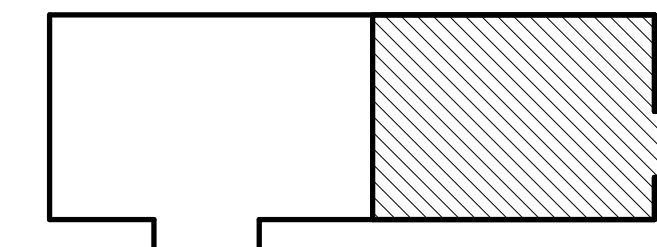


FÖRKLARINGAR

LITTERA:
VH - NY VENTILATIONSHUV

FÖRESKRIFTER

BRAND:
VÄGGAR SKA UTFÖRAS I BRANDKLASS ENL
BRANDSKYDDSBESKRIVNING OCH BRANDCELLSINDELNING PÅ
BRANDSKYDDSRITNINGAR.
VID AVVIKELSER MELLAN A-RITNINGAR OCH
BRANDSKYDDSRITNINGAR GÄLLER
UTFÖRANDE ENLIGT BRANDSKYDDSRITNINGAR.

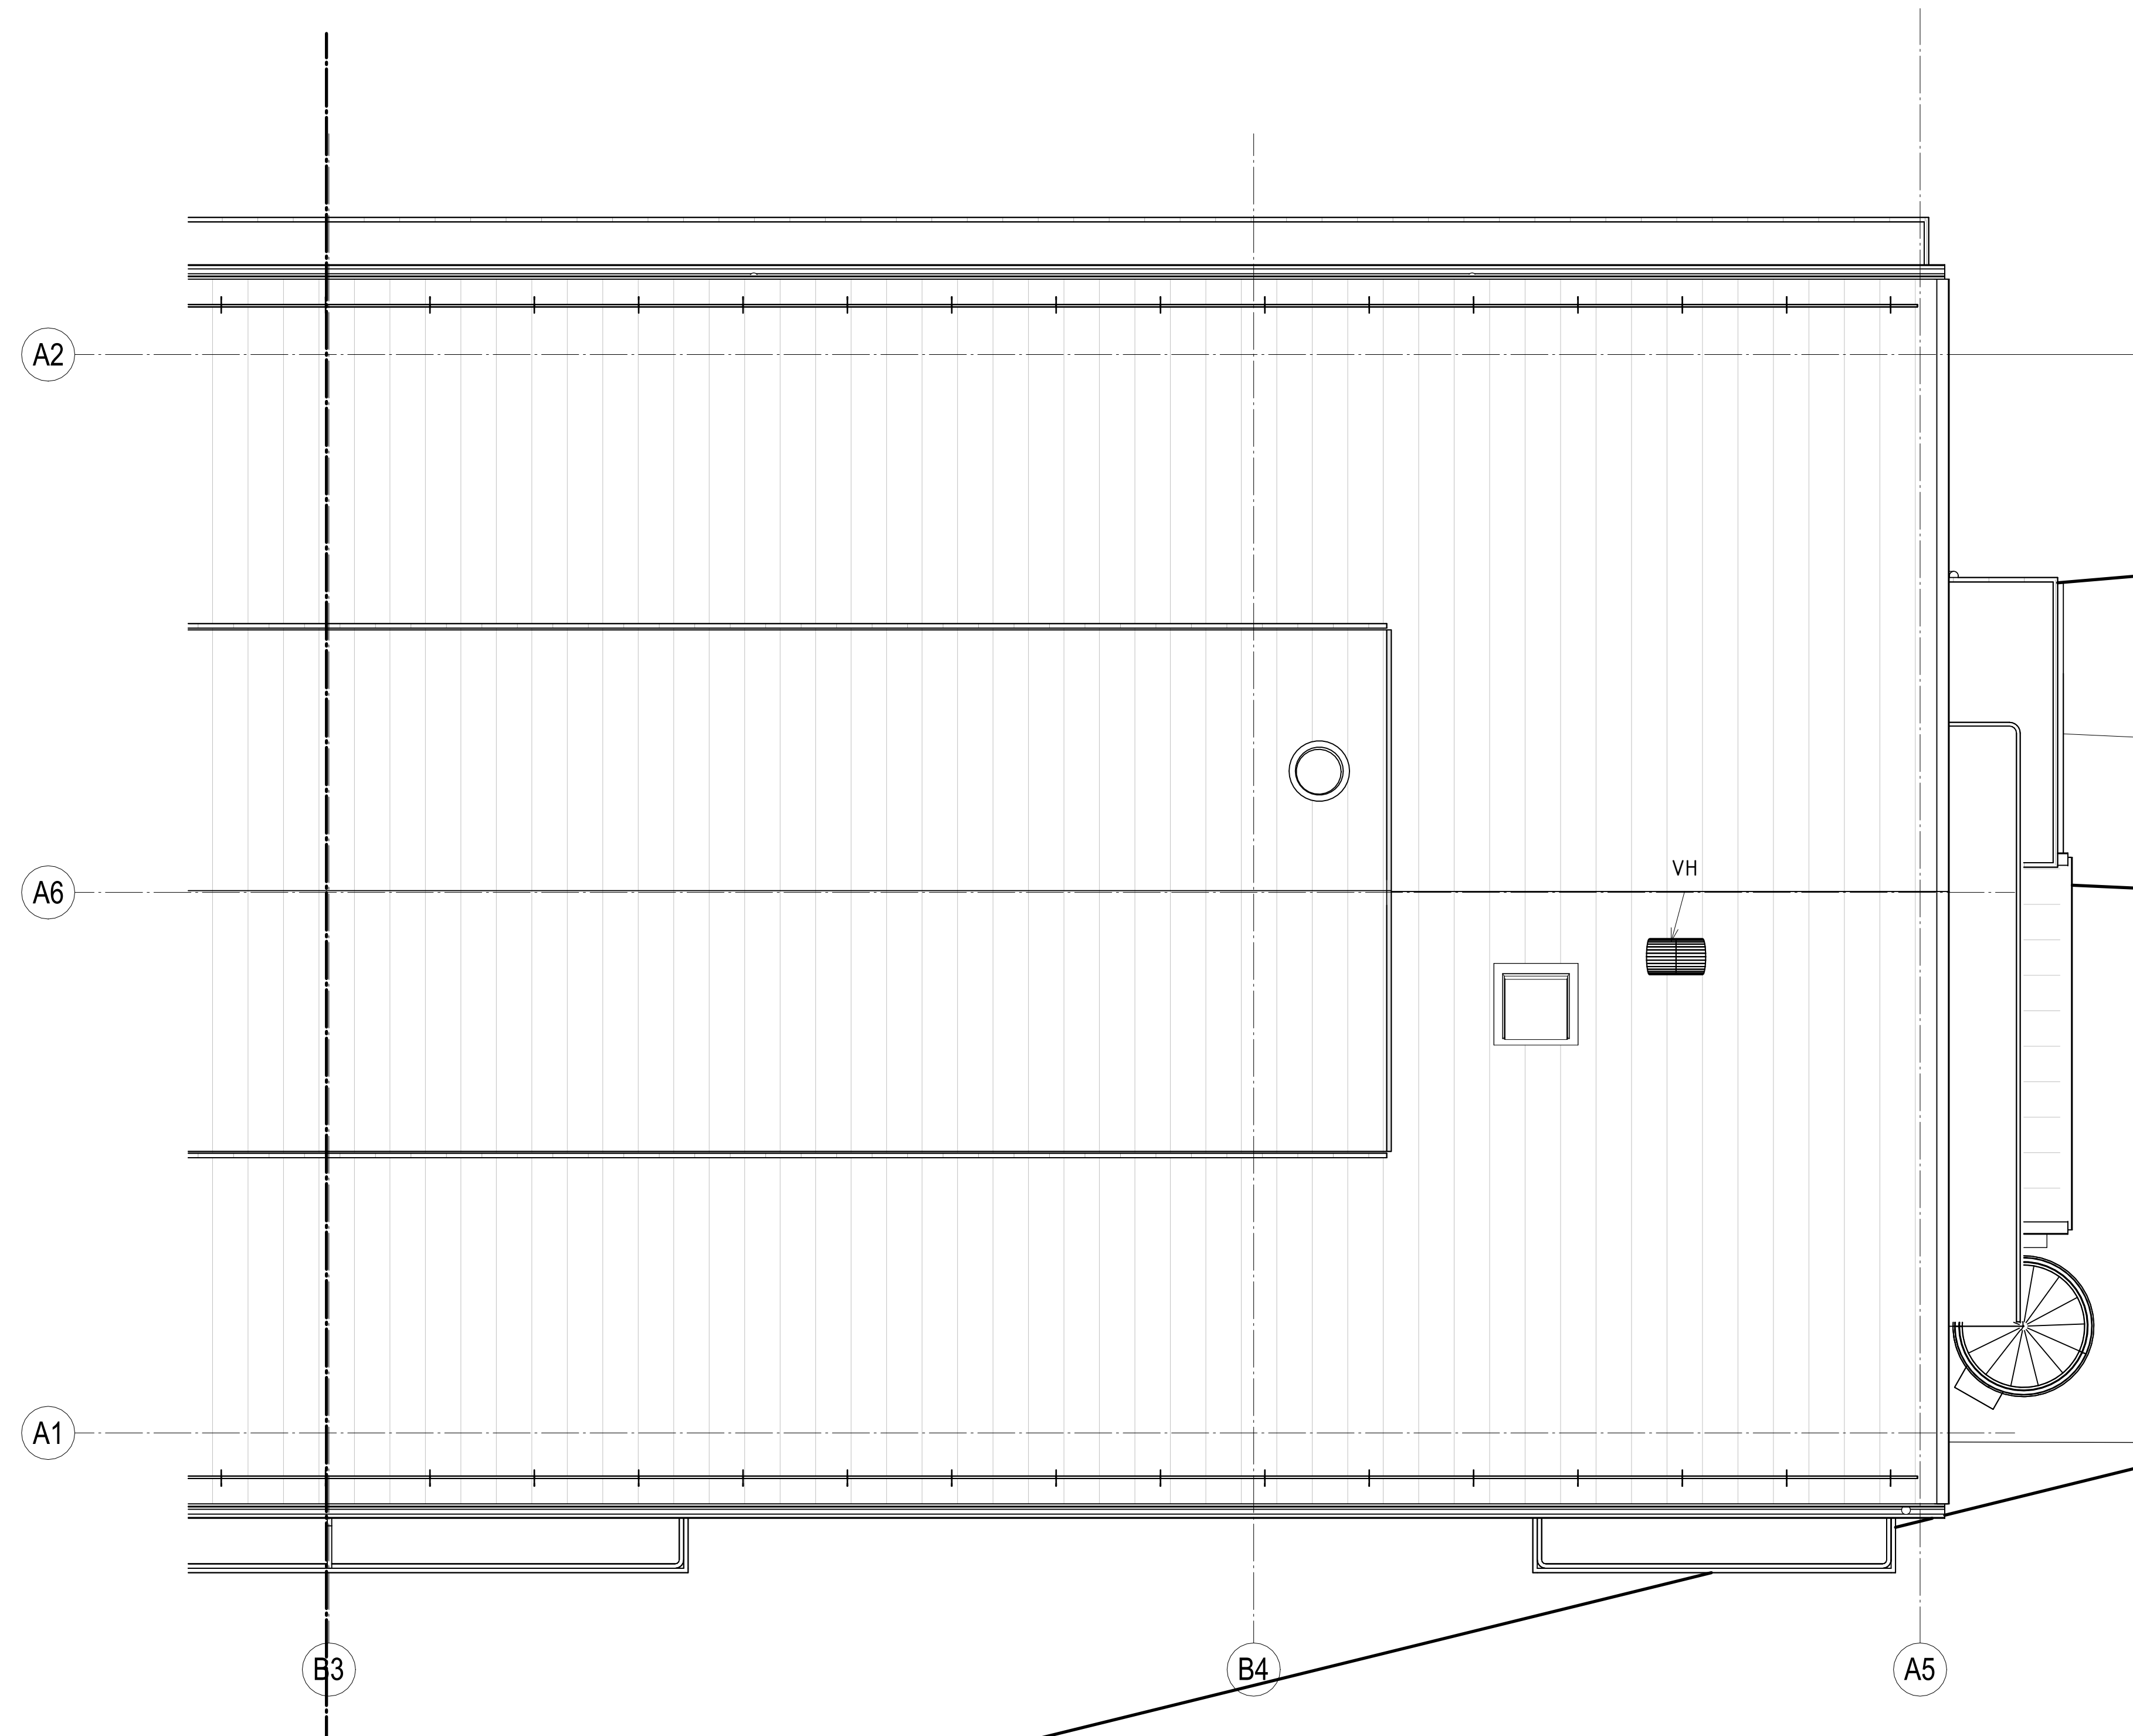

BET	ANDRING AVSEER	DATUM	SIDEN	514705
GRANSKNINGSHANDLING				
BYGGHANDLING			HANDLING	
2025-02-26		DATUM	ANDRING	
CENTRUMHUSET HUS D KRÅKAN 1, ROBERTSFORS				PROJEKT
		ANSVARIG PART AFRY Ark Studio		
J. Sjögren	KONTAKTPERSON	L.Grubbström	SKAPAD AV	
J. Sjögren	GÖKKAND. AV	210550	UPPERGÅNGSNUMMER	
				ÄTTENSKRAKATEGORI
OMBYGGNAD BIBLIOTEK OCH LÄGENHETER			INNEHÅLL	FORMAT
TAKPLAN DEL 2			A1	SKALA
			NUMMER	BET
A-41-1-02				

File C:\Users\jmd534\OneDrive - AFRY\Documents\A-40-V-01_ludwig.grubbsfrom.rvt

SKALA 1:50 0 1 2
METER