

FÖRKLARINGAR

MÄTT ANGES I MILLIMETER.  
HÖJD TILL UNDERTAK AVSER MÄTT FRÅN FG.  
TOTAL BYGGHÖJD AVSER UNDERTAKSKONSTRUKTIONENS TOTALA TJOCKLEK.  
TOTAL KONSTRUKTIONSHÖJD AVSER  
UNDERTAKSKONSTRUKTIONENS TOTALA TJOCKLEK INKL  
FRITT/PENDLAT AVSTÅND TILL OVANLIGGANDE BJÄLKLAG.

UT1 = UNDERTAK+TYP

+ 2.700 ÖFG PLUSHÖJD - ÖVER FÄRDIGT GOLV

FÖRESKRIFTER

VID MONTERING SAMORDNAS UNDERTAKET MED INSTALLATIONER.  
INSTALLATIONER MONTERAS MED ERFODERLIGA  
FÖRSTÄRKNINGAR ENLIGT FABRIKANTENS MONTAGEANVISNINGAR.

UT1:  
NEDPENDLAT UNDERTAK ECOPHON FOCUS  
TAKABSORBENTER 600X600X20 MM  
KULÖR: VIT  
MONTERAS ENLIGT M01  
VID NIVÅSKILLNAD ANVÄNDS VERTIKAL PLAN PLÅT VIT

UT2:  
DIKTMONTERAT GIPSTAK  
TOTAL KONSTRUKTIONSHÖJD 69 MM.  
28 MM GLESPANEL  
28 MM GLESPANEL  
13 MM GIPS  
VID NIVÅSKILLNAD ANVÄNDS VERTIKAL GIPSSKIVA


UT3:  
DIKTMONTERAT UNDERTAK ECOPHON MODUS  
TAKABSORBENTER 600X1200X100 MM  
KULÖR: VIT  
MONTERAS ENLIGT M23

UT4:  
NEDPENDLAT GIPSTAK  
TOTAL KONSTRUKTIONSHÖJD 40 MM.  
27 MM GK-PROFIL  
13 MM GIPS

UT5:  
INKLÄDNAD INSTALLATIONER  
HÖRNPROFIL H50/50  
13 MM GIPS  
VID NIVÅSKILLNAD ANVÄNDS VERTIKAL GIPSSKIVA

UT6:  
KABELRÄNNA ENL EL

| BET                                | ÄNDRING AVSER | DATUM        | SIGN           | STATUS |
|------------------------------------|---------------|--------------|----------------|--------|
| GRANSKNINGSHANDLING                |               |              |                |        |
| BYGGHANDLING                       |               |              |                |        |
| INNEHÅLL<br>2025-02-26             |               | ÄNDRING      |                |        |
| CENTRUMHUSET HUS D                 |               |              |                |        |
| KRÅKAN 1, ROBERTSFORS              |               |              |                |        |
| ANSVARIG PART                      |               |              |                |        |
| AFRY Ark Studio                    |               |              |                |        |
| J. Sjögren                         | KONTAKTPERSON | L.Grubbström | SKAPAD AV      |        |
| J. Sjögren                         | GODKÄND AV    | 210550       | UPPERAGSNUMMER |        |
| RITNINGSKATEGORI                   |               |              |                |        |
| OMBYGGNAD BIBLIOTEK OCH LÄGENHETER |               |              | INNEHÅLL       | FORMAT |
| UNDERTAK PLAN 100 DEL 2            |               |              | A1             | SKALA  |
| A-43-1-D102                        |               |              | 1:50           | BET    |
|                                    |               |              | NUMBER         |        |

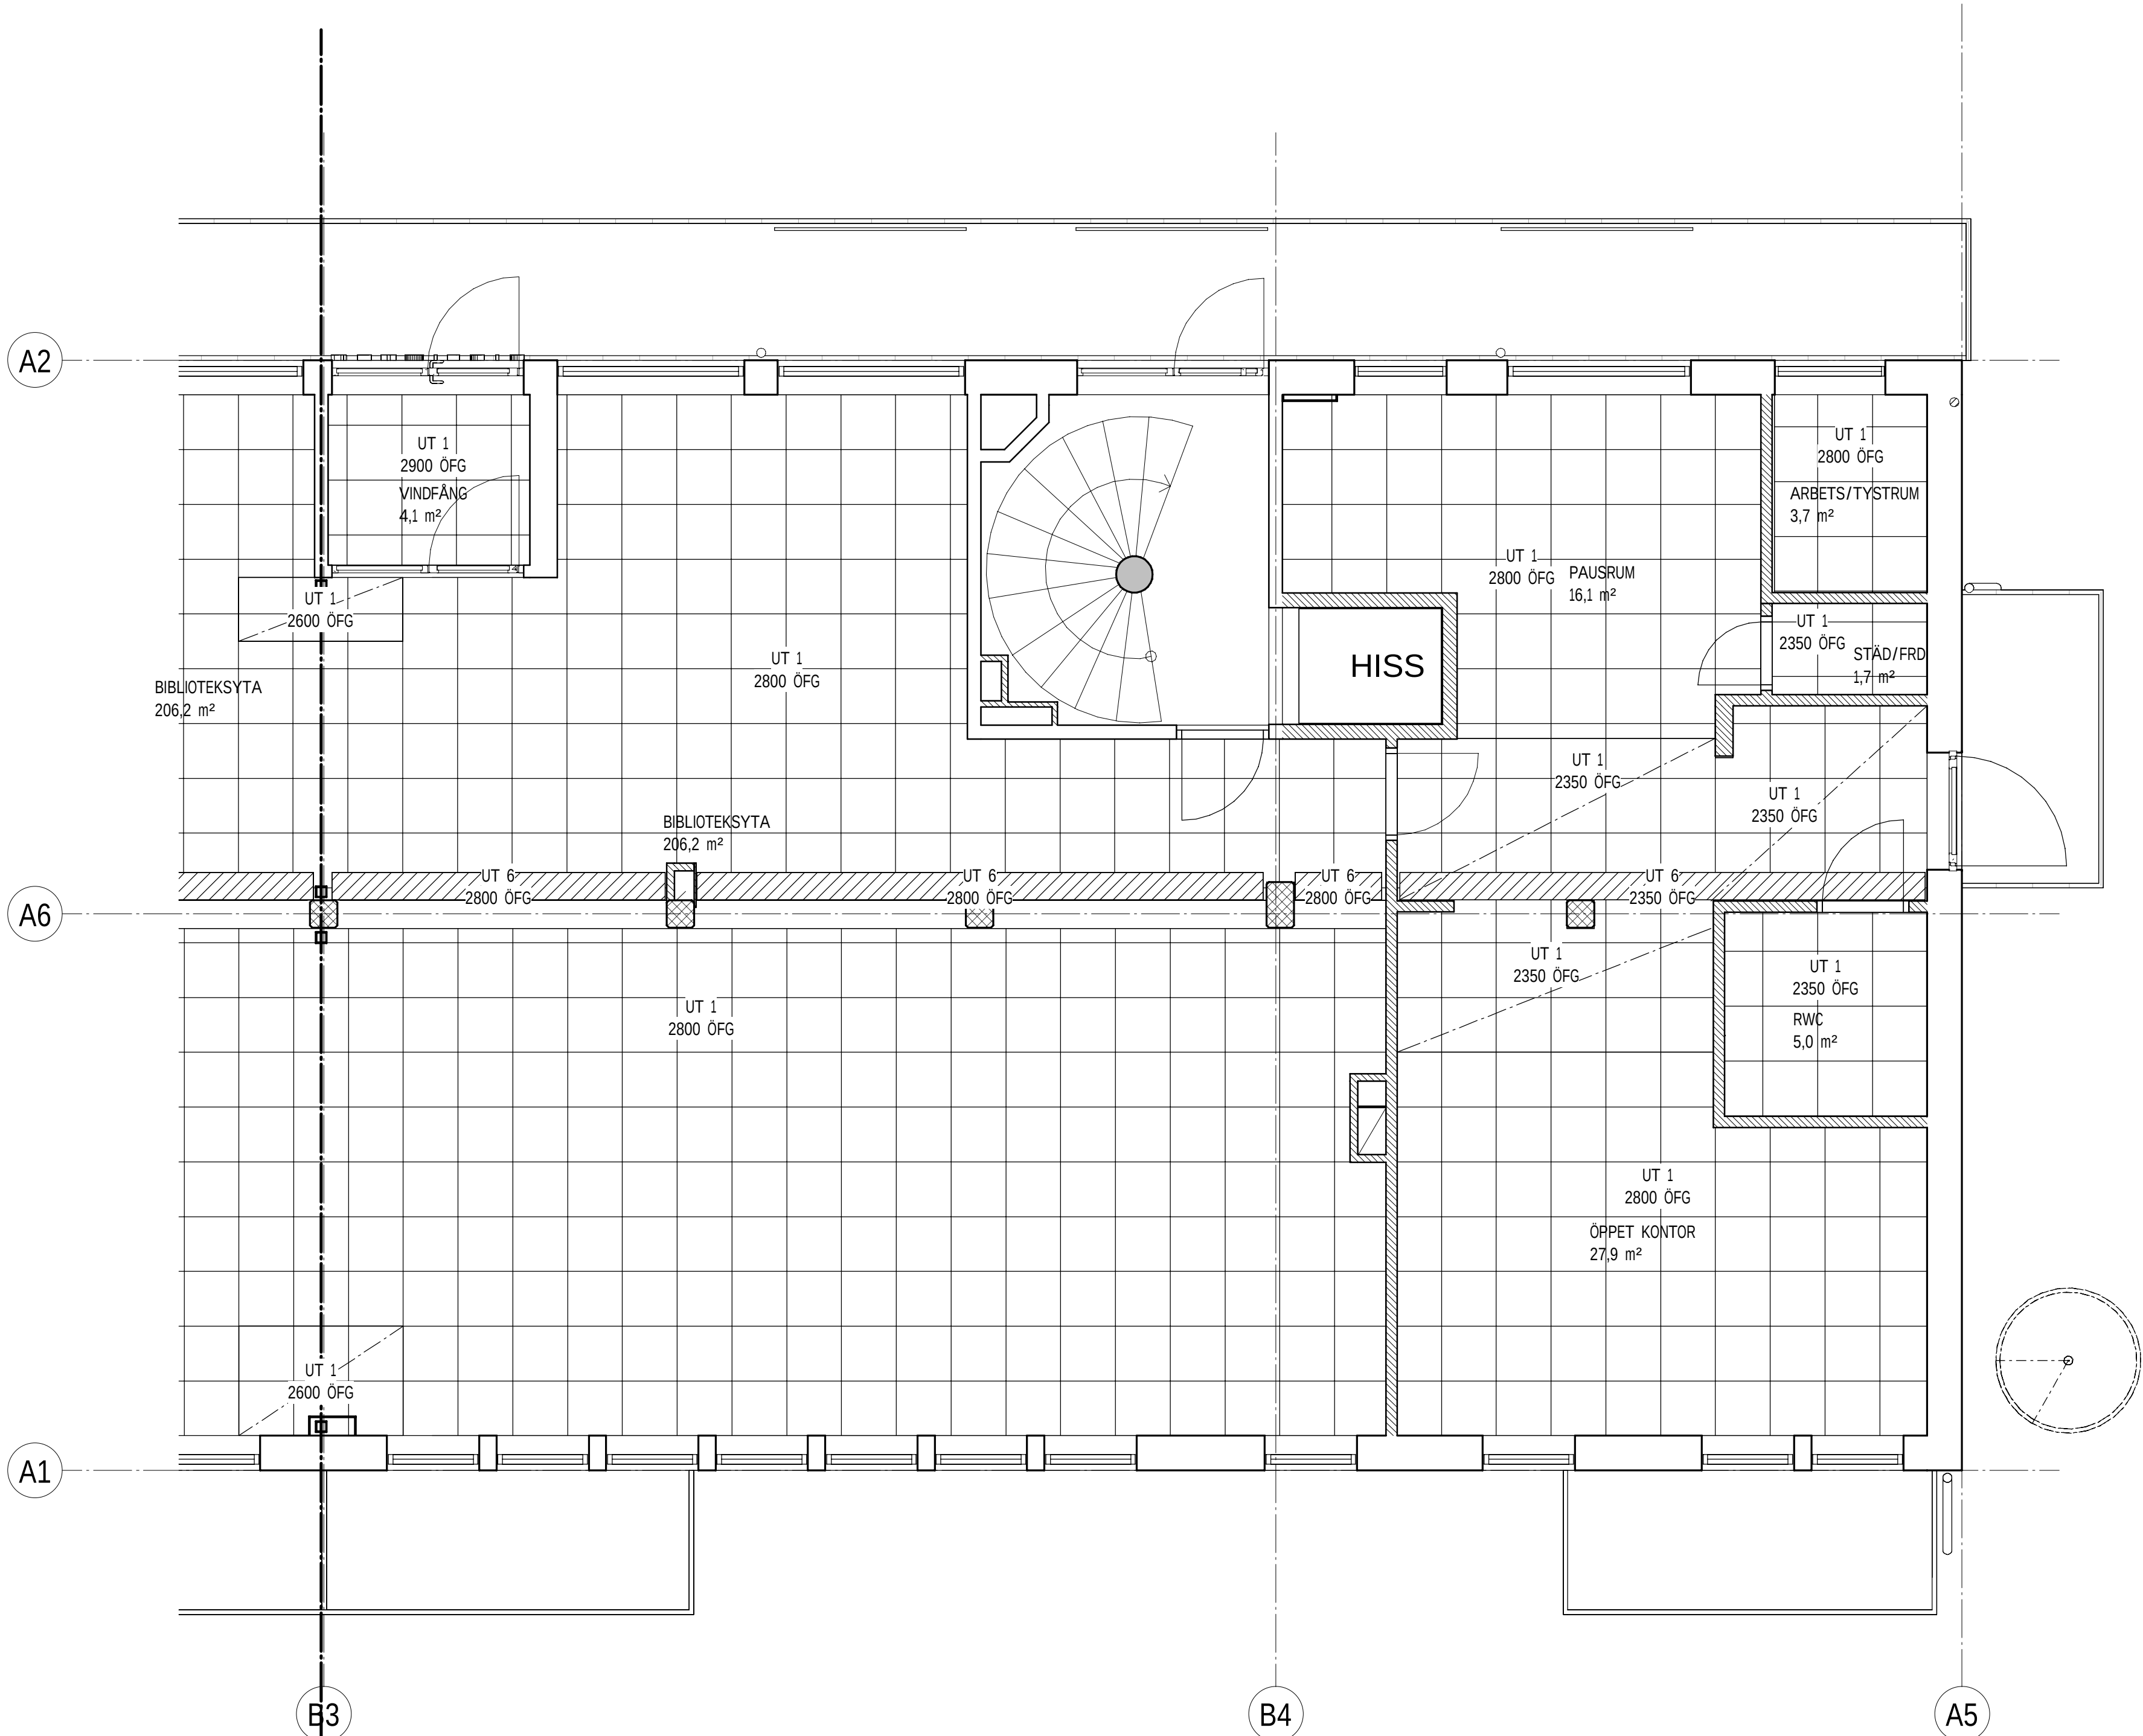

SKALA 1:50  
0 1 2 5  
METER