

MÅTT ANGES I MILLIMETER.
HÖJD TILL UNDERTAK AVSER MÅTT FRÅN FG.
TOTAL BYGGHÖJD AVSER UNDERTAKSKONSTRUKTIONENS TOTALA TJOCKLEK.
TOTAL KONSTRUKTIONSHÖJD AVSER
UNDERTAKSKONSTRUKTIONENS TOTALA TJOCKLEK INKL
FRITT/PENDLAT AVSTÅND TILL OVANLIGGANDE BJÅLKLAG.


+ 2,700 ÖFG PLUSHÖJD - ÖVER FÄRDIGT GOLV

VID MONTERING SAMORDNAS UNDERTAKET MED INSTALLATIONER.
INSTALLATIONER MONTERAS MED ERFODERLIGA
FÖRSTÄRKNINGAR ENLIGT FABRIKANTENS MONTAGEANVISNINGAR.

UT2:
DIKTMONTERAT GIPSTAK
TOTAL KONSTRUKTIONSHÖJD 69 MM.
28 MM GLESPANEL
28 MM GLESPANEL
13 MM GIPS
VID NIVÅSKILLNAD ANVÄNDS VERTIKAL GIPSSKIVA

UT4:
NEDPENDLAT GIPSTAK
TOTAL KONSTRUKTIONSHÖJD 40 MM.
27 MM GK-PROFIL
13 MM GIPS

UT6:
KABELRÄNNA ENL EL

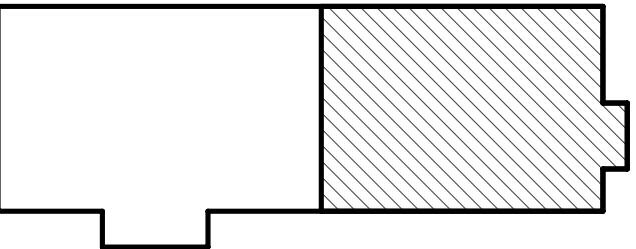

BET	ANDRING AVSER	DATUM	SIGN	STATUS
GRANSKNINGSHANDLING				
BYGGHANDLING				
DATUM 2025-02-26				
CENTRUMHUSET HUS D				
KRÅKAN 1, ROBERTSFORS				
				PROJEKT
				ANSVARIG PART
 AFRY				AFRY Ark Studio
S. Sjögren	KONTAKTPERSON	L.Grubbström	SKAPAD AV	
S. Sjögren	GÖKAND AV	210550	UPPRÄSSNINGSMÄN	
				RTINTEKSTÖR
OMBYGGNAD BIBLIOTEK OCH LÅGENHETER			INNEHÅLL	FORMAT
UNDERTAK PLAN 200 DEL 2			A1	SKALA
A-43-1-D202			1:50	BET
			NUMMER	

File: C:\Users\jmd534\OneDrive - AFRY\Documents\A-40-V-01_ludwig.grubbstrom.rvt

SKALA 1:50

0
METER