


Innerdörrar av trä/stål

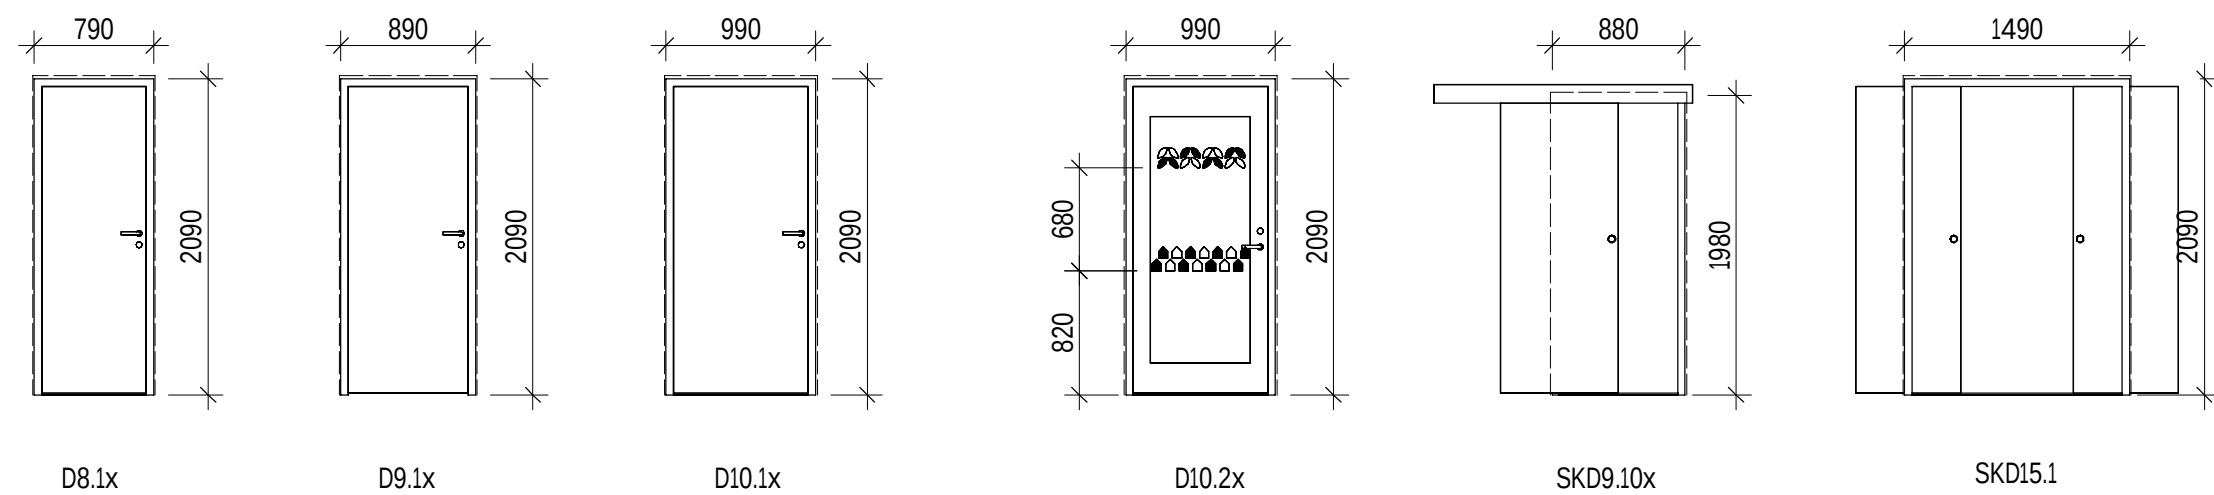

Littera	Hängning	Antal	ID	Brandklas s	Ljudkrav	7.Dörrblad	Ytbehandling/Kul ör	8.Glasöpp ning	11.Karm	12.Tröskel	14.Beslagskombination	15. Anmärkning
D8.10	H	1	Daloc T10			Massiv trädörr	Laminat F 7603 Bio-Oak liggnade		Trä	Tröskelplatta i hårdträ,typ B	7	
D8.11	H	1	Daloc T24		33	Massiv trädörr	Laminat F 7603 Bio-Oak liggnade		Trä	Våtrumströskel hårdträ, typ K	6	
D8.12	H	1	Daloc T10			Massiv trädörr	Laminat F 7603 Bio-Oak liggnade		Trä	Gummitröskel	7	
D9.10	H	8	Swedoor Easy			Lätt trädörr	Vit		Trä	Tröskelplatta i hårdträ,typ B	1	
D9.10	V	3	Swedoor Easy			Lätt trädörr	Vit		Trä	Tröskelplatta i hårdträ,typ B	1	
D9.11	H	2	Swedoor Easy			Lätt trädörr	Vit		Trä	Våtrumströskel hårdträ, typ V	2	
D9.11	V	3	Swedoor Easy			Lätt trädörr	Vit		Trä	Våtrumströskel hårdträ, typ V	2	
D9.13	H	1	Daloc T10			Massiv trädörr	NCS S9000-N		Trä	Fasad anslagströskel av hårdträ, typ G	7	
D10.10	H	2	Daloc T34	EI 30-S200	43	Massiv trädörr	Laminat F 7603 Bio-Oak Stående		Trä	Fasad anslagströskel av hårdträ, typ G	3	Mekanisk ringklocka, Dörröga
D10.10	V	3	Daloc T34	EI 30-S200	43	Massiv trädörr	Laminat F 7603 Bio-Oak Stående		Trä	Fasad anslagströskel av hårdträ, typ G	3	Mekanisk ringklocka, Dörröga
D10.11	V	2	Daloc T24		33	Massiv trädörr	Laminat F 7603 Bio-Oak liggnade		Trä	Mekanisk tätningströskel, utan tröskelplatta	5	
D10.13	V	1	Daloc T25	EI 30-S200C		Massiv trädörr	Laminat F 7603 Bio-Oak liggnade		Trä	Fasad anslagströskel av hårdträ, typ G	10	
D10.14	V	1	Daloc T24		33	Massiv trädörr	Laminat F 7603 Bio-Oak liggnade		Trä	Tröskelplatta i hårdträ med släplist	7	
D10.15	H	1	Daloc T15	EI 30-S200C		Massiv trädörr	Laminat F 7603 Bio-Oak liggnade		Trä	Fasad anslagströskel av hårdträ, typ G	13	
D10.20	H	1	Daloc T25		38	Massiv trädörr	Laminat F 7603 Bio-Oak liggnade	Typ 01	Trä	Tröskelplatta i hårdträ med släplist	11	Kontrastmarkering enl uppställning
D10.21	V	1	Daloc T25		38	Massiv trädörr	Laminat F 7603 Bio-Oak liggnade	Typ 01	Trä	Tröskelplatta i hårdträ med släplist	8	Kontrastmarkering enl uppställning
SD10.11	H	1	Daloc S30	EI60C		Ståldörr	NCS S9000-N		Stål	Tröskelplatta i stål med släplist	12	
SKD9.10	V	1	SSC Solid		33	Massiv trädörr	Laminat F 7603 Bio-Oak liggnade		Trä	Solid mekanisk tröskel	9	
SKD15.1		1	Swedoor Easy skjutdörr			Lätt trädörr	Vit		Trä		4	Integrerad parskjutdörr
ÖK10.10 Grand total		2 37	<varies>									Karmofattning M10x21 av 19mm Vitlackad MDF

Beslagspaket

1. 14.2: LÅSHUS 2014 HÖ/VÅ
14.3: TRYCKE 5614 INKL NYCKELSKYLTT MATTKROM
2. 14.2: LÅSHUS 2014 HÖ/VÅ
14.3: TRYCKE 5614 INKL WC BEHÖR MATTKROM
3. 14.2: LÅSHUS 510-50
14.3: TRYCKE 6696 MATTKROM
14.8: ÖVRIGA CYLINDERBEHÖR M.M I MATTKROM
4. 14.2: DRAGRING STAINLESS
14.3: OVALT SKÅLHANDTAG STAINLESS
5. 14.2: LÅSHUS ASSA 310-50
14.3: TRYCKE 6696 MATTKROM INKL WC BEHÖR 9265 MATTKROM DRAGHANDTAG BB 815 BORSTAT ROSTFRITT STÅL
INSIDA DÖRR FG+800
6. 14.2: LÅSHUS ASSA 310-50
14.3: TRYCKE 6696 MATTKROM INKL WC BEHÖR 265 MATTKROM
7. 14.2: LÅSHUS ASSA 310-50
14.3: TRYCKE 6696 MATTKROM INKL CYLINDERBEHÖR UTSIDA VRED INSIDA MATTKROM
8. 14.2: LÅSHUS ASSA 310-50
14.3: TRYCKE 6696 MATTKROM INKL TÄCKBRICKA UT/INSIDA
9. 14.2: LÅSHUS ASSA 311-50
14.3: ROCA SKÅLHANDTAG 120 ROSTFRITT STÅL
10. 14.2: LÅSHUS ASSA 410-50
14.3: TRYCKE 6696 MATTKROM DUBBELCYLINDER INKL CYLINDERBEHÖR UTSIDA OCH INSIDA
14.6: DÖRRSTÅNGARE DC310 MED FÖRDRÖJD STÅNGNING
11. 14.2: LÅSHUS ASSA 710-50 + ASSA 179
14.3: TRYCKE 6696 MATTKROM INKL CYLINDERBEHÖR ANSLAGSSIDA VRED GÅNGJÄRNSSIDA
12. 14.2: LÅSHUS ASSA 310-50
14.3: TRYCKE 6696 MATTKROM INKL CYLINDERBEHÖR ANSLAGSSIDA VRED GÅNGJÄRNSSIDA
14.6: DÖRRSTÅNGARE DC310 MED FÖRDRÖJD STÅNGNING
13. 14.2: LÅSHUS ASSA 310-50
14.3: TRYCKE 6696 MATTKROM INKL TÄCKBRICKA UT/INSIDA
14.7: DÖRRÖPPNARE SW300 + SENSORLISTER
STYRS VI AK x2
ELSLUTBECK STEP KOPPLAS MOT DÖRRAUTOMATIK
KANALISATION FÖR EL MED 6M FÖRDRAGEN LEDNING

FÖRKLARINGAR

ALLMÄNT:
MÅTT SÅKA KONTROLLERAS OCH SAMORDNAS INNAN TILLVERKNING
PÅBÖRJAS.
MÅTT ANGES I MILLIMETER (MM) OCH/ELLER MODULMÅTT (M).
MÅTTA HÖJD- OCH BREDDMÅTT AVSER KARMYTTERMÅTT (KYM).
DETALJMÅTT ENLIGT DETALJRITNINGAR.
DÖRRAR SES FÄRN GÅNGJÄRNSIDAN.
MÅTTSÄTTNING AV GLASÖPPNINGAR AVSER GLASFASLMÅTT.
DÖRRAR DRUVAS OCH FOGAS.

HÄNGNING:
V=VÄNSTERHÄNGD
H=HÖGERHÄNGD
FÖR PARDÖRRAR AVSER HÄNGNING GÅNGDÖRR/AKTIVT
DÖRRBLAD.

KANTNUMMER ANGER:

4. DÖRRTYP

6. FUNKTIONSKRAV
6.1 BRANDKRAV: ENLIGT TABELL
6.2 LJUDKRAV: ENLIGT TABELL

7. MATERIAL DÖRRBLAD

8. GLASÖPPNING

8.1 ENLIGT TYPISKISSER

11. MATERIAL KARM

12. TRÖSKEL

14. BESLAGSKOMBINATION
14.2: LÅSTYP
14.3: TRYCKE, DRAGHANDTAG, TRYCKPLATTA
14.6: DÖRRSTÄNGARE
14.7: EL-SLUTBLECK, PASSAGESYSTEM
14.8: ANMÄRKNING/ÖVRIGT

FÖRESKRIFTER

DÖRREGENSKAPER:
DÖRRAR SKA LEVERERAS FÄRDIGMÅLADE/LAMINERADE/FANERADE
ENLIGT UPPSTÄLLNING
DÖRRAR UTFÖRAS MED TYPGODKÄND KLÄMSKYDD ENLIGT
TILLVERKARENS STANDARD.

KLASSINDELNING OCH FORDRINGAR:
DÖRRAR SKA VARA TYPGODKÄNDA I ERFORDERLIG BRAND-, LJUD-
OCH INBROTTSKLASS OCH UTFÖRAS ENLIGT ANGIVNA KLASSE.

MÄRKNING:
DÖRRAR SKA VARA P- OCH/ELLER CE-MÄRKTA OCH HA 10-ÅRS
GARANTI.
GODS SKA MÄRKAS MED LITTERA ENL. UPPSTÄLLNING. DÖRRARNA
SKA MÄRKAS MED UPPGIFT OM LITTERA, TILLVERKARE,
TILLVERKNINGSÅR SAMT I FÖREKOMMANDE FALL
TYPGODKÄNNANDESKYLT FÖR BRAND-, LJUDISOLERING- OCH
INBROTTSKLASS.

TÄTNINGSLISTER:
TÄTNINGSLISTER ENLIGT TILLVERKARENS STANDARD.
LISTEN SKALL VARA MONTERAD TILL KARM VID LEVERANS TILL
BYGGPLATSEN.

GLASNING:
GLASNING UTFÖRS ENLIGT MTK:S ANVISNINGAR FÖR BLA.
MONTERING, BRAND OCH SÄKERHETSKRAV. PERSONSÄKERHET
ENL. BBR 8:35
SKYDD MOT SKÄRSKADOR OCH SAMMANSTÖTNING.
ÖVRIGA KRAV ENLIGT UPPSTÄLLNING.

GENERELLT:

- FÖRESKRIFTER 1-17 GÄLLER GENERELLT FÖR ALLA DÖRRAR.
- AVVIKELSE FRÅN GENERELLA FÖRESKRIFTER ANGES I KLARTEXT UNDER RESPEKTIVE UPPSTÄLLNING.
- DÅR KANTNUMMER UNDER RESP UPPSTÄLLNING FÖLJS AV ETT STRECK (-) INGÅR INTE EGENSKAPEN / KRAVET FÖR DÖRREN.

SET	ÄNDRING AVSER	DATUM	SIGN	STATUS
GRANSKNINGSHANDLING				
BYGGHANDLING				
INOM 2025-02-26	ÄNDRING			
CENTRUMHUSET HUS D				
KRÅKAN 1, ROBERTSFORS				
ANSVARIG PART				
 AFRY		AFRY Ark Studio		
J. Sjögren	KONTAKTPERSON	L.Grubbström	SKAPAD AV	
J. Sjögren	GÖRKÄND AV	210550	UPPDRAGSNUMMER	
DMBYGGNAD BIBLIOTEK OCH LÄGENHETER		INNEHÅLL	RITNINGSGRUPP	
INNERDÖRRAR		A1	FORM	
A-43-4-01		1:50	SKALA	
		NUMMER	BE	

