



Nya utvändiga glaspartier vån 100

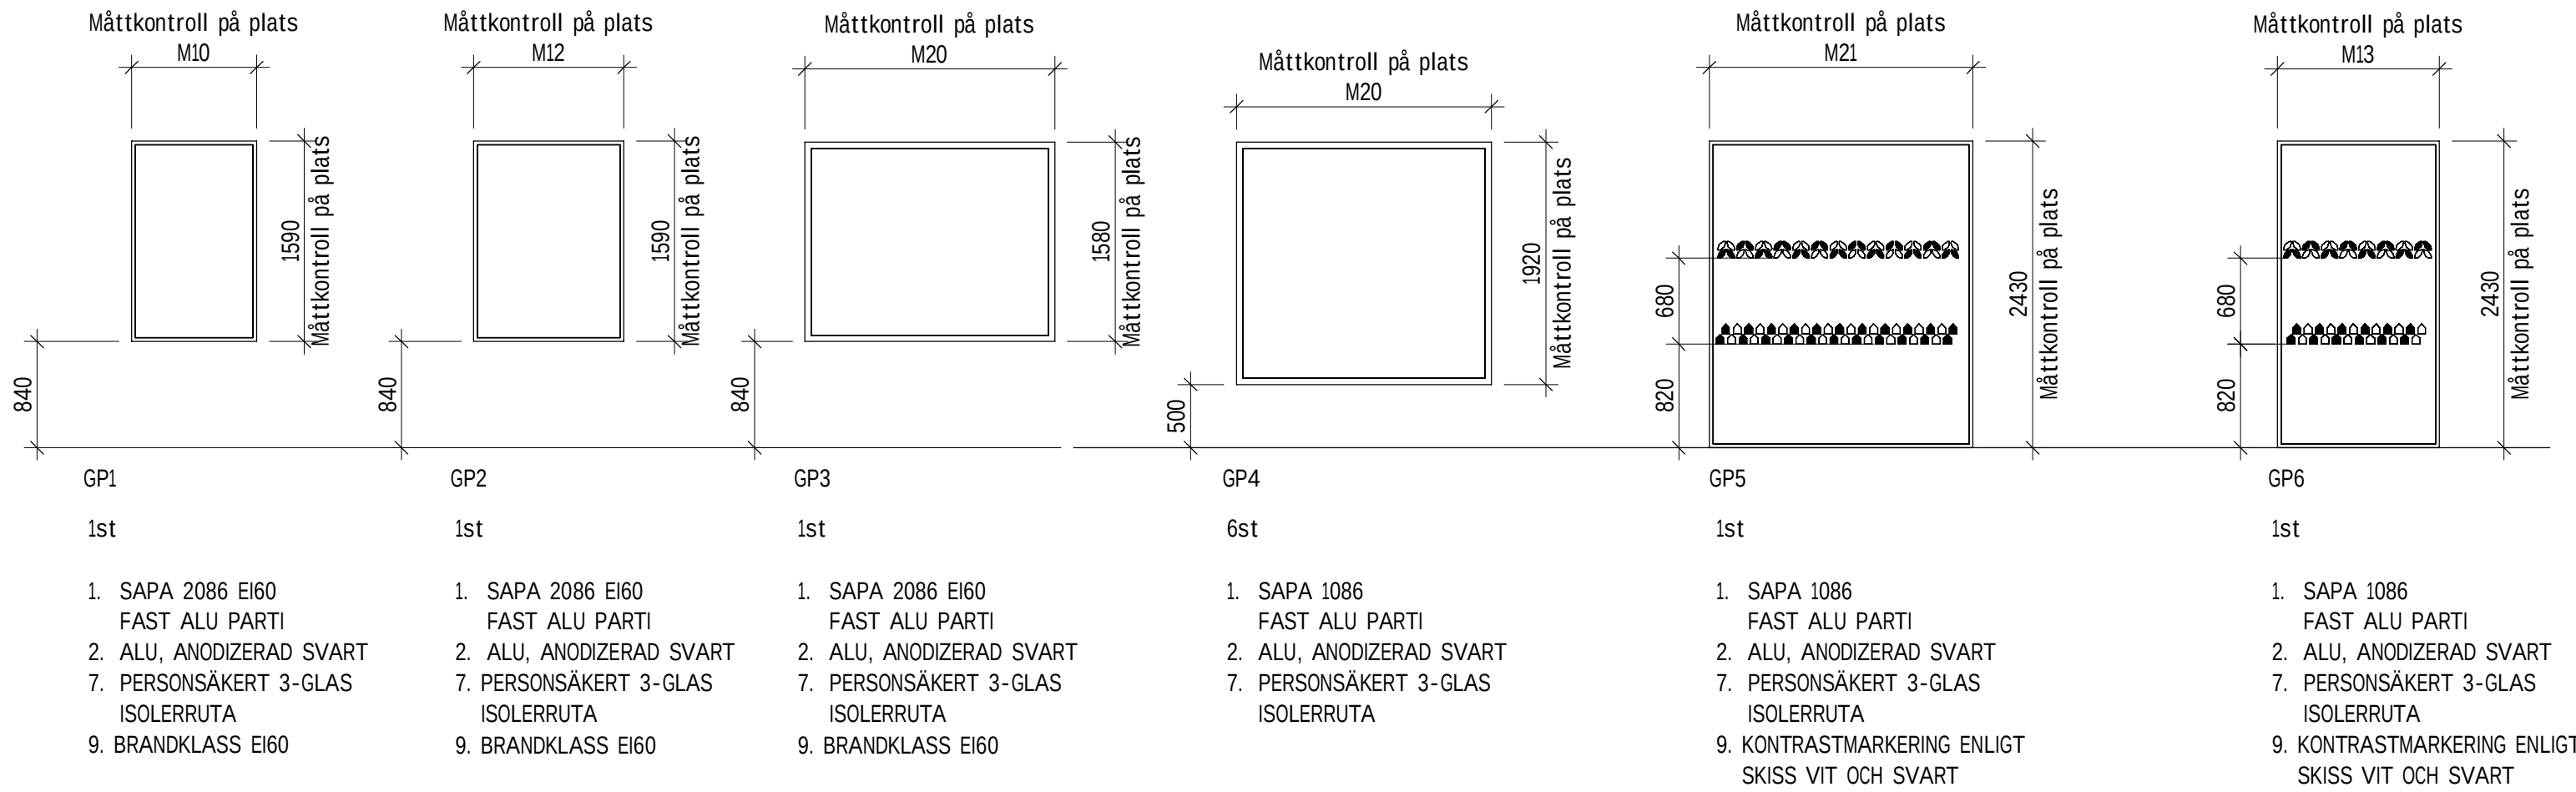

Nya fönster invändigt våning 100

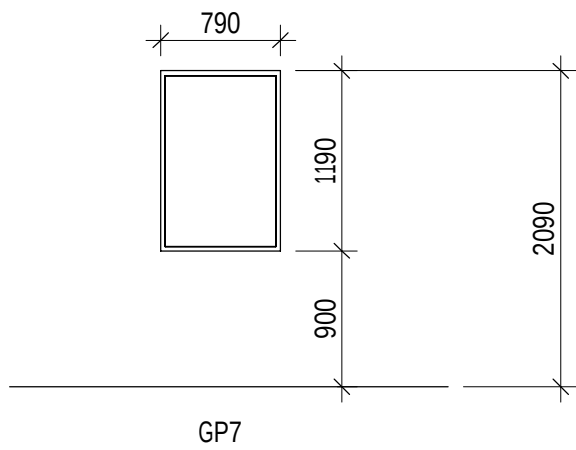

- 1st
1. SAPA 1086 FAST ALU PARTI
 2. ALU, ANODIZERAD SVART
 7. PERSONSÅKERT 3-GLAS ISOLERRUTA

FÖRKLARINGAR

ALLMÄNT:
MÄTT SKA KONTROLLERAS OCH SAMORDNAS INNAN TILLVERKNING PÅBÖRJAS.
MÄTT ANGES I MILLIMETER (MM) OCH/ELLER MODULMÄTT (M).
TOTALA HÖJD- OCH BREDDMÄTT AVSER KARMYTTERMÄTT (KYM).
GLASPARTIER SES FRÅN UTSIDAN.
MÄTTSÄTTNING AV GLASÖPPNINGAR AVSER GLASFALSMÄTT.
GLASPARTIER DREVAS OCH FOGAS.

GLASPARTITYPER
GP GLASPARTIER AV ALUMINIUM

FÖRESKRIFTER

GLASPARTIEGENSKAPER:
GLASPARTIER SKA TILLVERKAS AV ALUMINIUM PROFILER ENLIGT TILLVERKARENS STANDARD.

KLASSINDELNING OCH FÖRDRINGAR:
GLASPARTIER SKA VARA TYPGODKÄNDA I ERFORDERLIG BRAND-, LJUD- OCH INBROTTSKLASS OCH UTFÖRAS ENLIGT ANGIVNA KLASSER.

MÄRKNING:
GLASPARTIER SKA VARA P- OCH/ELLER CE-MÄRKTA OCH HA 10-ÅRS GARANTI.
GODS SKA MÄRKAS MED LITTERA ENL. UPPSTÄLLNING.
GLASPARTIER SKA MÄRKAS MED UPPGIFT OM LITTERA, TILLVERKARE, TILLVERKNINGSÅR SAMT I FÖREKOMMANDE FALL TYPGODKÄNNANDESKYLT FÖR BRAND-, LJUDISOLERING- OCH INBROTTSKLASS.

TÄTNINGSLISTER:
TÄTNINGSLISTER ENLIGT TILLVERKARENS STANDARD.

GLASNING:
GLASNING UTFÖRS ENLIGT MTK:S ANVISNINGAR FÖR BLA. MONTERING, BRAND OCH SÄKERHETSKRAV. PERSONSÄKERHET ENL. BBR 8:35.
PERSONSÄKERHETSGLAS ENLIGT EN 12600.
SKYDD MOT SKÅRSKADOR OCH SAMMANSTÖTNING.
ÖVRIGA KRAV ENLIGT UPPSTÄLLNING.

GENERELLT:
• FÖRESKRIFTER 1-17 GÄLLER GENERELLT FÖR ALLA PARTIER.
• AVVIKELSE FRÅN GENERELLA FÖRESKRIFTER ANGES I KLARTEXT UNDER RESPEKTIVE UPPSTÄLLNING.
• DÅR KANTNUMMER UNDER RESP UPPSTÄLLNING FÖLJS AV ETT STRECK (-) INGÅR INTE EGENSKAPEN / KRAVET FÖR GLASPARTIET.

1. SORT/TYP
2. MATERIAL KARM
3. MATERIAL DÖRRBLAD/BÄGE
4. MATERIAL TRÖSKEL
5. KARMDIMENSION
6. URTAG
7. GLAS
8. FYLLNING
9. ÖVRIGT

BET	ÄNDRING AVSER	DATUM	SIGN	STATUS
GRANSKNINGSHANDLING				
BYGGHANDLING				
2025-02-26		ÄNDRING		
CENTRUMHUSET HUS D				
KRÅKAN 1, ROBERTSFORS				
 AFRY				ANSVARIG PARTI
AFRY Ark Studio				
J. Sjögren	KONTAKTPERSON	L.Grubbström	SKAPAD AV	
J. Sjögren	GÖKÄND AV	210550	UPPDRAGSNUMMER	
				RTNINGSKATEGORI
ÖMBYGGNAD BIBLIOTEK OCH LÄGENHETER			INNEHÅLL	FORMAT
GLASPARTIER			1:50	SKALA
A-43-4-02			NUMMER	BET

SKALA 1:50

