




- IV01
- 13mm Normalgips
 - 12mm Plywood
 - 70mm Multiregel
 - 12mm Plywood
 - 13mm Normalgips

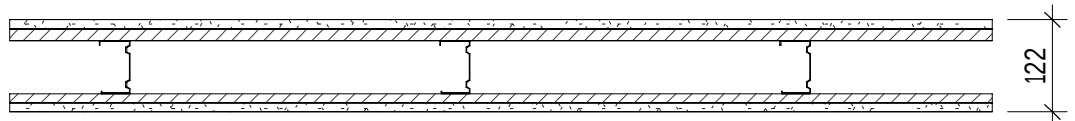


- IV02
- 12,5mm Normalgips
 - 15mm Plywood
 - 70mm Multiregel
 - 12mm Plywood
 - 12,5mm Normalgips

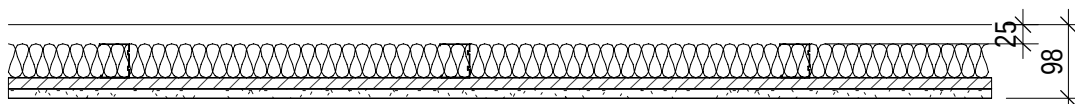


- IV03
- Befintlig vägg
- 25mm Luftspalt
 - 45mm Multiregel
 - 45mm Mineralull
 - 15mm Plywood
 - 12,5mm Normalgips

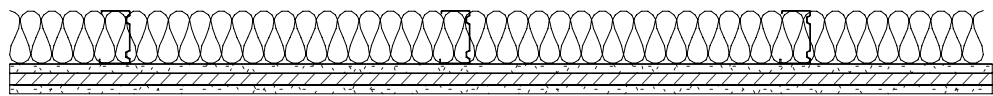


- IV04
- 70mm Multiregel
 - 70mm Mineralull
 - 13mm Normalgips
 - 15mm Plywood
 - 13mm Normalgips

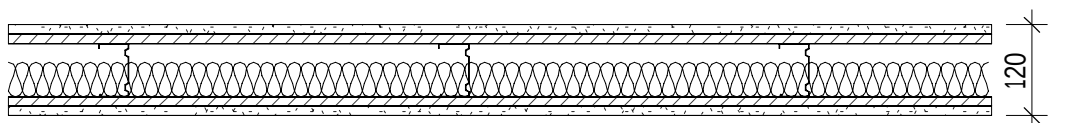


- IV05
- 13mm Normalgips
 - 12mm Plywood
 - 70mm Multiregel
 - 45mm Mineralull
 - 12mm Plywood
 - 13mm Normalgips

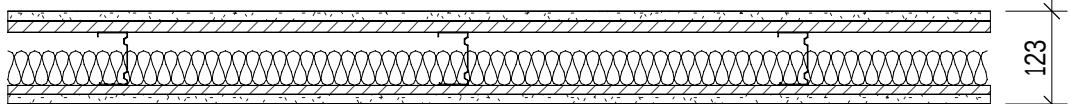


- IV06
- 13mm Normalgips
 - 15mm Plywood
 - 70mm Multiregel
 - 45mm Mineralull
 - 12mm Plywood
 - 13mm Normalgips

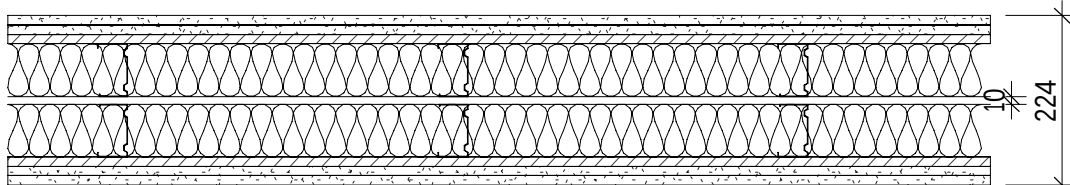


- IV07
- 12,5mm Normalgips
 - 12,5mm Normalgips
 - 12mm Plywood
 - 70mm Multiregel
 - 70mm Mineralull
 - 10mm Luftspalt
 - 70mm Multiregel
 - 70mm Mineralull
 - 12mm Plywood
 - 12,5mm Normalgips
 - 12,5mm Normalgips

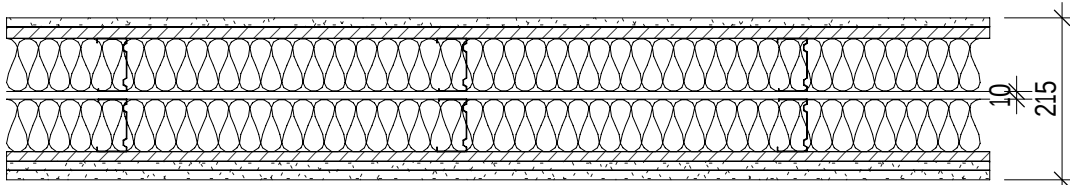


- IV08
- 12,5mm Normalgips
 - 15mm Plywood
 - 70mm Multiregel
 - 10mm Luftspalt
 - 70mm Multiregel
 - 12mm Plywood
 - 12,5mm Normalgips
 - 12,5mm Normalgips

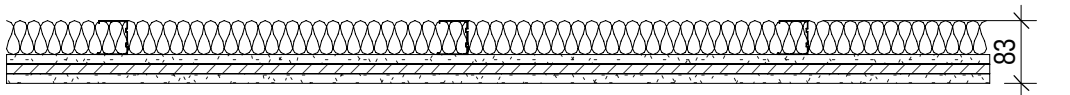


- IV09
- 45mm Multiregel
 - 45mm Mineralull
 - 13mm Normalgips
 - 12mm Plywood
 - 13mm Normalgips

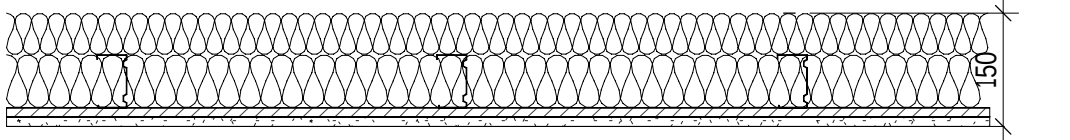

- IV10
- 55mm Mineralull
 - 70mm Multiregel
 - 70mm Mineralull
 - 12,5mm Plywood
 - 12,5mm Normalgips

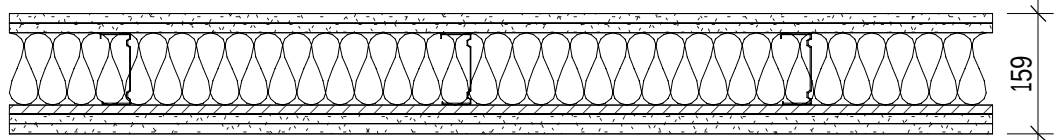


- IV11
- 13mm Normalgips
 - 13mm Normalgips
 - 95mm Multiregel
 - 95mm Stenull
 - 12mm Plywood
 - 13mm Normalgips
 - 13mm Normalgips

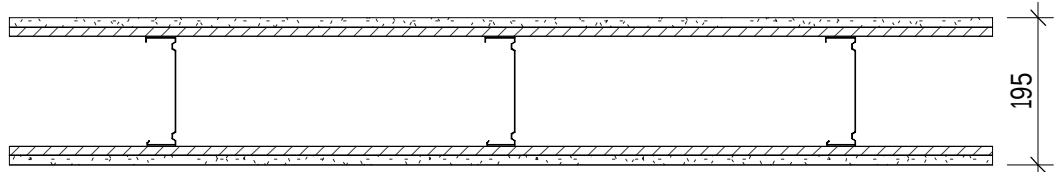

- IV12
- 13mm Normalgips
 - 12mm Plywood
 - 145mm Multiregel
 - 12mm Plywood
 - 13mm Normalgips

- IV13
- 13mm Normalgips
- SKILJEVÄGG INOM VVS SCHAKT
- HÖRNPROFIL H50/50 ALTERNATIVT 45 MULTIREGEL

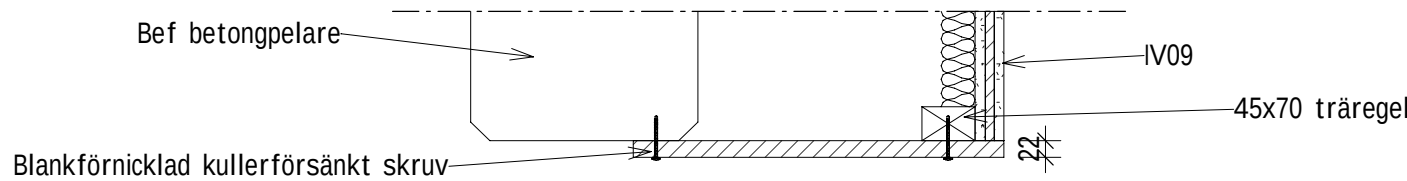

- IV14
- 22mm MDF-Board Fabrikslackerad enl färgsättning
- Demonterbar el-nisch front
- Samtliga kanter på skivor ska utföras fasade ca 4 mm
- Skivorna ska levereras förborrade för infästning
- Skiva ska passera undertak i höjddled

FÖRESKRIFTER

Innervägssystem enl. Gyproc eller likv.

För generella detaljer, som anslutningar mot golv - tak - övr. Konstruktioner / utförande hörnt-hörn gäller detaljer i fabrikantens handböcker.

Vägg ovan öppningar för komponenter skall utföras lika intilliggande vägg, dock med FR-skena mot öppning.

Vägghänvisningar är ett hjälpmedel, en väggtyp kan förekomma på flera ställen.

Förstärkningar

För större ursparingar, håltagningar, avvaxlingar od. -utförs med förstärkningsreglar.

Inspektionssluckor

Luckor typ hila monteras i omfattnin installationsritningar. Kulör efter färgsättning.

Vid brandklassade väggar av gips skall inspektionssluckan utföras i samma brandklass, ex HILA A 60, el. Likv.

Brandklassning

Se planritningar för brandkrav. Väggar ska utföras i brandklass enl brandskyddsbeskrivning och brandcellsindelning på brandskyddsritningar. Genomföringar ska tätas med värmeexpanderande fogmassa. Stenull används som isolering i ventschakt.

Ljudklassning

Ljudklass Rw avser klassning som vägguppbyggnad uppfyller.

Väggar med ljudkrav lika eller högre än 44dB ska spåras enl ljuddok

Ljudklass C gäller

BET	ÄNDRING AVSER	DATUM	SIGN	STATUS
GRANSKNINGSHANDLING				
BYGGHANDLING				
ÄNDRING 2025-02-26		ÄNDRING		
CENTRUMHUSET HUS D		PROJEKT		
KRÅKAN 1, ROBERTSFORS		ANSVARIG PART AFRY Ark Studio		
 AFRY				
J. Sjögren	KONTAKTPERSON	L.Grubbström	SKAPAD AV	
J. Sjögren	GODKÄND AV	210550	UPPERAGSNUMMER	
RITNINGSKATEGORI				
OMBYGGNAD BIBLIOTEK OCH LÄGENHETER		INNEHÅLL	A1	FORMAT
INNerväggstyper och detaljer			1:10	SKALA
A-43-6-01		NUMBER		BET

