



KÖKSUPPSTÄLLNINGAR LÄGENHETER PLAN 200


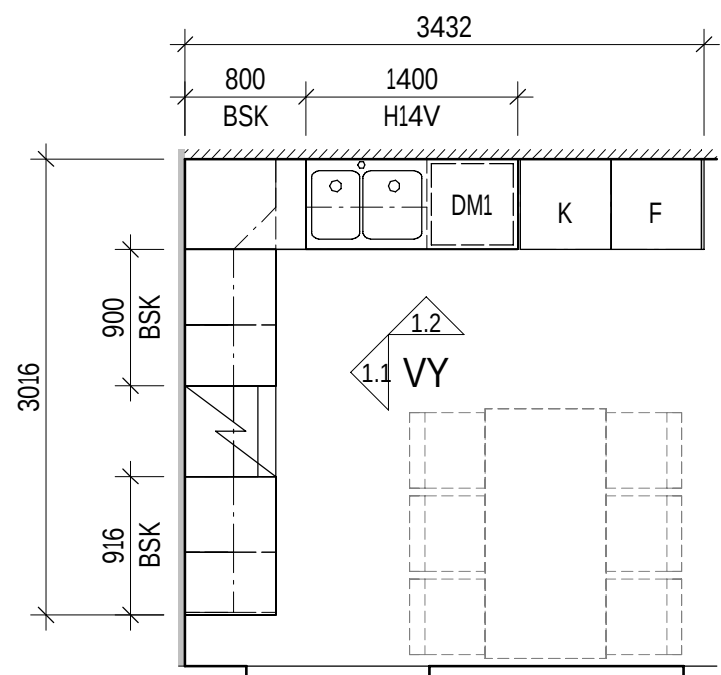


1101.

1.1.

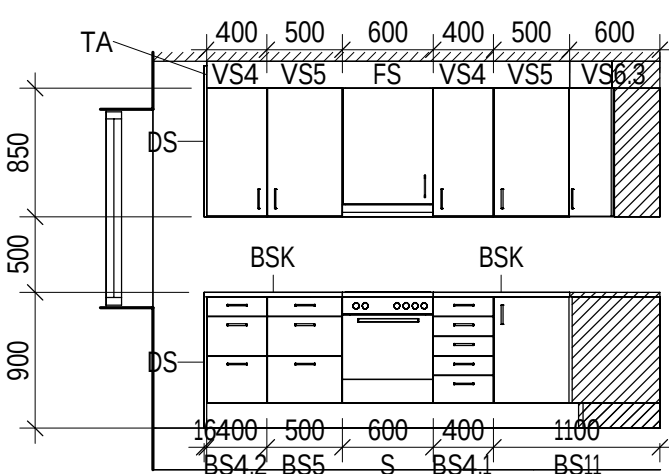


1.2.

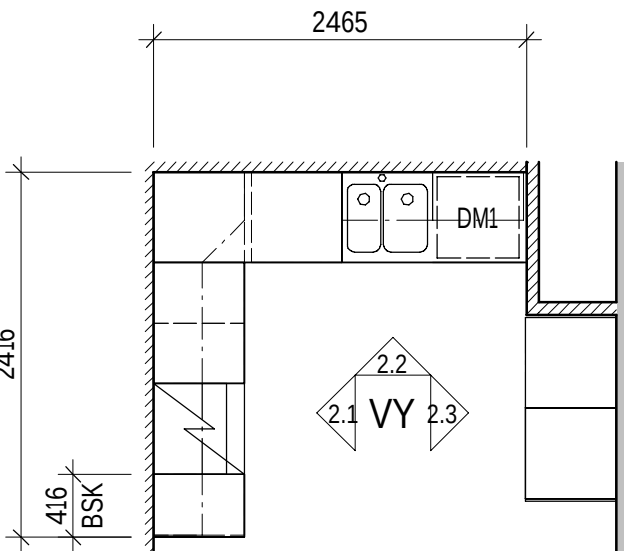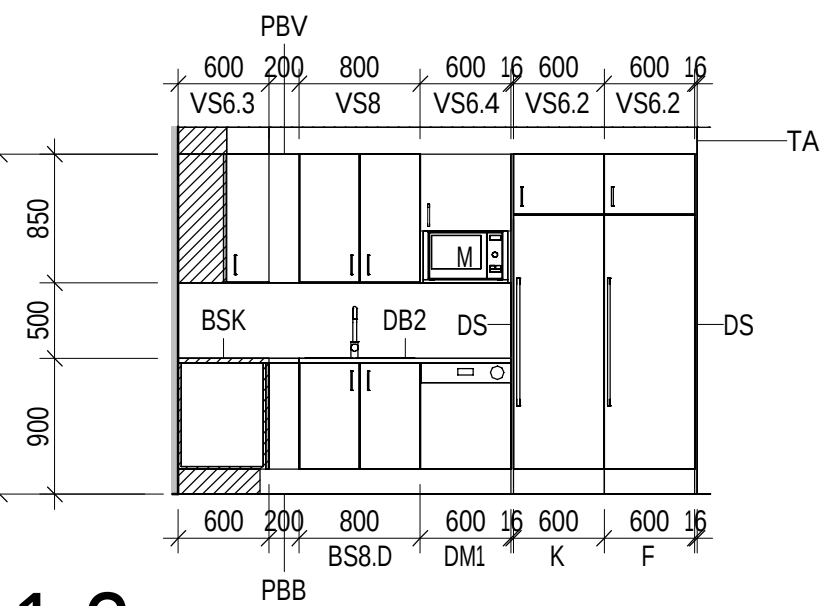


1102.


2.1.

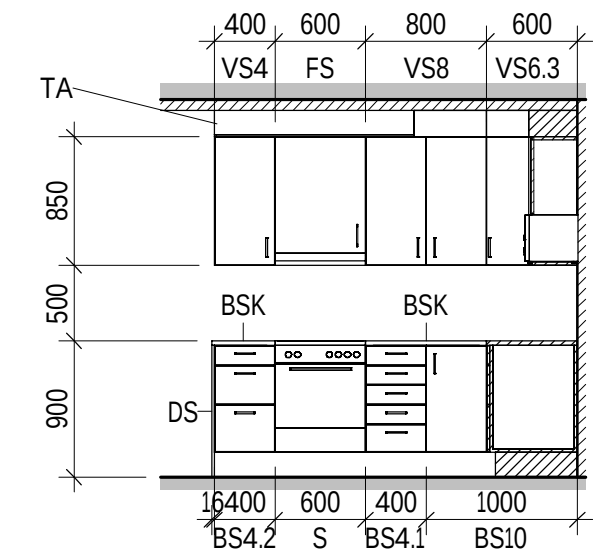


2.2.

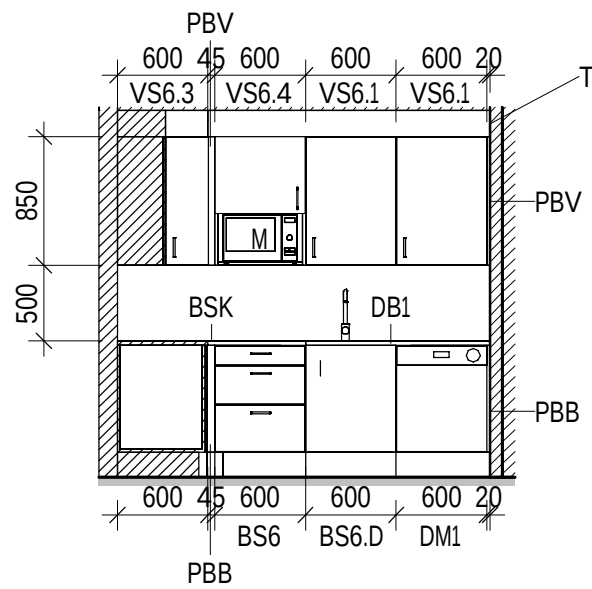


2.3.

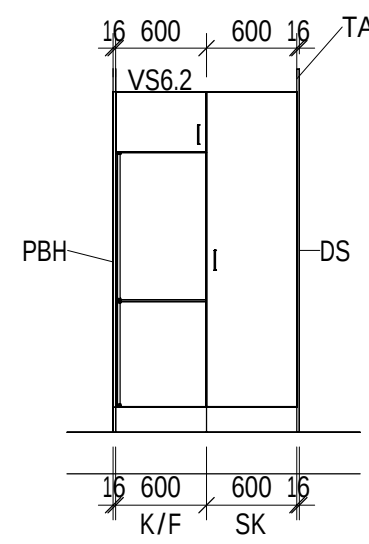


PENTRY UPPSTÄLLNINGAR PLAN 100

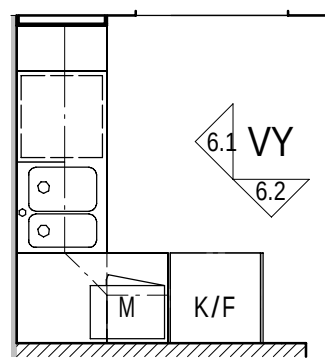


Personalrum.

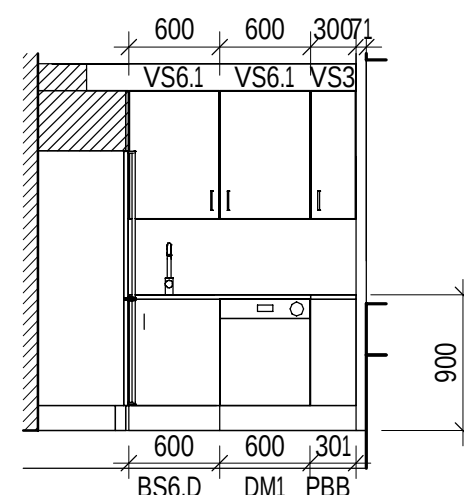

6.1.


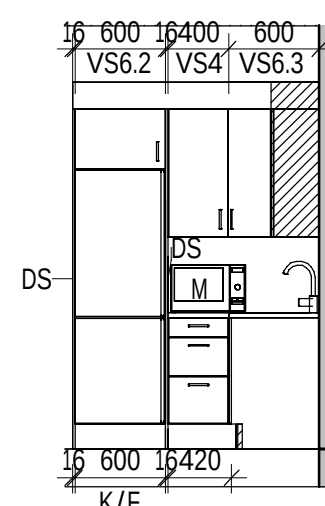


6.2.

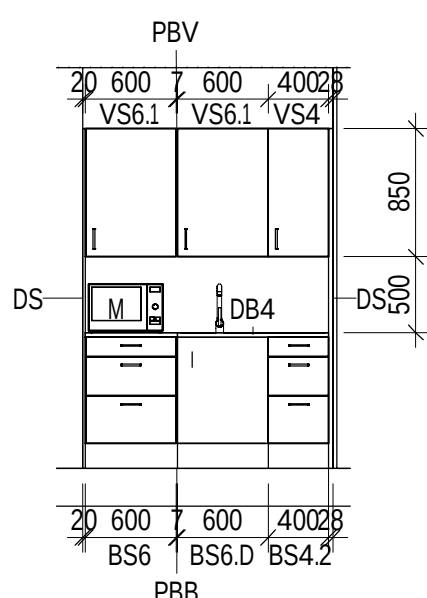


7.1.

Bibliotek.

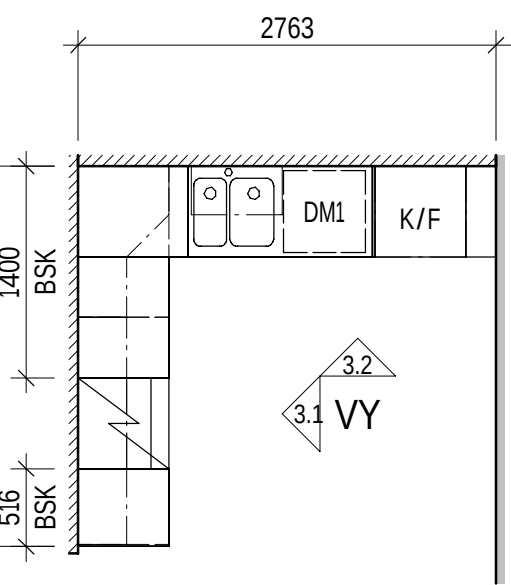
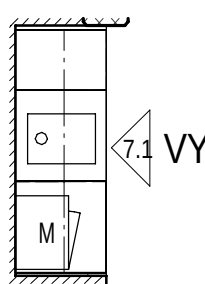


1103.

3.2.

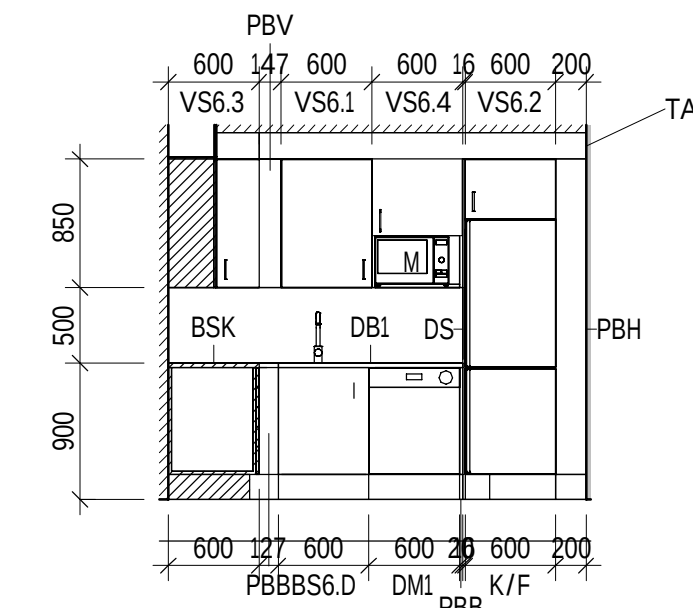


3.1.

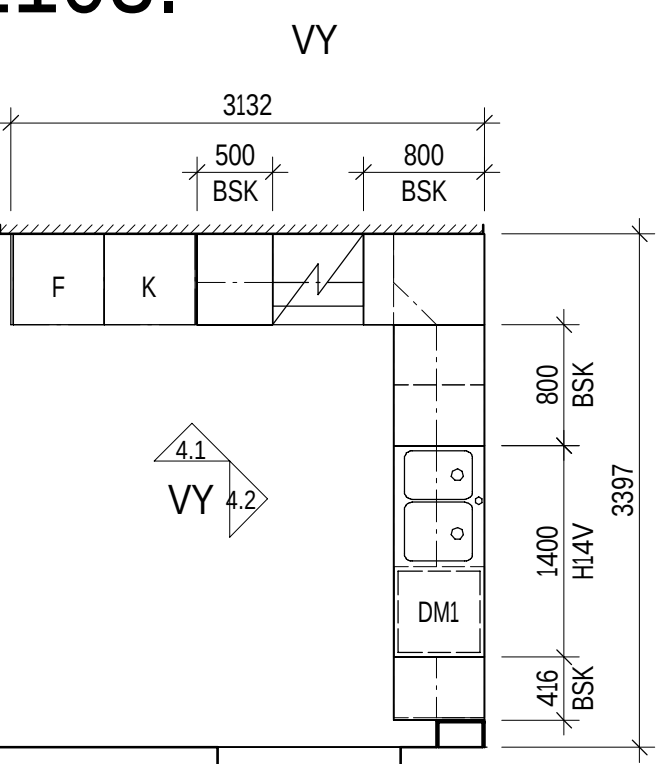
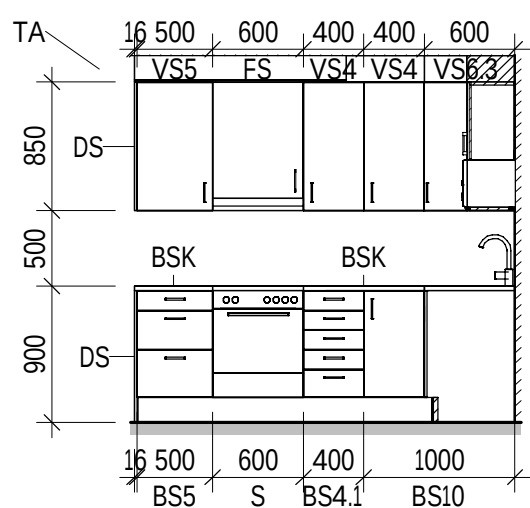


1104.

4.1.

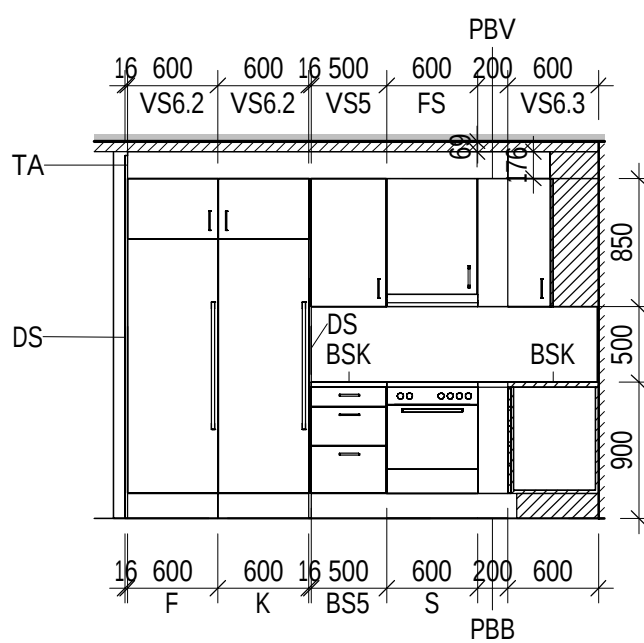


4.2.

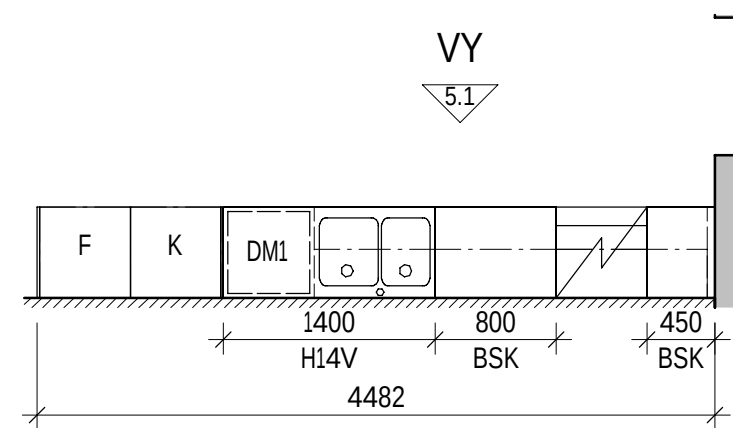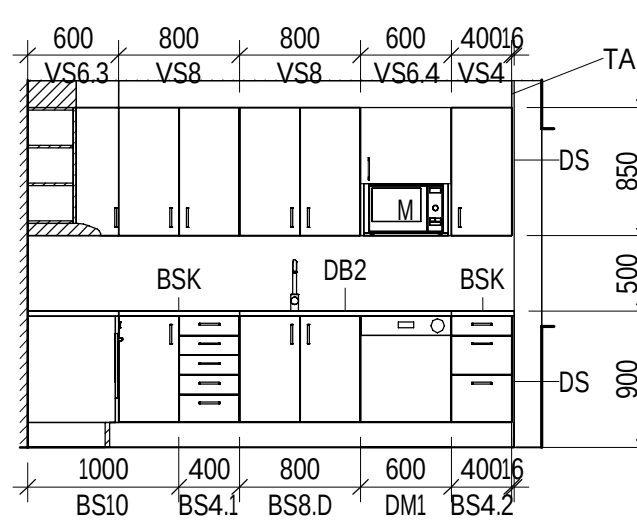

1105.

5.1.

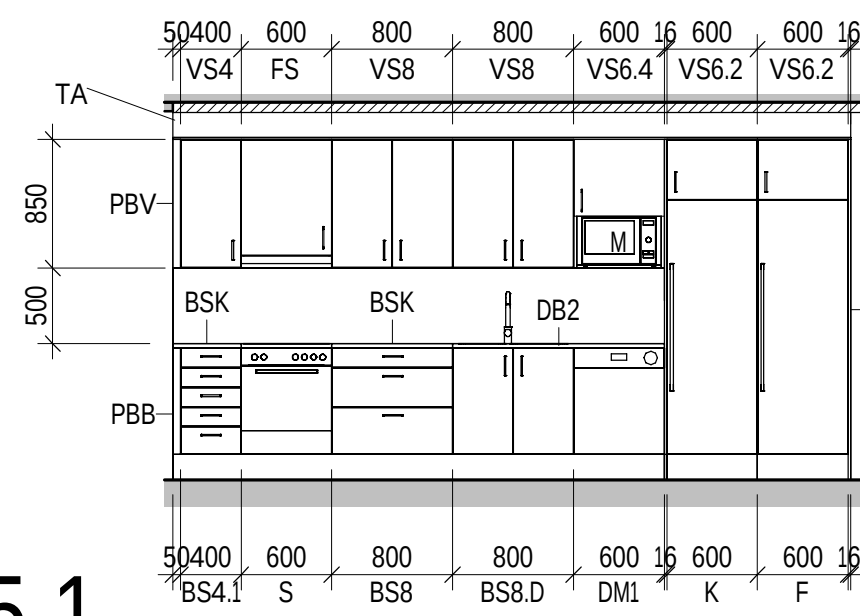

SKALA 1:50

0 1 2 5
METER

FÖRESKRIFTER

Samtliga mått kontrolleras på plats före tillverkning och montering.
Alla mått anges i millimeter.

Stommar:
16 mm spånskiva belagd med vit melamin direktaminat på båda sidor.
0,8 mm slagtälig pvc-list på alla kanter.
Rygg av 3,2 mm vittackerad träfiberplatta

Hyllor i skåp:
16 mm spånskiva belagd med vit melamin på båda sidor.
Kantlister av 0,8 mm pvc

Luckor/låd- förstycken:
Marbodal Malevik, Ljus el. likvärdigt
Dekorsidor (DS) Marbodal malevik lika luckor.
Luckor och lådförstycken med invändigt placerade gångjärn.
Lådsidor: Enl. fabr.
Lådbotten/ ryggar : Enl. fabr.
Fullutdragslådor med självstängande, dämpade gångjärn.

Bänkskivor:
Marbodal Delaware stone 652 (Tjocklek 20mm) laminatbänkskiva, eller likvärdigt

Stänkskydd
200 mm stänkskydd mellan bänkskiva och överskåp.
Marbodal Delaware stone (Tjocklek12 mm) el. likvärdigt
Väggyta ovanför stänkskydd målas i kulör lika bakomliggande vägg enl rumsbeskrivning.

Gångjärn:
Enl. fabr.

Hyllbärare:
Enl. fabr.

Handtag:
Marbodal Lounge krom/svart läder c/c 128mm el likv.

Barnsäkerhet:
Bestickkläda i lådhurst samt diskbänkskåp förses med barnsäkerhetsbeslag.

Övrigt:
En bestickkläda per kök.
Kyl, frys samt diskmaskin förses med foolproof underlägg.
Diskbänkskåp förses med kärl för sortering

Kök Specifikation

BET .	TYP, BREDD	ÖVRIGT
-------	------------	--------

Casework		
BS4.1	BÄNKSÅP 400	
BS4.2	BÄNKSÅP 400 mm	
BS5	BÄNKSÅP 500mm	
BS6	BÄNKSÅP 600	
BS6.D	DISKBÄNKSÅP 600	Pardör inkl 4st avfallsfraktioner. Tät botten
BS8	800 mm	Bänkskåp med tre fullutdragslådor
BS8.D	DISKBÄNKSÅP 800mm	Pardör inkl 4st avfallsfraktioner. Tät botten
BS10	BÄNKSÅP HÖRN 1000	Lucka 400mm. Karusell
BS11	HÖRNSÅP 1100	Lucka 500mm. Karusell
BSK	BÄNKSIVA RAK	
DS	DEKORSIDA, BÄNKSÅP, H=870	
DS	DEKORSIDA, HÖGSKÅP, H=2250	
DS	DEKORSIDA, HÖGSKÅP, H=2400	
DS	DEKORSIDA, VÄGGSKÅP, H=850	
DS	DEKORSIDA, VÄGGSKÅP, H=1000	
FS	FLÄKTSÅP, 600, H=770	Spiskåpa enl V
PBB	VARIABEL BREDD H=870	
PBH	VARIABEL BREDD, HÖJD=2250	
PBV	PASSBIT, VÄGGSKÅP, H=850	
TA	TAKANSLUTNING	Anslutning mellan kök och innetak
VS3	VÄGGSKÅP 300 mm H=850	
VS4	VÄGGSKÅP 400, H=850	
VS5	VÄGGSKÅP500 H=850	
VS6.1	VÄGGSKÅP 600 H=850	
VS6.2	SKÅP ÖVER KYLFRYS H=400	
VS6.3	VÄGGSKÅP HÖRN 600x600 H=850	
VS6.4	VÄGGSKÅP 600 H=850	Väggskåp med plats för micro
VS8	VÄGGSKÅP 800, H=850, PD	Pardör

Plumbing Fixtures		
DB1	G1220V	Diskbänk rostfri, Intra Atlantic el likv.
DB2	H14V	Diskbänk rostfri, Intra Atlantic el likv.
DB3	G12V	Diskbänk rostfri, Intra Atlantic el likv.
DB4	F10V	Diskbänk rostfri, Intra Atlantic el likv.

Specialty Equipment		
DM1	Bredd 600 mm	vit, Bosch/Electrolux. energiklass A+
F	Frys	Vit, energiklass A++ Deklarerad ljudnivå 39dB(A)
K	Kyl	Vit, energiklass A++ Deklarerad ljudnivå 39dB(A)
K/F	Kyl/Frys	Vit, energiklass A++ Deklarerad ljudnivå 39dB(A)
M	Micro	Plats för Micro
S	600 mm	Spis med håll. vit, energiklass A

BET	ÄNDRING AVSER	DATUM	SIGN	STATUS
GRANSKNINGSHANDLING				
BYGGHANDLING				
2025-02-26		ÄNDRING		
2025-02-26		PROJEKT		
CENTRUMHUSET HUS D				
KRÅKAN 1, ROBERTSFORS				
ANSVARIG PART				
AFRY AFRY Ark Studio				
J. Sjögren		KONTAKTPERSON	L.Grubbström	SKAPAD AV
J. Sjögren		GODKÄND AV	210550	UPPERRAGSNUMMER
OMBYGGNAD BIBLIOTEK OCH LÄGENHETER		INNEHÅLL	A1	FORMAT
UPPSTÄLLNING KÖK		SKALA	1:50	SKALA
A-46-4-01		NUMBER		BET