


FASTIGHETSBOX

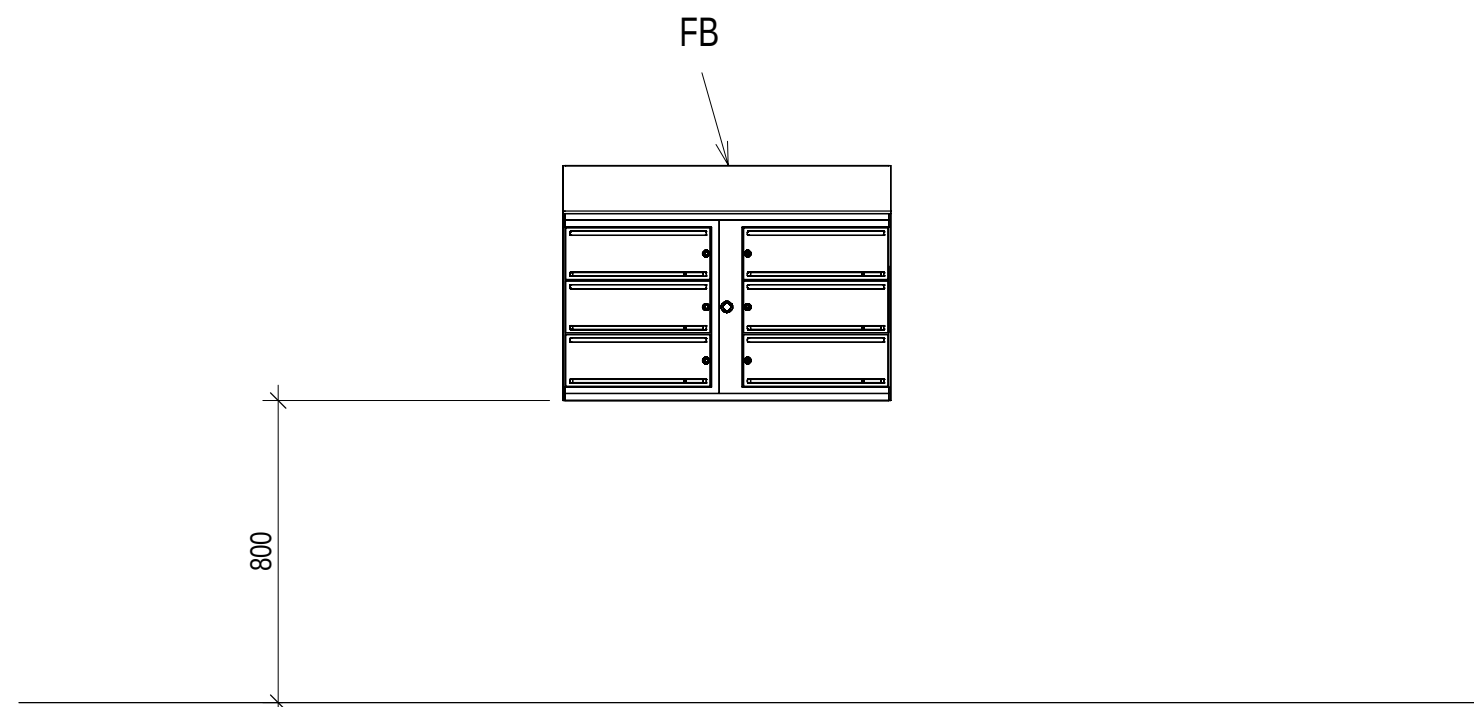

Fastighetsbox		
Littera	Typ	Antal
FB	Boxicon Lynx 2x3	1

FÖRKLARINGAR

INREDNING, LITTERA:

- PK PAPPERSKORG - MONTERAS ÖK 700 MM ÖFG
- TD TYÅLBENHÄLLARE - MONTERAS UK 1000 MM ÖFG
- PH THORPAPPERSHÄLLARE - MONTERAS UK 1000 MM ÖFG
- TH TAOLETTRULLHÄLLARE - MONTERAS 700 MM ÖFG
- SB SANITETSBENHÄLLARE - MONTERAS ÖK 675 MM ÖFG
- SP SPEGEL - MONTERAS UK 900 MM ÖFG
- TH TAOLETTRULLHÄLLARE - MONTERAS 700 MM ÖFG
- KM KOMBIMASKINGS DUSCHKÄRM I GLAS
- DS DUSCHDÅPERISKENA
- HT HANDDUKSTORK - MONTERAS 1000 MM ÖFG
- IL INSPEKTIONSLOCKA
- ST STÅDSKÅP
- KM BADRUMSSKÅP
- FB FASTIGHETSBOX - BOXICON LYNX 2X3

FÖRESKRIFTER

MONTAGE:
SAMTLIGA SÄKVAROR SKA MONTERAS ENLIGT:
BRANSCHREGLER SÄKER VATTENINSTALLATION 2016:1

BET	ANSVARIG AVYSER		DATUM	SIGN	STATUS
GRANSKNINGSHANDLING					
BYGGHANDLING					
2025-02-26		DATUM		ANMÄRKNING	
CENTRUMHUSET HUS D KRÅKAN 1, ROBERTSFORS					
ANSVARIG PART					
 AFRY		AFRY Ark Studio			
J. Sjögren	KONTAKTPERSON	L.Grubbström		SKAPAD AV	
J. Sjögren	GÖDKÄND AV	210550		UPPERGRANSNUMMER	
RITNINGSCATEGORY					
OMBYGGNAD BIBLIOTEK OCH LÄGENHETER			INNEHÅLL	FORMAT	
UPPSTÄLLNING ÖVRIGT			A1		SKALA
A-4-4-03			1:20		BET
			NUMMER		

File C:\Users\jmd534\OneDrive - AFRY\Documents\A-40-V-01_ludwig.grubbstrom.rvt