

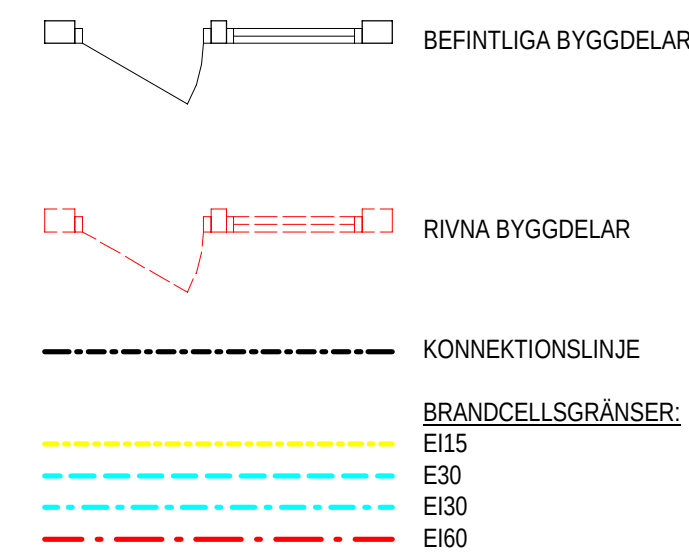


FÖRKLARINGAR

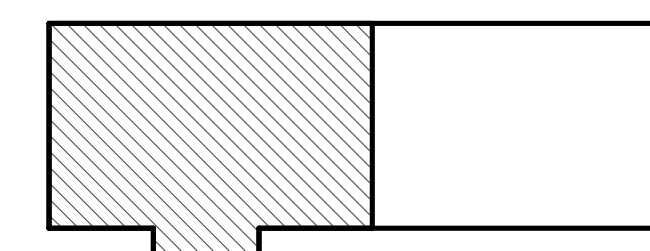

FÖRESKRIFTER

SANERING:
Sanering enl miljöinventering utförd av konsultera 22-12-2023

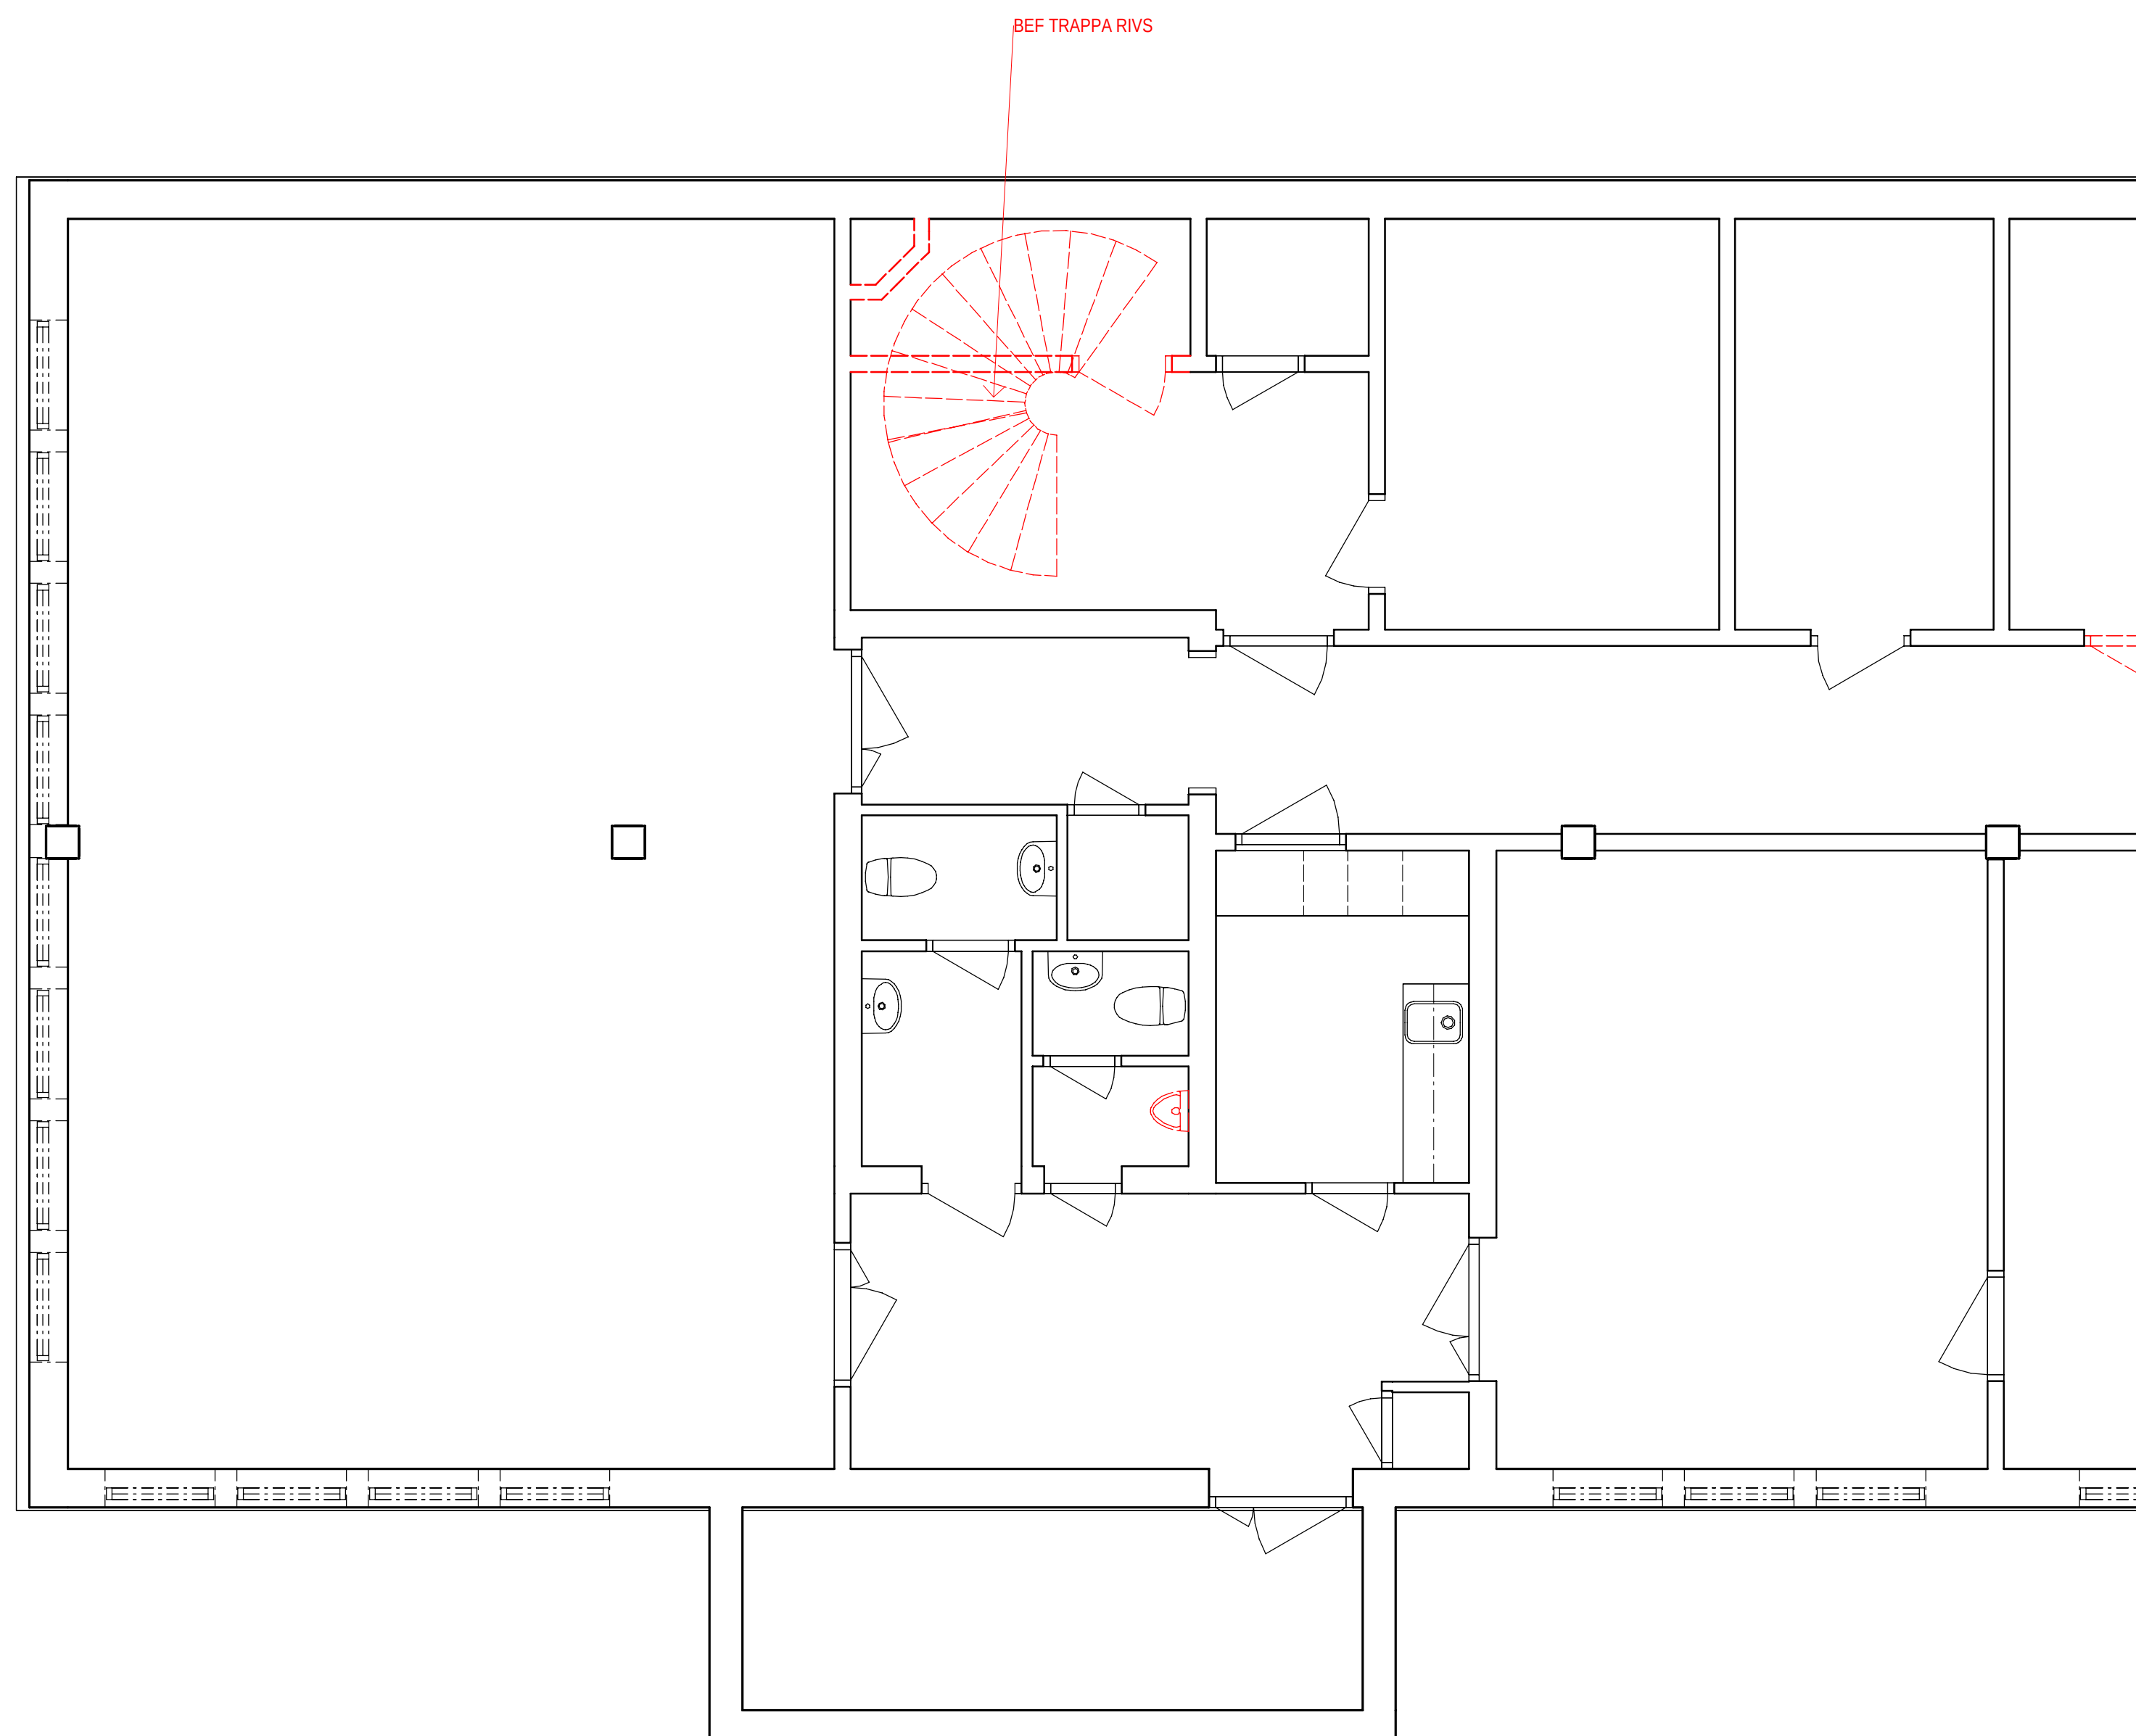

BET	ANDRING AVSEER	DATUM	SIGN	STA
GRANSKNINGSHANDLING				
BYGGHANDLING				
2025-02-26		DATUM	ANDR	
CENTRUMHUSET HUS D				
KRÅKAN 1, ROBERTSFORS				
ANSVARIG RA				
		AFRY Ark Studio		
J. Sjögren	KONTAKTPERSON	L.Grubbström	SKRAPAD	
J. Sjögren	GÖKÄND AV	210550	UPPRÄGSLIV	
			RITNINGSSÄTT	
OMBYGGNAD BIBLIOTEK OCH LÄGENHETER			INNEHÅLL	FORM
RIVNING PLAN 090 - DEL 1			A1	SK
A-9-1-D091			NUMMER	1:50

SKALA 1:50

0
METER

1