

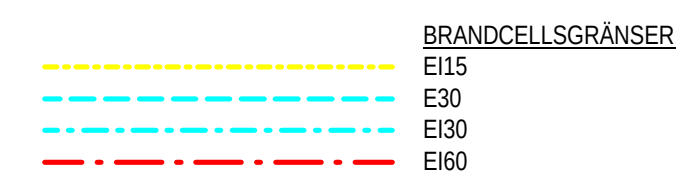


FÖRKLARINGAR

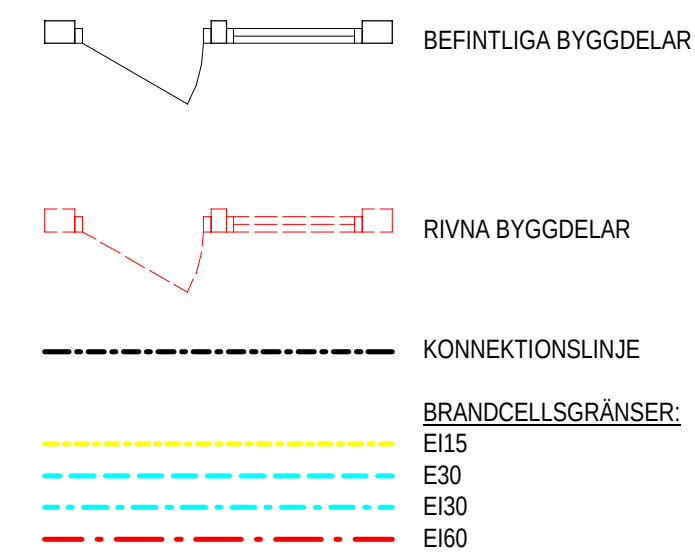

FÖRESKRIFTER

SANERING:
Sanering enl miljöinventering utförd av konsultera 22-12-2023

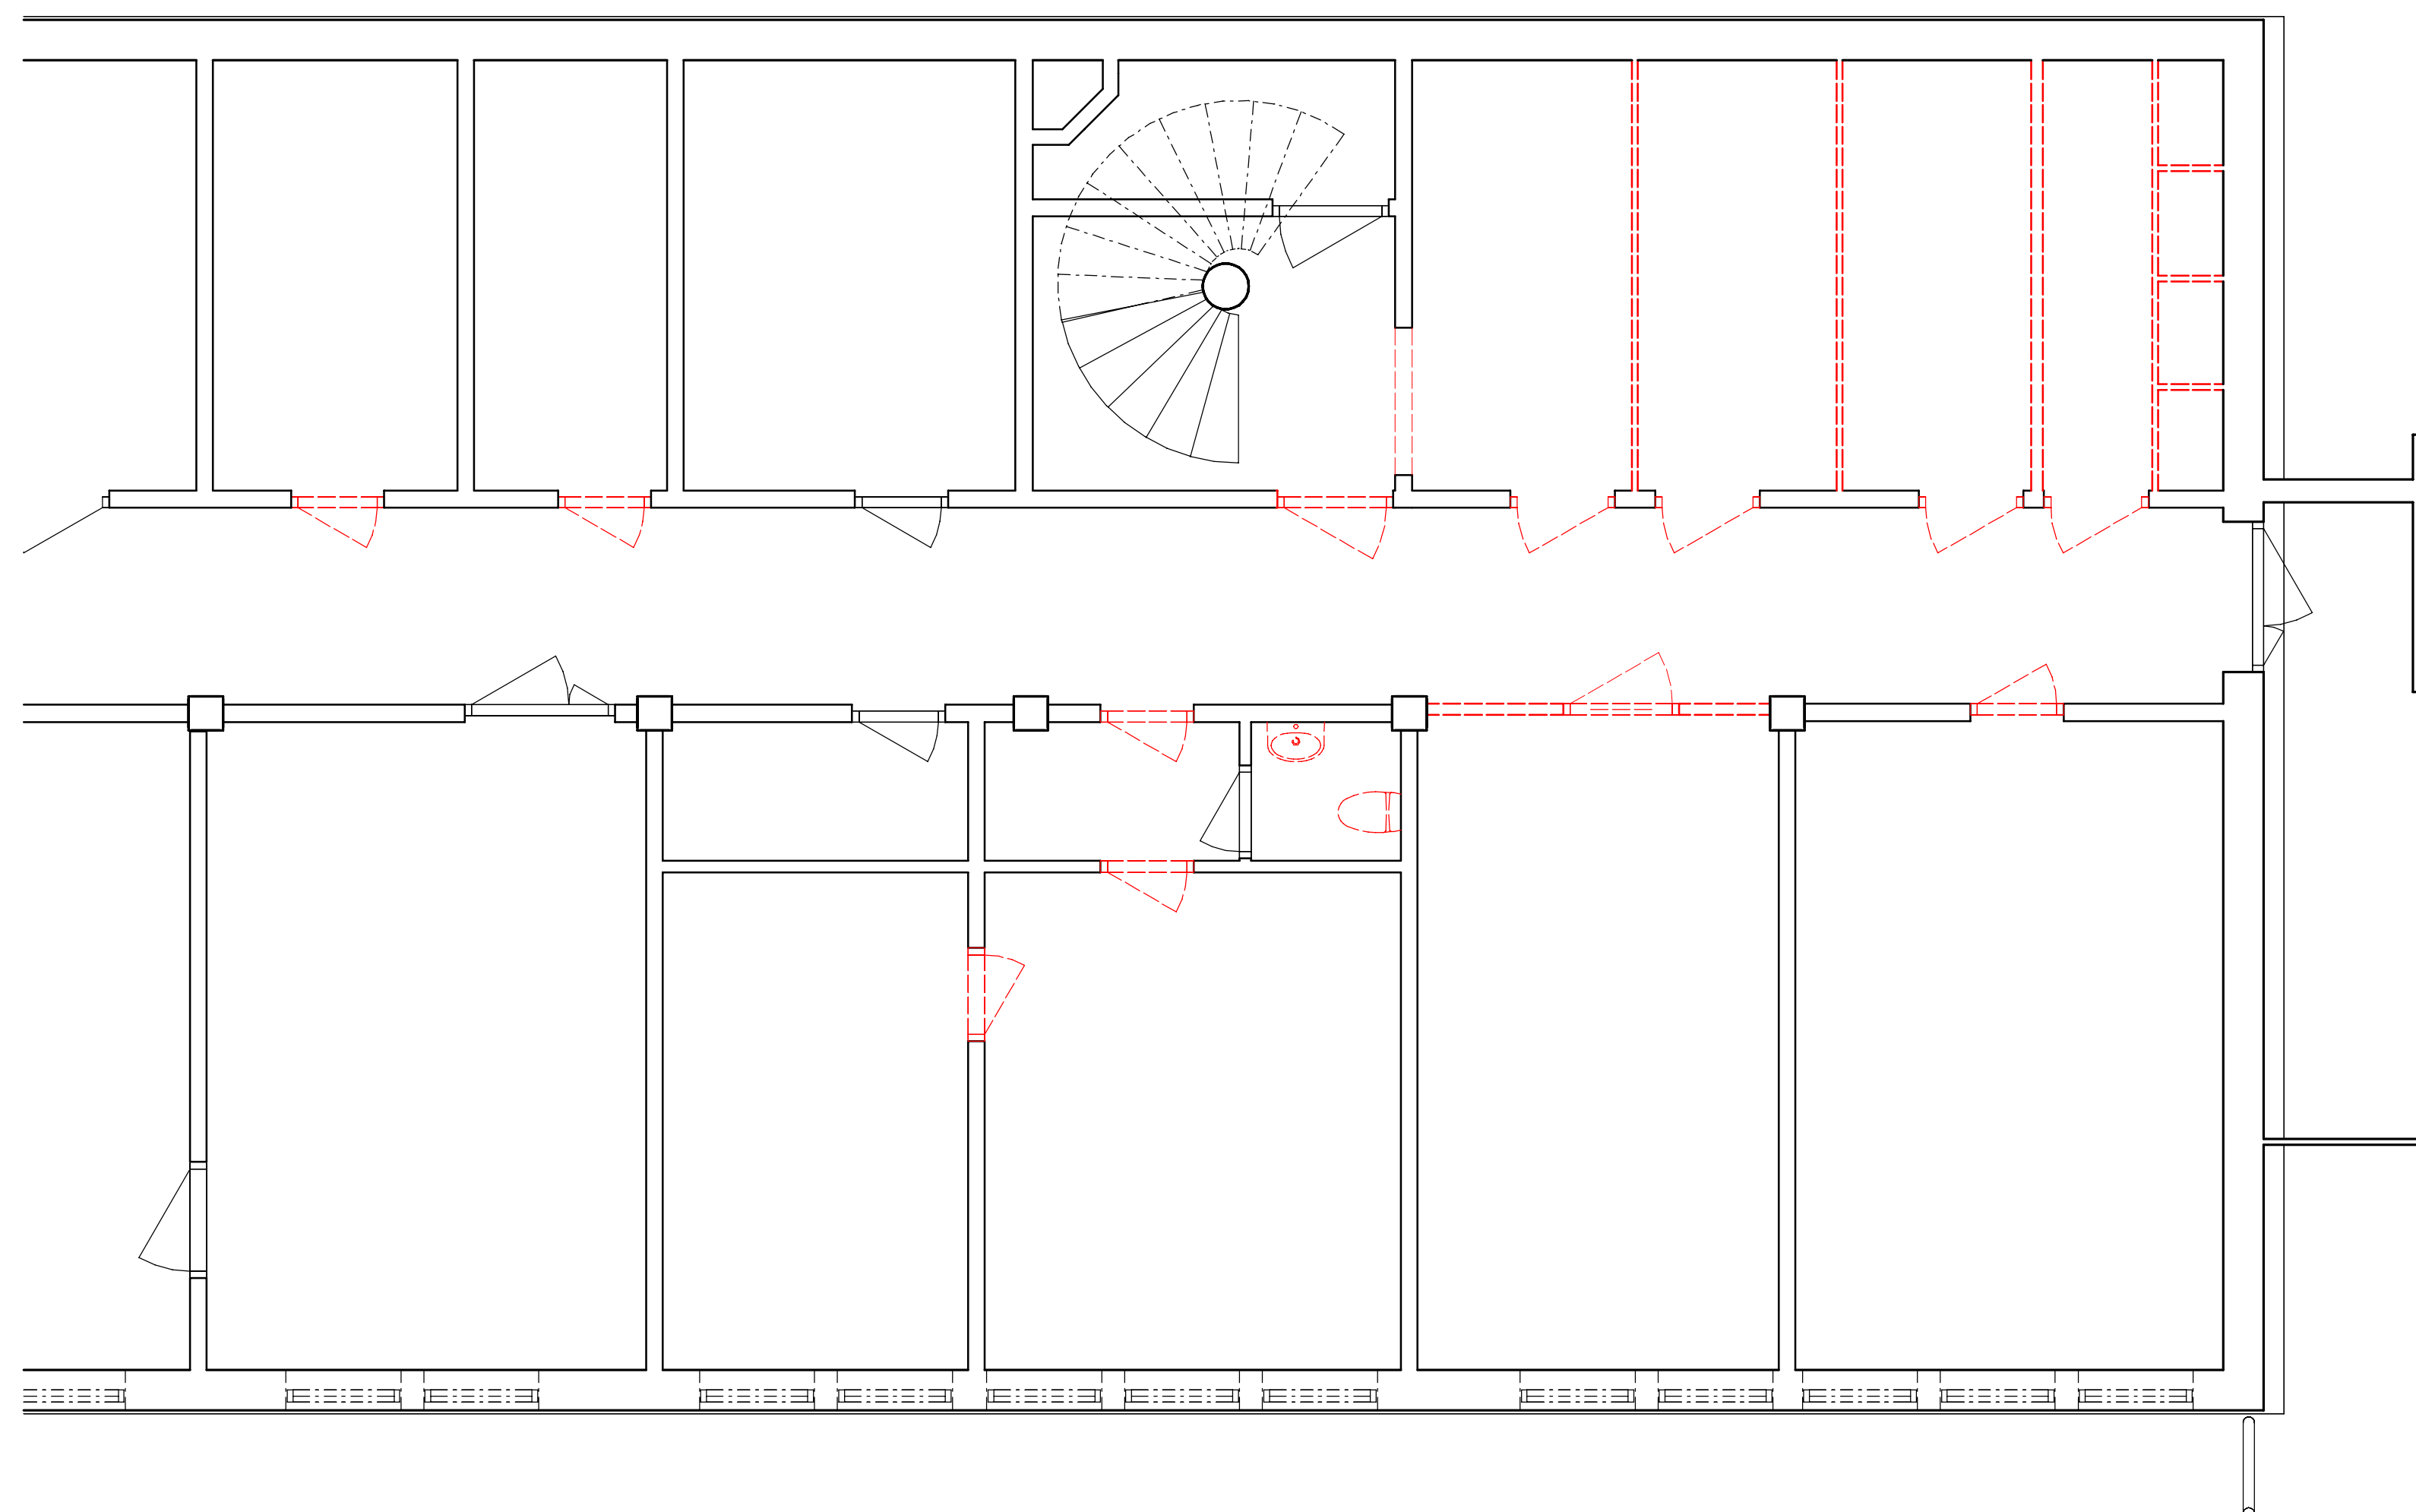

SKALA 1:50

0
METER

METER

BET	ANDRING AVSEER	DATUM	SIGN	STA
GRANSKNINGSHANDLING				
BYGGHANDLING				
DATUM 2025-02-26		ANDR		
CENTRUMHUSET HUS D KRÅKAN 1, ROBERTSFORS				
FRÖJ				
ANSVARIG RA				
		AFRY Ark Studio		
J. Sjögren	KONTAKTPERSON	L.Grubbström	SKRAPAD	
J. Sjögren	GÖKÄND AV	210550	UPPRAGSGNUMM	
			BETINGSKALLA	
OMBYGGNAD BIBLIOTEK OCH LÄGENHETER			INNEHÅLL	FORM
RVNING PLAN 090 - DEL 2			A1	SK
A-9-1-D092			NUMBER	C

BYGGHANDLING

CENTRUMHUSET HUS D
KRÅKAN 1, ROBERTSFORS

KRÅKAN 1, ROBERTSFORS



AFRY Ark Studio

1	Siögren	KONTAKTPERSON	1	Grubbström	SKAPAD
---	---------	---------------	---	------------	--------

KONTAKTPERSON

SON	I Grubhströ
-----	-------------

SKAPAD

1 Sjögren	GÖDKÄND AV	210550	UPPDRAGSNUMM
-----------	------------	--------	--------------

GOODKIND AV

AV	210550
----	--------

UPPDRAGSNUMMER:

OMBYGGNAD BIBLIOTEK OCH LÄGENHETER	INNEHÅLL	A1	FORM
------------------------------------	----------	----	------

INNEHÅLL

FORM 1

MINING PLAN 200 251 2

KL	
50	SKA

RIVNING PLAN 090 - DEL 2	1.50
1. 10. 1. 0000	NUMBER

NUMBER

50