

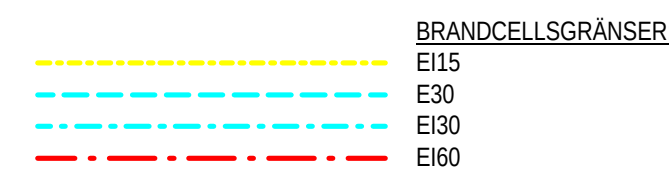
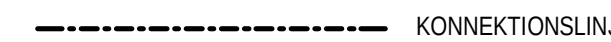
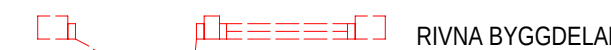


FÖRKLARINGAR

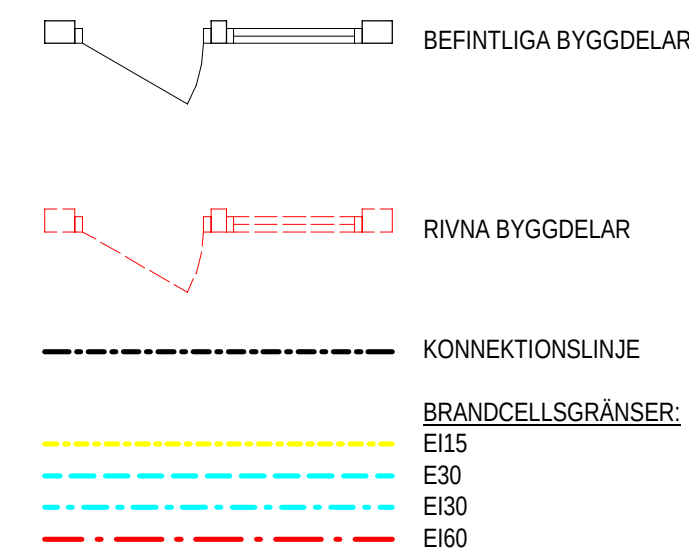

FÖRESKRIFTER

SANERING:
Sanering enl miljöinventering utförd av konsultera 22-12-2023

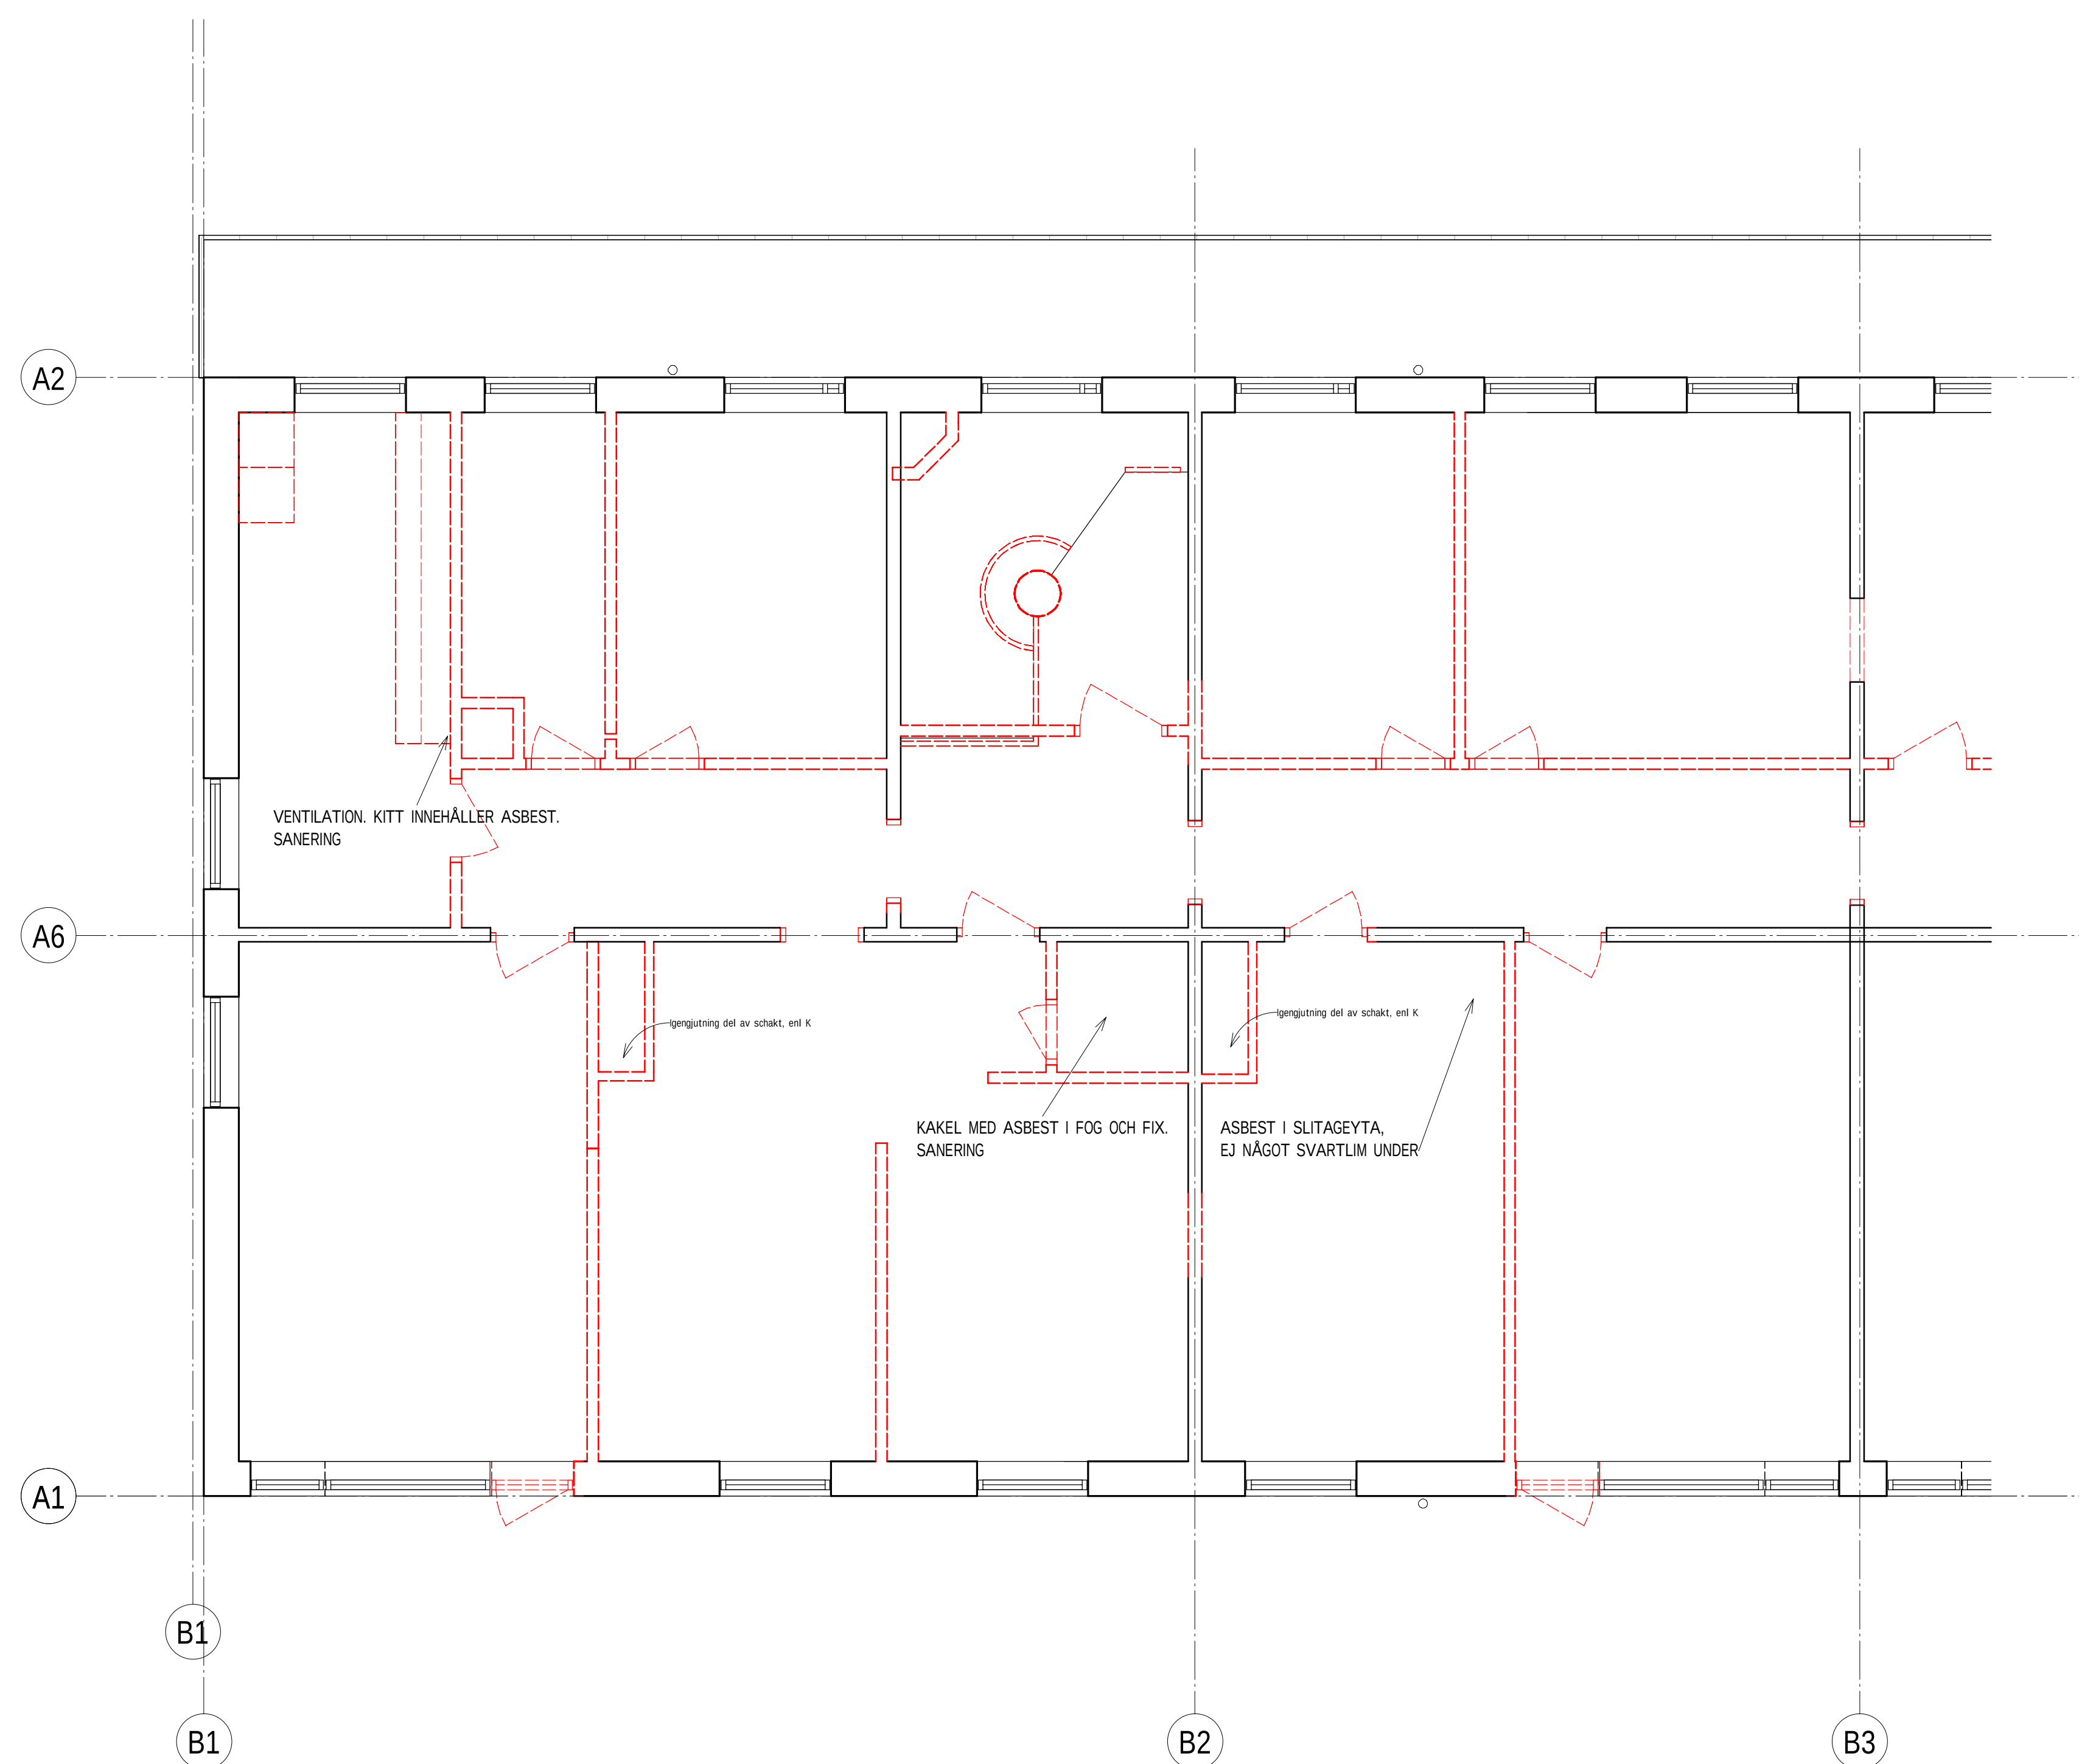


igengjutting del av skakt, enl

KAKEL MED ASBEST I FOG OCH FIX.
SANERING

ASBEST I SLITAGEYTA,
EJ NÅGOT SVARTLIM UNDER

—loengjutning del av schakt, enl

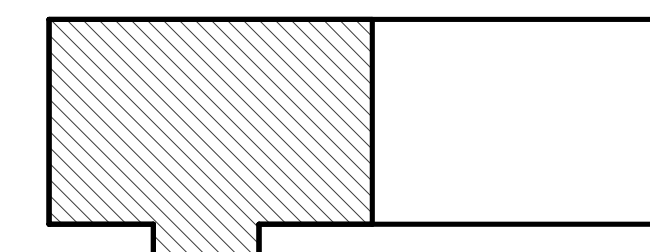

SKALA 1:50

0
METER

METER

BET	ÄNDRING AVSEER	DATUM	SIGN	STAT
GRANSKNINGSHANDLING				
BYGGHANDLING				
2025-02-26		DATUM	ÄNDRING	
CENTRUMHUSET HUS D				
KRÅKAN 1, ROBERTSFORS				
ANSVARIG PÅ				
		AFRY Ark Studio		
J. Sjögren	KONTAKTPERSON	L.Grubbstrom	SKAPAD	
J. Sjögren	GÖKKAND AV	210550	UPPGRADENUMM	
			RTINGSKATEGORI	
OMBYGGNAD BIBLIOTEK OCH LÄGENHETER			INNEHÅLL	FORM
RIVNING PLAN 200 - DEL 1			A1	SKALA
A-9-1-D201			NUMMER	B

BYGGHANDLING

CENTRUMHUSET HUS D
KRÅKAN 1, ROBERTSFORS

KRÅKAN 1, ROBERTSFORS



AFRY Ark Studies

J. Sjögren	KONTAKTPERSON	L.Grubbström	SKAPAD
J. Sjögren	GODKÄND AV	210550	UPPDRAGSNUMM
RITNINGSKATEGORI			
OMBYGGNAD BIBLIOTEK OCH LÄGENHETER		INNEHÅLL	FORM
RIVNING PLAN 200 - DEL 1			SKALA
A-49-1-D201		NUMMER	B

SON	I Grubhströ
-----	-------------

J. Sjögren	GODKÄND AV	210550	UPPDRAGSNUMMER
------------	------------	--------	----------------

AV	210550
----	--------

OMBYGGNAD BIBLIOTEK OCH LÄGENHETER	INNEHÅLL	A1	FORM
------------------------------------	----------	----	------

ALL	A1	FORM
-----	----	------

RIVNING PLAN 200 - DEL 1	1:50	SKALA
--------------------------	------	-------

1:50 SKA

A-49-1-D201	NUMBER	B
-------------	--------	---