


I SAMBAND MED RIVNING SKALL PENDLAR,
SVEP, ISOLERING, YTSKIKT OCH INFÄSTNINGSDETALJER RIVAS
FÖR SAMTLIGA INSTALLATIONER.

PROPPADE RÖRLEDNINGAR FRÅN GOLV ELLER TAKBJÄLKLÄG
SKALL EJ VARA SYNLIKA EFTER PROPPNING.

X =RIVNING

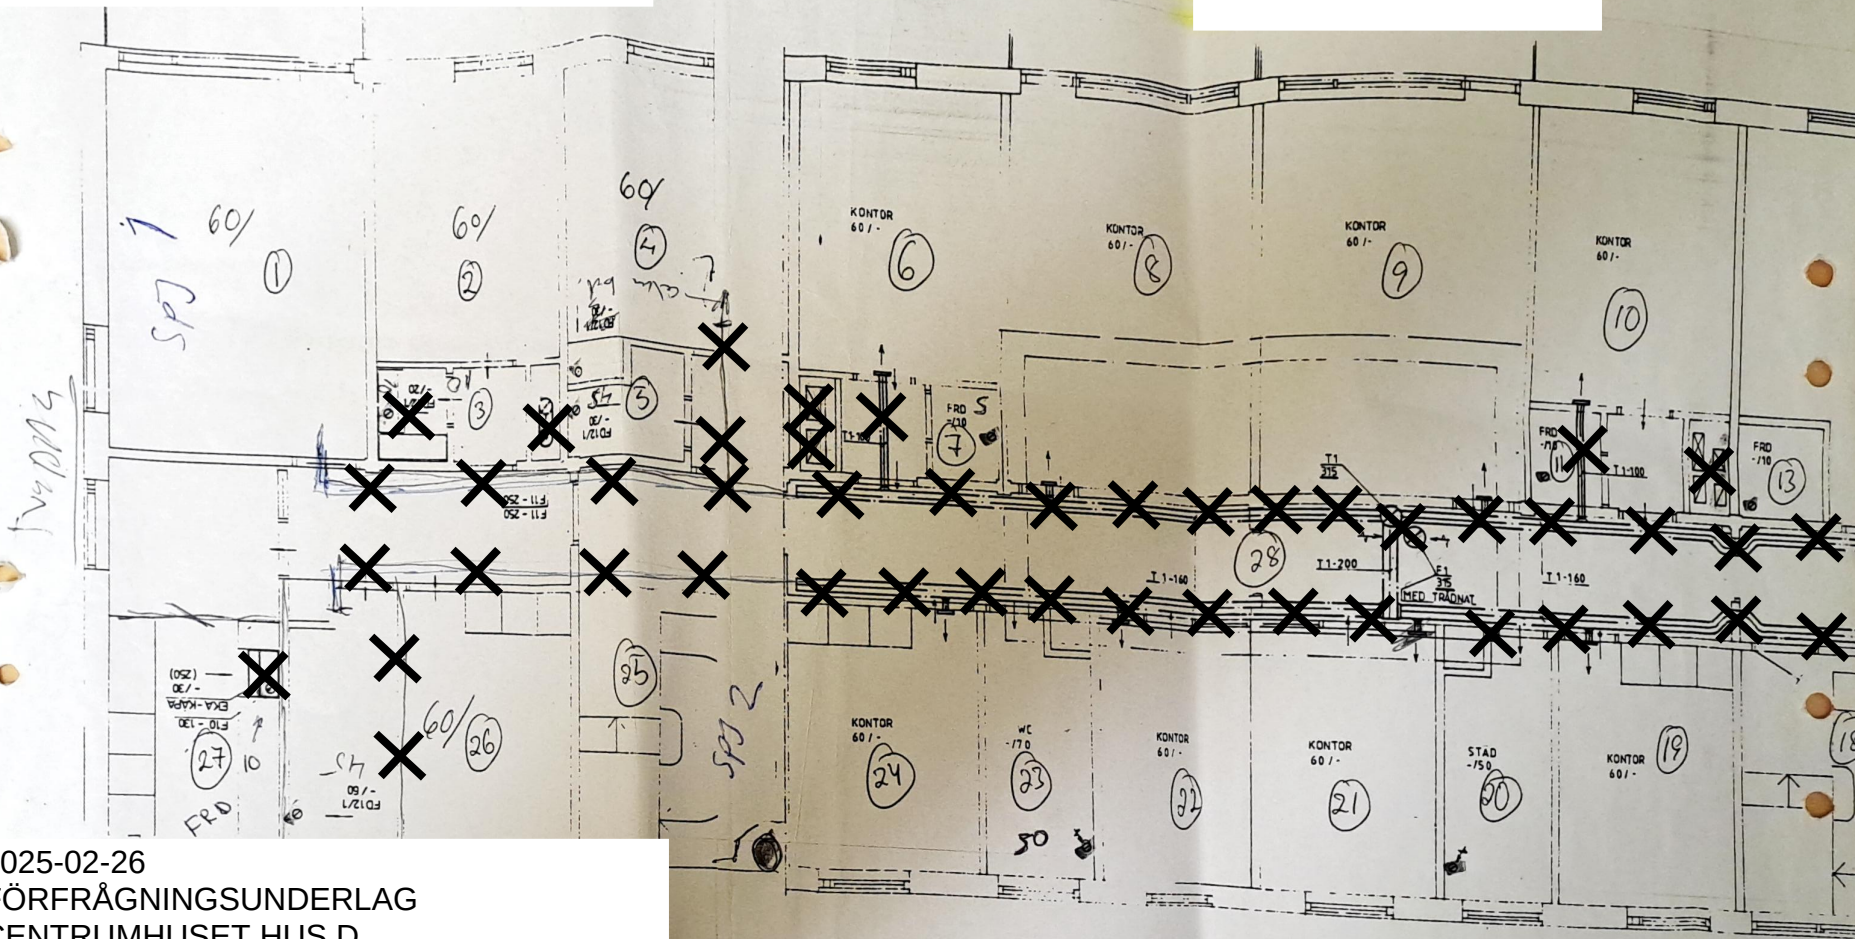

2025-02-26
FÖRFRÅGNINGSUNDERLAG
CENTRUMHUSET HUS D
PLAN 200 DEL 1
LUFTBEHANDLING_RIVNING

V-57-9-D201

PLAN
SKALA 1:50