


X = RIVNING

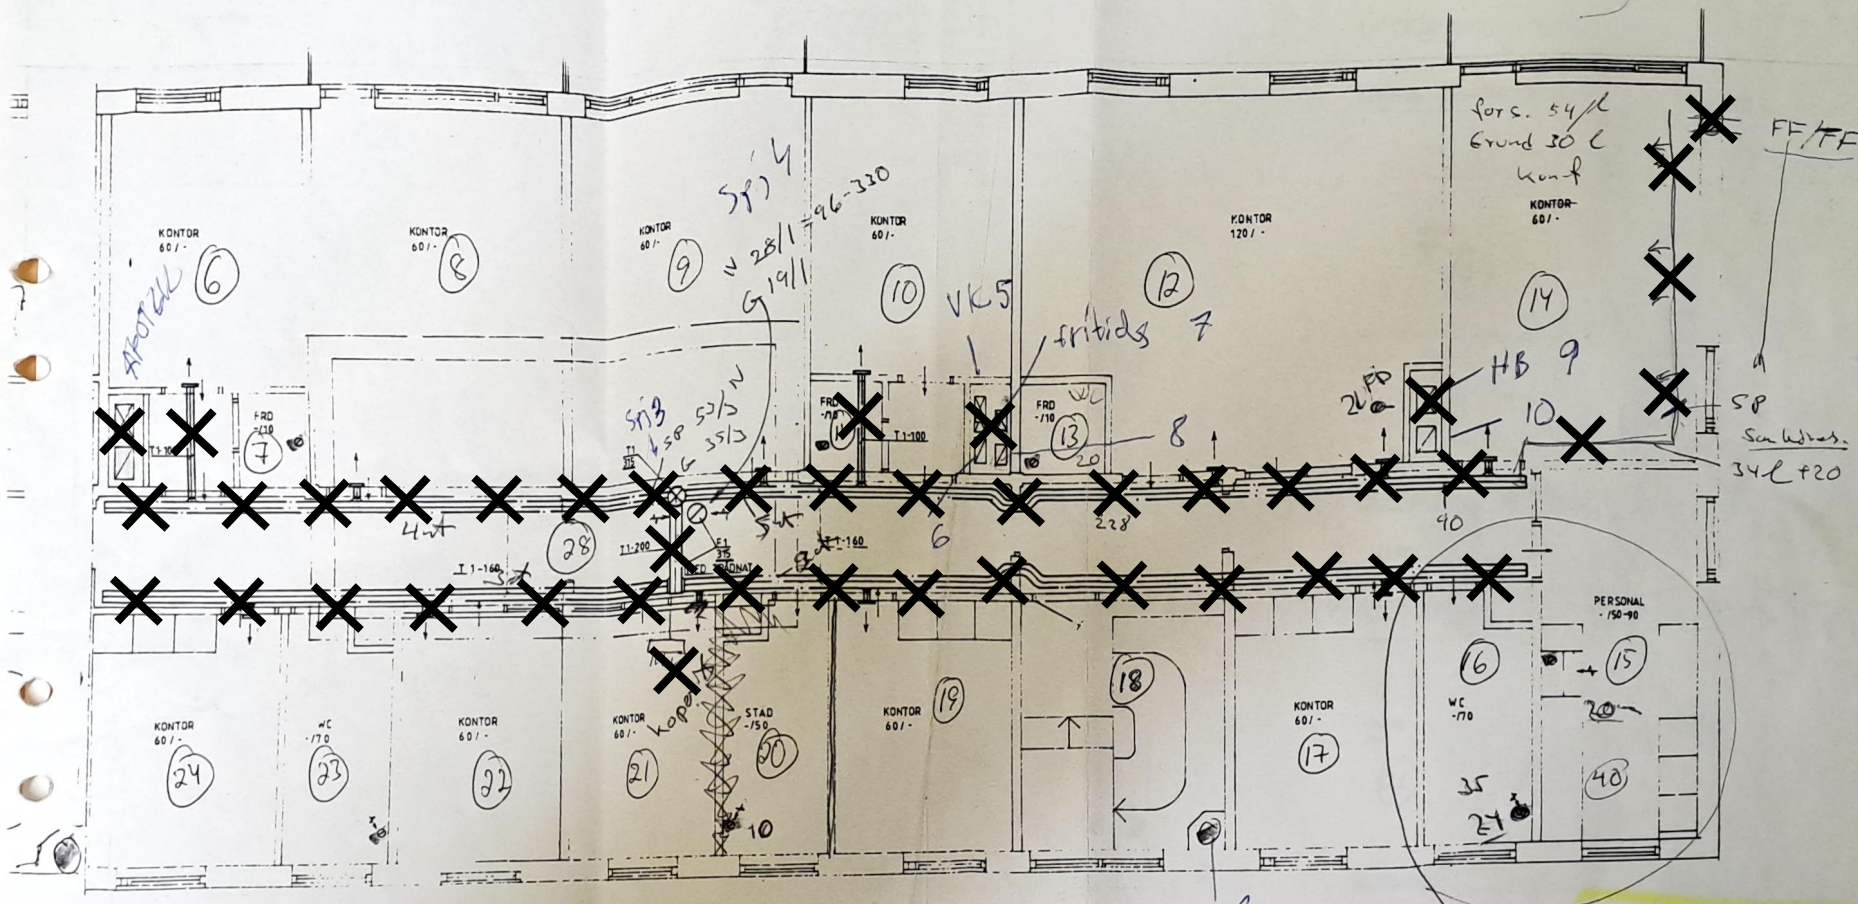

PLAN
SKALA 1:50

2025-02-26
FÖRFRÅGNINGSUNDERLAG
CENTRUMHUSET HUS D
PLAN 200 DEL 2
LUFTBEHANDLING_RIVNING

V-57-9-D202

Garl. 84
66 69
I SAMBAND MED RIVNING SKALL PENDLAR,
SVEP, ISOLERING, YTSKIKT OCH INFÄSTNINGSDETALJER RIVAS
FÖR SAMTLIGA INSTALLATIONER.

PROPPADE RÖRLEDNINGAR FRÅN GOLV ELLER TAKBJÄLKLAR
SKALL EJ VARA SYNLIGA EFTER PROPPNING.

116L - 420 = 84
96L Del 345 - = 69