



X:\U-Transit\Entries\TM\Uppdrag\2021\20550 Kråkan 1 - Centrumhuset\2 - Gemensamma underlag\Enhätna relationer\KVS - kopia.dwg \ \ V.A1 - Modeller\Export DWG\PLAN 1 BIBLIOTEK.dwg \ \ V.A1 - Modeller

✕ = RIVNING

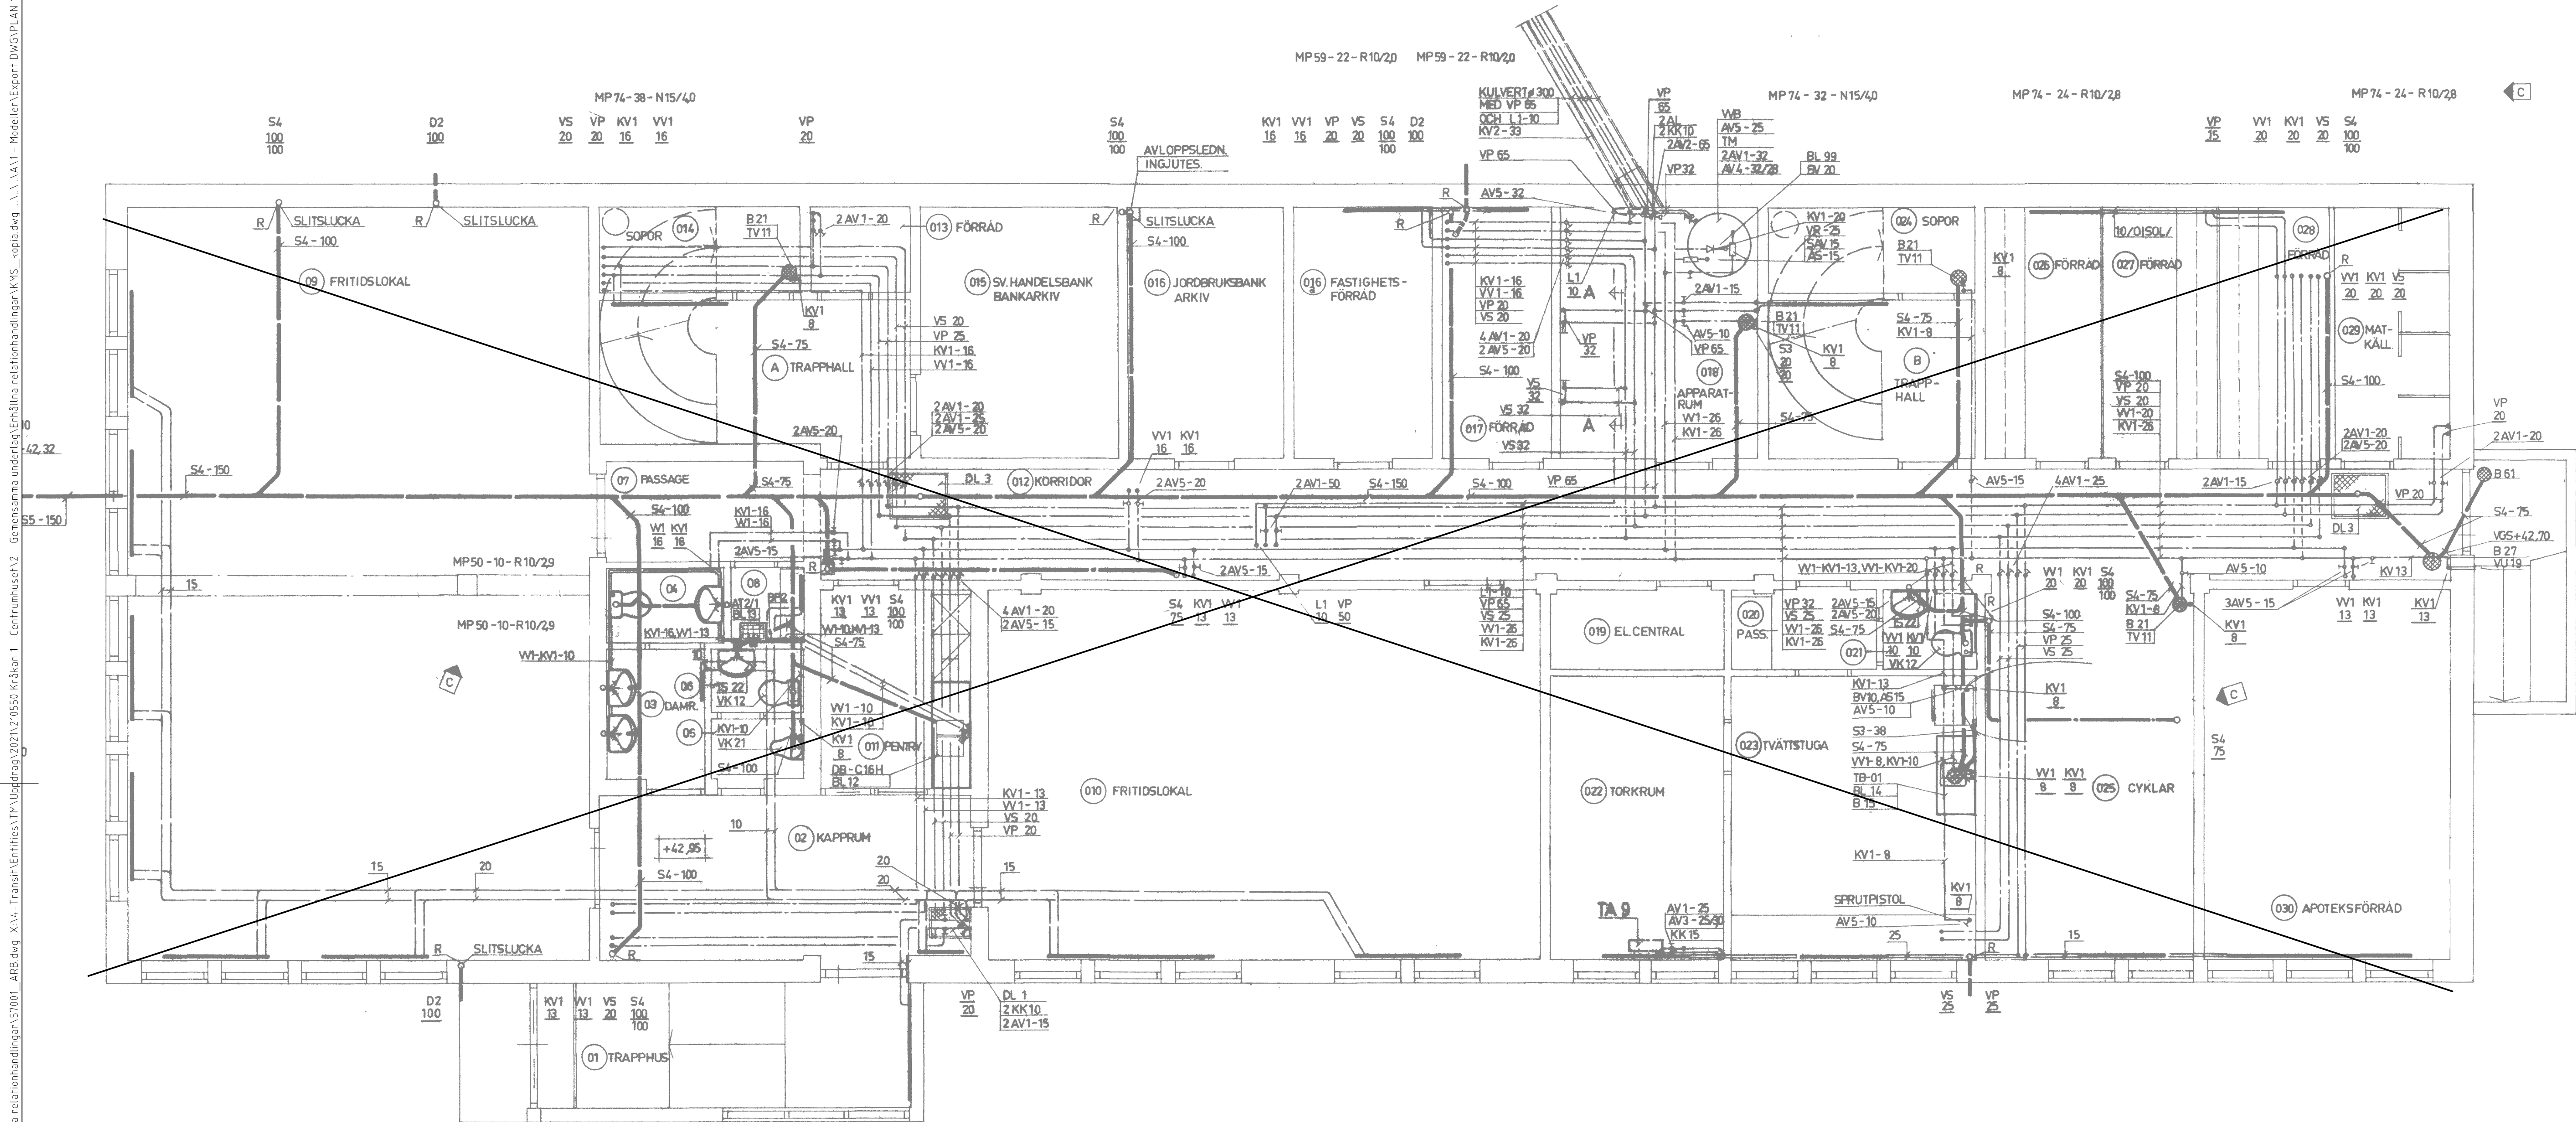

I SAMBAND MED RIVNING SKALL PENDLAR, SVEP, ISOLERING, YTSKIKT OCH INFÄSTNINGSDETALJER RIVAS FÖR SAMTLIGA INSTALLATIONER.

PROPPADE RÖRLEDNINGAR FRÅN GOLV ELLER TAKBJÄLKLAG SKALL EJ VARA SYNLIKA EFTER PROPPNING.

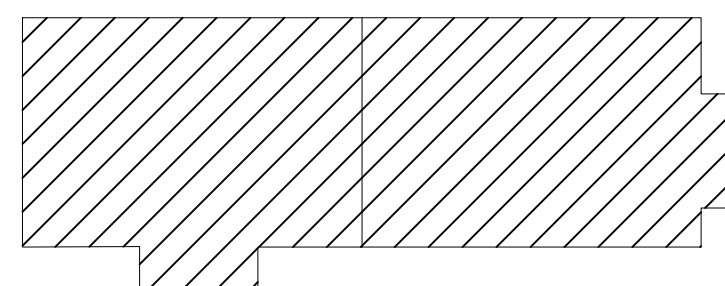

FÖRFRÅGNINGSUNDERLAG		STATUS
BYGGHANDLING		HANDLING
DATUM	2025-02-26	ÄNDRING
CENTRUMHUSET HUS D KRÅKAN 1, ROBERTSFORS		PROJEKT
AFRY-Infrastructure AB Storgatan 103 921 32 Lycksele Tel: 010-505 00 00		ANSVARIG PART
Simon Rudin	KONTAKTPERSON	Marzena Januszewska-Kut
Simon Abrahamsson	GÖRKÄND AV	D0182343 (210550)
PLANRITNING		RITNINGSKATEGORI
OMBYGGNAD BIBLIOTEK OCH LÄGENHETER		INNEHÅLL
KÄLLARPLAN - PLAN 09		FORMAT
VS-INSTALLATIONER_RIVNING		SKALA
V-50-9-D090		NUMMER
		BET