



X:\u-Transit\Entries\TM\Uppdrag\2021\210550 Kråkan 1 - Centrumhuset\2 - Gemensamma underlag\Enhätna relationer\Handlingar\KVS - kopia.dwg \ \ \ V A 1 - Modeller\Export DWG\SCAN 1 BIBLIOTEK.dwg \ \ \ V A 1 - Modeller

✕ = RIVNING

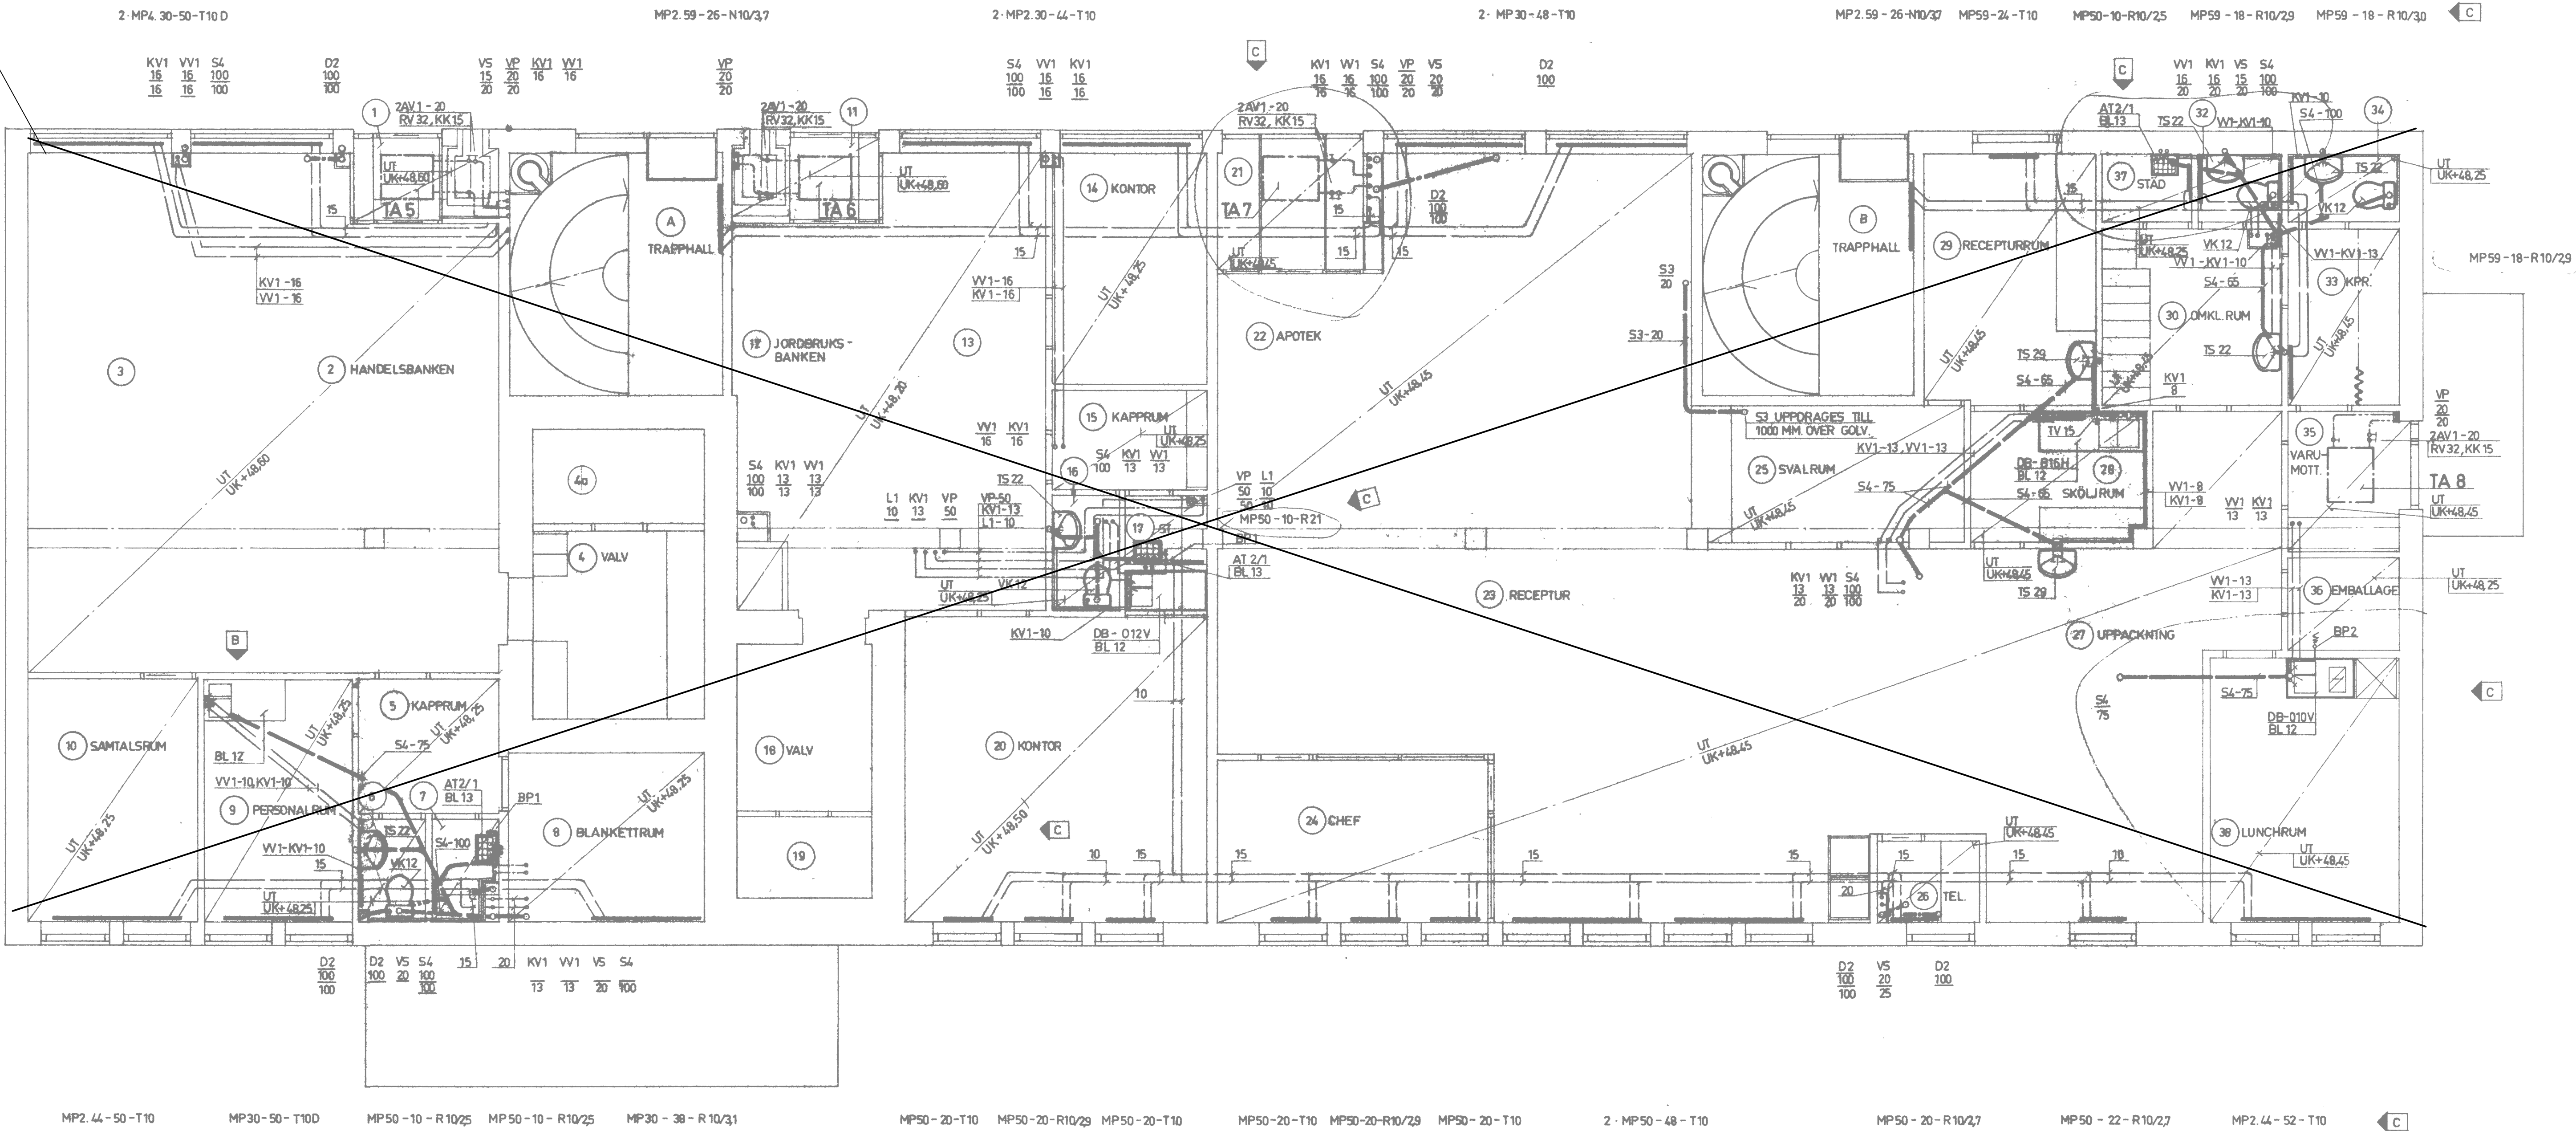

I SAMBAND MED RIVNING SKALL PENDLAR, SVEP, ISOLERING, YTSKIKT OCH INFÄSTNINGSDETALJER RIVAS FÖR SAMTLIGA INSTALLATIONER.

PROPPADE RÖRLEDNINGAR FRÅN GOLV ELLER TAKBJÄLKLAG SKALL EJ VARA SYNLIKA EFTER PROPPNING.

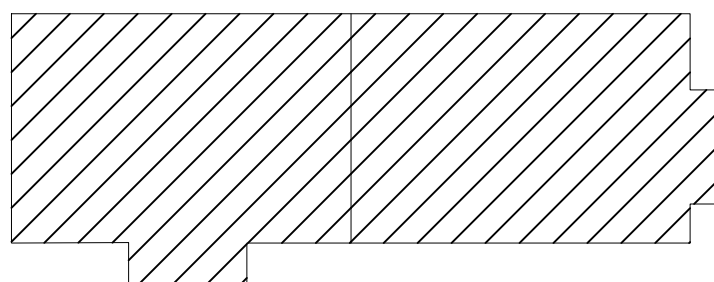

|                                                                                                 |                         |                   |
|-------------------------------------------------------------------------------------------------|-------------------------|-------------------|
| FÖRFRÅGNINGSUNDERLAG                                                                            |                         | STATUS            |
| BYGGHANDLING                                                                                    |                         | HANDLING          |
| DATUM                                                                                           | 2025-02-26              | ÄNDRING           |
| CENTRUMHUSET HUS D<br>KRÅKAN 1, ROBERTSFORS                                                     |                         | PROJEKT           |
| AFRY-Infrastructure AB<br>Storgatan 103<br>921 32 Lycksele<br>Tel: 010-505 00 00                |                         | ANSVARIG PART     |
| KONTAKTPERSON                                                                                   | Simon Rudin             | SKAPAD AV         |
| GODKÄND AV                                                                                      | Marzena Januszewska-Kut | UPPDRAGSNUMMER    |
| PLANRITNING                                                                                     | Simon Abrahamsson       | D0182343 (210550) |
| OMBYGGNAD BIBLIOTEK OCH LÄGENHETER<br>BOTENPLAN - PLAN 10 - DEL 1<br>VS-INSTALLATIONER, RIVNING |                         | RITNINGSKATEGORI  |
| A1                                                                                              |                         | FORMAT            |
| 1:50                                                                                            |                         | SKALA             |
| V-50-9-D100                                                                                     |                         | NUMMER            |
|                                                                                                 |                         | BET               |