

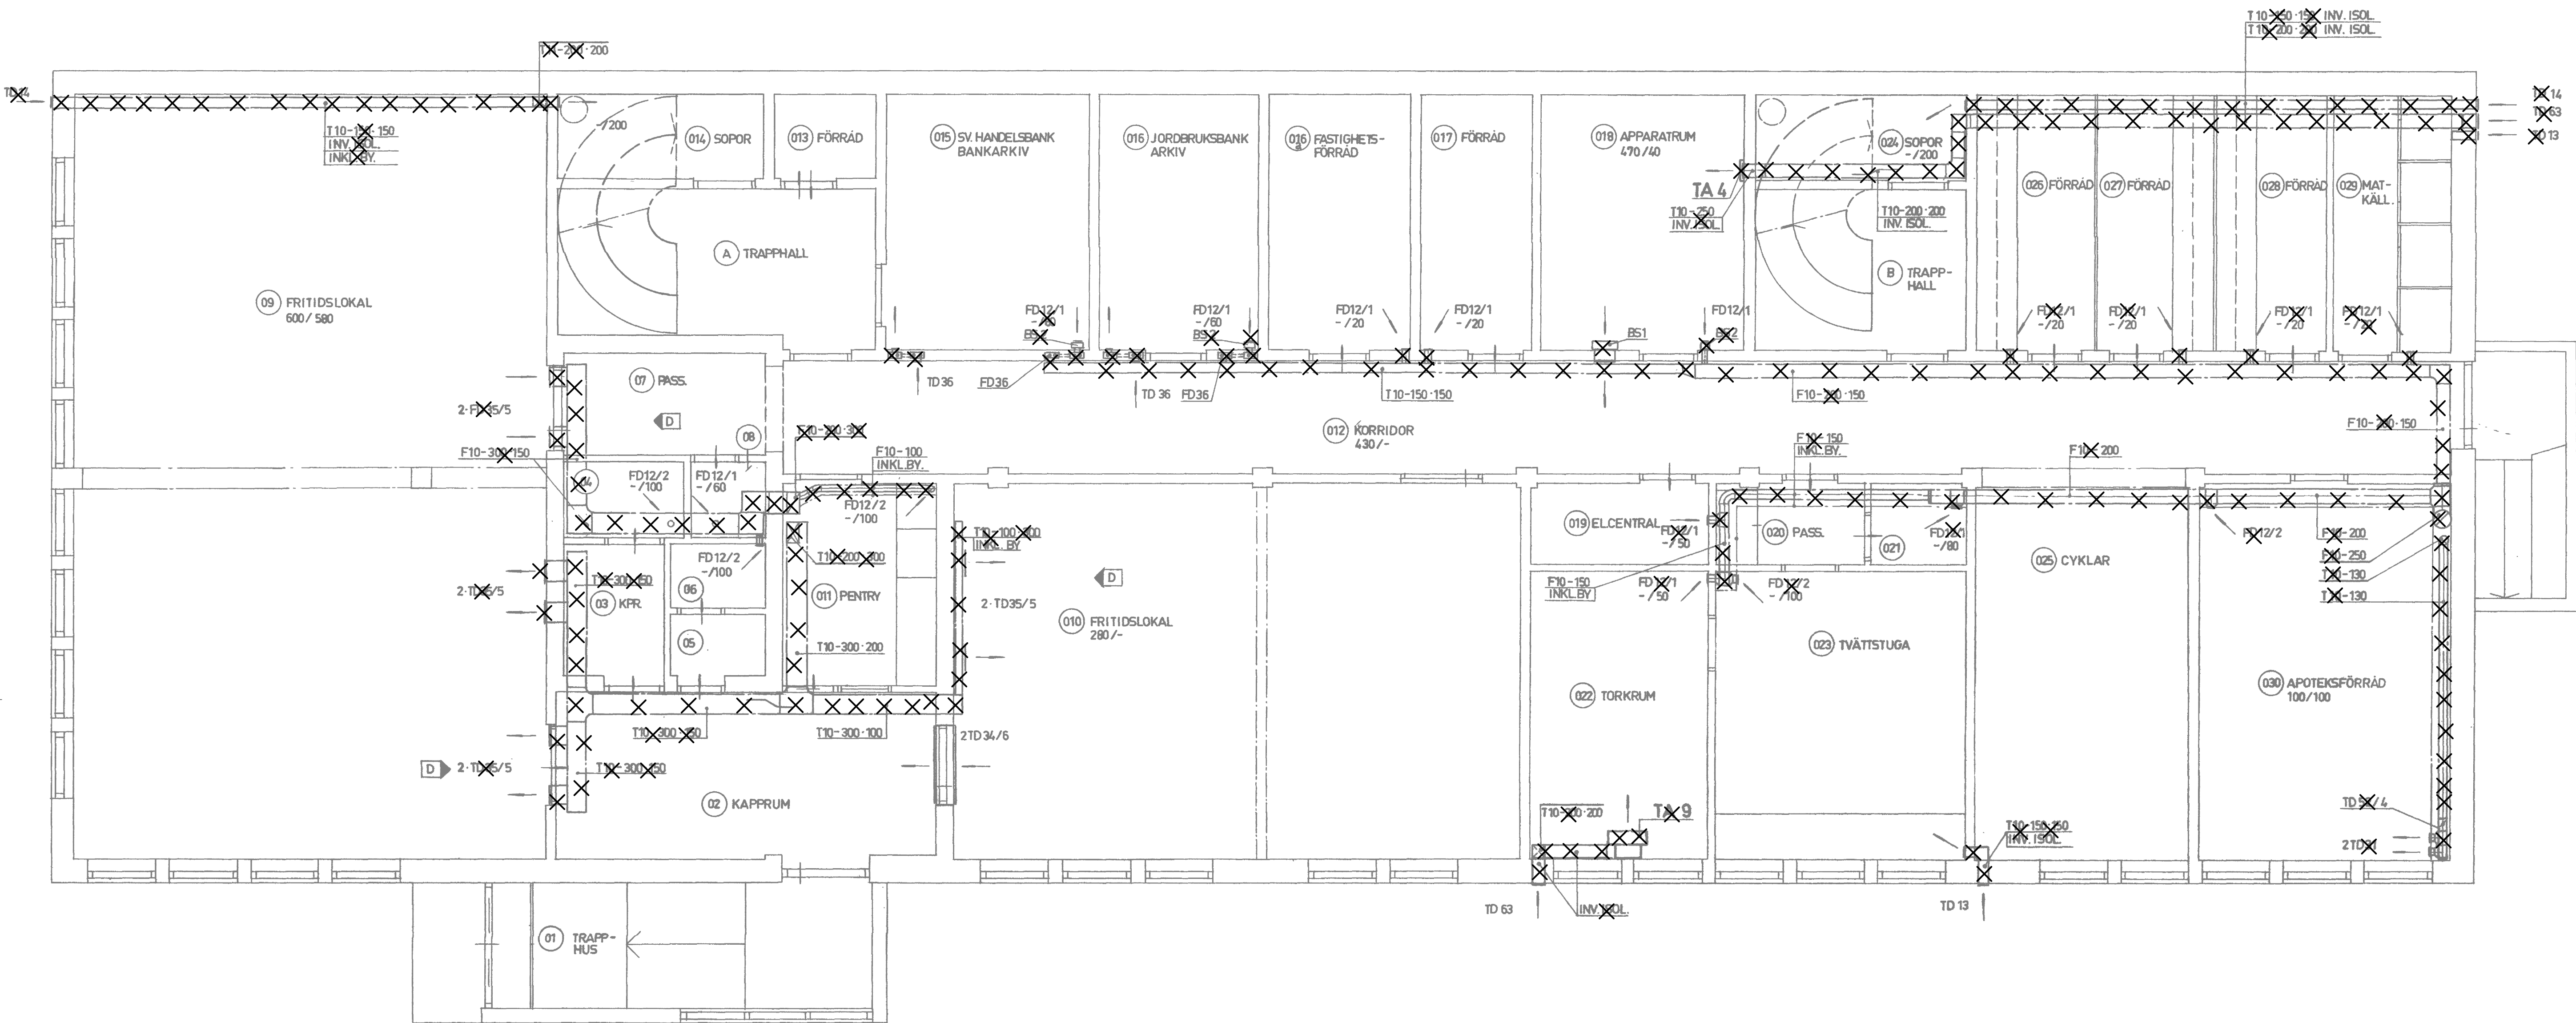


X:\u-Transit\Entries\TM\Uppdrag\2021\20550 Kråkan 1 - Centrumhuset\2 - Gemensamma underlag\Enhätna relationshandlingar\KMS - kopia.dwg \ \ \ V.A.1 - Modeller\Export DWG\PLAN 1 BIBLIOTEK.dwg \ \ \ V.A.1 - Modeller

✕ = RIVNING

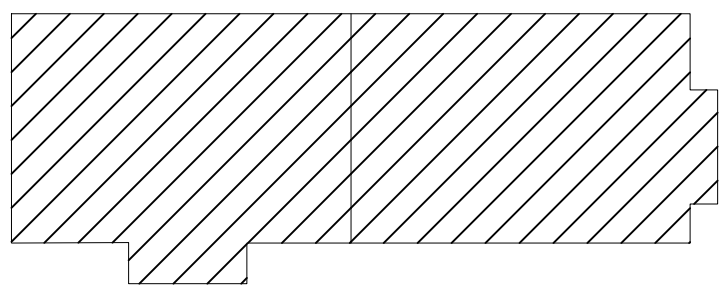

I SAMBAND MED RIVNING SKALL PENDLAR, SVEP, ISOLERING, YTSKIKT OCH INFÄSTNINGSDETALJER RIVAS FÖR SAMTLIGA INSTALLATIONER.

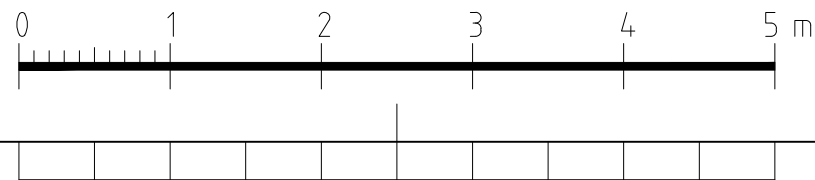

FÖRFRÅGNINGSUNDERLAG		STATUS
BYGGHANDLING		HANDLING
DATUM	2025-02-26	ÄNDRING
CENTRUMHUSET HUS D KRÅKAN 1, ROBERTSFORS		PROJEKT
AFRY-Infrastructure AB Storgatan 103 921 32 Lycksele Tel: 010-505 00 00		ANSVÄRIG PART
KONTAKTPERSON	Simon Rudin	Marzena Januszewska-Kut
GODKÄND AV	Simon Abrahamsson	D0182343 (210550)
PLANRITNING		RITNINGSKATEGORI
OMBYGGNAD BIBLIOTEK OCH LÄGENHETER		INNEHÅLL
KÄLLARPLAN - PLAN 08		FORMAT
LUFTBEHANDLING_RIVNING		SKALA
V-57-9-D090		NUMMER
		BET