



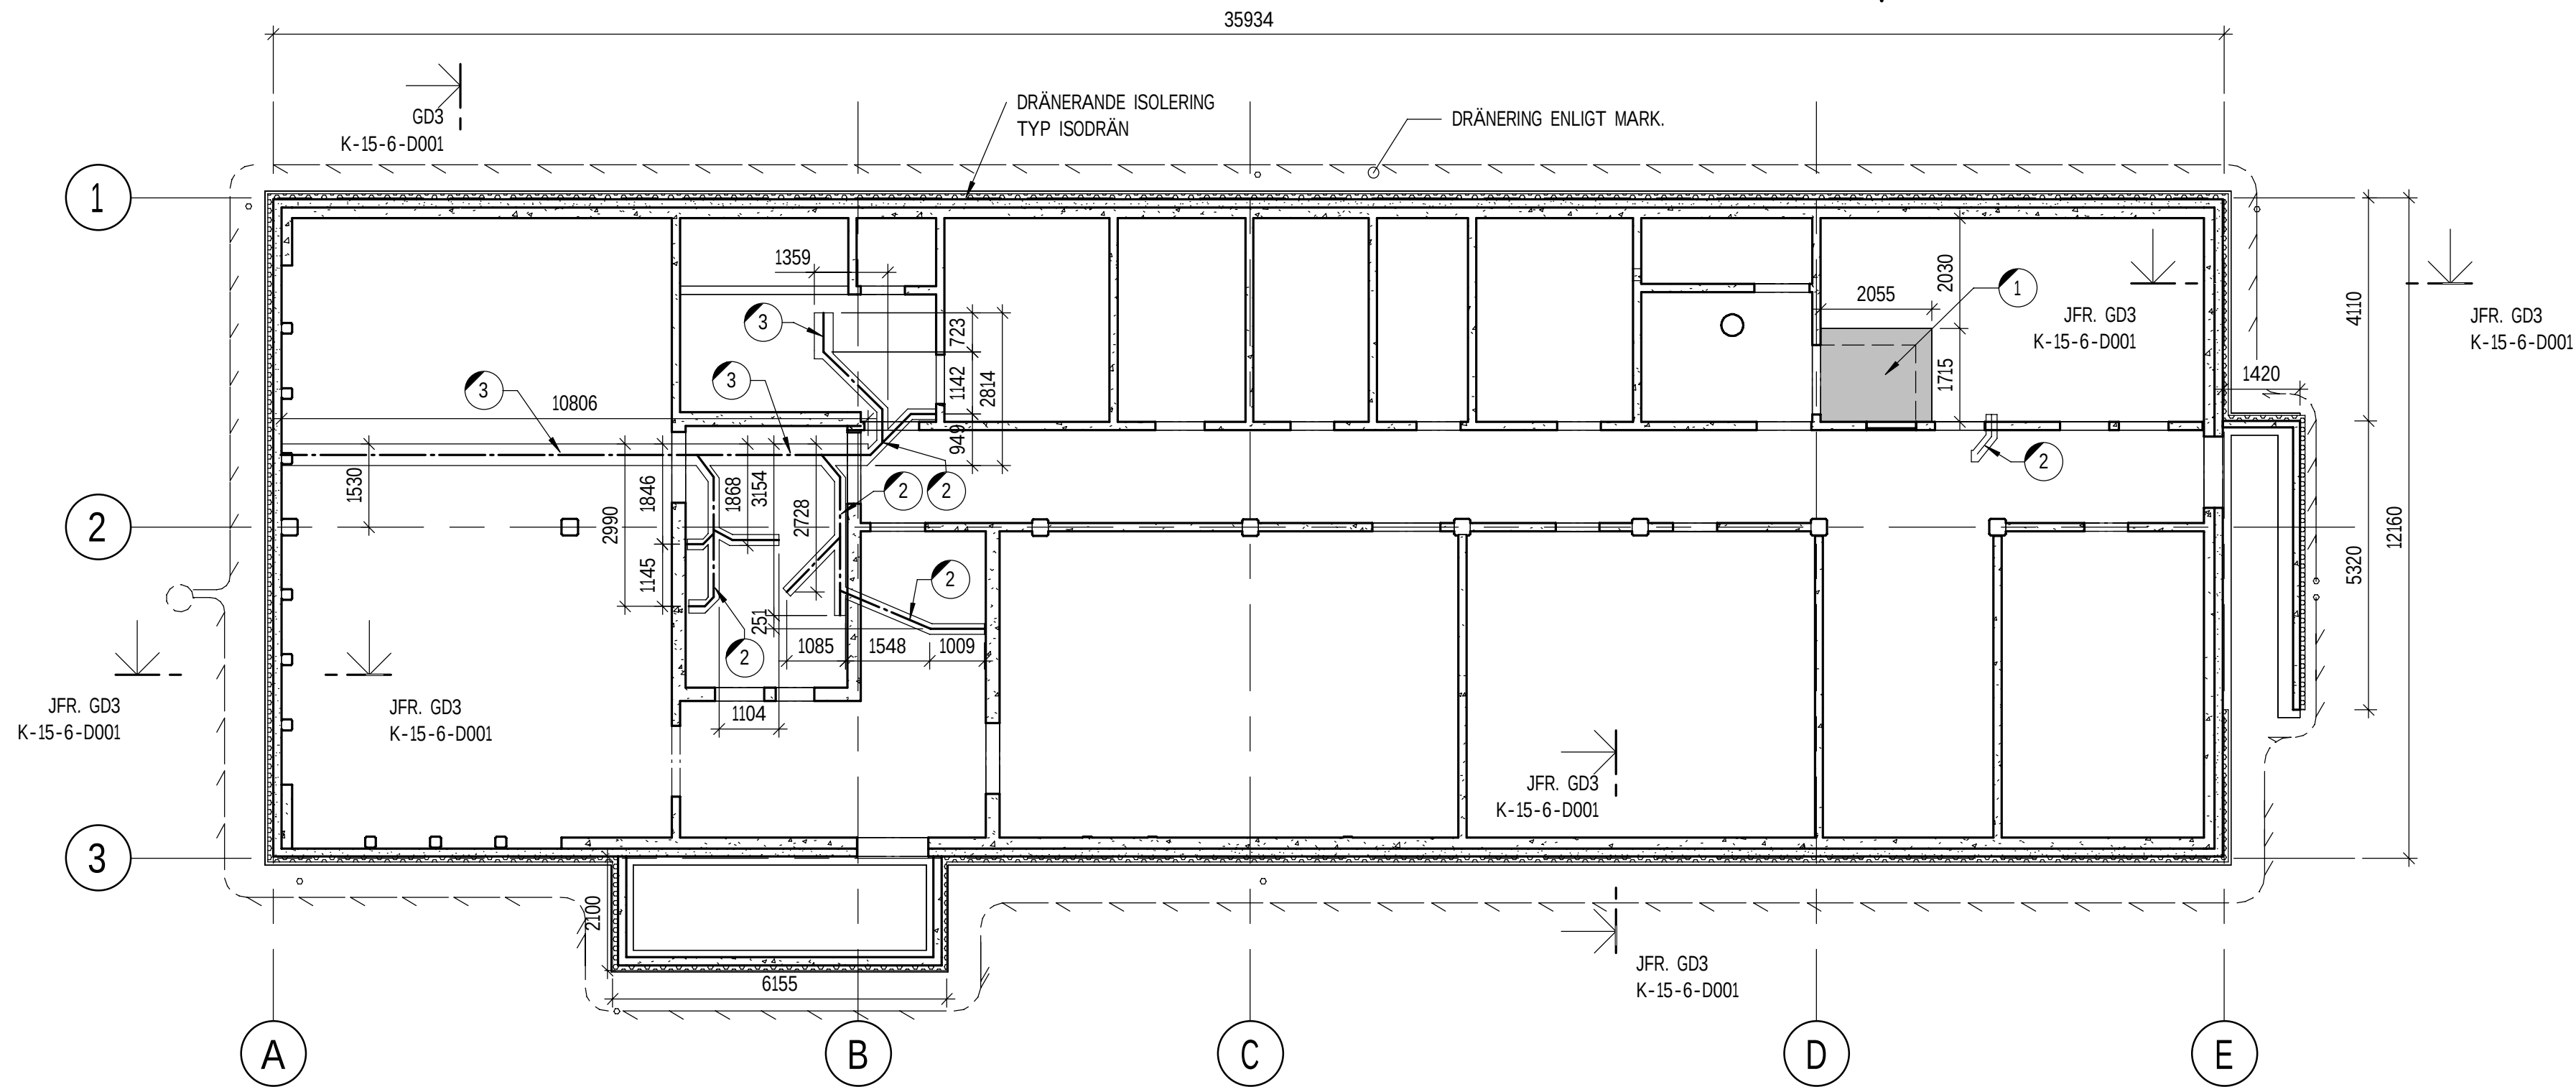

D090 GRUNDPLAN
1 : 100

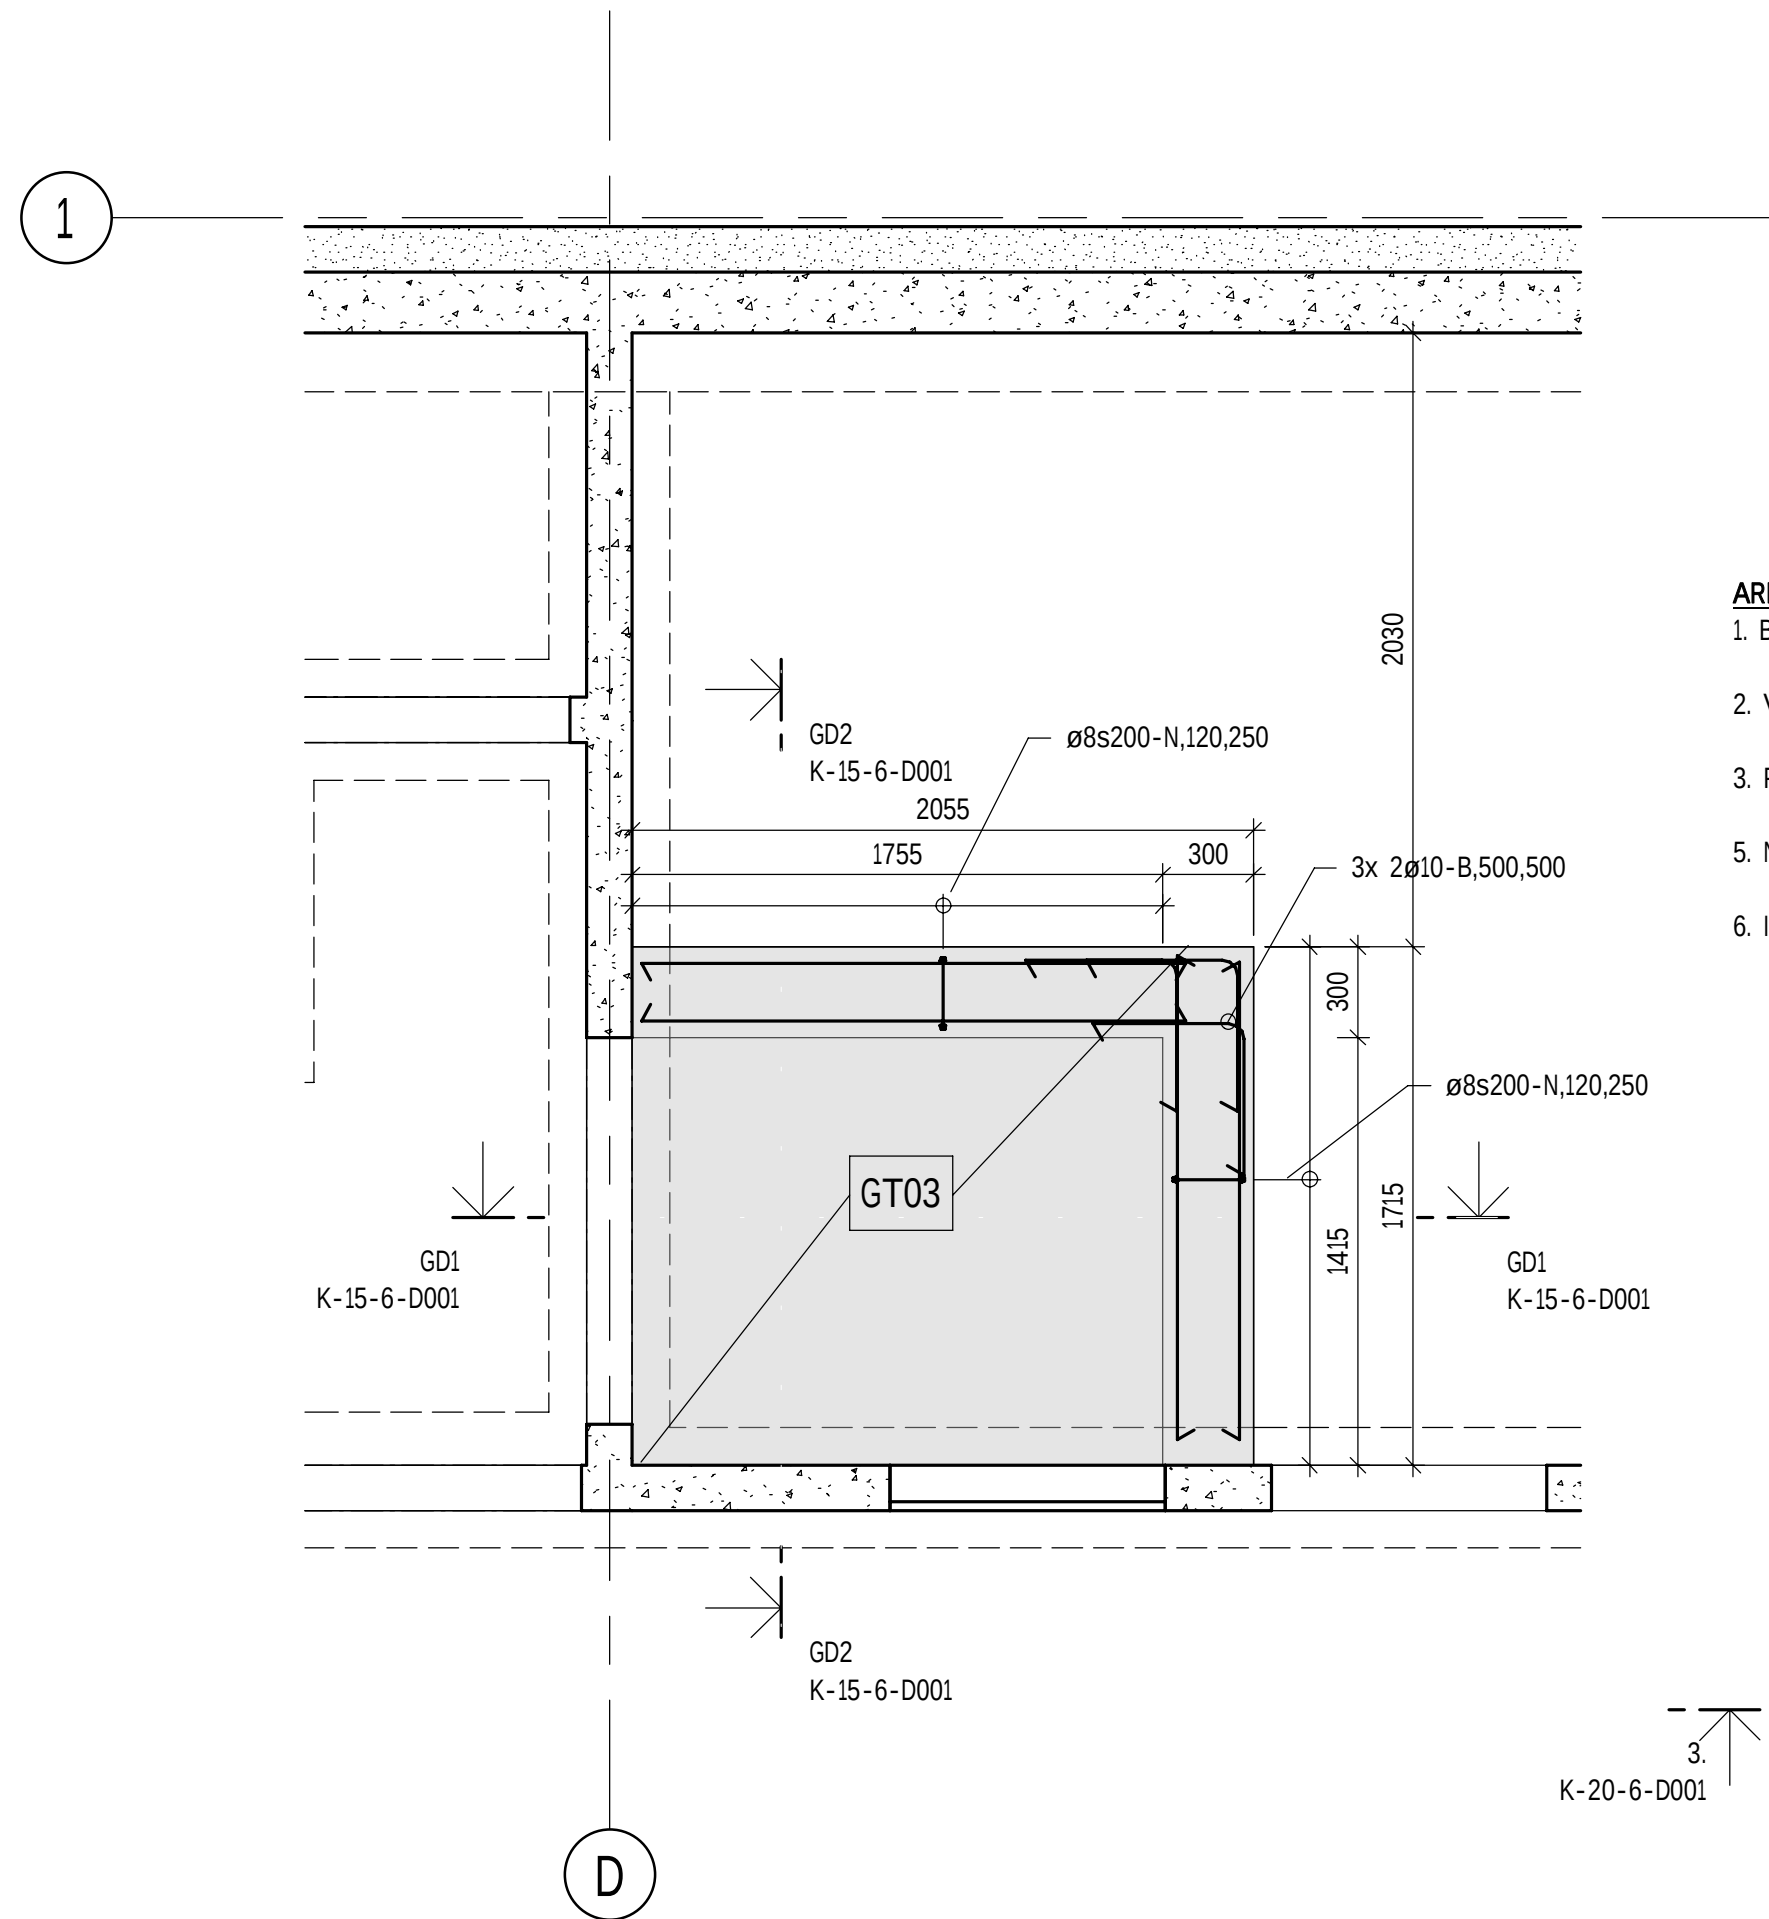

GRUNDPLAN HISSGROP
1 : 25

- ARBETSORDNING HISSGROP
- BEFINTLIG GRUNDPLATTA BILAS/SÄGAS UPP.
 - VARSAM URGRÄVNING AV BEFINTLIGT DRÄNERINGSLAGER.
 - PACKNING AV NY MAKADAM.
 - NY ARMERING OCH UTFÖRANDE ENLIGT PLAN OCH DETALJER.
 - IGENGJUTES.

SKALA 1:100
0 1 2 5 10
METER

FÖRESKRIFTER

ALLMÄNNA ANVISNINGAR K-01-1-D001

FÖRKLARINGAR

- BEFINTLIG BETONG
- PLATTSJUTEN BETONG
- BEFINTLIG LÄTTBETONG
- DRÄNERANDE PORDRÄN
- CELLPLAST EPS
- CELLPLAST XPS

- 1 = HISSGROP 60MM DJUP.
BEFINTLIG GRUNDPLATTA BILAS/SÄGAS UPP.
- 2 = GRUNDPLATTA BILAS/SÄGAS UPP FÖR VS I
GRUNDPLATTA.
200mm BREDD. DJUP ENLIGT VS RÖRLÄGGNING.
GRUNDPLATTA LAGAS LIKT GD4/K-15-6-D001
- 3 = GRUNDPLATTA BILAS/SÄGAS UPP FÖR VS I
GRUNDPLATTA.
400mm BREDD. DJUP ENLIGT VS RÖRLÄGGNING.
GRUNDPLATTA LAGAS LIKT GD4/K-15-6-D001.

HÄNVISNINGAR

GRUNDETALJER: K-15-6-D001

1	GODKÄND	2025-02-26	MG
BET	ÄNDRING AVSER	DATUM	SIGN
FÖRFRÅGNINGSUNDERLAG			
BYGGHANDLING			
2025-02-26	GODKÄND	ÄNDRING	STATUS
CENTRUMHUSET HUS D KRÅKAN 1, ROBERTSFORS			
ÄF-Infrastructure AB Strandgatan 9A			
891 39 Örnsköldsvik MARCUS GRANQVIST			
ROBIN ÖSTMAN			
D0192211			
OMBYGGNAD BIBLIOTEK OCH LÄGENHETER			
GRUNDPLAN			
K-15-1-D090			