

FÖRESKRIFTER

ALLMÄNNA ANVISNINGAR: K-01-1-D001

FÖRKLARINGAR


- 1 = HÅLTAGNING VENT I VÄGG ø100mm
2 = HÅLTAGNING VENT I VÄGG ø120mm
3 = HÅLTAGNING VENT I VÄGG ø150mm
4 = HÅLTAGNING VENT I VÄGG ø180mm
5 = HÅLTAGNING VENT I VÄGG ø220mm
6 = HÅLTAGNING VENT I VÄGG 190x540mm
7 = HÅLTAGNING VS I BJÄLKLAG
8 = HÅLTAGNING VENT ø220mm
9 = NYTT HISSCHAKT 1280x1590mm, I BEFINTLIGT BETONGBJÄLKLAG 250mm
10 = BEFINTLIG DÖRRÖPPNING BYGGS IGEN.
11 = NY DÖRRÖPPNING 1280x2230mm, I BEFINTLIG BETONGVÄGG MED TJOCKLEK 150mm.
12 = HÅLTAGNING VS I BEF. STÅLBALK HEB 300 MED BETONGFYLNING MELLAN FLÄNSAR.
1st ø18mm
2st ø22mm
2st ø30mm
13 = HÅLTAGNING EL 100x300mm, I BEFINTLIGT BETONGBJÄLKLAG 250mm
14 = HÅLTAGNING EL I VÄGG 100x300mm
15 = HÅLTAGNING EL I VÄGG 100x200mm
16 = HÅLTAGNING VS I VÄGG ø50
17 = HÅLTAGNING VS I VÄGG ø60
18 = HÅLTAGNING VS I VÄGG ø120
19 = HÅLTAGNING VS I VÄGG ø130
20 = HÅLTAGNING VS I VÄGG ø140
21 = HÅLTAGNING VS I VÄGG ø160
22 = HÅLTAGNING VS I VÄGG ø170
23 = HÅLTAGNING VS I VÄGG ø180
24 = HÅLTAGNING VS I VÄGG ø190
25 = HÅLTAGNING VS I VÄGG ø100

MÄTT I HÖJD FÖR HÅLTAGNINGAR I VÄGG ENLIGT RESPEKTIVE VS-, VENT- & EL-HANDLINGAR

HÄNVISNINGAR

PLANER
GRUNDPLAN: K-15-1-D090
KÄLLARPLAN -DEL 1: K-20-1-D091
KÄLLARPLAN - DEL 2: K-20-1-D092

1	GODKÄND		2025-02-26	MG
BET	ÄNDRING AVSER		DATUM	SIGN
FÖRFRÅGNINGSUNDERLAG				
BYGGHANDLING				
DATE		GODKÄND		ÄNDRING
2025-02-26				
CENTRUMHUSET HUS D				
KRÅKAN 1, ROBERTSFORS				
ÄF-Infrastructure AB				ÄNDRING PART
Strandgatan 9A				
891 39 Örnsköldsvik				Tel: 010-505 00 00
MARCUS GRANQVIST		KONTAKTPERSON	SKAPAD AV	
ROBIN ÖSTMAN		GODKÄND AV	MARCUS GRANQVIST	UPPDRAGSNUMMER
		D0192211	RITNINGSKATEGORI	
OMBYGGNAD BIBLIOTEK OCH LÄGENHETER				
BJÄLKLAG OVAN KÄLLARE				
KÄLLARPLAN - Del 1				
K-20-1-D091				
INNEHÅLL				FORMAT
				A1
				SKALA
				1:50
				NUMBER
				1
				BET

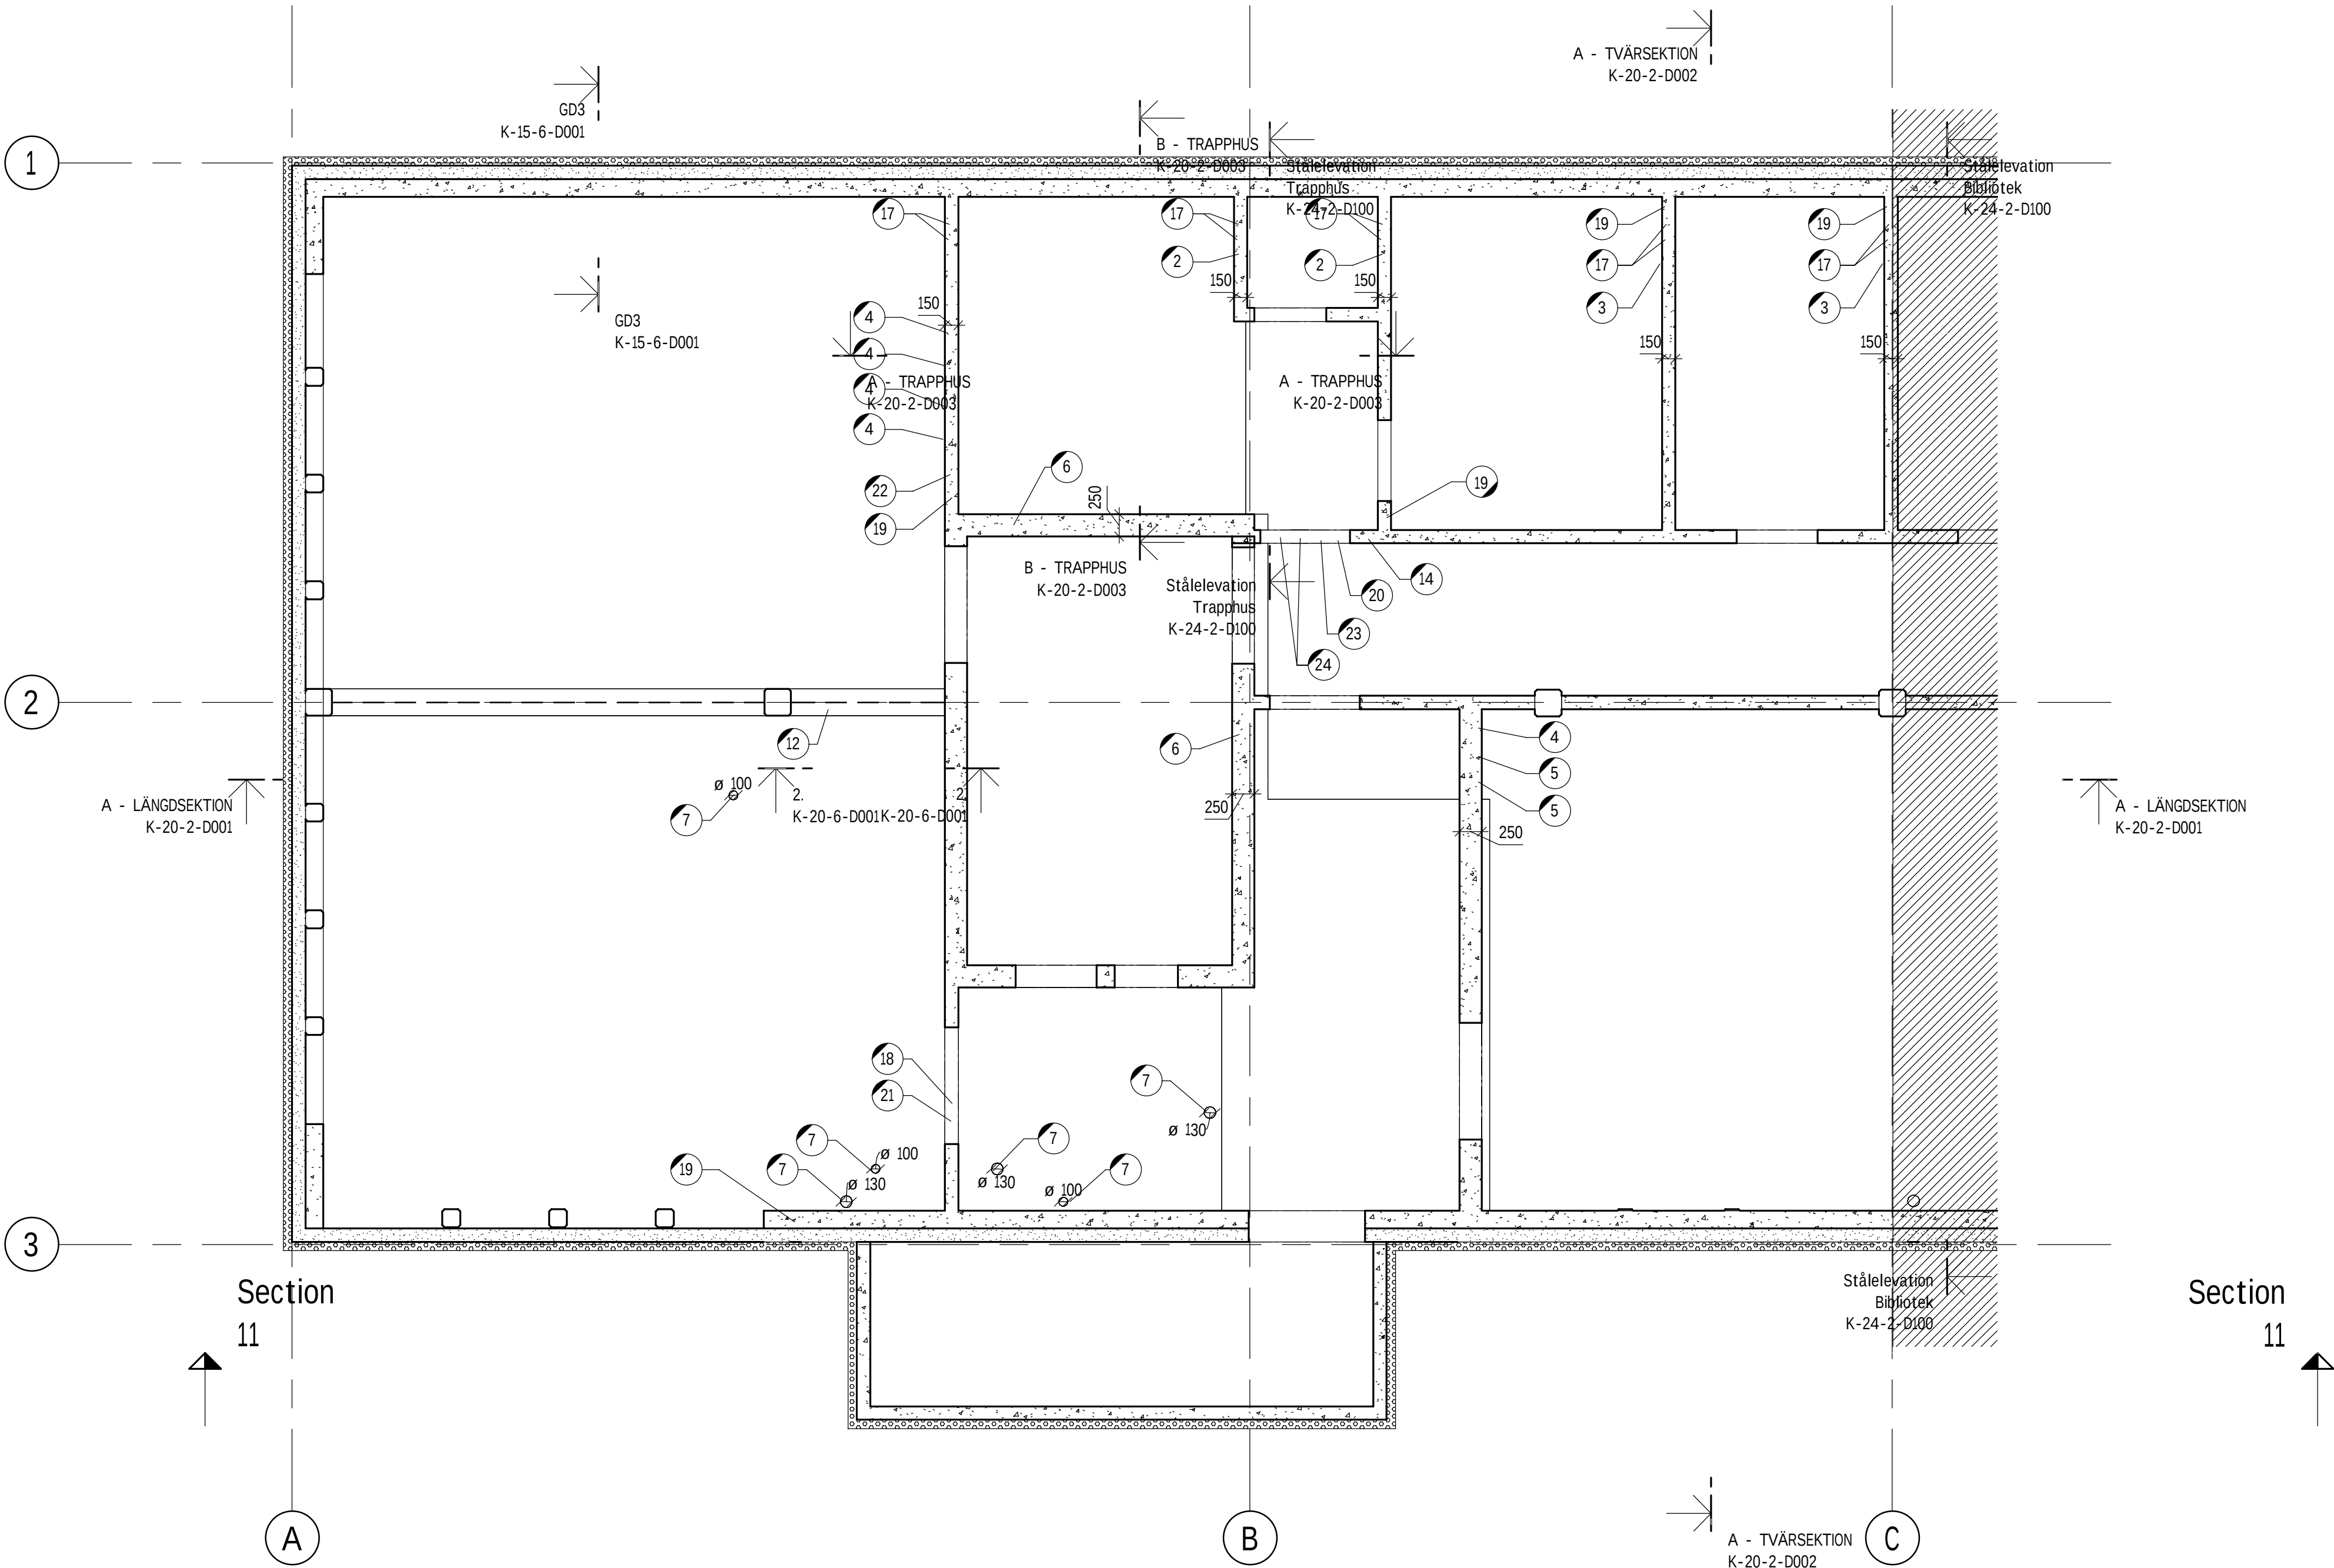

KÄLLARPLAN - Del 1
1 : 50

SKALA 1:50

0 1 2 5
METER