


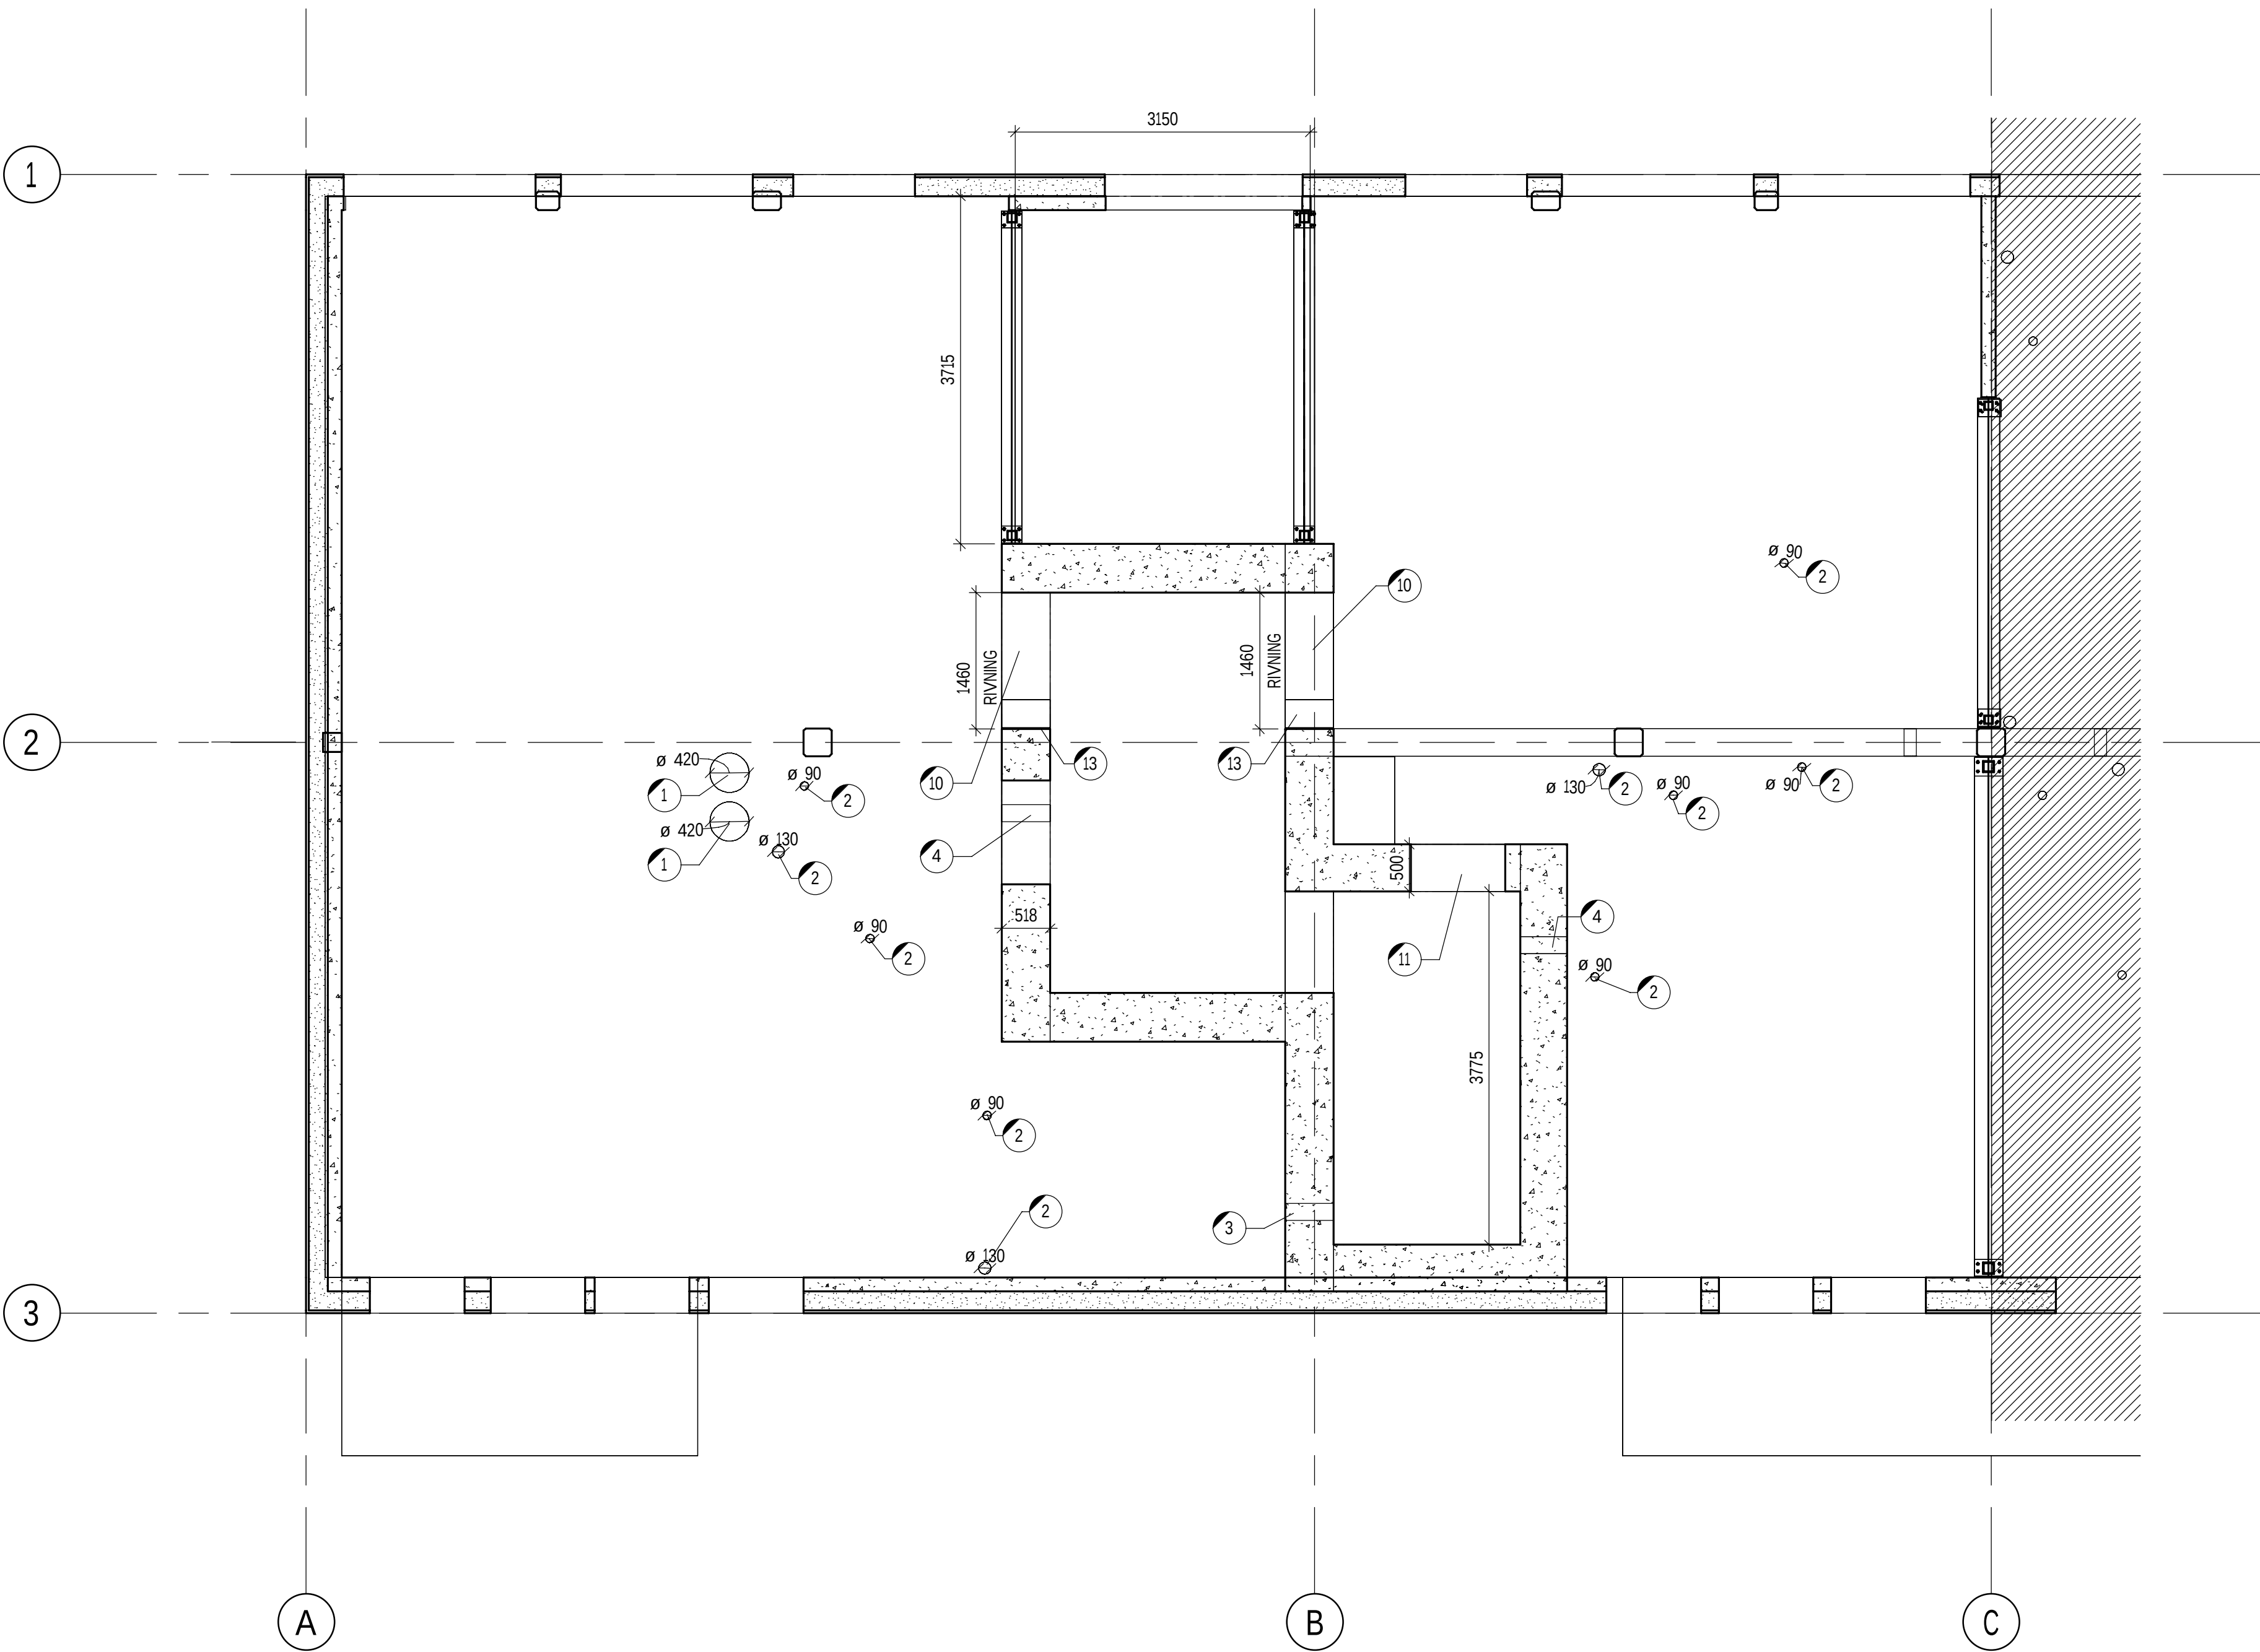

PLAN 1 - Del 1
1 : 50

FÖRESKRIFTER

ALLMÄNNA ANVISNINGAR: K-01-1-D001

FÖRKLARINGAR

- 1 = HÅLTAGNING I BJÄLKLAG FÖR VENT
- 2 = HÅLTAGNING I BJÄLKLAG FÖR VS
- 3 = HÅLTAGNING VENT 340x750mm. FÖR TVÅ KANALER 340x340mm
- 4 = HÅLTAGNING I VÄGG VENT ø180mm. HÖJD ENL. VENT-RITNING.
- 5 = HÅLTAGNING I VÄGG VS ø100mm. HÖJD ENL. VENT-RITNING.
- 6 = HÅLTAGNING I VÄGG VS ø130mm. HÖJD ENL. VENT-RITNING.
- 7 = HÅLTAGNING I VÄGG VS ø160mm. HÖJD ENL. VENT-RITNING.
- 8 = NY DÖRRÖPPNING 1010x2110mm I BEFINTLIG BETONGVÄGG MED TJOCKLEK 150mm.
- 9 = NY DÖRRÖPPNING 1280x2230mm I BEFINTLIG BETONGVÄGG MED TJOCKLEK 150mm.
- 10 = NY DÖRRÖPPNING I VALVVÄGG 1460x2110mm
- 11 = TIDIGARE IGENBYGGD ÖPPNING I VALVVÄGG ÖPPNAS UPP. 1010x2110mm
- 12 = NYTT HISSCHAKT 1280x1590mm. BEFINTLIGT BETONGBJÄLKLAG 250mm
- 13 = HÅLTAGNING I VÄGG EL, 100x300. HÖJD ENL. EL-RITNING.

MÅTT I HÖJD FÖR HÅLTAGNINGAR I VÄGG ENLIGT RESPEKTIVE VS-, VENT- & EL-HANDLINGAR

HÄNVISNINGAR

PLANER	
GRUNDPLAN:	K-15-1-D090
KÄLLARPLAN - DEL 1:	K-20-1-D091
KÄLLARPLAN - DEL 2:	K-20-1-D092
PLAN 1 - DEL 1:	K-20-1-D101
PLAN 1 - DEL 2:	K-20-1-D102
PLAN 2 - DEL 1:	K-20-1-D201
PLAN 2 - DEL 2:	K-20-1-D202
FLÅKTRUM - DEL 1:	K-20-1-D301
FLÅKTRUM - DEL 2:	K-20-1-D302

1	GODKÄND	2025-02-26	MG
BET	ÄNDRING AVSER	DATUM	SIGN
FÖRFRÅGNINGSUNDERLAG			
BYGGHANDLING			
2025-02-26	GODKÄND	ÄNDRING	STATUS
CENTRUMHUSET HUS D			
KRÅKAN 1, ROBERTSFORS			
ÄF-Infrastructure AB			
Strandgatan 9A			
891 39 Örnsköldsvik			
Tel: 010-505 00 00			
MARCUS GRANQVIST	MARCUS GRANQVIST	SKAPAD AV	ANSVARIG PART
ROBIN ÖSTMAN	D0192211	UPPERAGSNUMMER	
RITNINGSKATEGORI			
OMBYGGNAD BIBLIOTEK OCH LÄGENHETER			
BJÄLKLAG OVAN BIBLIOTEK			
PLAN 1 - Del 1			
K-20-1-D101			
1			

SKALA 1:50
0 1 2 5
METER